
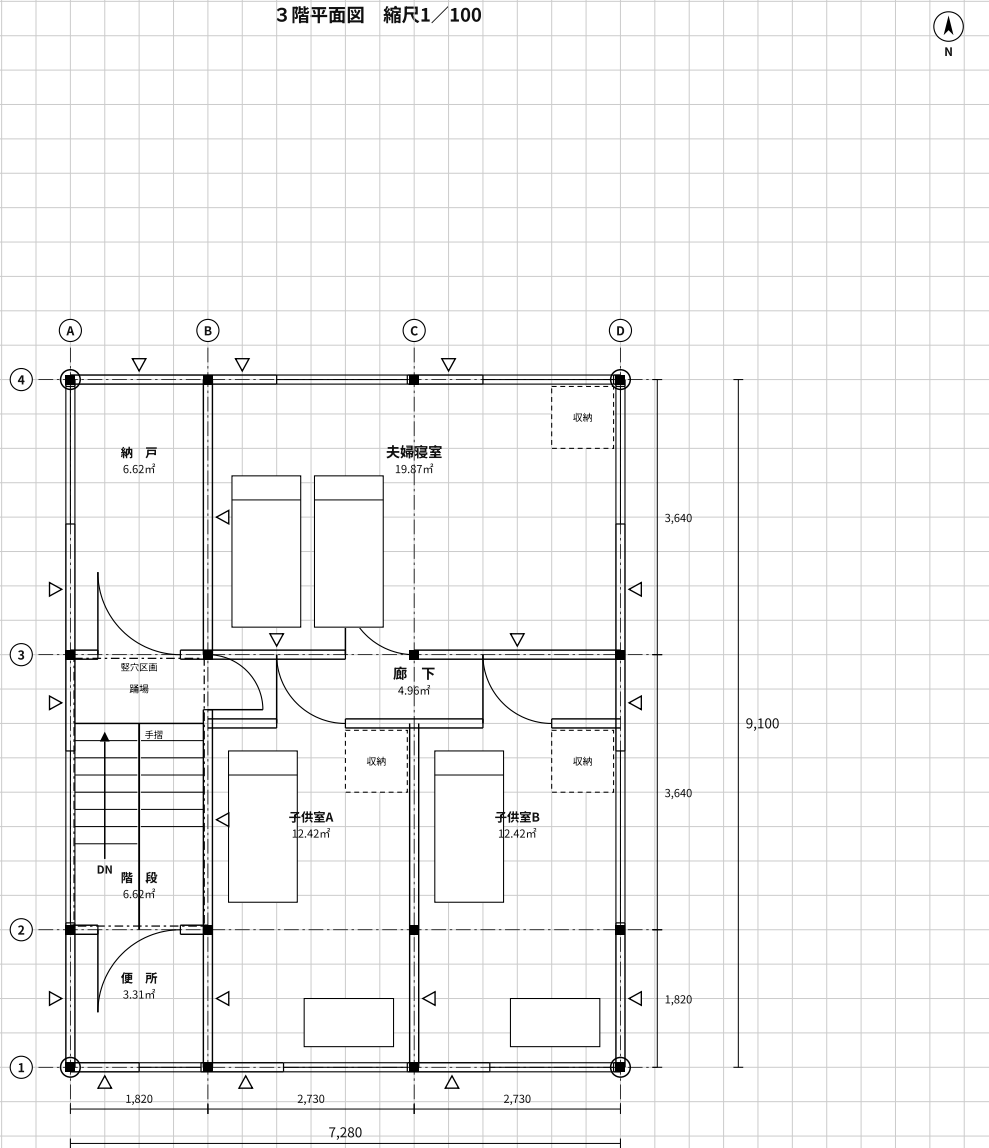
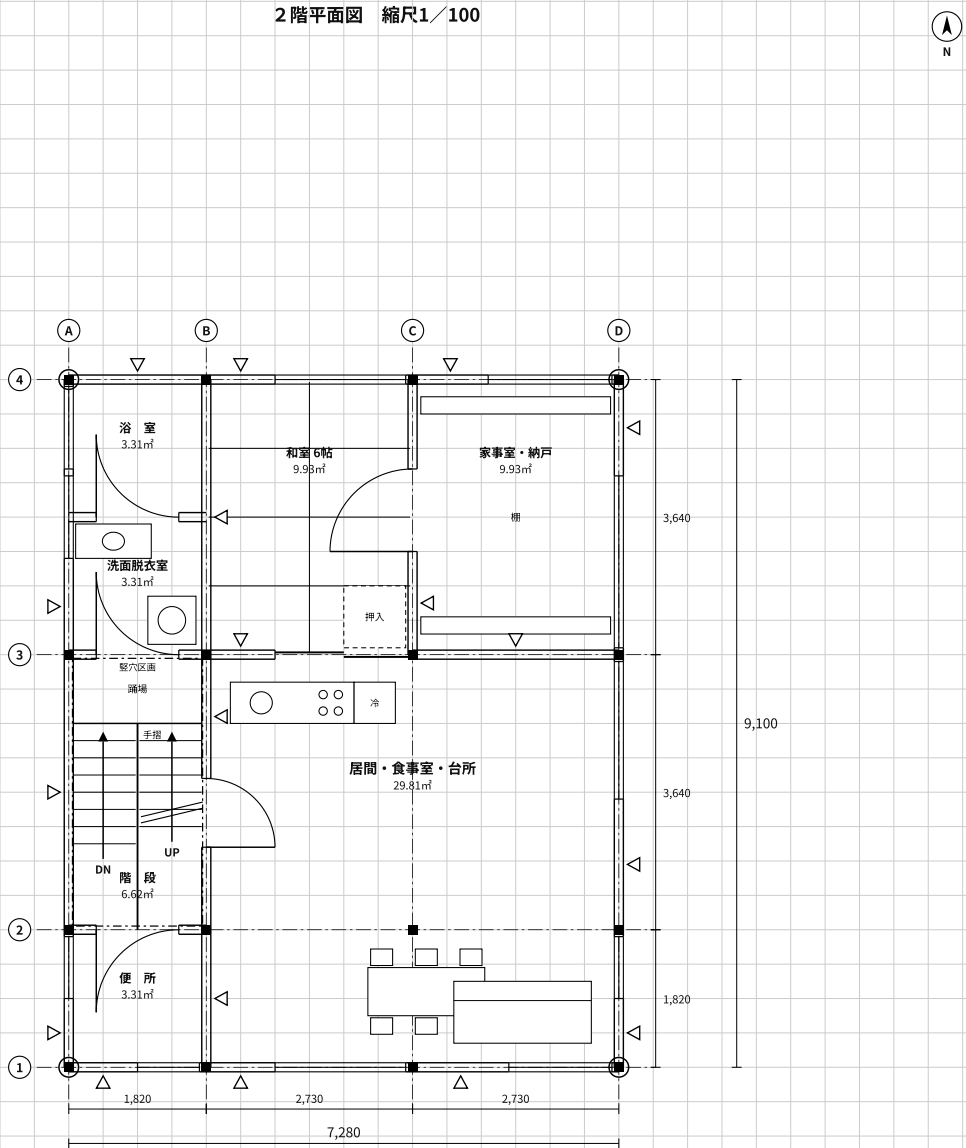


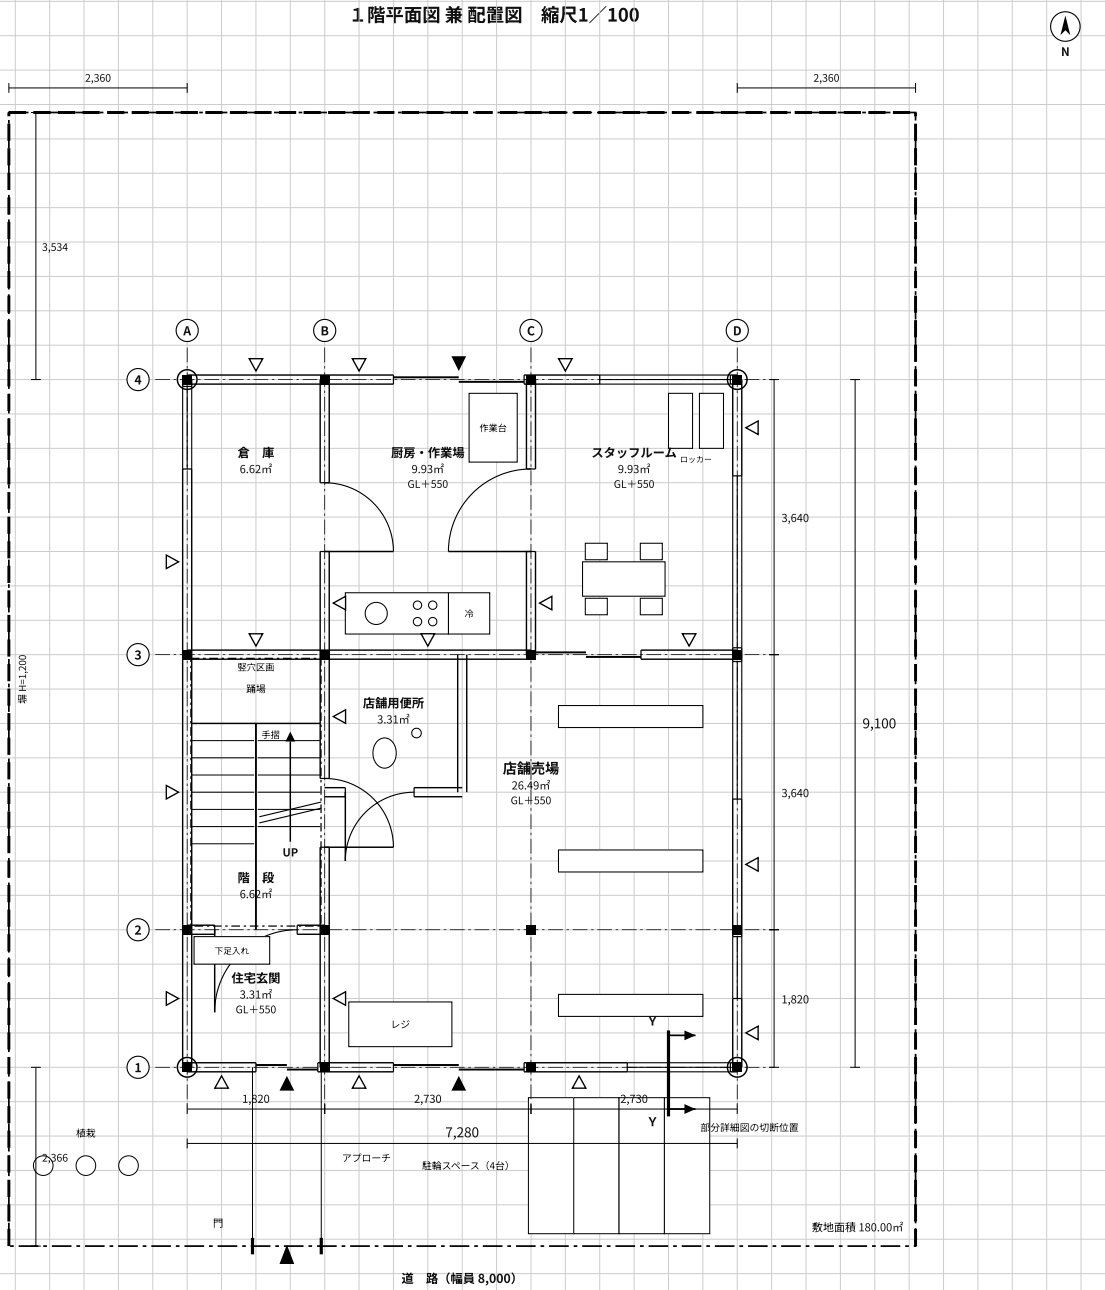

面積表

敷地面積		180.00	m ²
建築面積	(計算式) 7.28×9.10	66.24	m ²
床面積 1階 ア	(計算式) 7.28×9.10	66.24	m ²
2階 イ	(計算式) 7.28×9.10	66.24	m ²
3階 ウ	(計算式) 7.28×9.10	66.24	m ²
延べ面積 ア+イ+ウ		198.72	m ²

小数点以下第3位以下は切り捨て。計算式はm単位で書く。

凡例（床伏図兼小屋伏図の表示記号）

	通し柱	1階の管柱	2階の管柱	重なる管柱	胴差・桁（正角材）	同上（平角材）	同上（丸太材）	火打梁	棟木	母屋・小屋束
記号										
寸法	120×120	120×120	120×120	—	120×120	図中に記入	図中に記入	90×90	120×120	90×90

※ 平角材（120×240 など）の断面寸法は、この欄ではなく 床伏図の中の梁1本ずつのわきに記入する。




標準解答例

予想問題 A
商店街に建つ併用住宅（物販店舗）
木造3階建て 〃 8マス × 10マス（7,280 × 9,100）

※ 立面図・床伏図兼小屋伏図・部分詳細図は、別紙「共通図」を見てください。

この解答例のポイント

- 売場を道路（南）に面して最大に取り、住宅玄関と店舗出入口を分けている。
- 店舗用便所を売場の角から直接入れるようにして、客が厨房を通らない。
- 階段を西側の同じ位置に3階まで通し、直下率100%としている。

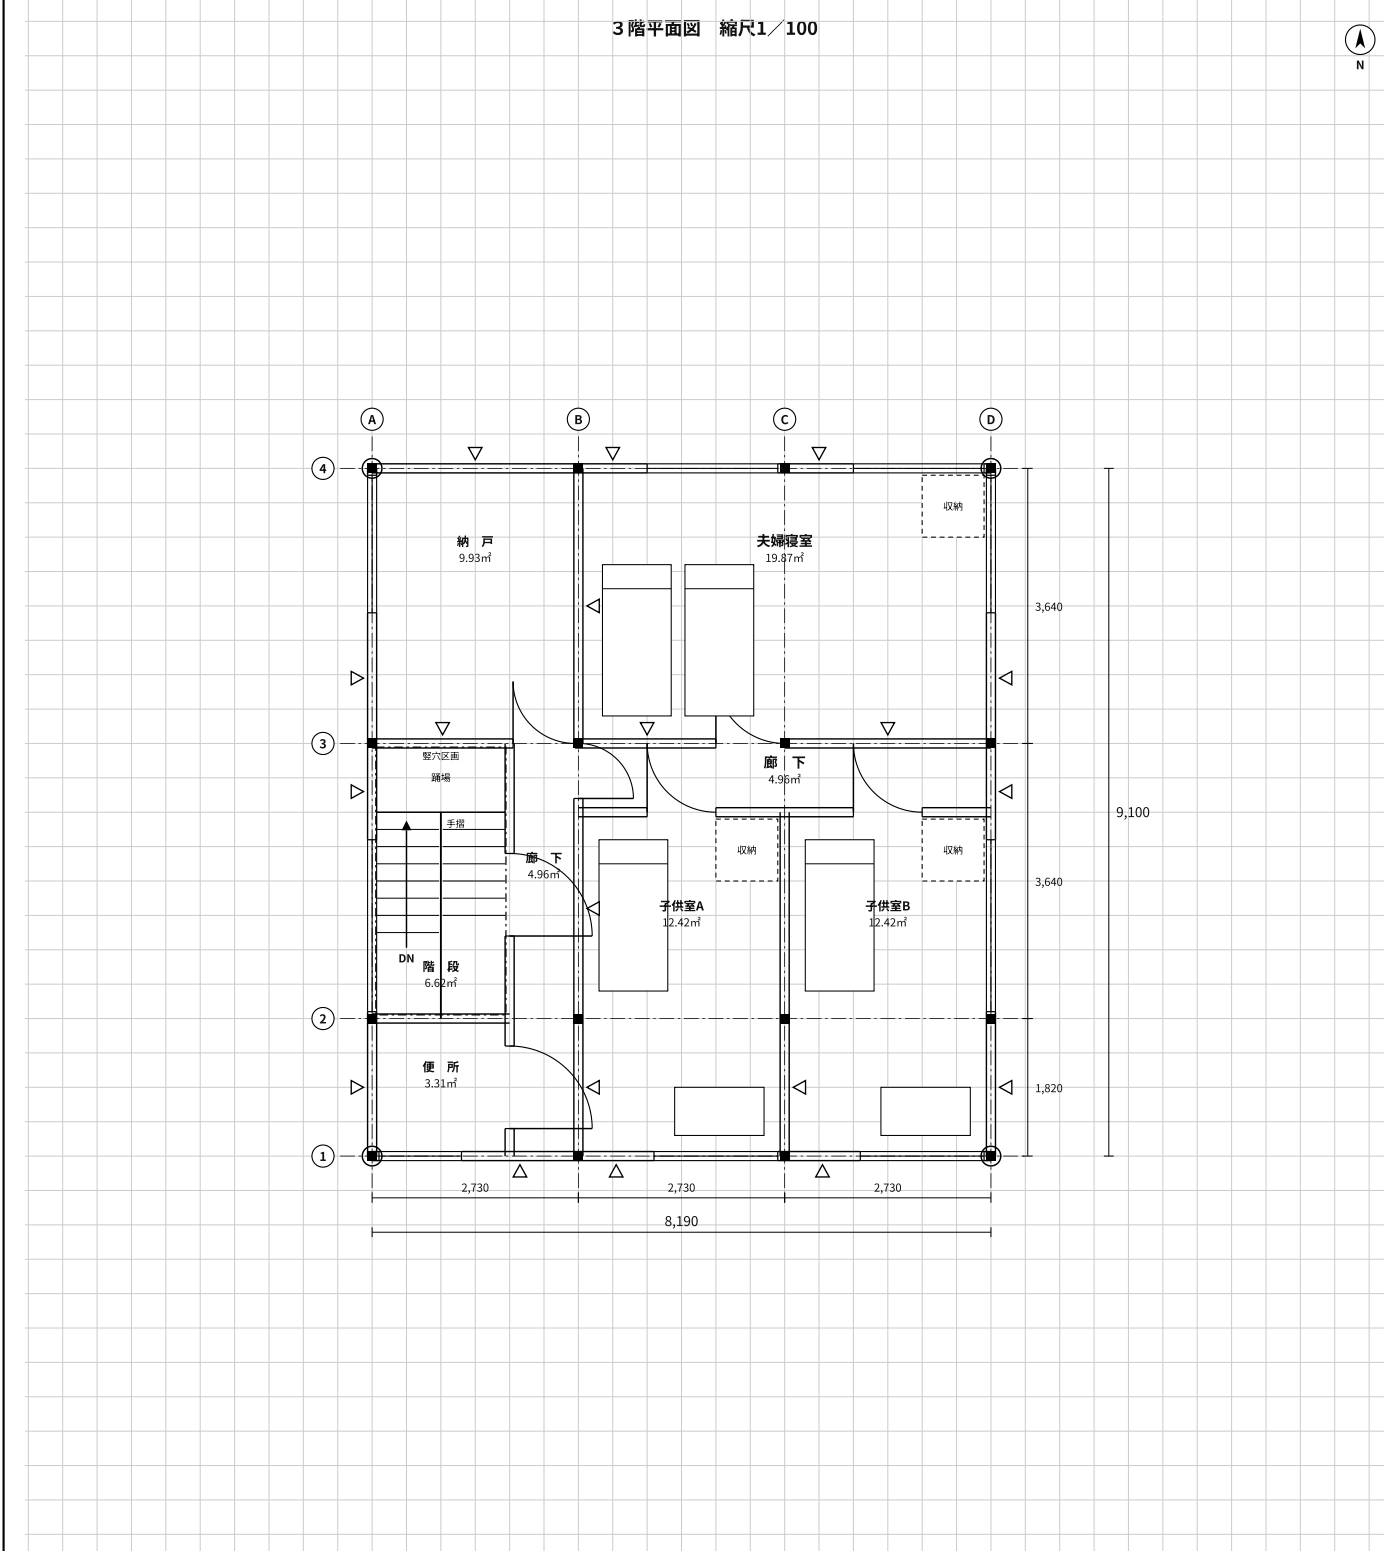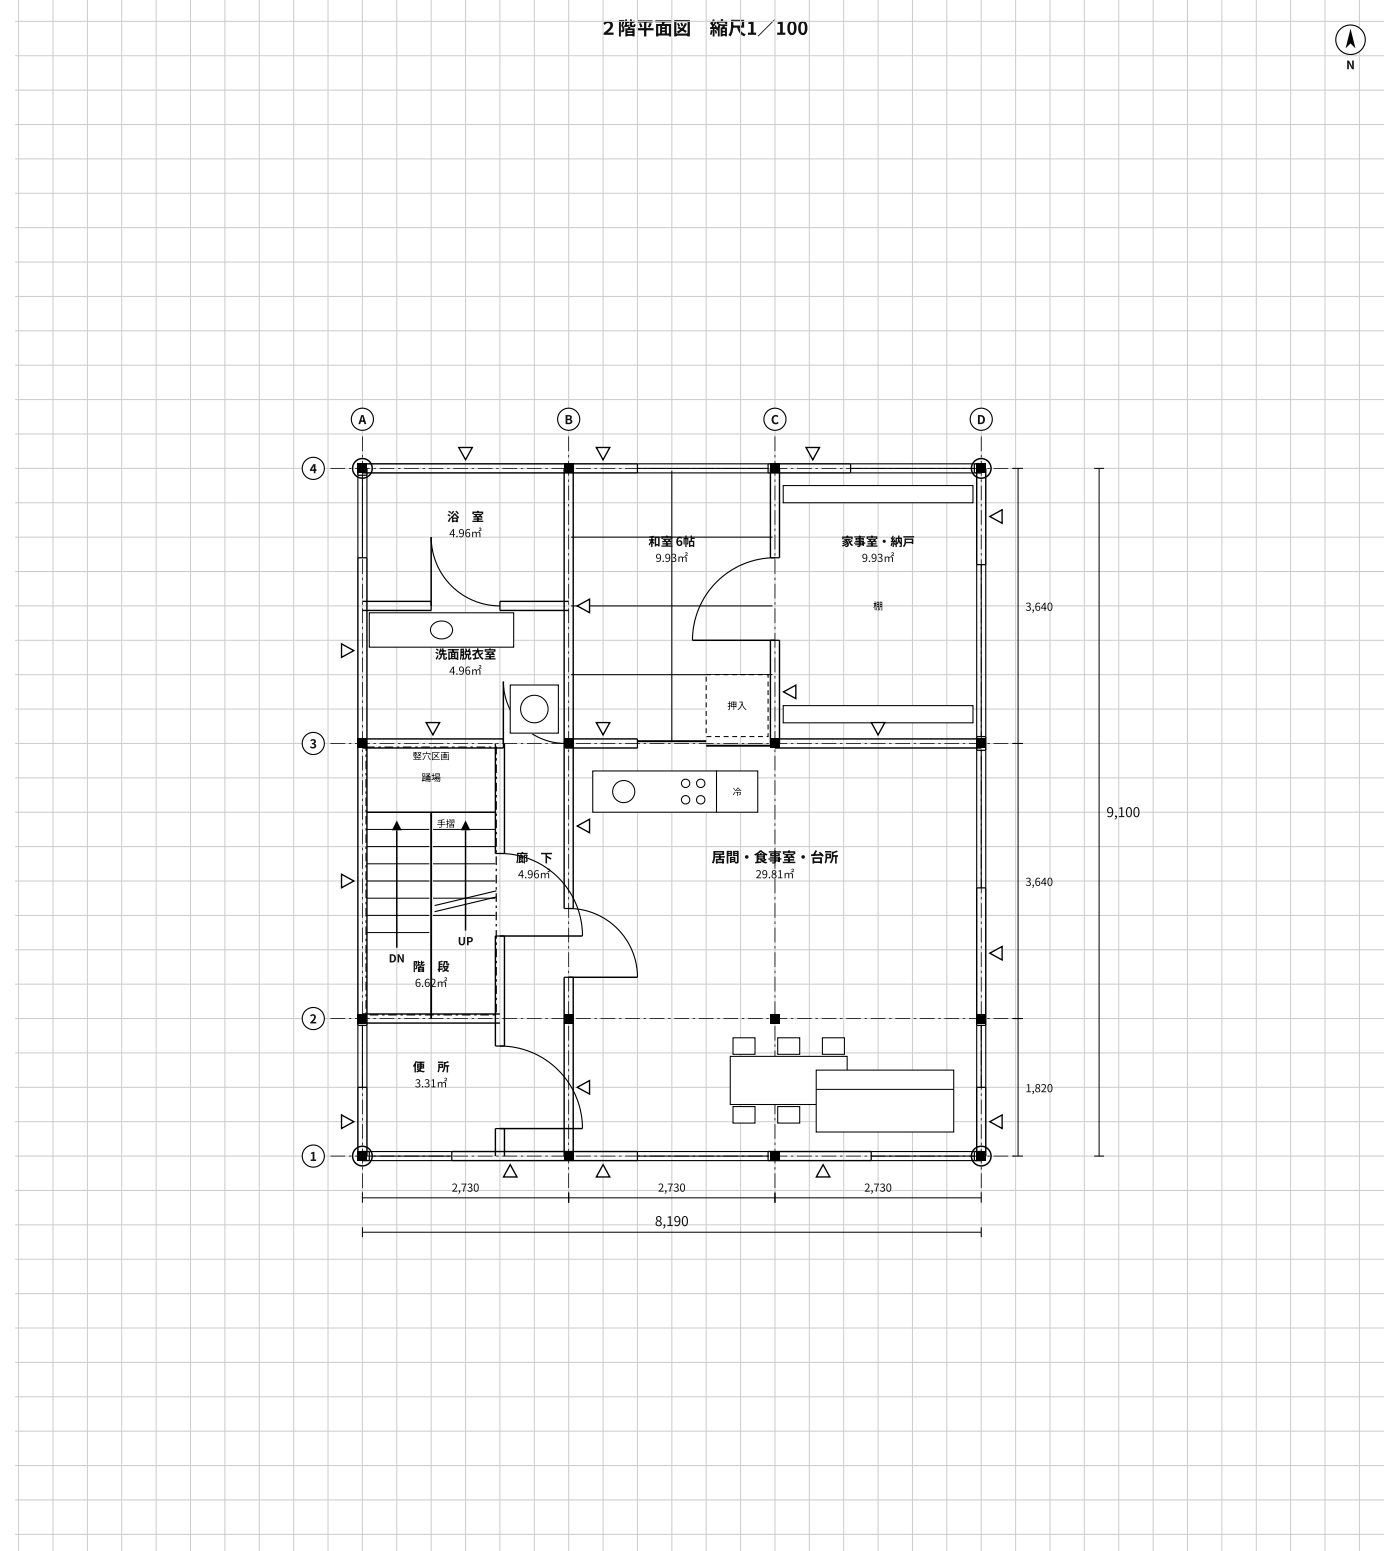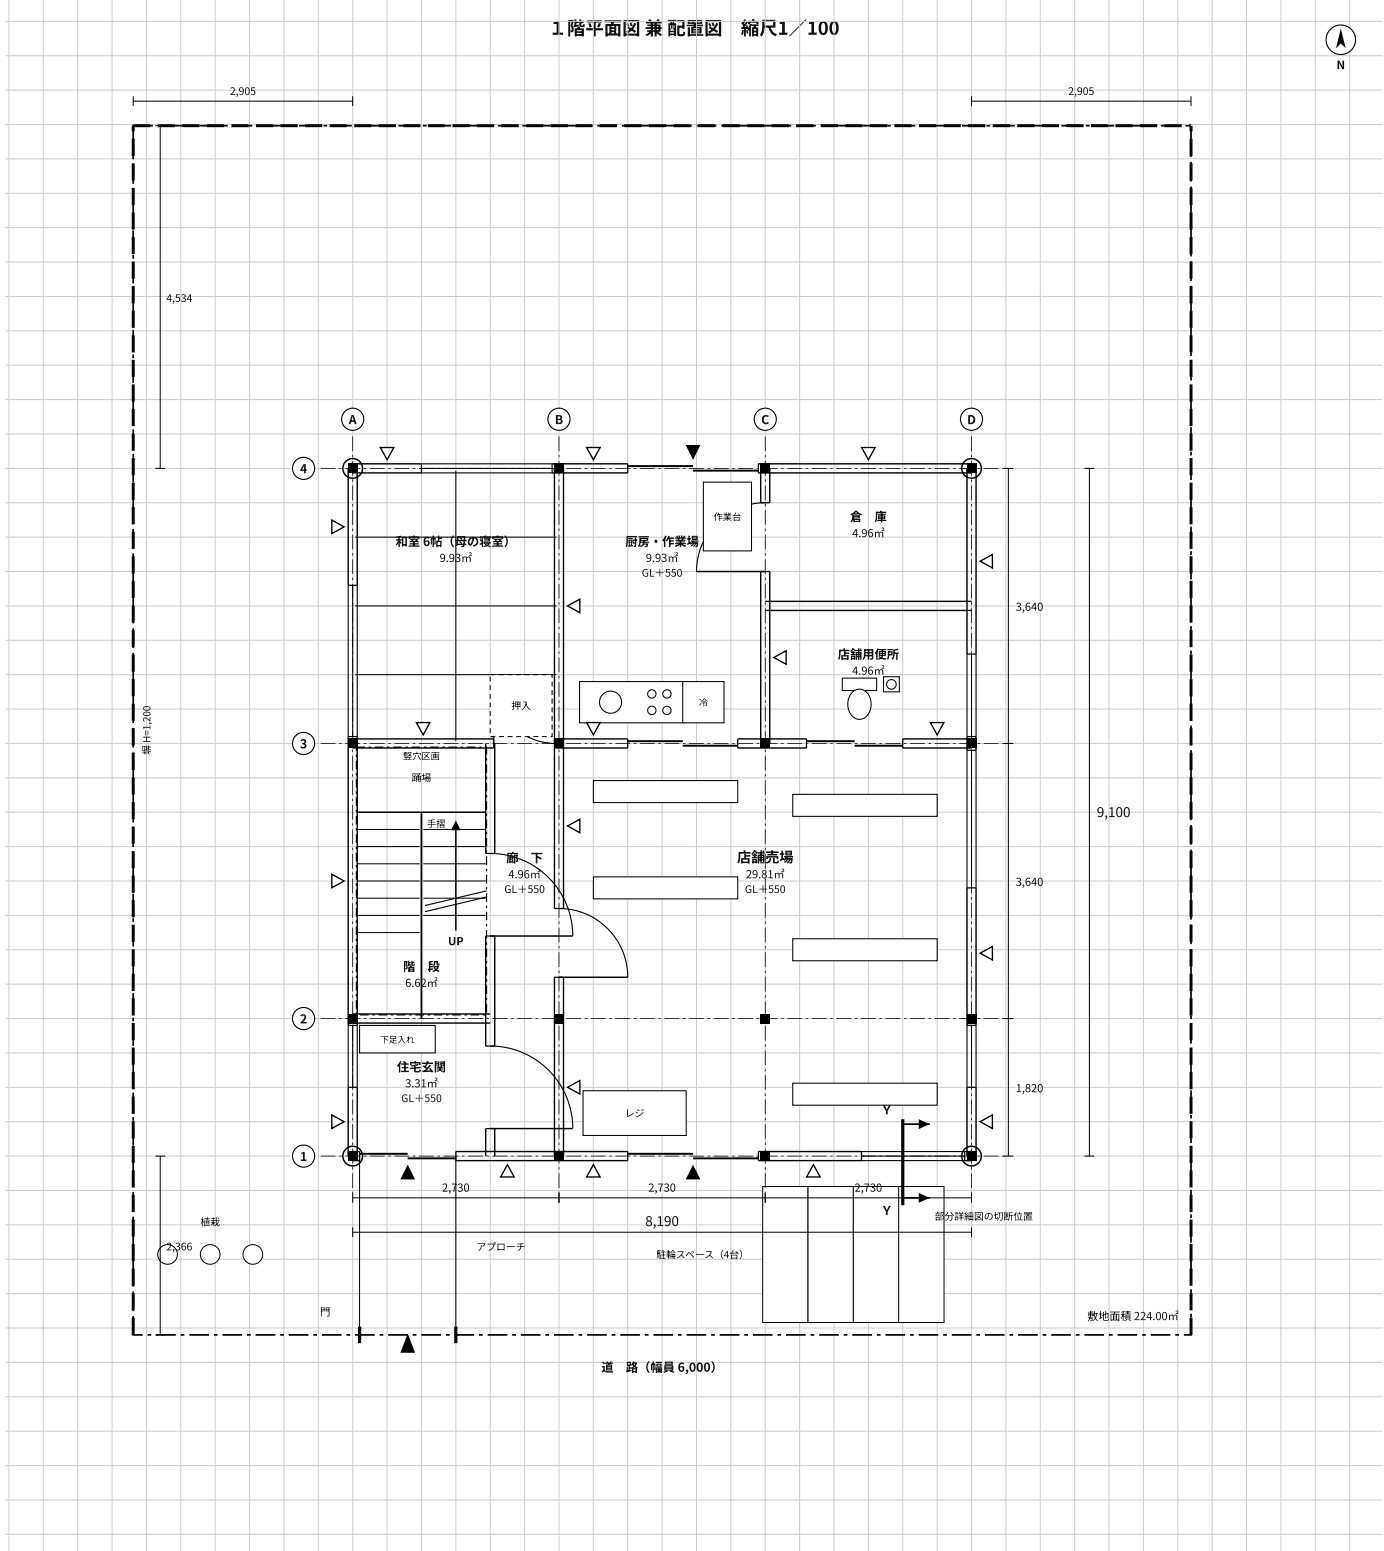

面積表

敷地面積		224.00	m ²
建築面積	(計算式) 8.19×9.10	74.52	m ²
床面積 1階 ア	(計算式) 8.19×9.10	74.52	m ²
2階 イ	(計算式) 8.19×9.10	74.52	m ²
3階 ウ	(計算式) 8.19×9.10	74.52	m ²
延べ面積 ア+イ+ウ		223.56	m ²

小数点以下第3位以下は切り捨て。計算式はm単位で書く。

凡 例（床伏図兼小屋伏図の表示記号）

	通し柱	1階の管柱	2階の管柱	重なる管柱	胴差・桁（正角材）	同上（平角材）	同上（丸太材）	火打梁	棟木	母屋・小屋束
記号										
寸法	120×120	120×120	120×120	—	120×120	図中に記入	図中に記入	90×90	120×120	90×90

※ 平角材（120×240 など）の断面寸法は、この欄ではなく 床伏図の中の梁1本ずつのわきに記入する。

標準解答例

予想問題 B


母と暮らす併用住宅（和菓子店）
木造3階建て ／ 9マス×10マス（8,190×9,100）

※ 立面図・床伏図兼小屋伏図・部分詳細図は、別紙「共通図」を見てください。


この解答例のポイント

- 1階の西側を3マス幅にして廊下を通し、その北に母の和室6帖を置いている。
- 和室から便所・洗面へ廊下1本で行けるようにして、段差をなくしている。
- 間口を9マスに広げたぶん、通り芯をA・B・C・Dの4本に組みかえている。


1 階平面図 兼 配置図 縮尺1／100

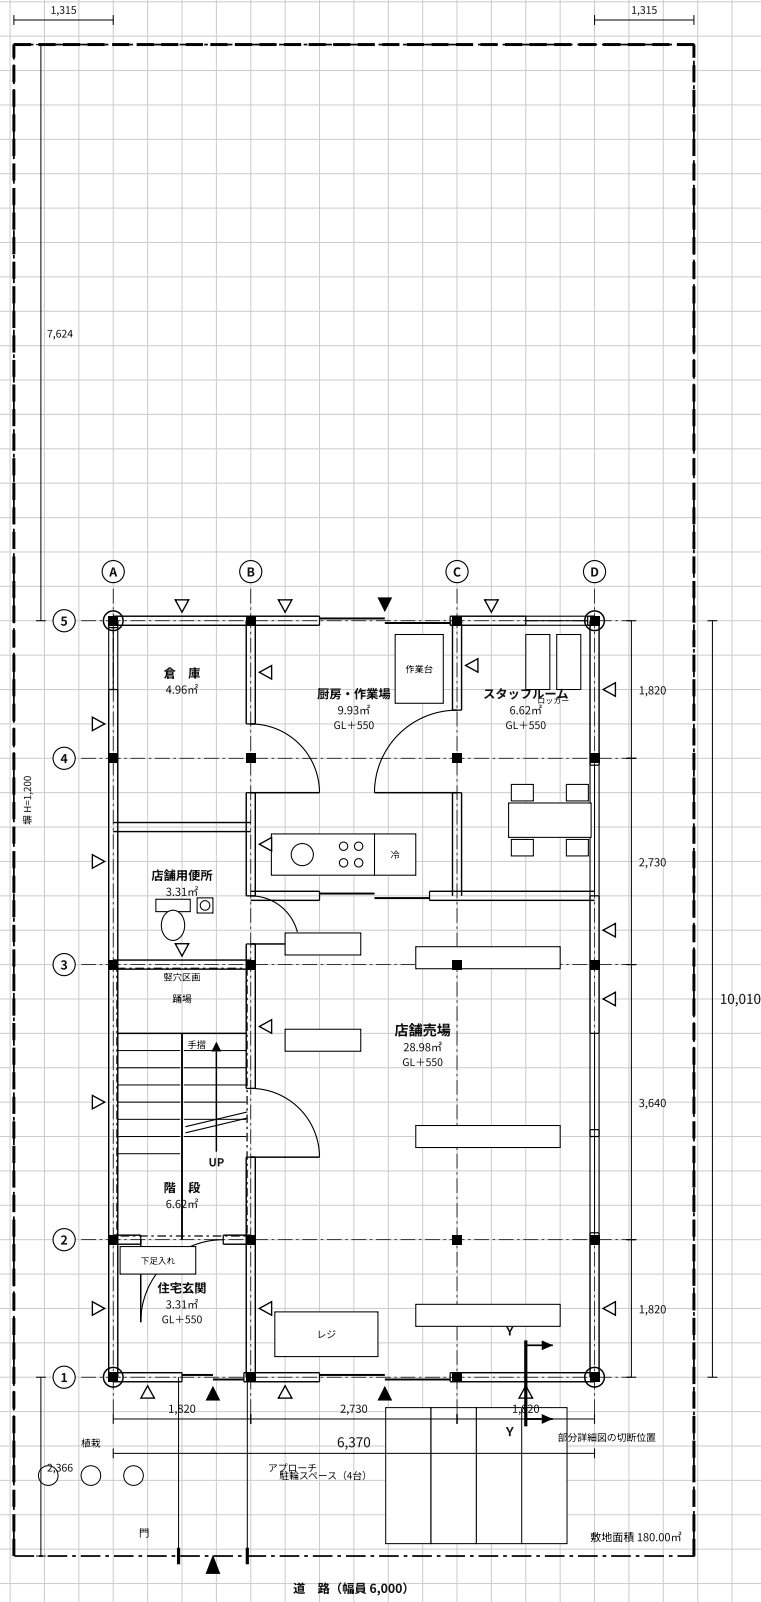

2 階平面図 縮尺1／100

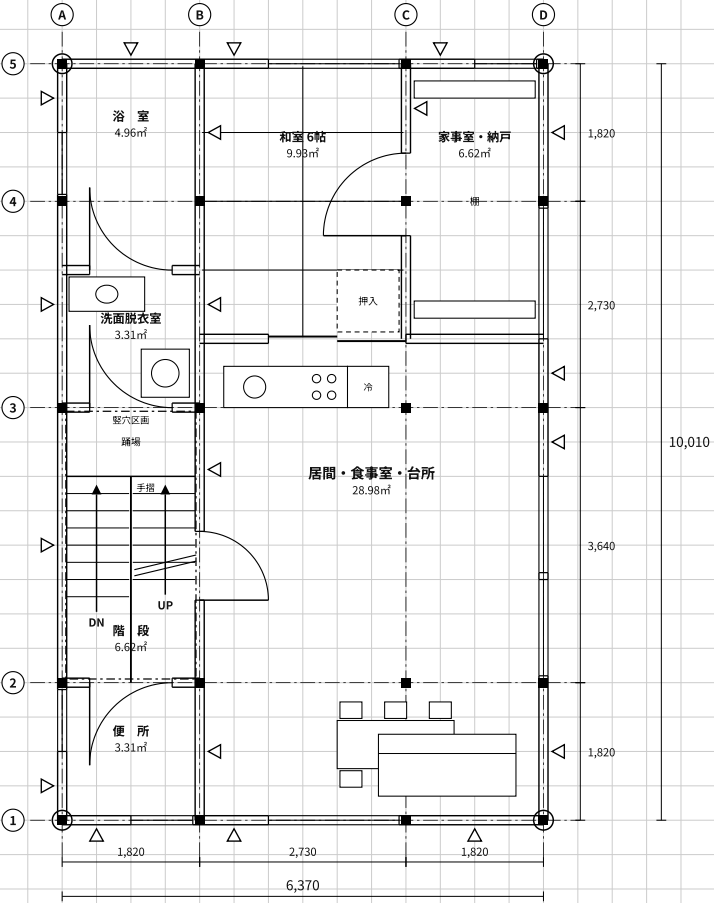

3 階平面図 縮尺1／100

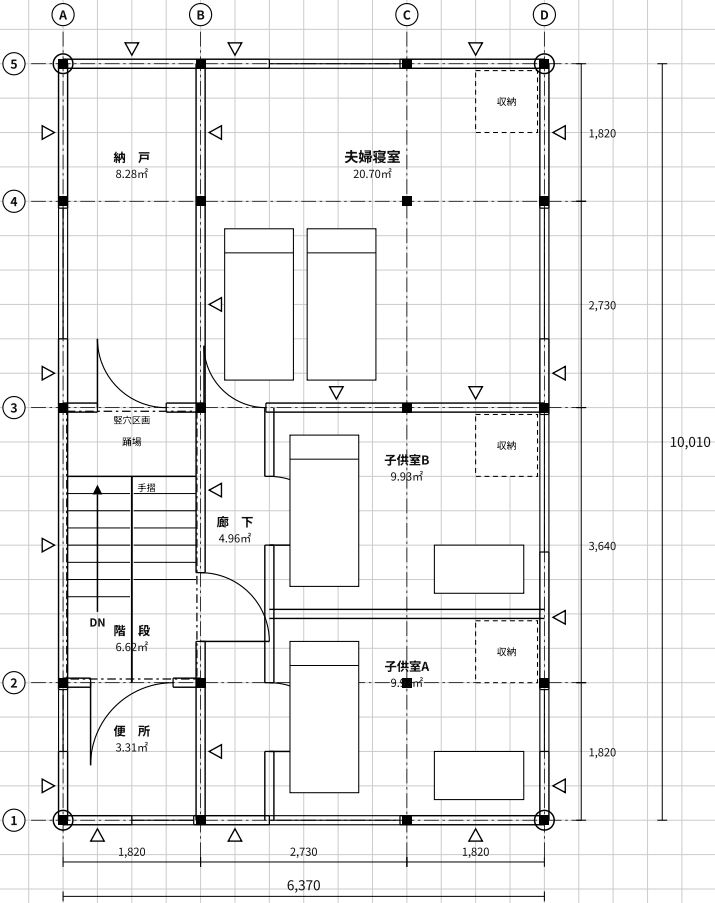

面 積 表

敷地面積		180.00 m ²
建築面積	(計算式) 6.37×10.01	63.76 m ²
床面積 1階 ア	(計算式) 6.37×10.01	63.76 m ²
2階 イ	(計算式) 6.37×10.01	63.76 m ²
3階 ウ	(計算式) 6.37×10.01	63.76 m ²
延べ面積 ア+イ+ウ		191.28 m ²

小数点以下第3位以下は切り捨て。計算式はm単位で書く。

凡 例（床伏図兼小屋伏図の表示記号）

	通し柱	1階の管柱	2階の管柱	重なる管柱	胴差・桁（正角材）	同上（平角材）	同上（丸太材）	火打梁	棟木	母屋・小屋束
記号										
寸法	120×120	120×120	120×120	—	120×120	図中に記入	図中に記入	90×90	120×120	90×90

※ 平角材（120×240 など）の断面寸法は、この欄ではなく 床伏図の中の梁1本ずつのわきに記入する。

標 準 解 答 例




予想問題 C

間口の狭い敷地の併用住宅（喫茶店）
木造3階建て ／ 7マス × 11マス（6,370 × 10,010）

※ 立面図・床伏図兼小屋伏図・部分詳細図は、別紙「共通図」をご覧ください。

この解答例のポイント

- 間口が狭いので7マス×11マスとし、売場を奥へ長く取っている。
- 水まわりを西の列にそろえて、1階から3階まで配管の位置を合わせている。
- 通り芯を1・2・3・4・5の5本にして、奥行方向のスパンを2,730以下に抑えた。

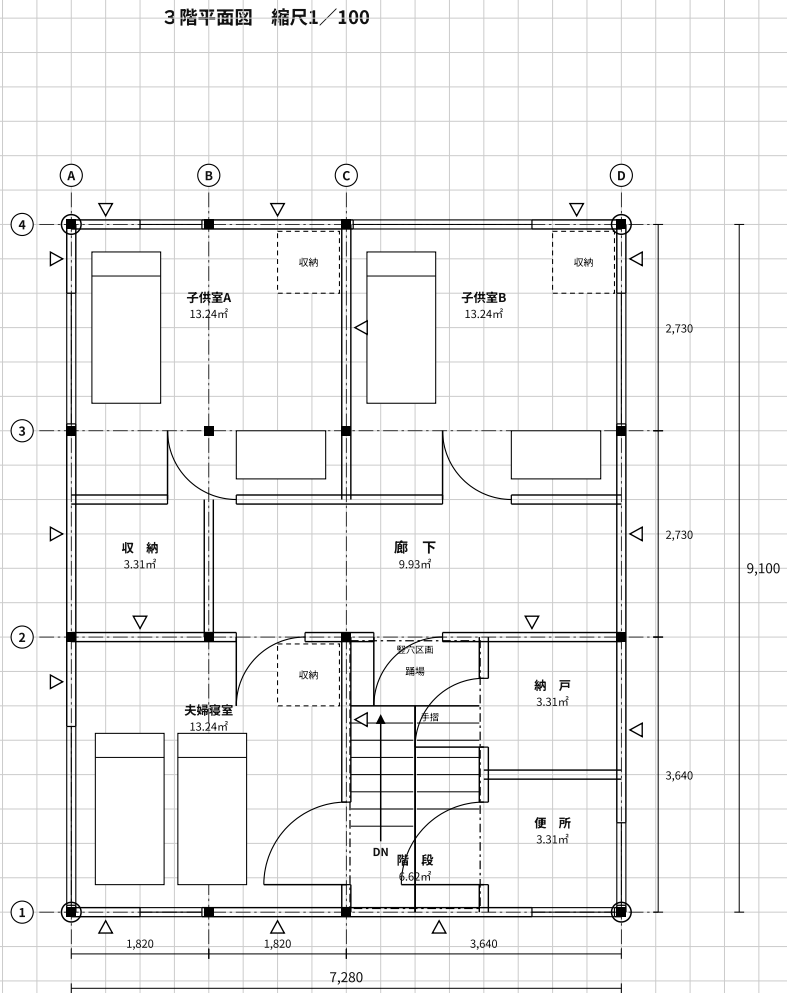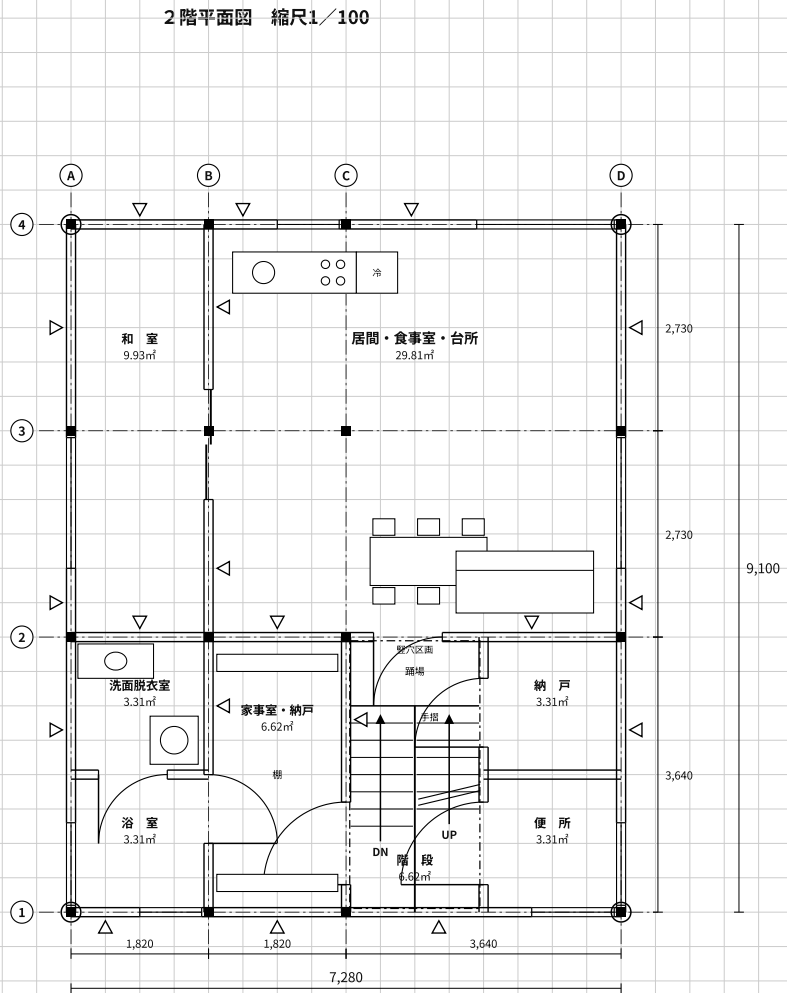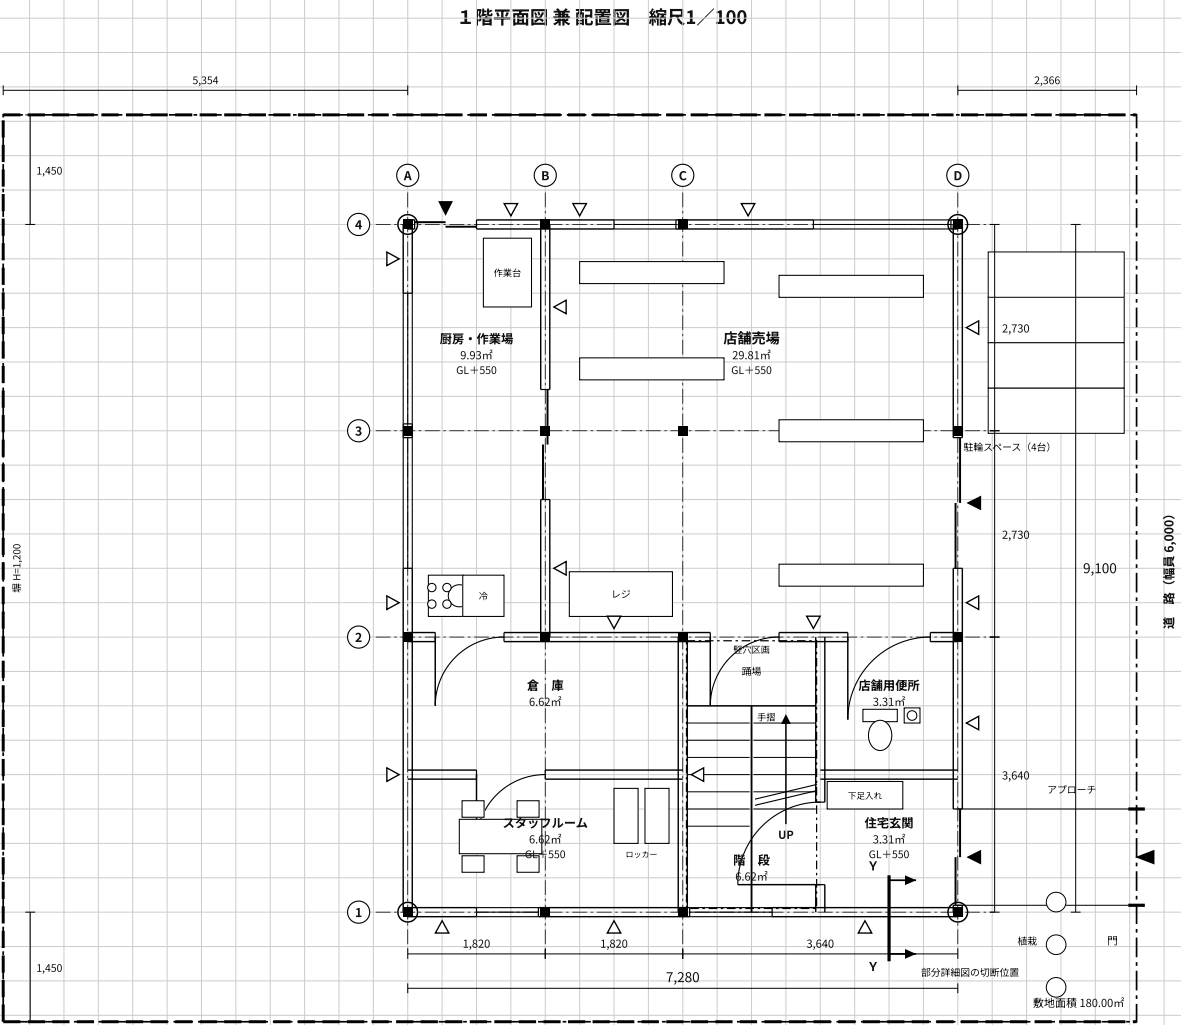

面積表

敷地面積		180.00	㎡
建築面積	(計算式) 7.28×9.10	66.24	㎡
床面積 1階 ア	(計算式) 7.28×9.10	66.24	㎡
2階 イ	(計算式) 7.28×9.10	66.24	㎡
3階 ウ	(計算式) 7.28×9.10	66.24	㎡
延べ面積 ア+イ+ウ		198.72	㎡

小数点以下第3位以下は切り捨て。計算式はm単位で書く。

凡例（床伏図兼小屋伏図の表示記号）

	通し柱	1階の管柱	2階の管柱	重なる管柱	胴差・桁（正角材）	同上（平角材）	同上（丸太材）	火打梁	棟木	母屋・小屋束
記号										
寸法	120×120	120×120	120×120	—	120×120	図中に記入	図中に記入	90×90	120×120	90×90

※ 平角材（120×240 など）の断面寸法は、この欄ではなく 床伏図の中の梁1本ずつのわきに記入する。




標準解答例

予想問題 D
東側道路の併用住宅（美容室）
木造3階建て 〳 8マス × 10マス (7,280 × 9,100)

※ 立面図・床伏図兼小屋伏図・部分詳細図は、別紙「共通図」をご覧ください。

この解答例のポイント

- 道路が東なので売場を東面に向け、店舗出入口も東に取っている。
- 階段を玄関の西となりへ動かし、住宅の動線が売場を通らないようにした。
- 通り芯の組み方を東西方向に変え、大梁のスパンを3,640以下に収めている。

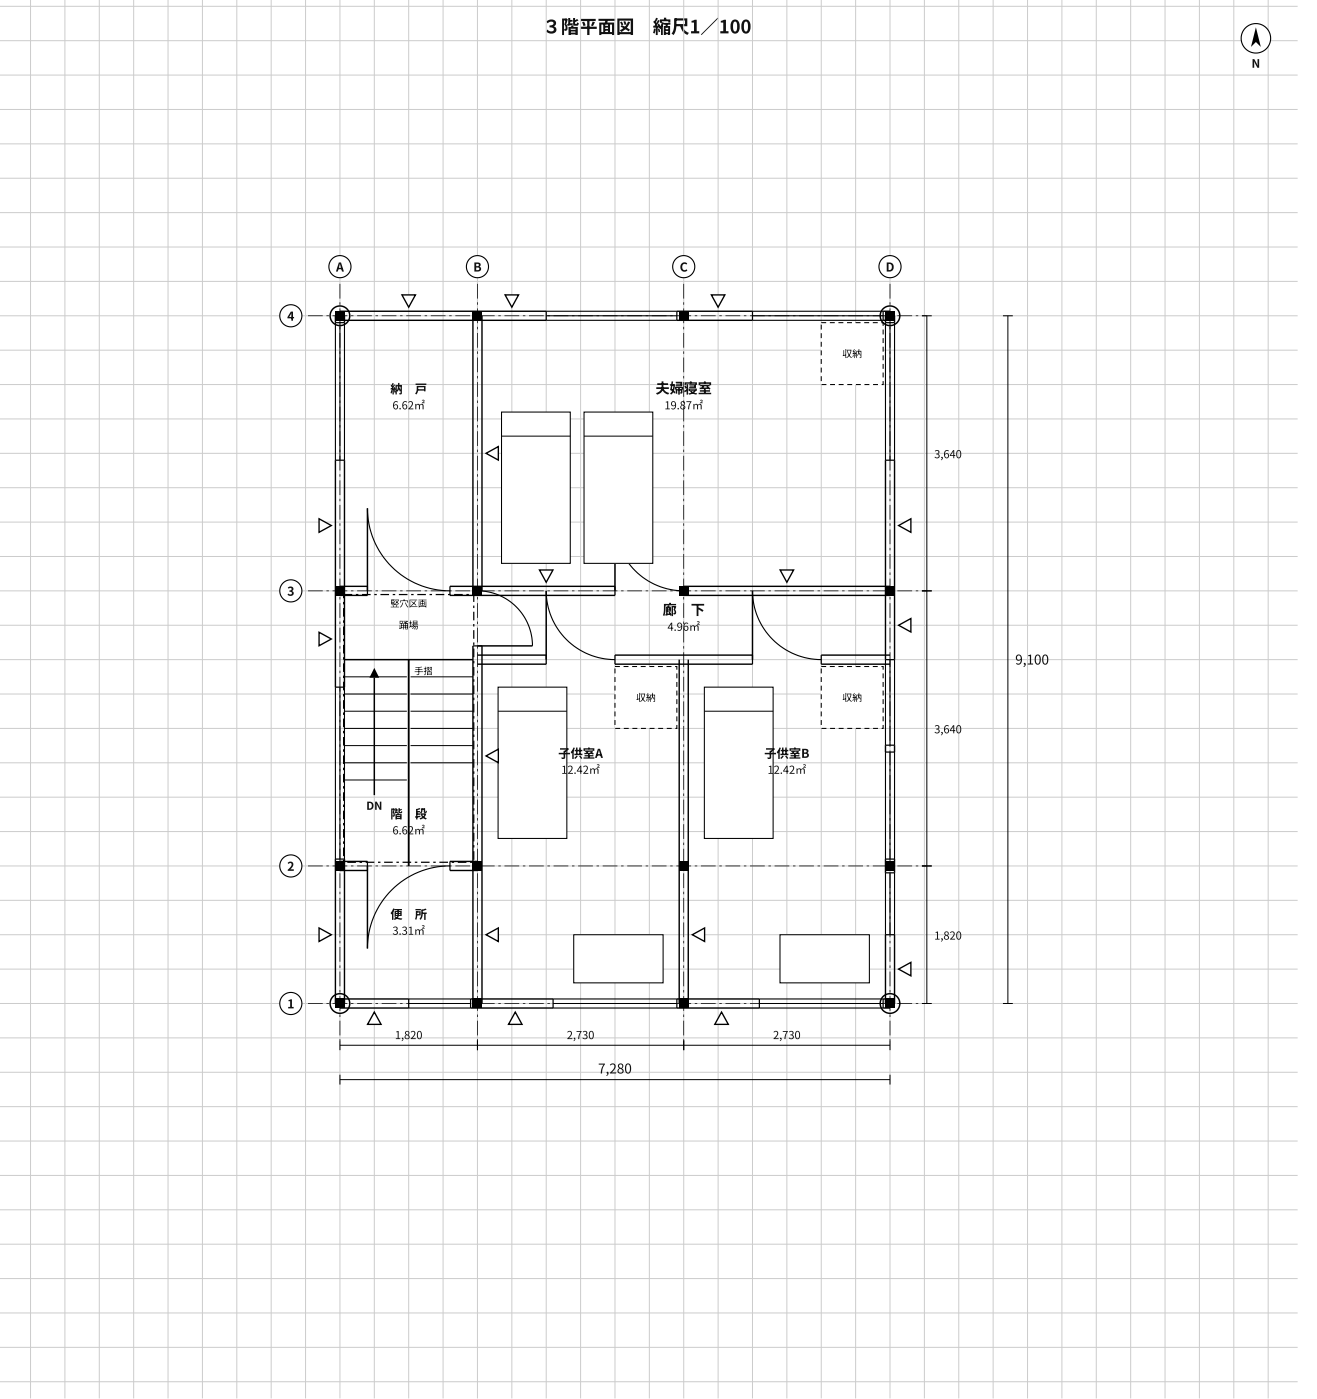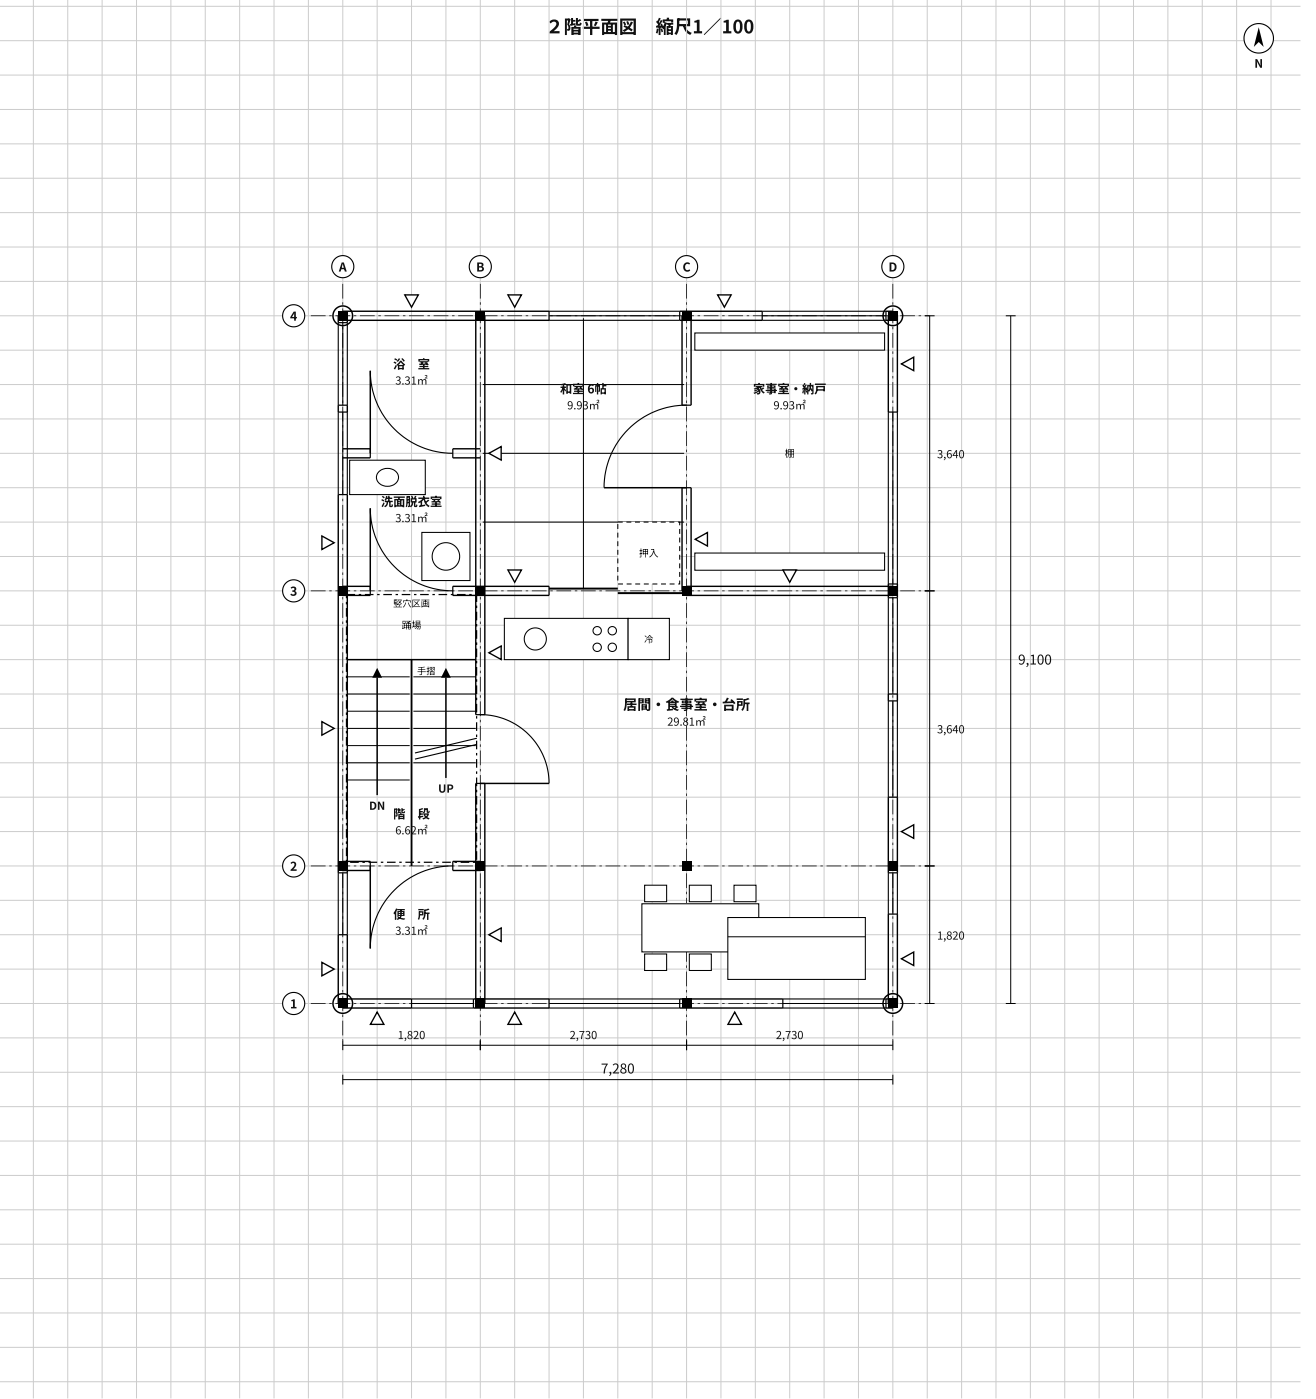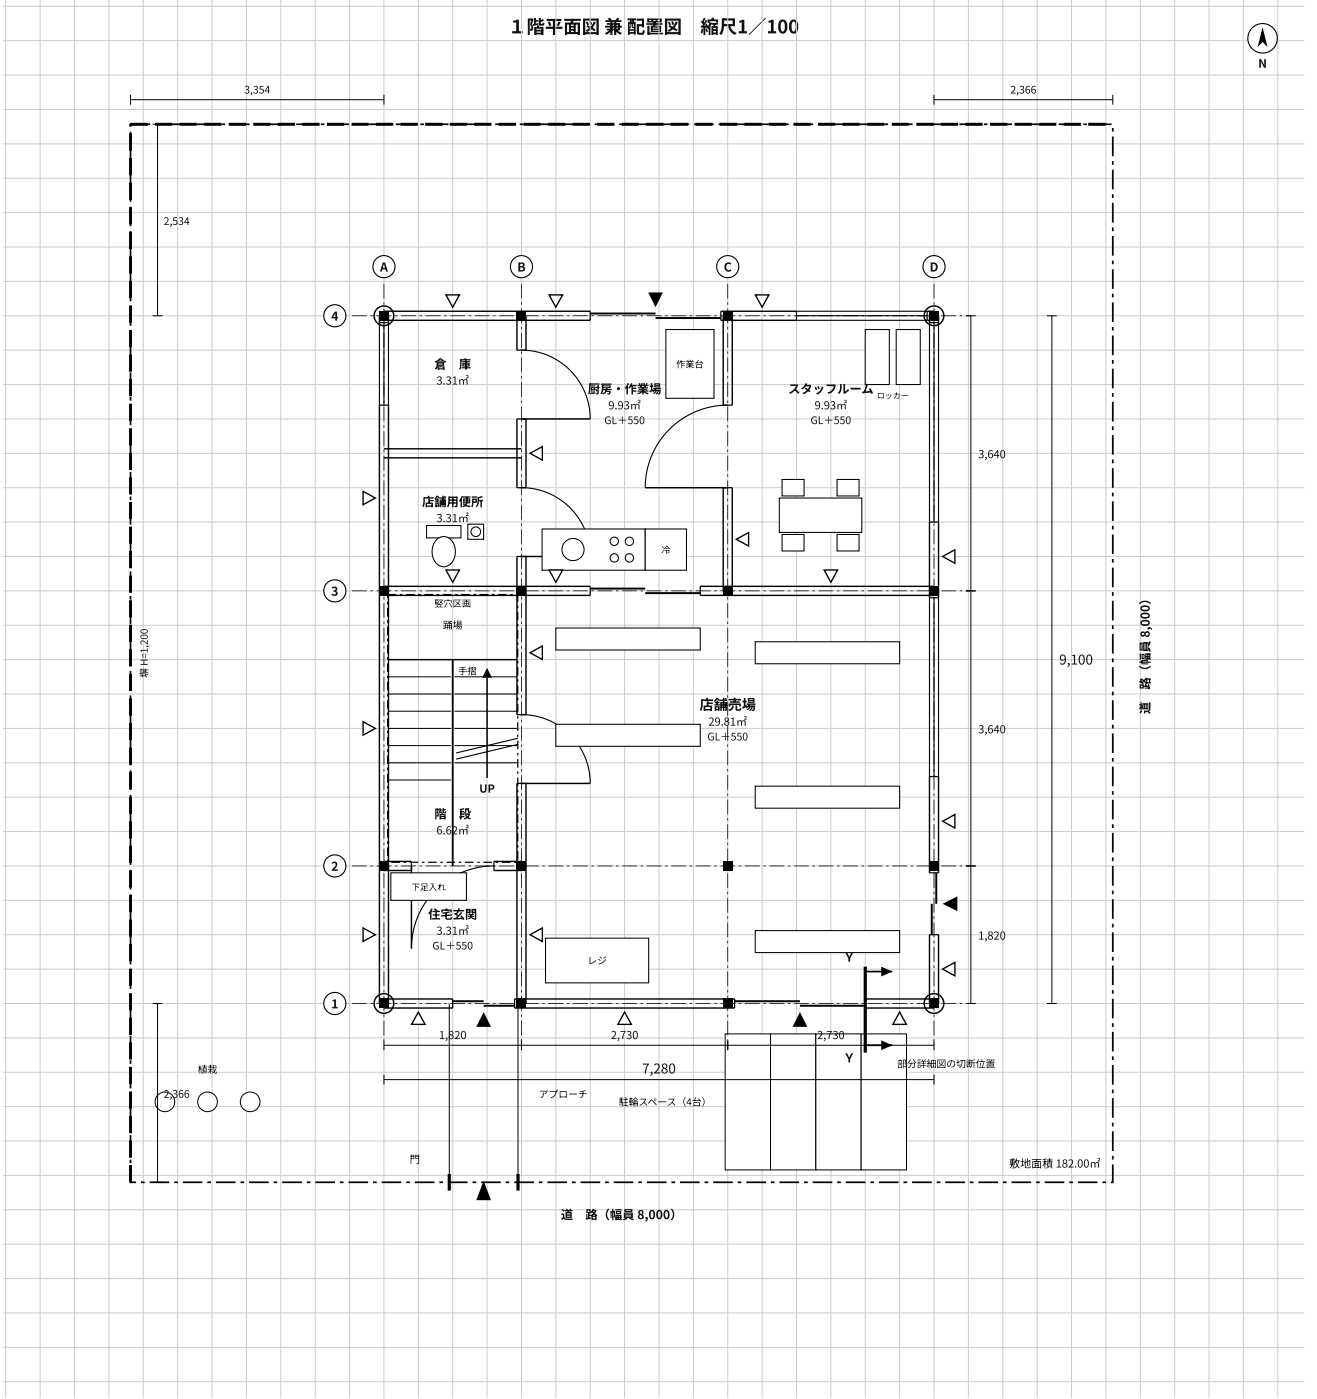

面積表

敷地面積		182.00	m ²
建築面積	(計算式) 7.28×9.10	66.24	m ²
床面積 1階 ア	(計算式) 7.28×9.10	66.24	m ²
2階 イ	(計算式) 7.28×9.10	66.24	m ²
3階 ウ	(計算式) 7.28×9.10	66.24	m ²
延べ面積 ア+イ+ウ		198.72	m ²

小数点以下第3位以下は切り捨て。計算式はm単位で書く。

凡例（床伏図兼小屋伏図の表示記号）

	通し柱	1階の管柱	2階の管柱	重なる管柱	胴差・桁（正角材）	同上（平角材）	同上（丸太材）	火打梁	棟木	母屋・小屋束
記号										
寸法	120×120	120×120	120×120	—	120×120	図中に記入	図中に記入	90×90	120×120	90×90

※ 平角材（120×240 など）の断面寸法は、この欄ではなく 床伏図の中の梁1本ずつのわきに記入する。

標準解答例

予想問題 E

南東の角地に建つ併用住宅（パン店）
木造3階建て ／ 8マス × 10マス（7,280 × 9,100）

※ 立面図・床伏図兼小屋伏図・部分詳細図は、別紙「共通図」を見てください。

この解答例のポイント

- ・ 南と東の2面が道路なので、店舗出入口を角に向けて開いている。
- ・ 東面にも窓を取り、売場と住宅の採光を両方から確保している。
- ・ 角地の建蔽率の割増し（法53条3項）を使える敷地としている。




面積表

敷地面積		180.00	m ²
建築面積	(計算式) 7.28×9.10	66.24	m ²
床面積 1階 ア	(計算式) 7.28×9.10	66.24	m ²
2階 イ	(計算式) 7.28×9.10	66.24	m ²
3階 ウ	(計算式) 7.28×9.10	66.24	m ²
延べ面積 ア+イ+ウ		198.72	m ²

小数点以下第3位以下は切り捨て。計算式はm単位で書く。

この解答例のポイント

- 道路が北なので、1階だけ南北を入れかえて店舗を北（道路側）に向けた。
- 階段の位置は動かさないなので、2階・3階は型のまま使える。
- 住宅の居室は南側に集め、日当たりを確保している。

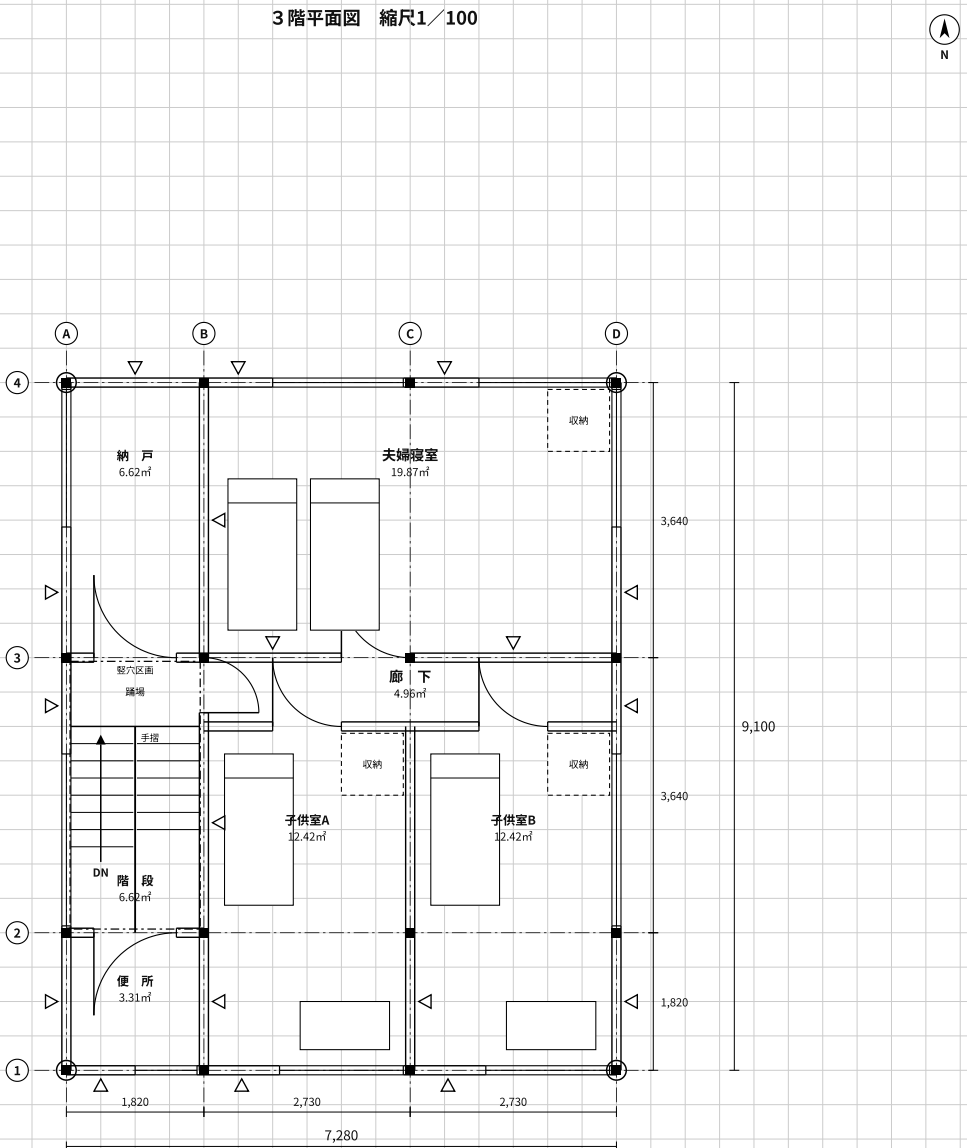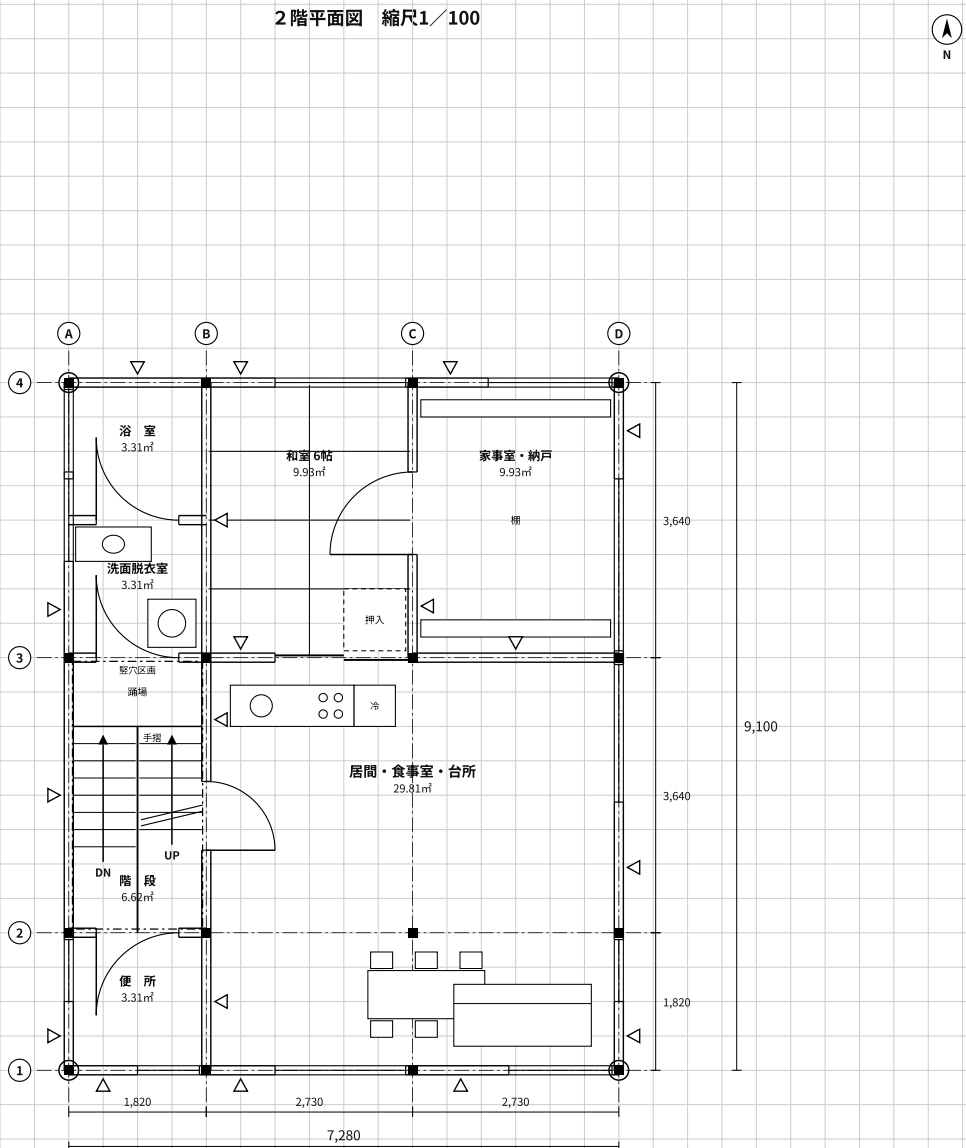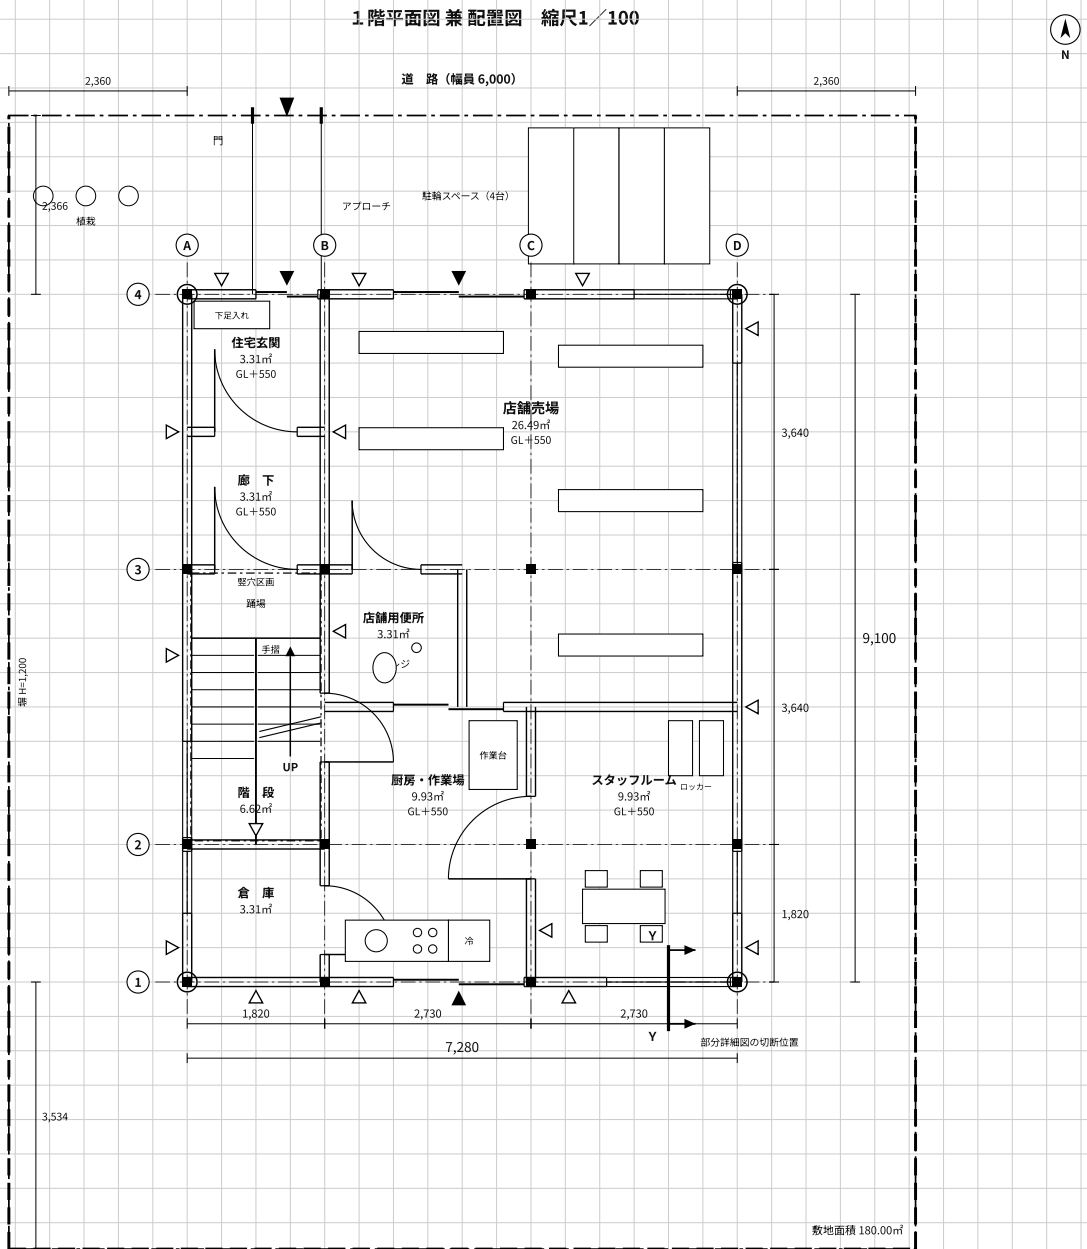

凡例（床伏図兼小屋伏図の表示記号）

	通し柱	1階の管柱	2階の管柱	重なる管柱	胴差・桁（正角材）	同上（平角材）	同上（丸太材）	火打梁	棟木	母屋・小屋束
記号										
寸法	120×120	120×120	120×120	—	120×120	図中に記入	図中に記入	90×90	120×120	90×90



※ 平角材（120×240 など）の断面寸法は、この欄ではなく 床伏図の中の梁1本ずつのわきに記入する。

標準解答例


予想問題 F

北側道路の併用住宅（書店）
木造3階建て 〳 8マス × 10マス（7,280 × 9,100）

※ 立面図・床伏図兼小屋伏図・部分詳細図は、別紙「共通図」をご覧ください。

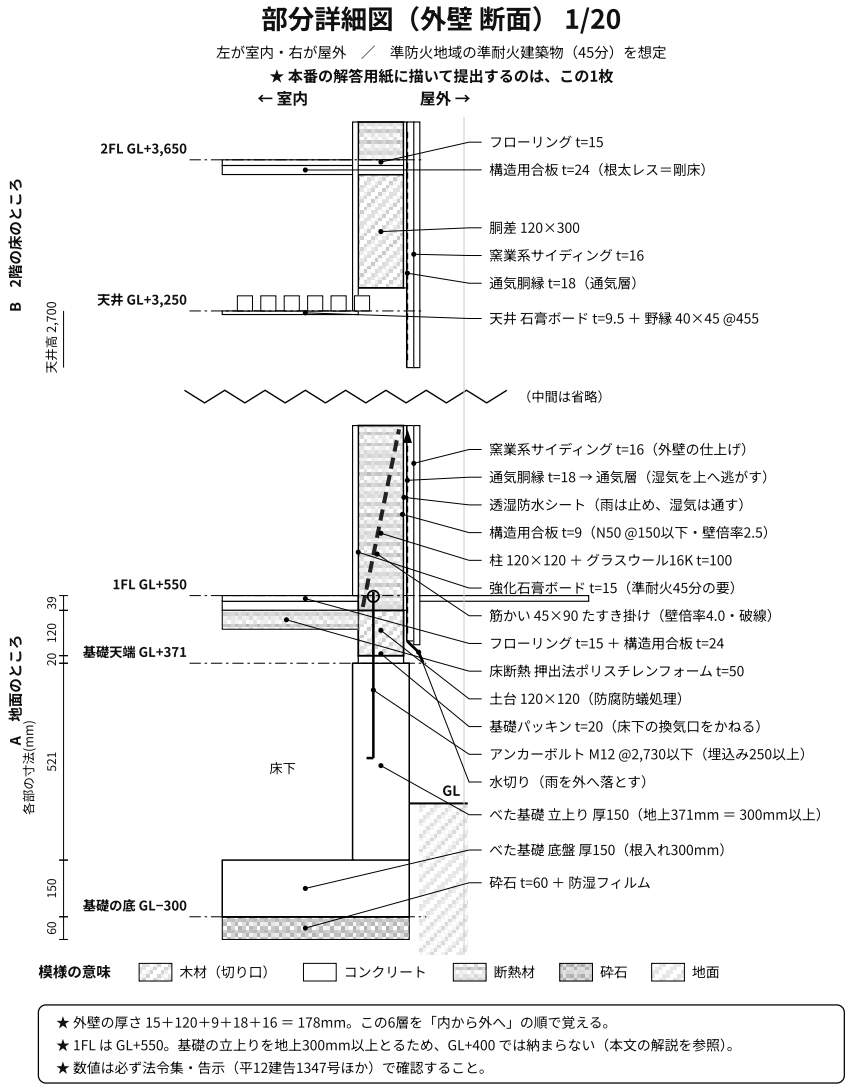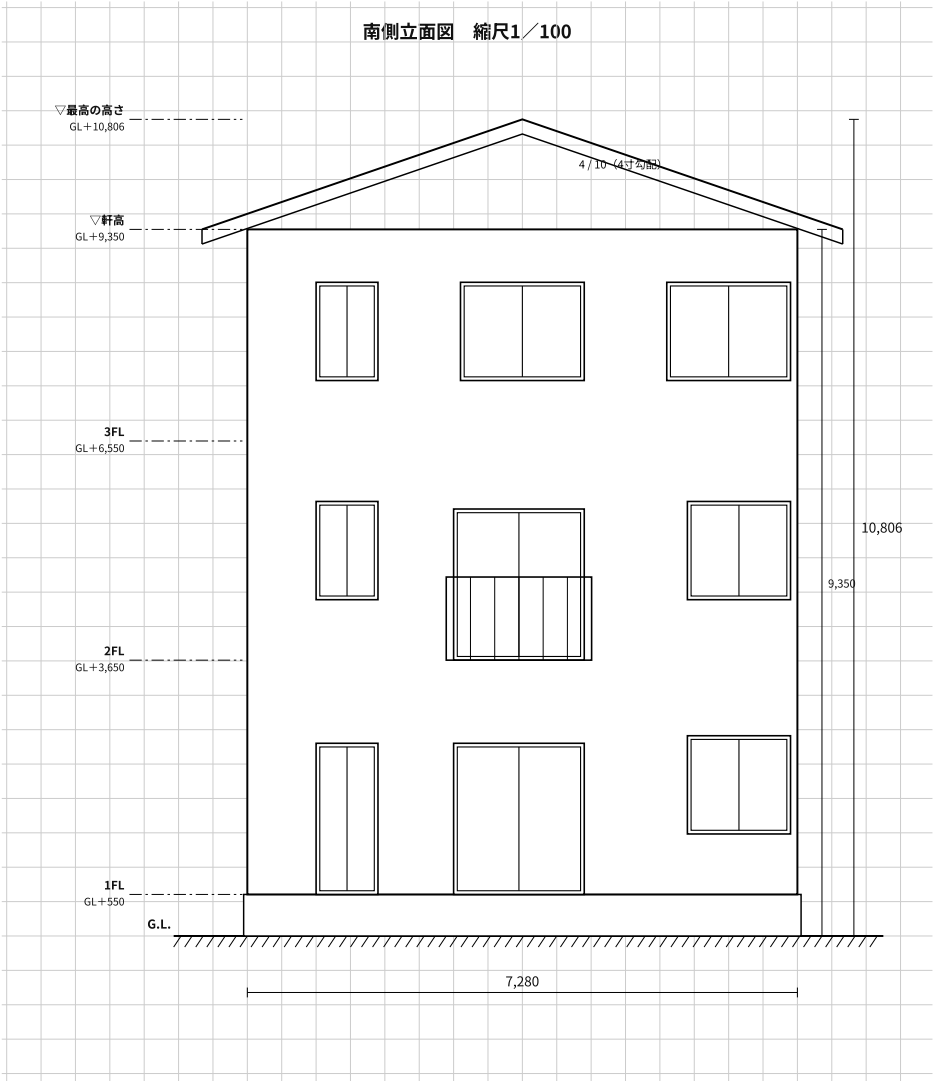

※ この2枚は「型 (8マス×10マス)」のもの。問題B (9マス)・C (7マス) は間口が違うので寸法を読みかえる。

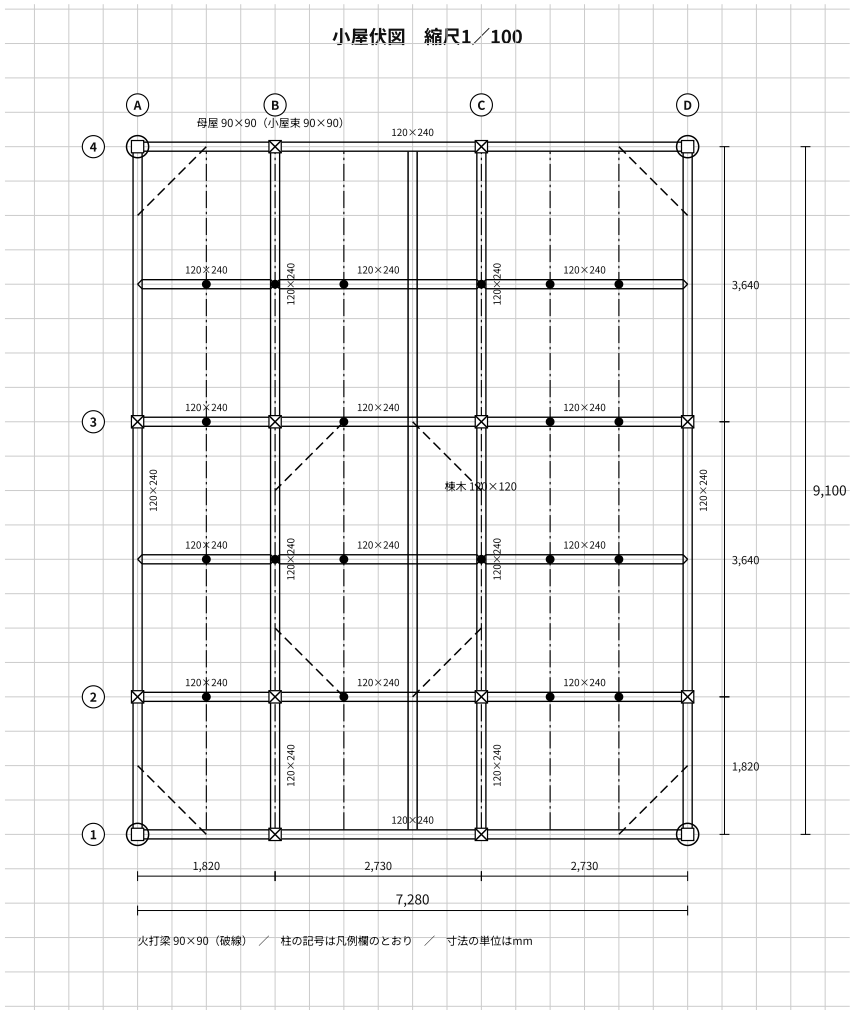

※ 2階の床伏図と3階の床伏図は同じ組み方でよい。小屋伏図は棟が南北方向・4寸勾配。