
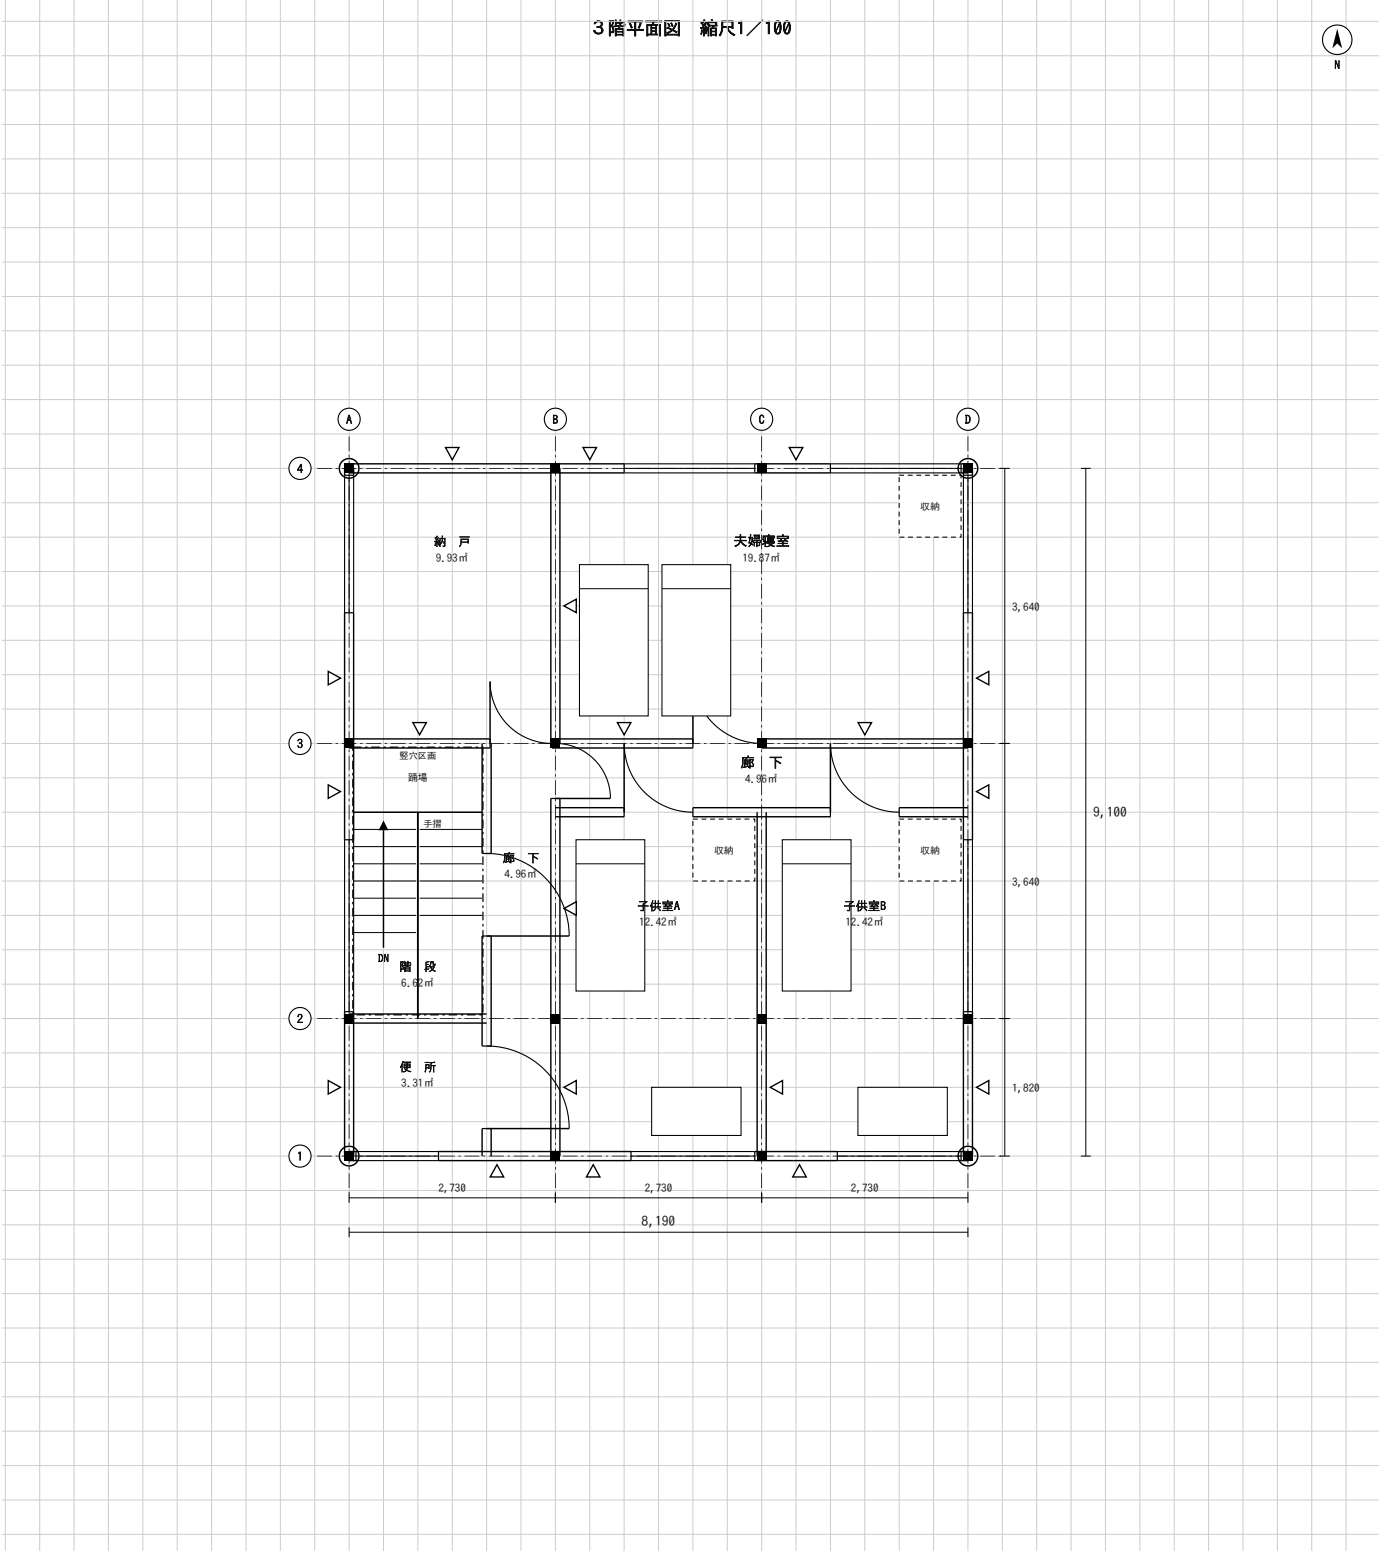
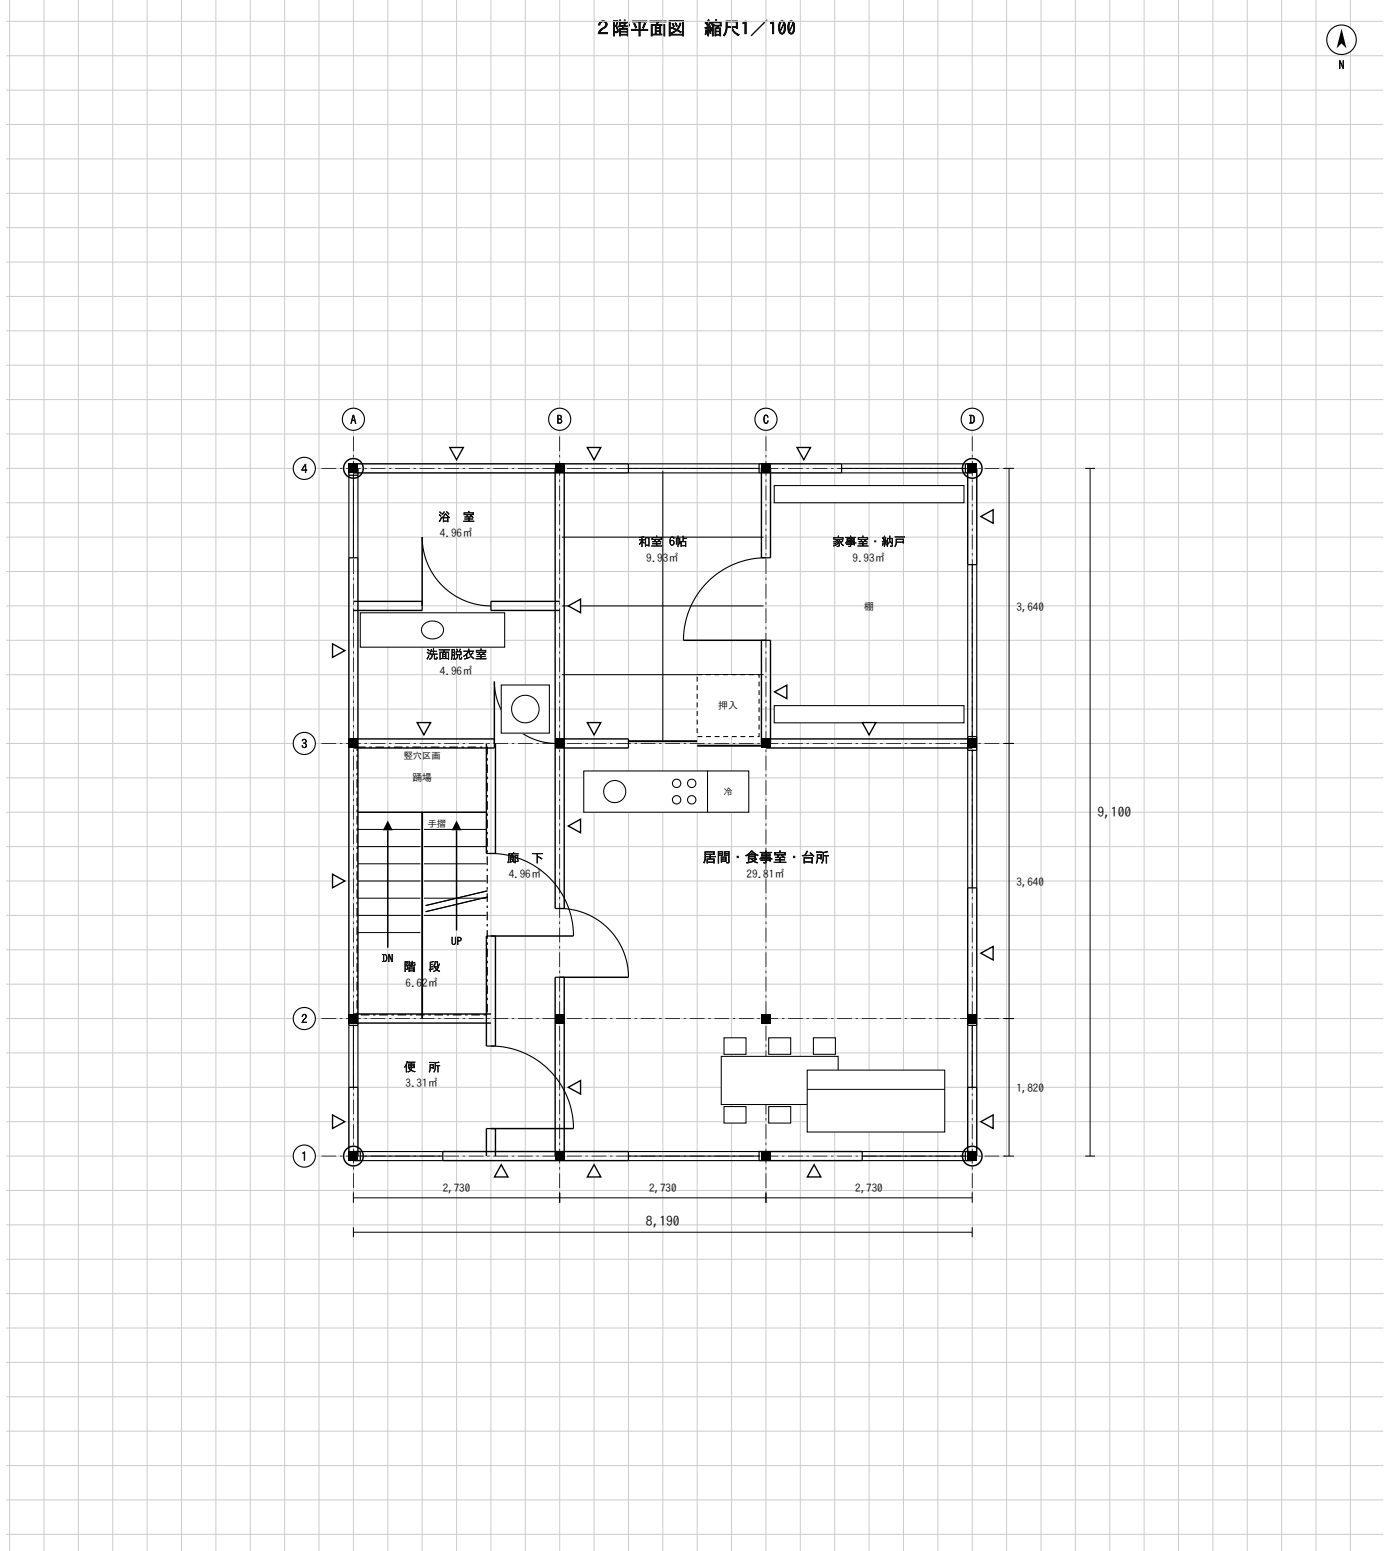


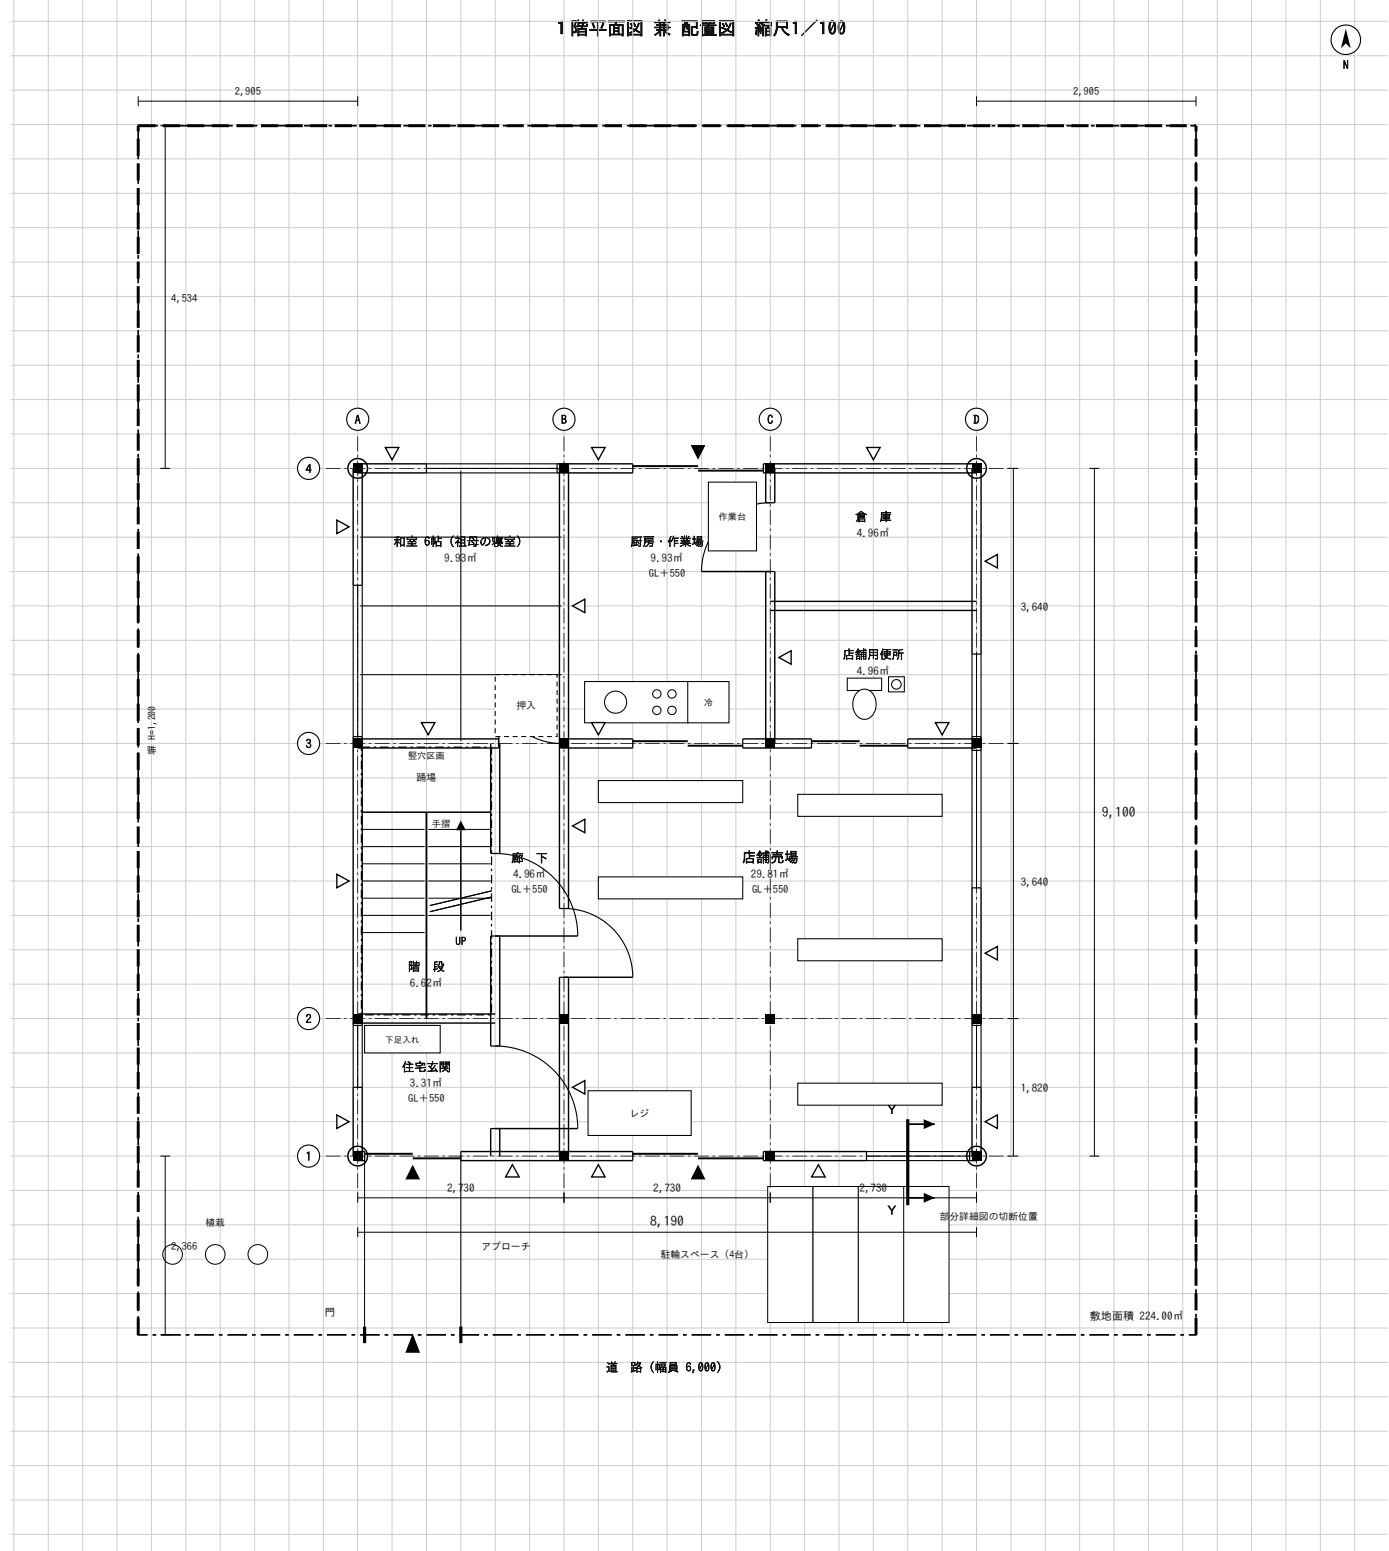

面積表

敷地面積		224.00㎡
建築面積	(計算式) 8.19×9.10	74.52㎡
床面積 1階 ア	(計算式) 8.19×9.10	74.52㎡
2階 イ	(計算式) 8.19×9.10	74.52㎡
3階 ウ	(計算式) 8.19×9.10	74.52㎡
延べ面積 ア+イ+ウ		223.56㎡

小数点以下第3位以下は切り捨て。計算式はm単位で書く。

凡例（床伏図兼小屋伏図の表示記号）

	通し柱	1階の管柱	2階の管柱	重なる管柱	胴差・桁（正角材）	同上（平角材）	同上（丸太材）	火打梁	棟木・小屋束	母屋・小屋束
記号										
寸法	120×120	120×120	120×120	—	120×120	図中に記入	図中に記入	90×90	120×120	90×90

標準解答例

予想問題 B



祖母と暮らす併用住宅（和菓子店）

木造3階建て / 9マス × 10マス (8,190 × 9,100)


※ 立面図・床伏図兼小屋伏図・部分詳細図は、別紙「共通図」をご覧ください。

この解答例のポイント

- 1階の西側を3マス幅にして廊下を通し、その北に祖母の和室6帖を置いている。
- 和室から便所・洗面へ廊下1本で行けるようにして、段差をなくしている。
- 間口を9マスに広げたぶん、通り芯をA・B・C・Dの4本に組みかえている。

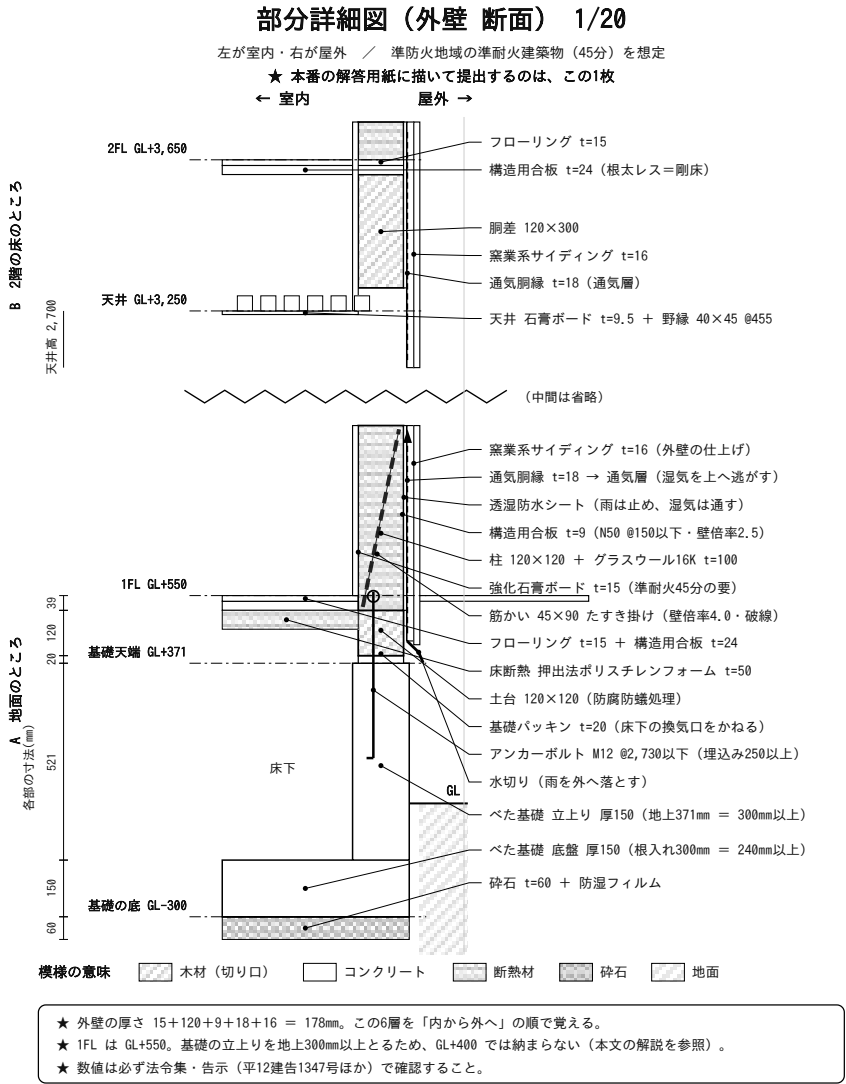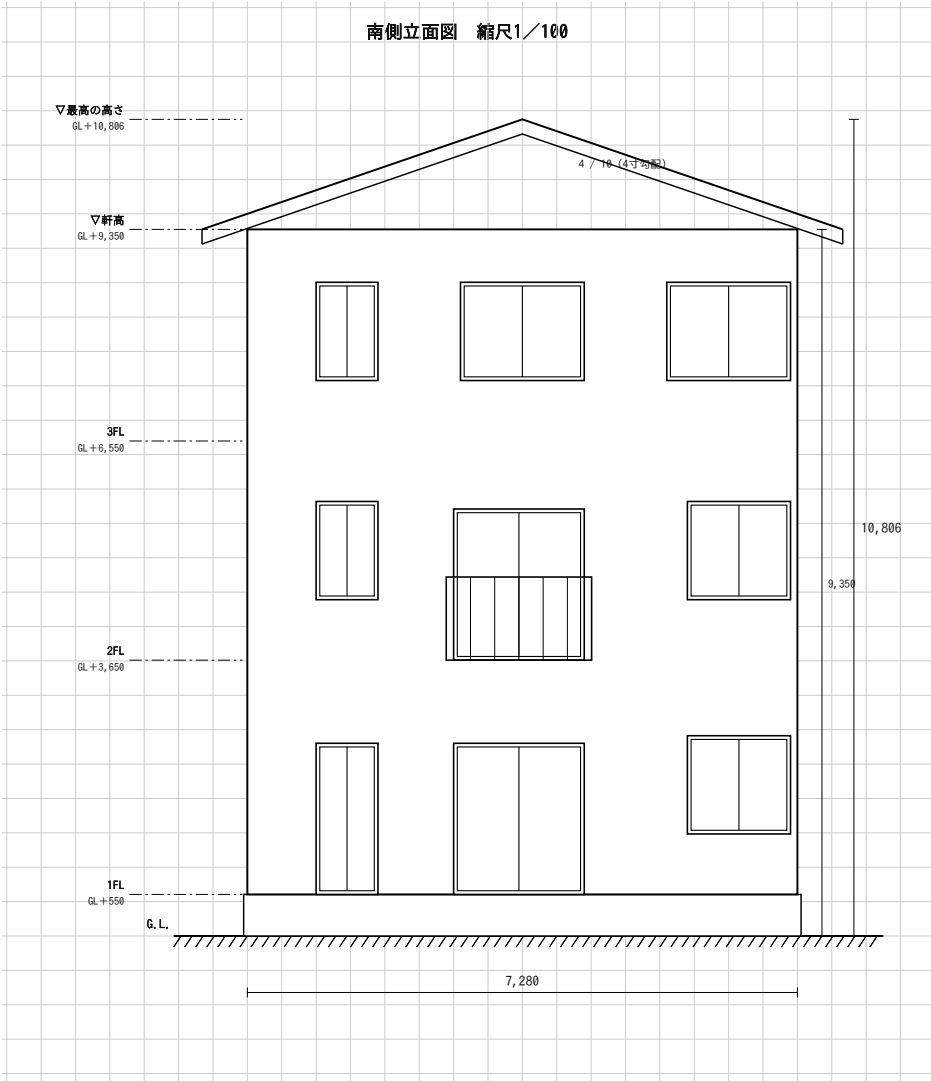

※ この2枚は「型 (8マス×10マス)」のもの。問題B (9マス)・C (7マス) は間口が違うので寸法を読みかえる。

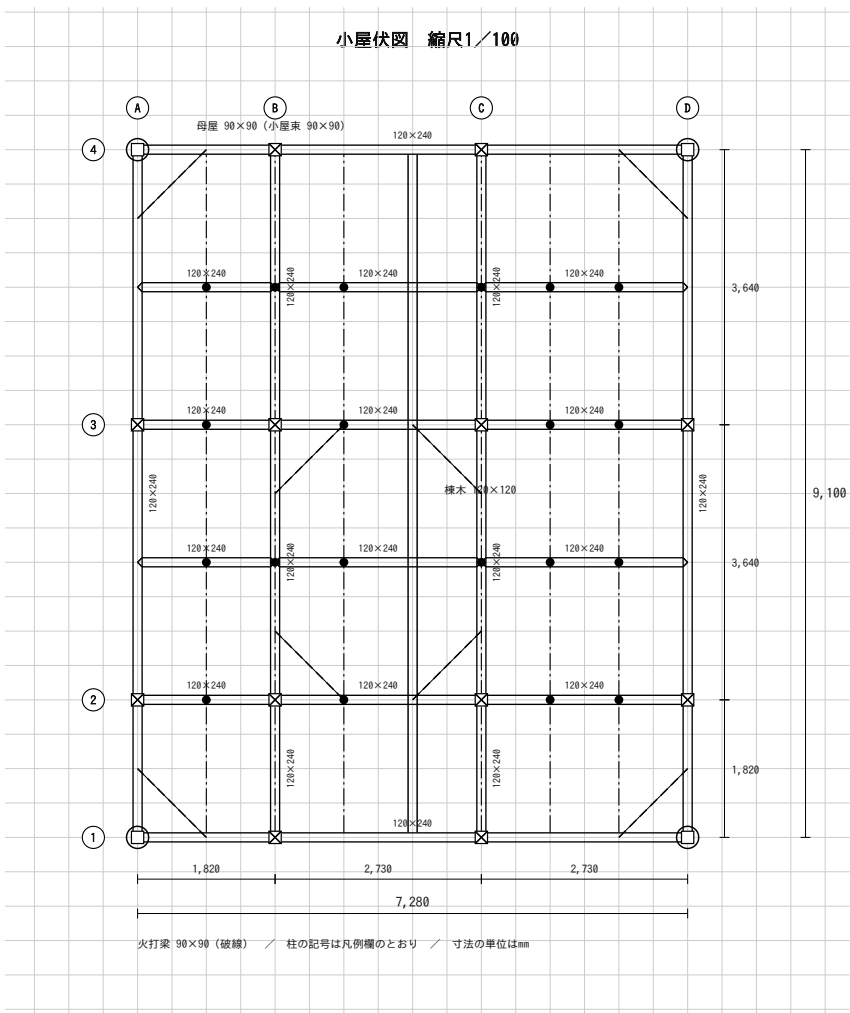

※ 2階の床伏図と3階の床伏図は同じ組み方でよい。小屋伏図は棟が南北方向・4寸勾配。