




(1) 1階平面図 兼 配置図 縮尺1／100

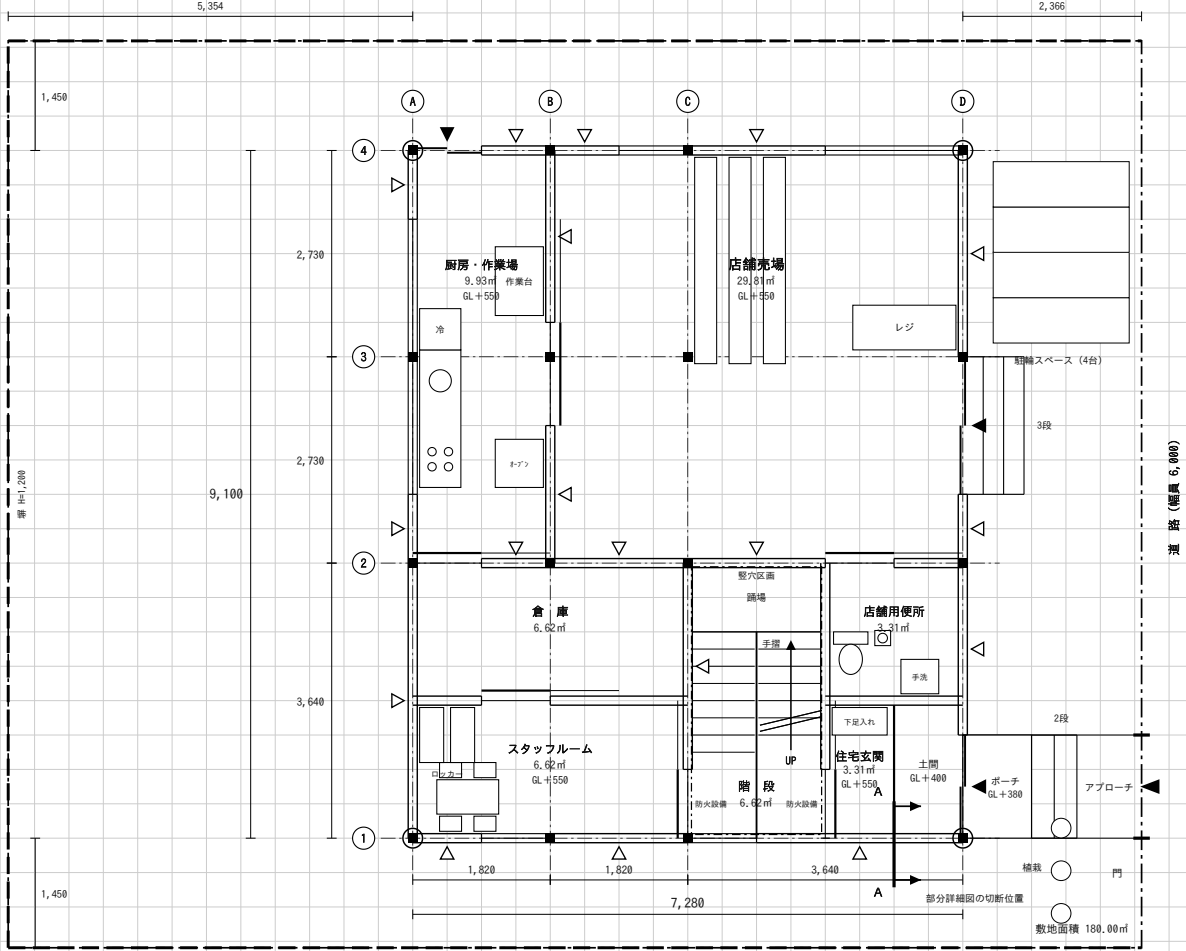

(2) 2階平面図 縮尺1／100

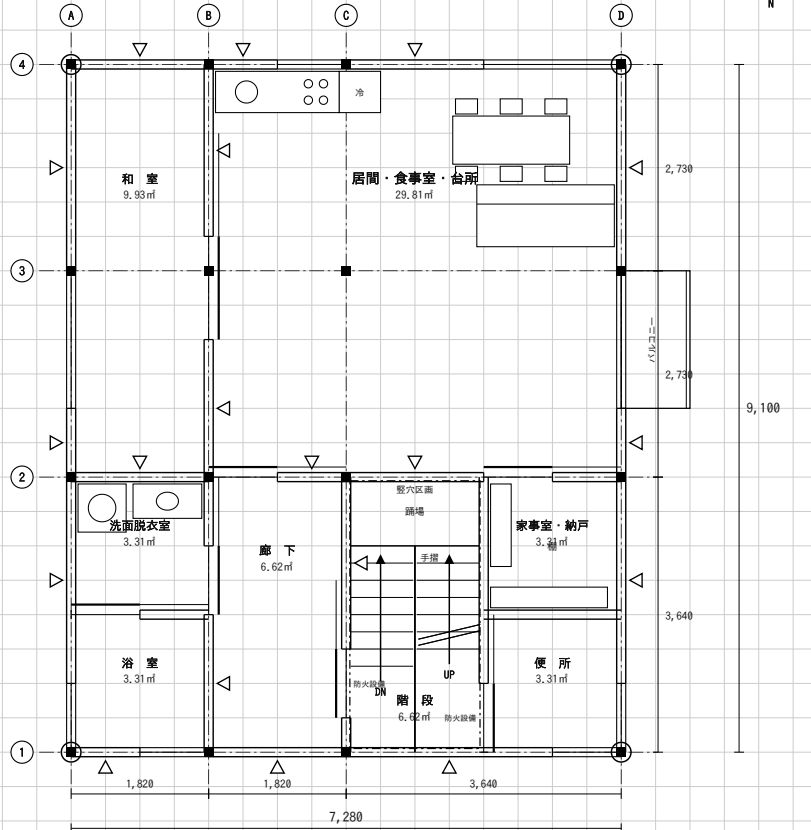

(3) 3階平面図 縮尺1／100

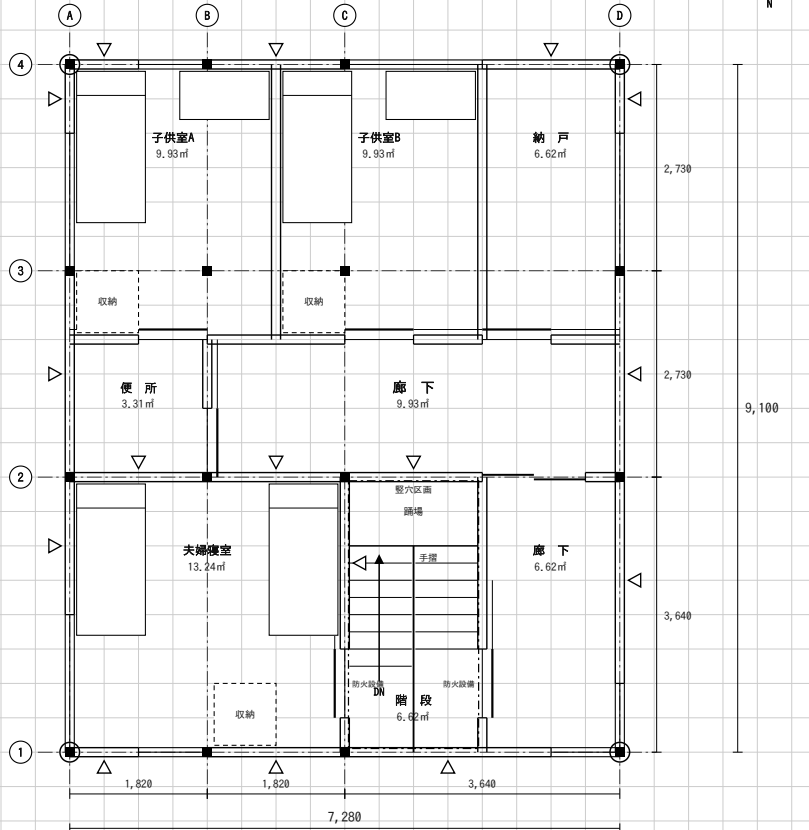


(7) 面積表


敷地面積	180.00	m ²
建築面積 (計算式) 7.28×9.10	66.24	m ²
床面積 1階 ア (計算式) 7.28×9.10	66.24	m ²
2階 イ (計算式) 7.28×9.10	66.24	m ²
3階 ウ (計算式) 7.28×9.10	66.24	m ²
延べ面積 ア+イ+ウ	198.72	m ²

※ 小数点以下第3位以下は切り捨て。計算式はm単位で書く。


(4) 3階床伏図 (1／100)

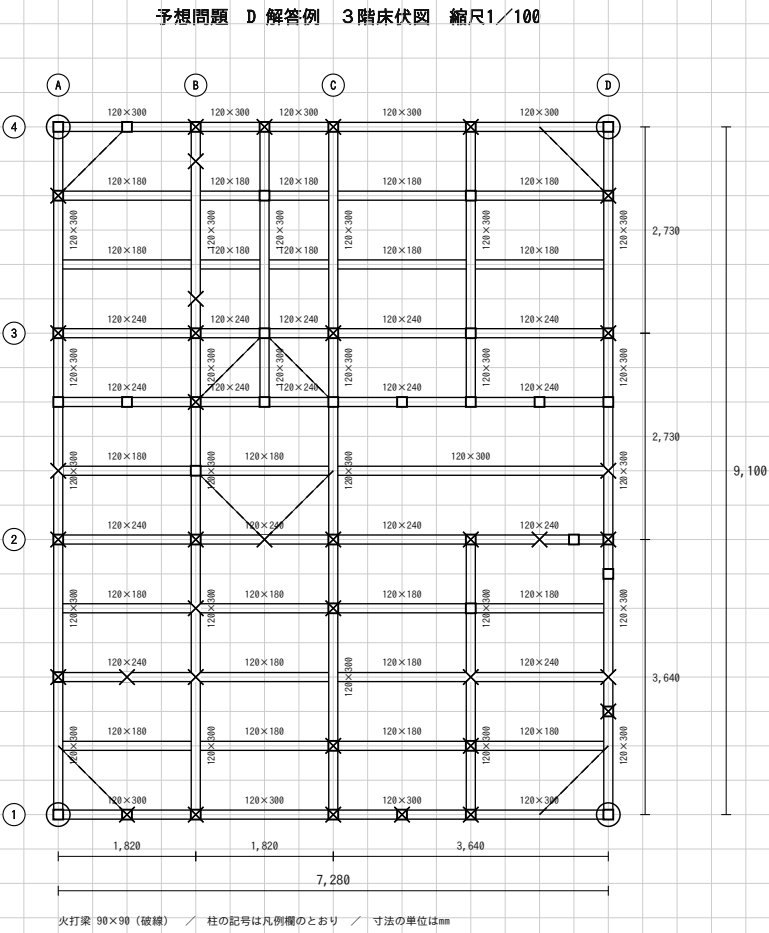


(4) 小屋伏図 (1／100)

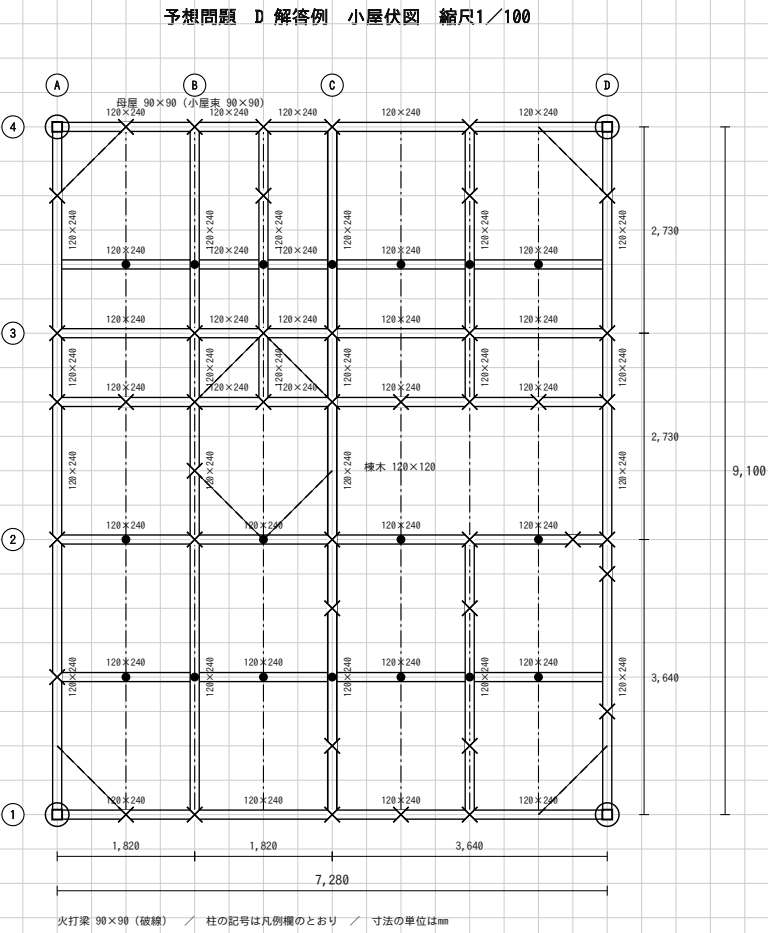

(5) 南側立面図 (1／100)

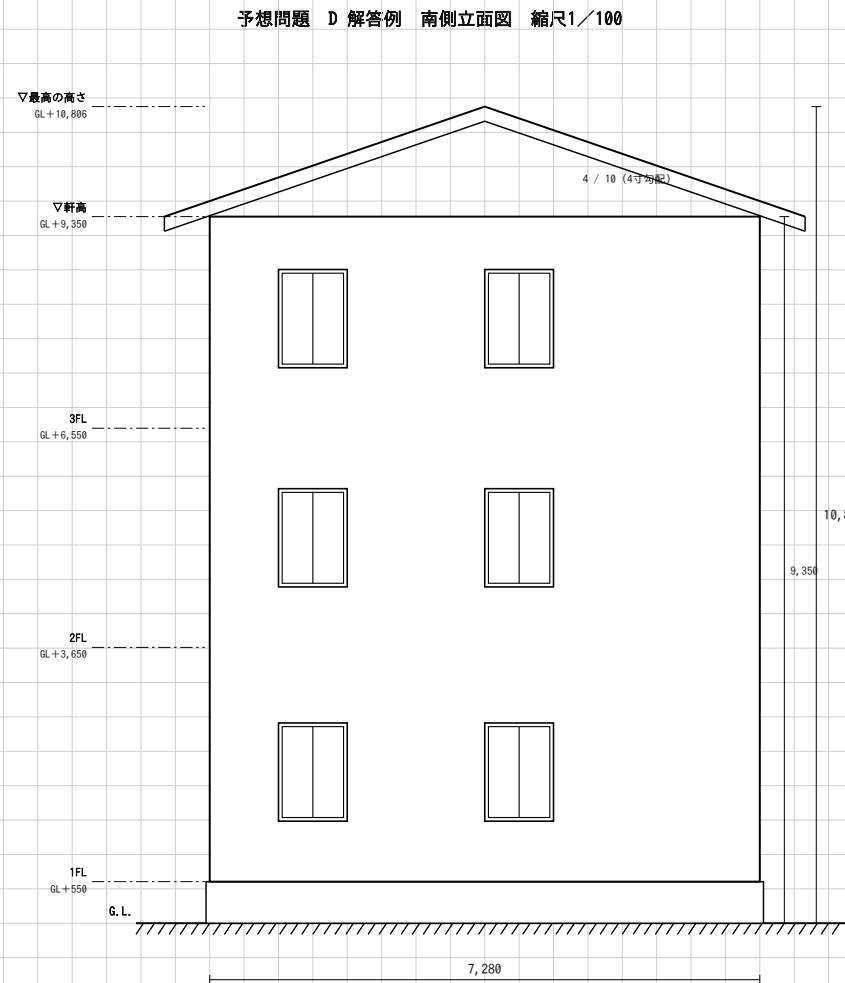

(6) 部分詳細図 (断面) (1／20)

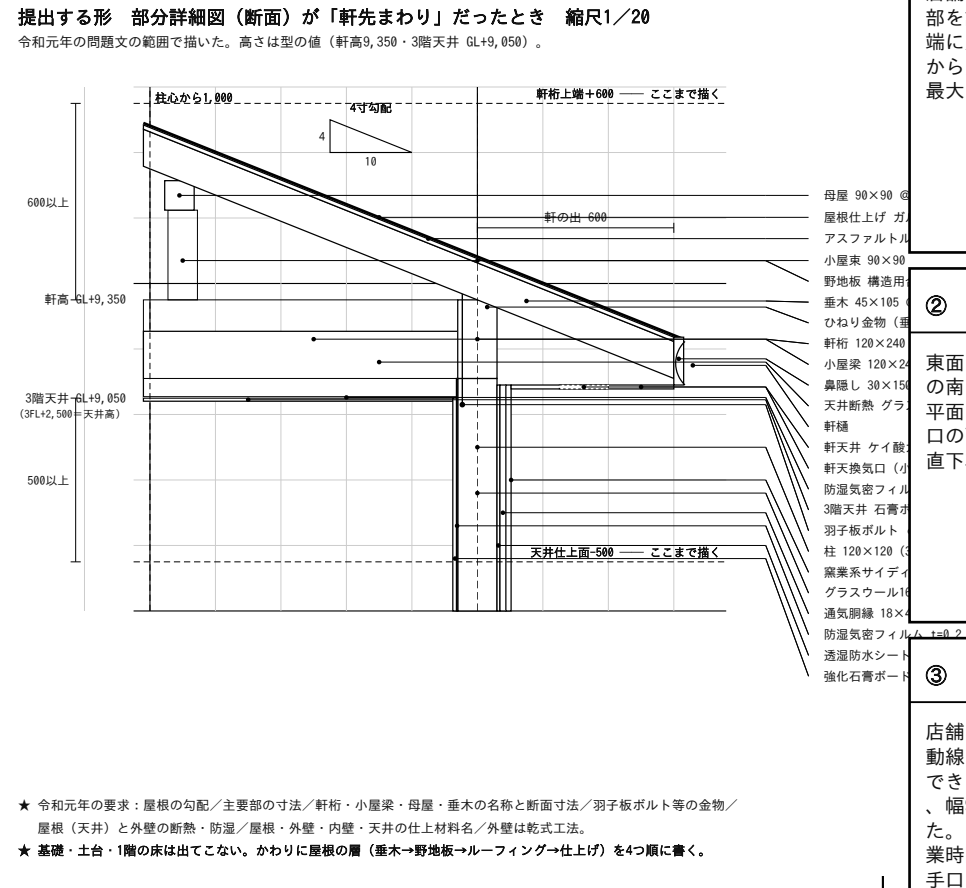

(8) 計画の要点等

① 東側道路に対して、平面計画上工夫した点

店舗売場を建築物の東側に配置し、道路に面する東面に出入口と大きな開口部を設けて、通りから店内が見えるようにした。住宅の玄関は同じ東面の南端に別に設け、来店客と住まい手の出入口を分けている。厨房・倉庫は道路から見えない西側にまとめ、北面の勝手口から搬入できるようにした。梁の最大スパンは3,640mmに抑え、柱の位置は各階共通としている。

② 階段の位置と直下率について工夫した点

東面は店舗売場と住宅玄関で使い切るため、階段は玄関の西となり（建築物の南中央）に配置した。この位置を1階から3階まで変えず、2階・3階の平面も同じ階段位置を前提に組み立てている。柱は通り芯の交点と窓・出入口の両わきに各階共通で配置し、柱と柱の間隔は1,820mm以下として直下率を高めた。梁の最大スパンは3,640mmに抑えている。

③ 店舗部分と住宅部分の動線計画について工夫した点

店舗の出入口は道路に面して設け、来店客は店舗売場から店舗用便所へ至る動線とした。店舗用便所は売場の一部を区画して設け、厨房を通らずに利用できるようにしている。住宅の玄関は店舗の出入口と壁をへだてて別に設け、幅910mm（有効約780mm）の廊下ですぐ階段へ上られる配置とした。これにより住まい手が売場を通らずに2階・3階へ行くことができ、営業時間中も両者の動線が交錯しない。商品及び材料の搬入は建築物背面の勝手口から厨房・倉庫へ直接行える。

凡 例（床伏図兼小屋伏図の表示記号）

	通し柱	1階の管柱	2階の管柱	重なる管柱	胴差・桁（正角材）	同上（平角材）	同上（丸太材）	火打梁	棟木	母屋・小屋束
記号										
寸法	120×120	120×120	120×120	—	120×120	図中に記入	図中に記入	90×90	120×120	90×90

※ 平角材（120×240 など）の断面寸法は、この欄ではなく 床伏図の中の梁1本ずつのわきに記入する。

標準解答例

予想問題 D 東側道路の併用住宅（美容室）

木造3階建て / 8マス × 10マス（7,280 × 9,100）

- ・道路が東なので売場を東面に向け、店舗出入口も東に取っている。
- ・階段を玄関の西となりへ動かし、住宅の動線が売場を通らないようにした。
- ・通り芯の組み方を東西方向に変え、大梁のスパンを3,640以下に収めている。