




1 階平面図 兼 配置図 縮尺1／100

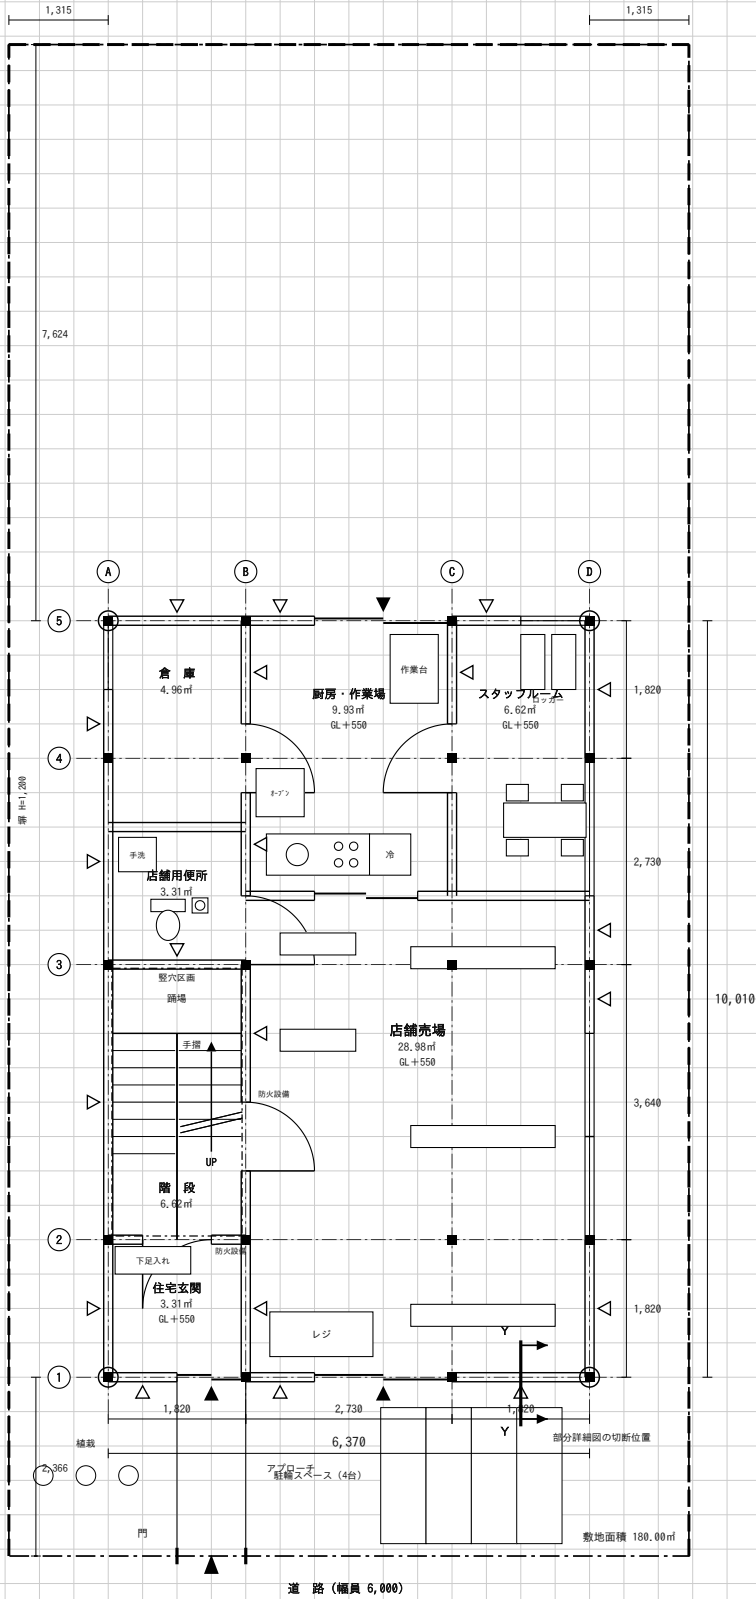

2 階平面図 縮尺1／100

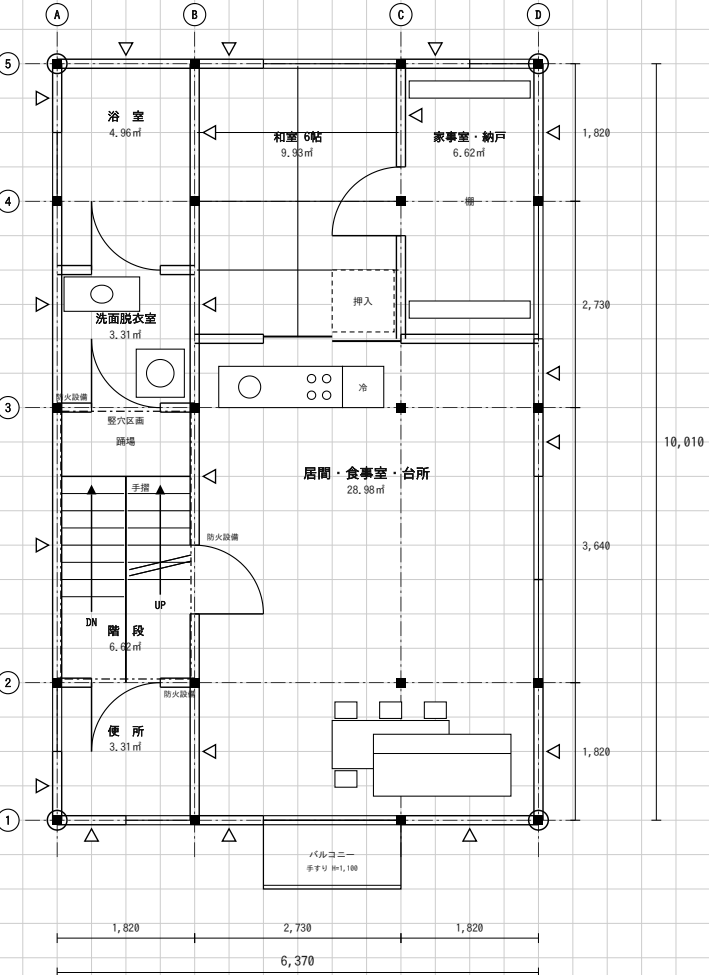

3 階平面図 縮尺1／100

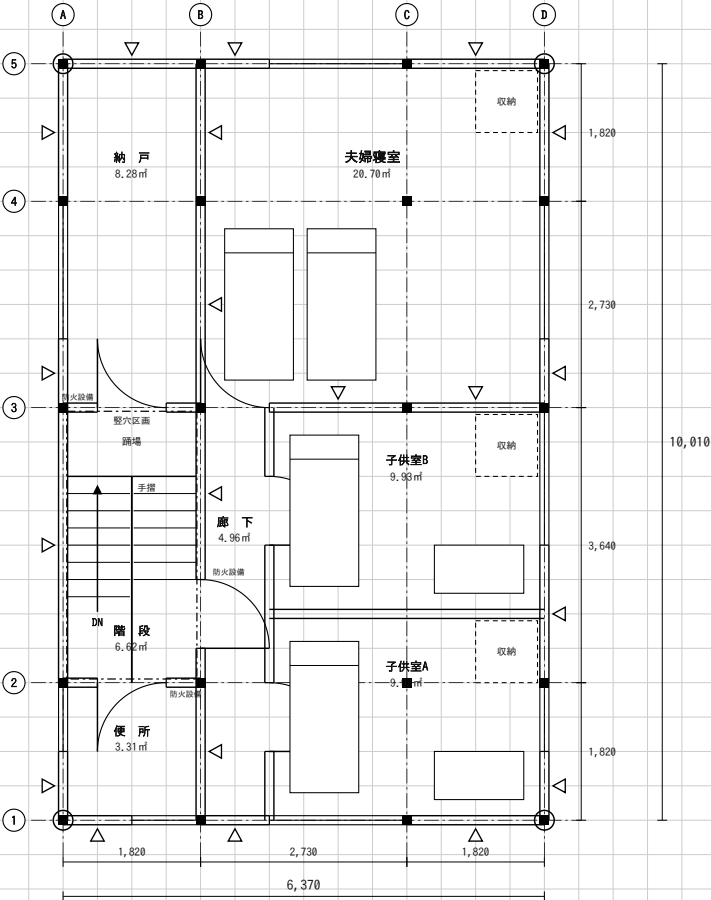

面 積 表

敷地面積		180.00㎡
建築面積	(計算式) 6.37×10.01	63.76㎡
床面積 1階 ア	(計算式) 6.37×10.01	63.76㎡
2階 イ	(計算式) 6.37×10.01	63.76㎡
3階 ウ	(計算式) 6.37×10.01	63.76㎡
延べ面積 ア+イ+ウ		191.28㎡

小数点以下第3位以下は切り捨て。計算式はm単位で書く。

凡 例（床伏図兼小屋伏図の表示記号）

	通し柱	1階の管柱	2階の管柱	重なる管柱	胴差・桁（正角材）	同上（平角材）	同上（丸太材）	火打梁	棟木	母屋・小屋束
記号										
寸法	120×120	120×120	120×120	—	120×120	図中に記入	図中に記入	90×90	120×120	90×90

※ 平角材（120×240 など）の断面寸法は、この欄ではなく 床伏図の中の梁1本ずつのわきに記入する。

標 準 解 答 例



予想問題 C

間口の狭い敷地の併用住宅（喫茶店）
木造3階建て ／ 7マス × 11マス（6,370 × 10,010）



※ 立面図・床伏図兼小屋伏図・部分詳細図は、別紙「共通図」をご覧ください。

この解答例のポイント

- ・ 間口が狭いので7マス×11マスとし、売場を奥へ長く取っている。
- ・ 水まわりを西の列にそろえて、1階から3階まで配管の位置を合わせている。
- ・ 通り芯を1・2・3・4・5の5本にして、奥行方向のスパンを2,730以下に抑えた。

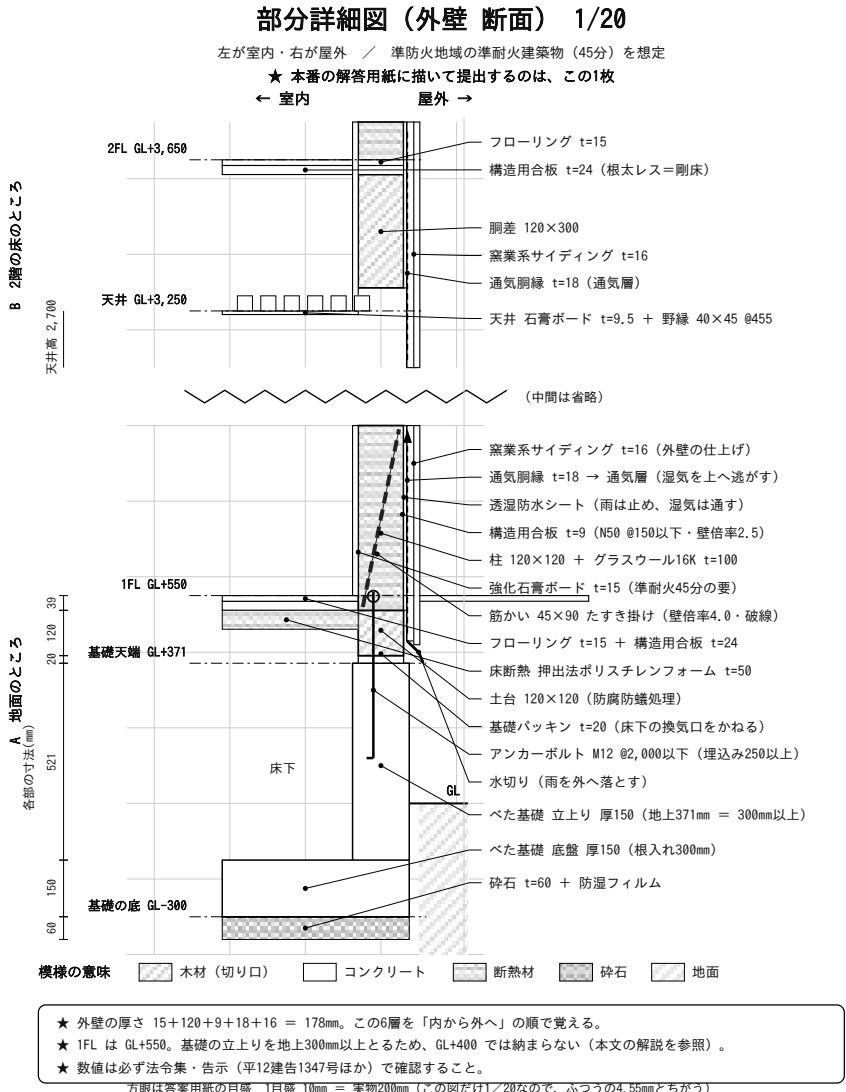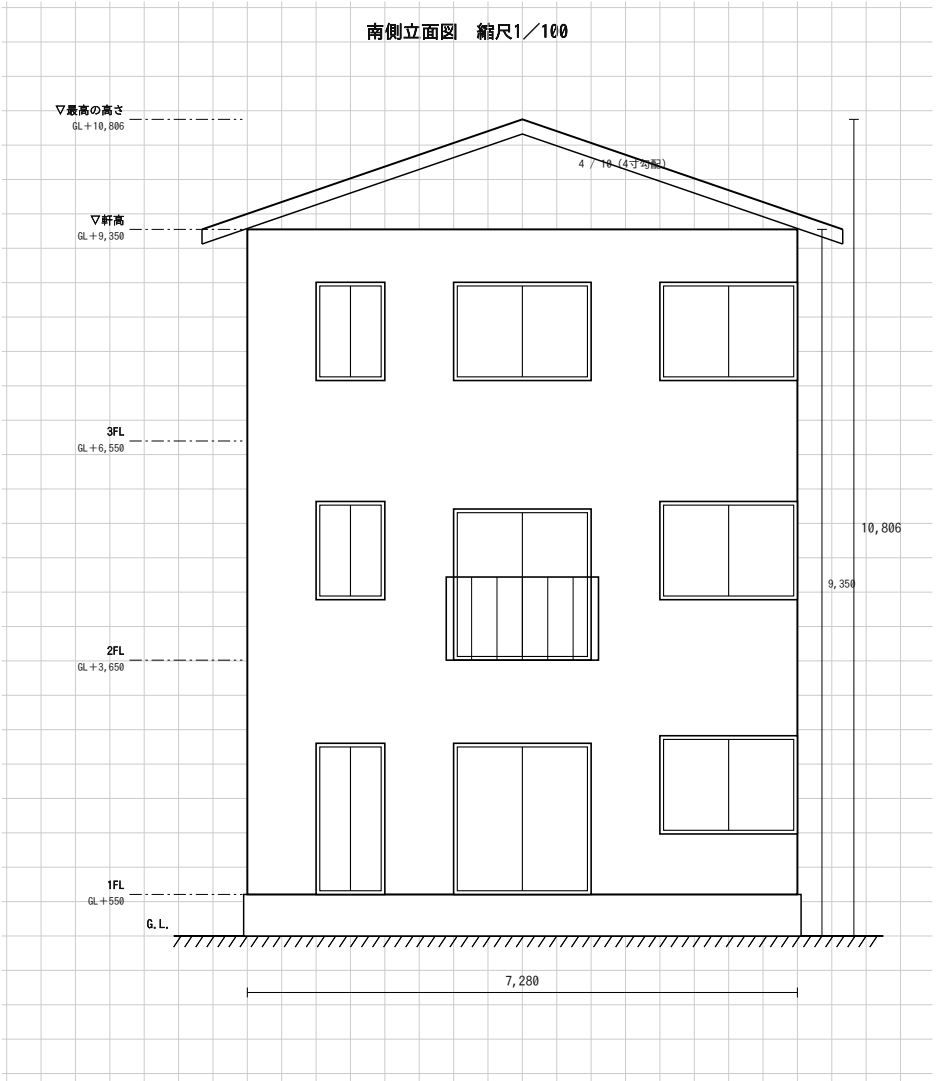

※ この2枚は「型（8マス×10マス）」のもの。問題B（9マス）・C（7マス）は間口が違うので寸法を読みかえる。

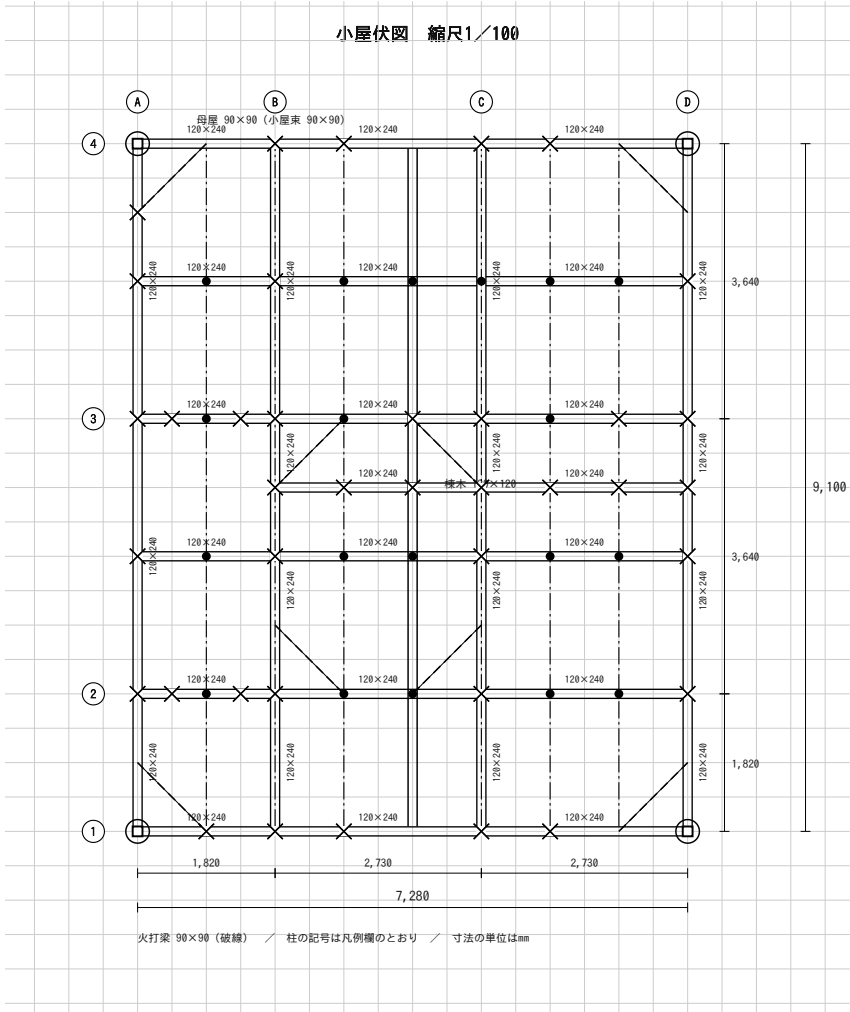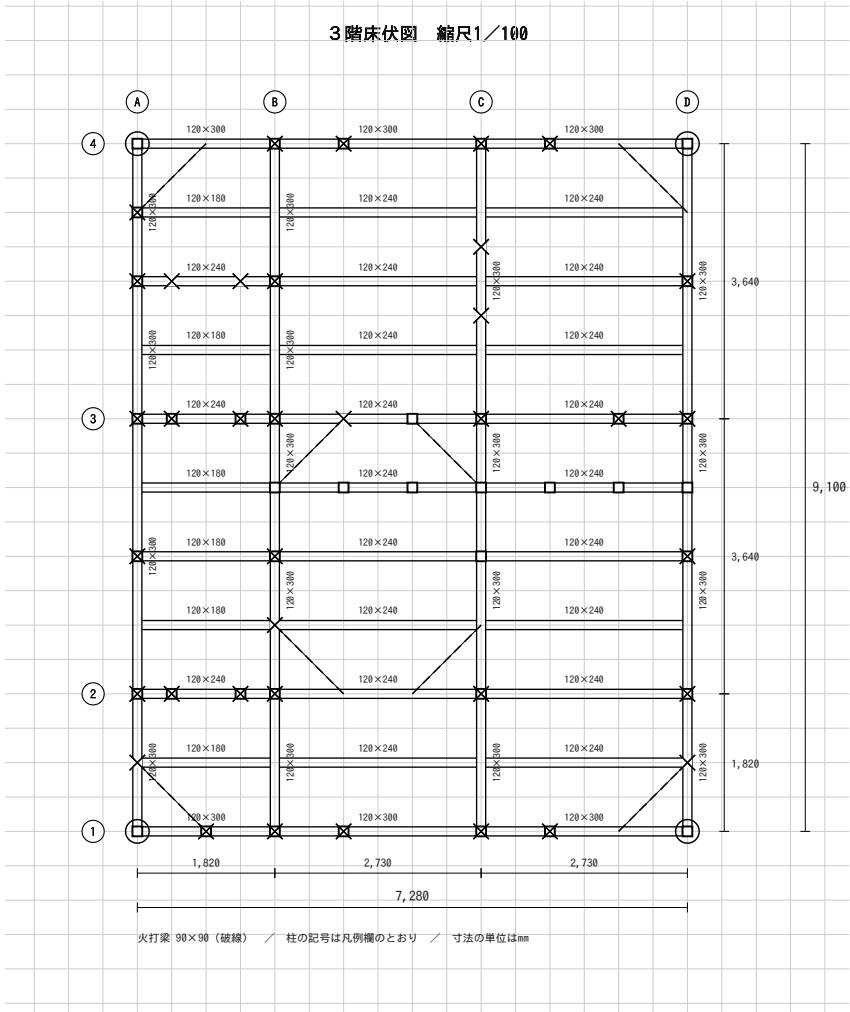

※ 梁は2階・3階の壁の上下と通り芯に必ず通し、残りを床梁φ910で埋める。小屋伏図は棟が南北方向・4寸勾配。3階の壁の上には桁。