
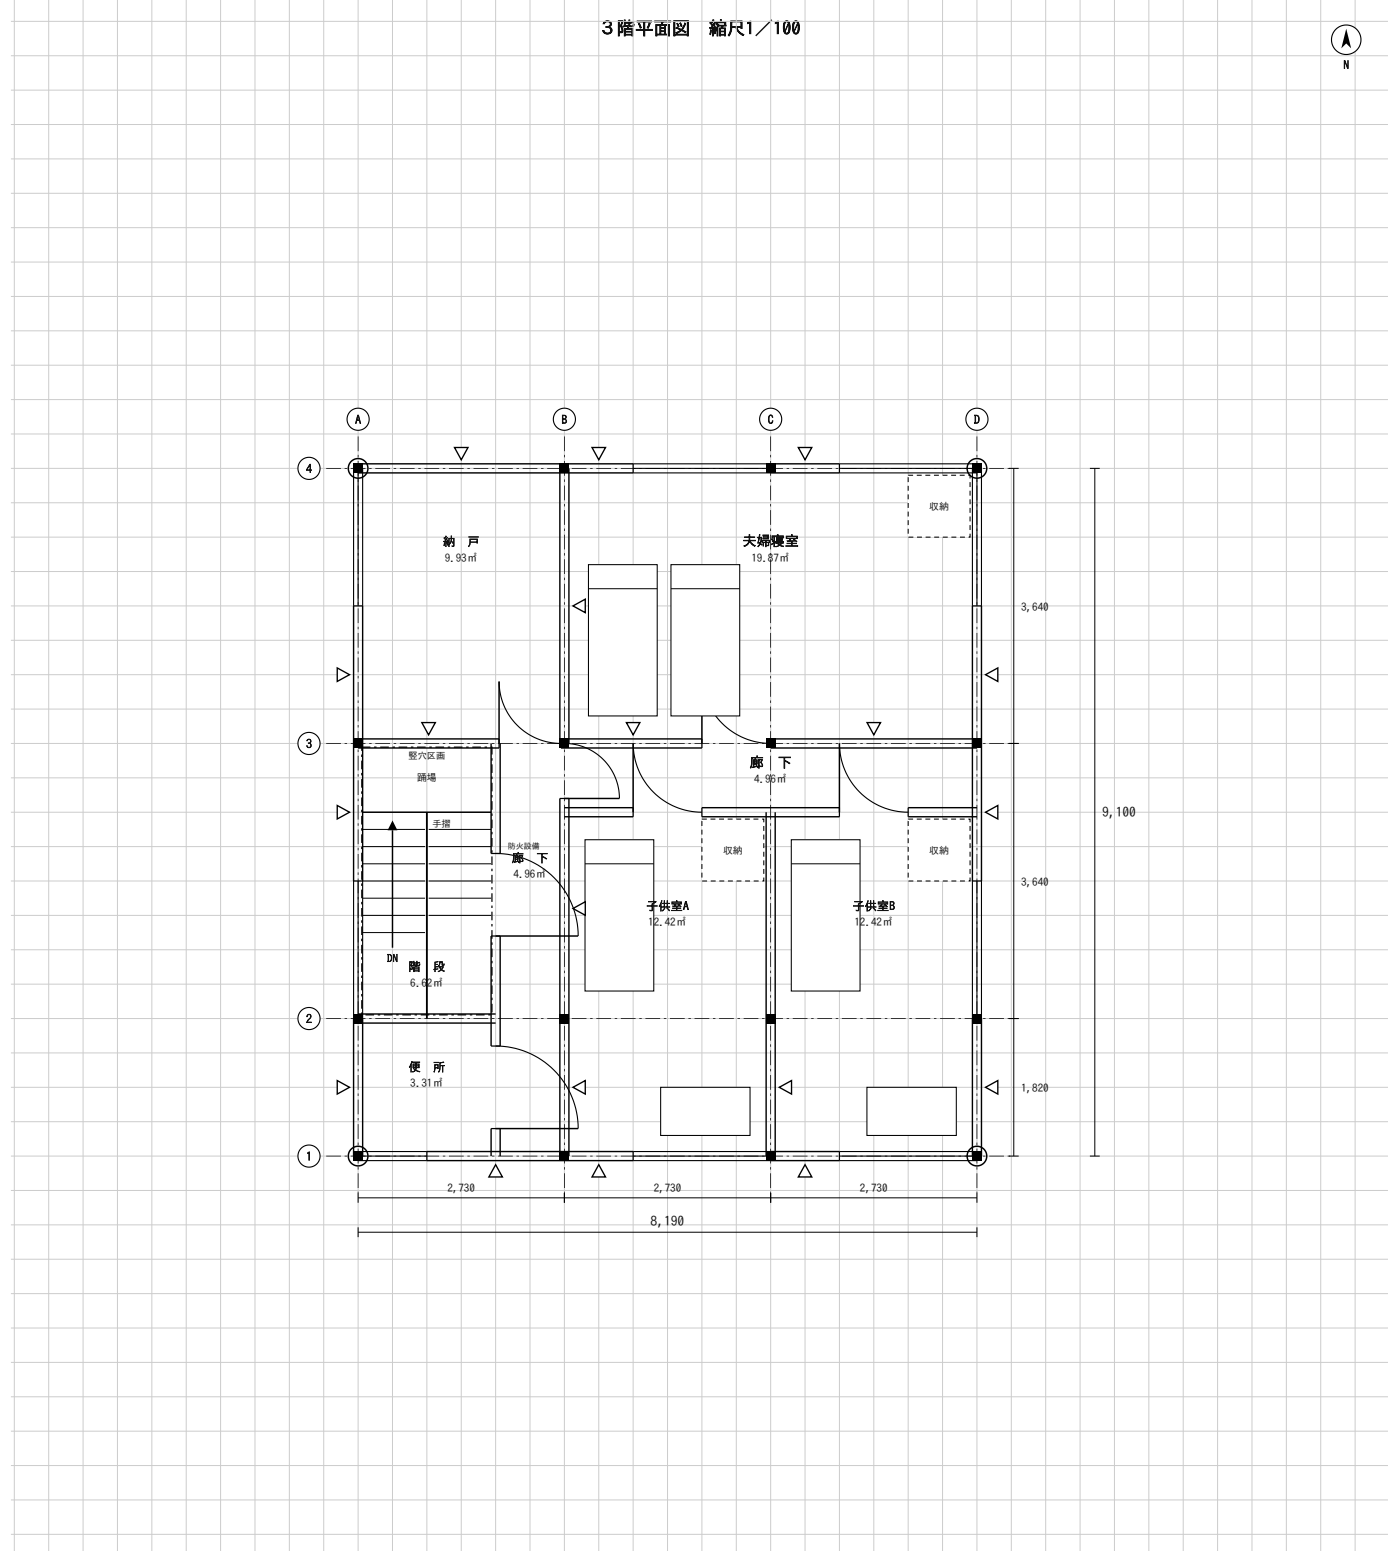
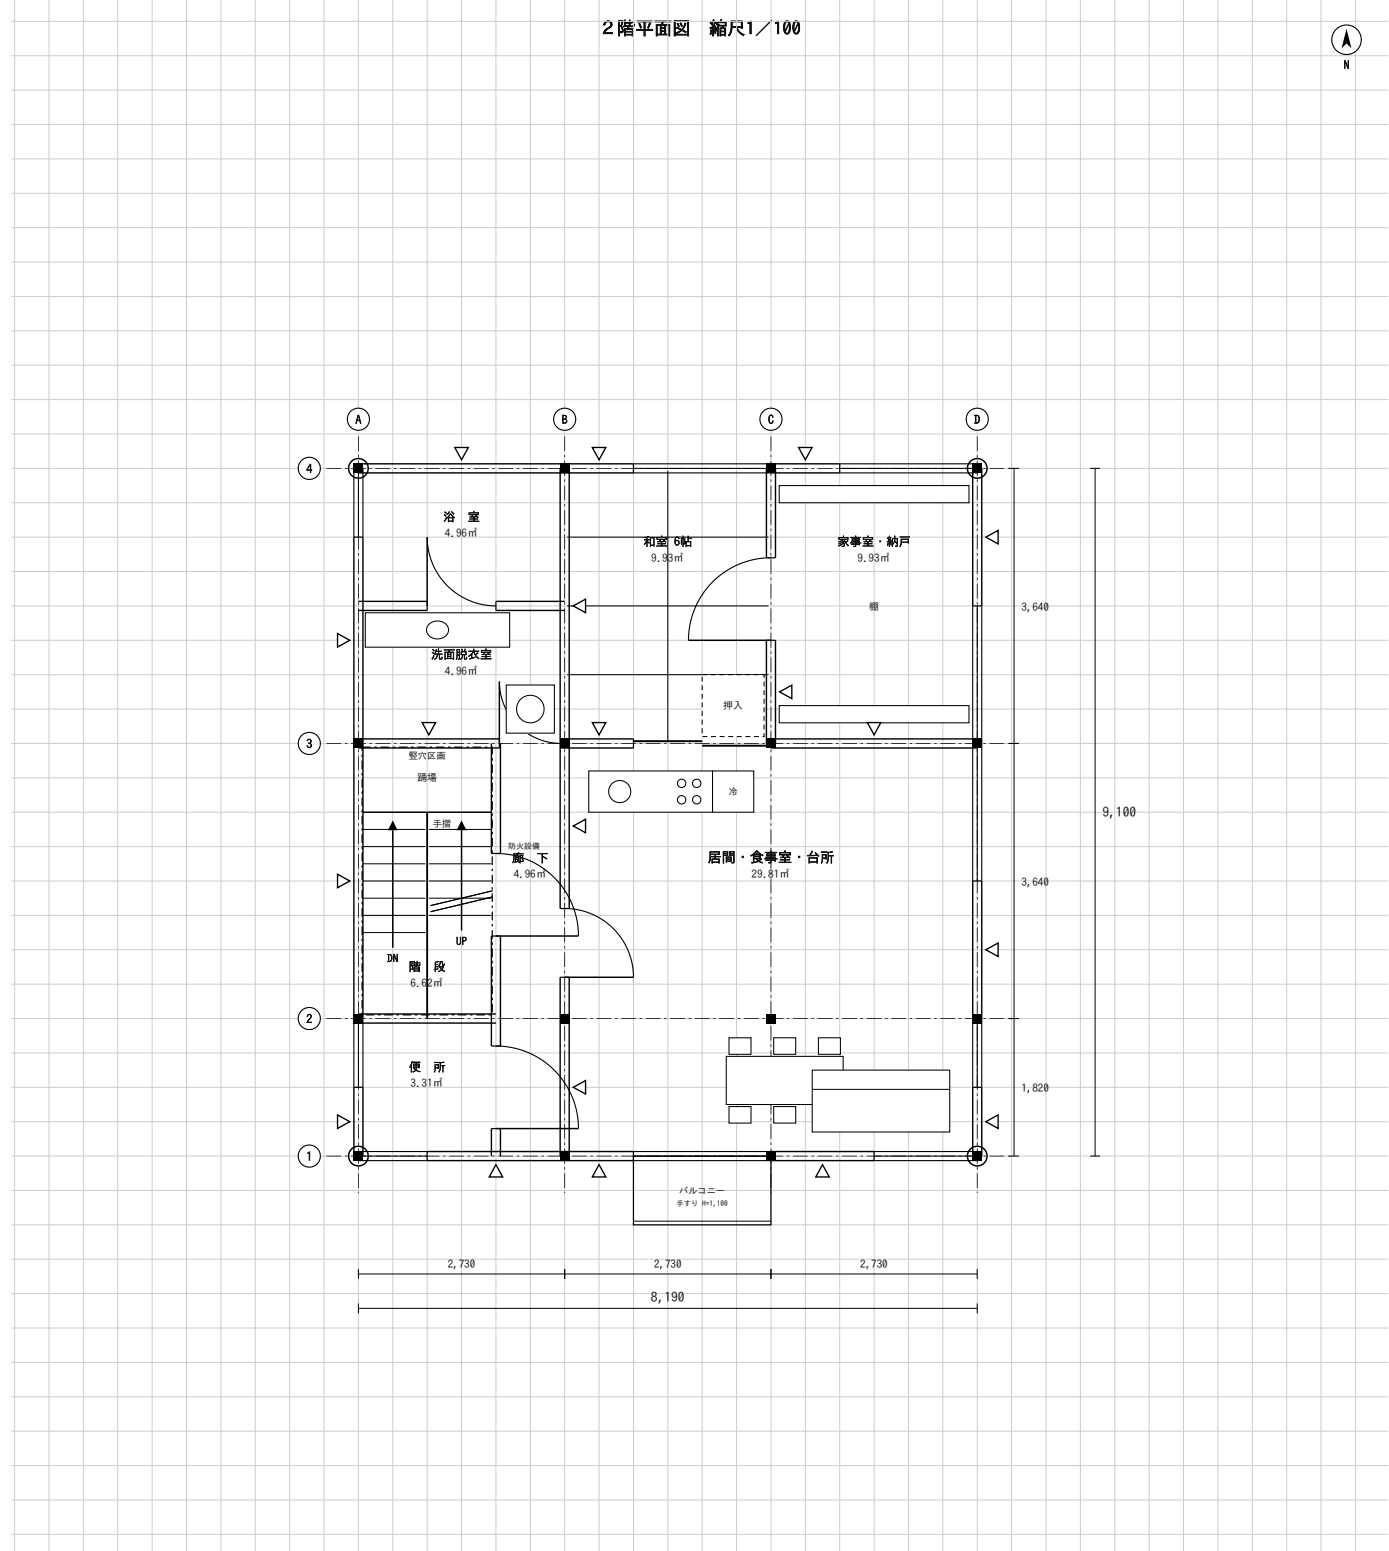


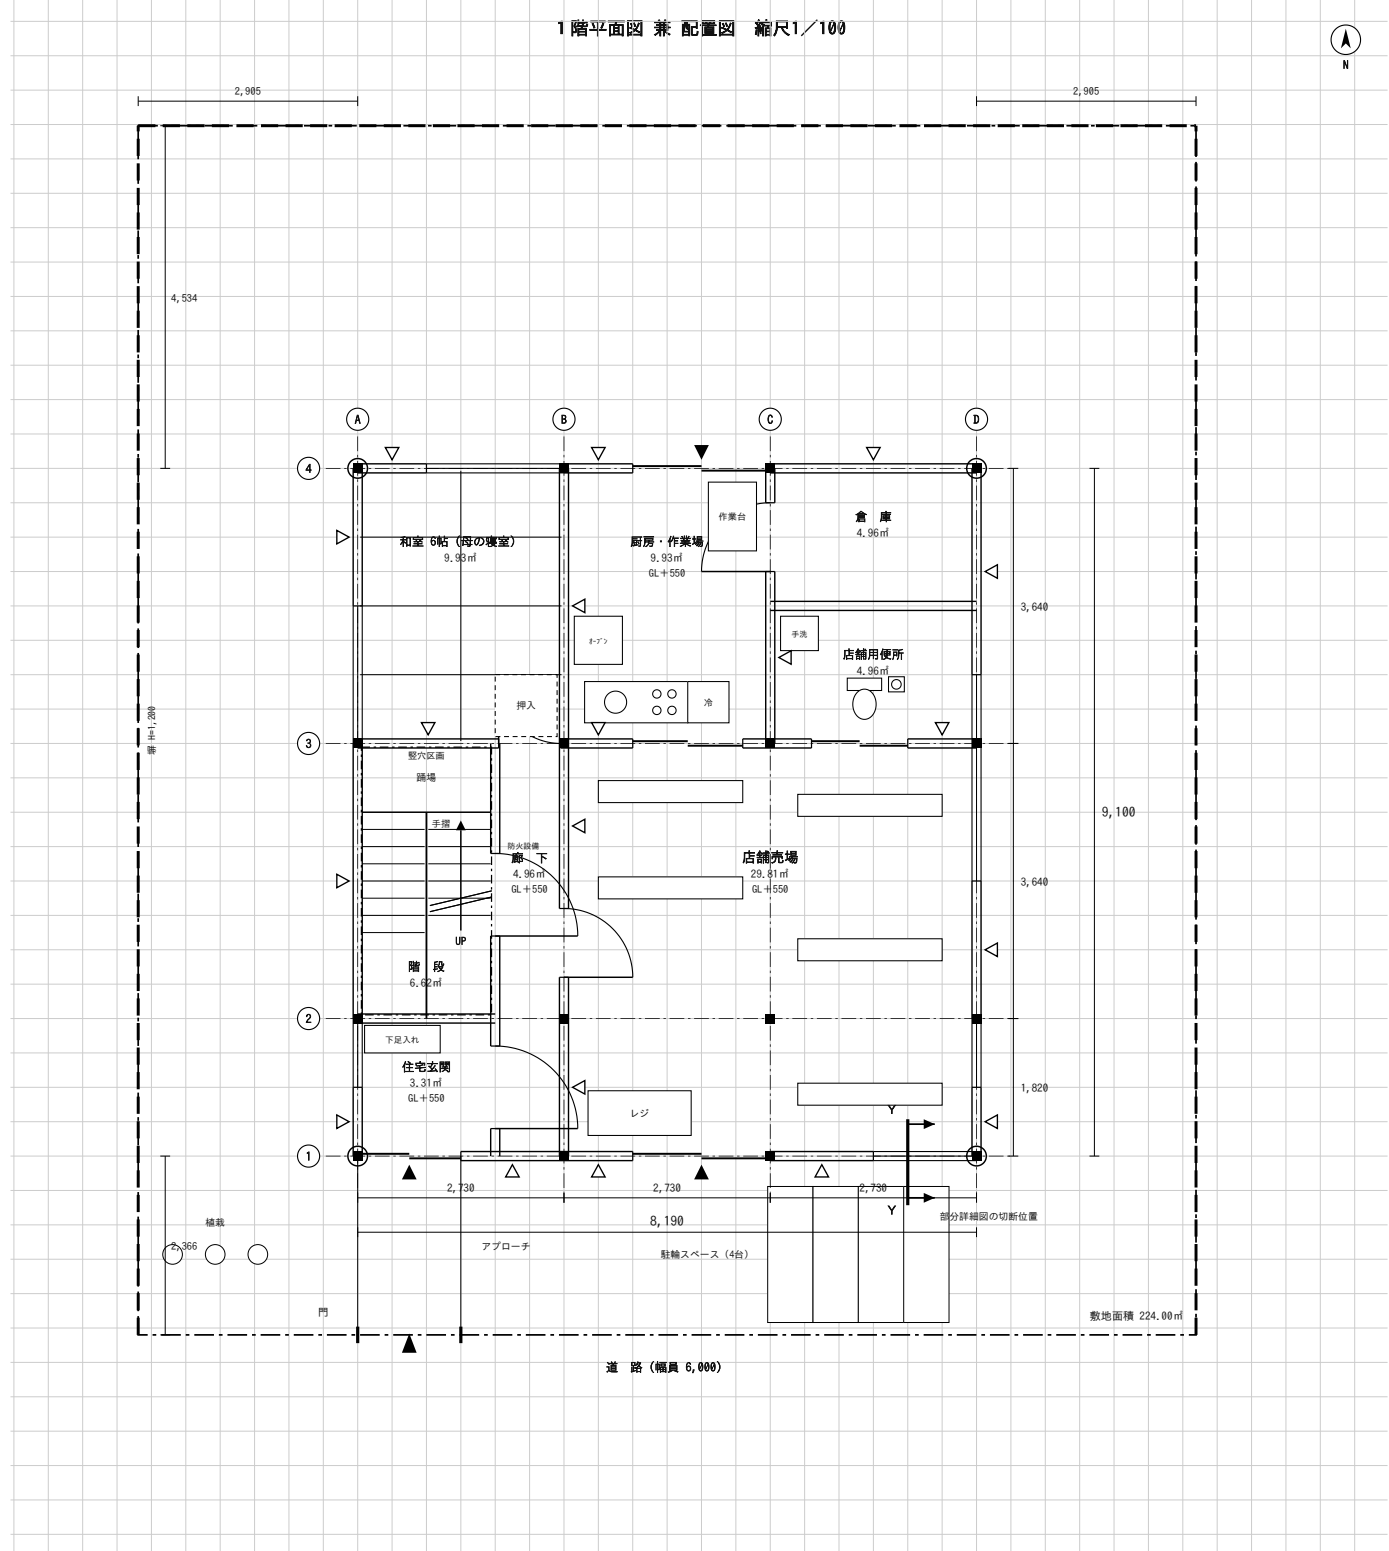

敷地面積		224.00 m ²
建築面積	(計算式) 8.19×9.10	74.52 m ²
床面積 1階 ア	(計算式) 8.19×9.10	74.52 m ²
2階 イ	(計算式) 8.19×9.10	74.52 m ²
3階 ウ	(計算式) 8.19×9.10	74.52 m ²
延べ面積 ア+イ+ウ		223.56 m ²

小数点以下第3位以下は切り捨て。計算式はm単位で書く。

	通し柱	1階の管柱	2階の管柱	重なる管柱	胴差・桁 (正角材)	同上 (平角材)	同上 (丸太材)	火打梁	棟木	母屋・小屋束
記号										
寸法	120×120	120×120	120×120	—	120×120	図中に記入	図中に記入	90×90	120×120	90×90

※ 平角材（120×240 など）の断面寸法は、この欄ではなく 床伏図の中の梁1本ずつのわきに記入する。

標準解答例

予想問題 B



母と暮らす併用住宅（和菓子店）

木造3階建て / 9マス × 10マス (8,190 × 9,100)



※ 立面図・床伏図兼小屋伏図・部分詳細図は、別紙「共通図」をご覧ください。

この解答例のポイント

- ・1階の西側を3マス幅にして廊下を通し、その北に母の和室6帖を置いている。
- ・和室から便所・洗面へ廊下1本で行けるようにして、段差をなくしている。
- ・間口を9マスに広げたぶん、通り芯をA・B・C・Dの4本に組みかえている。

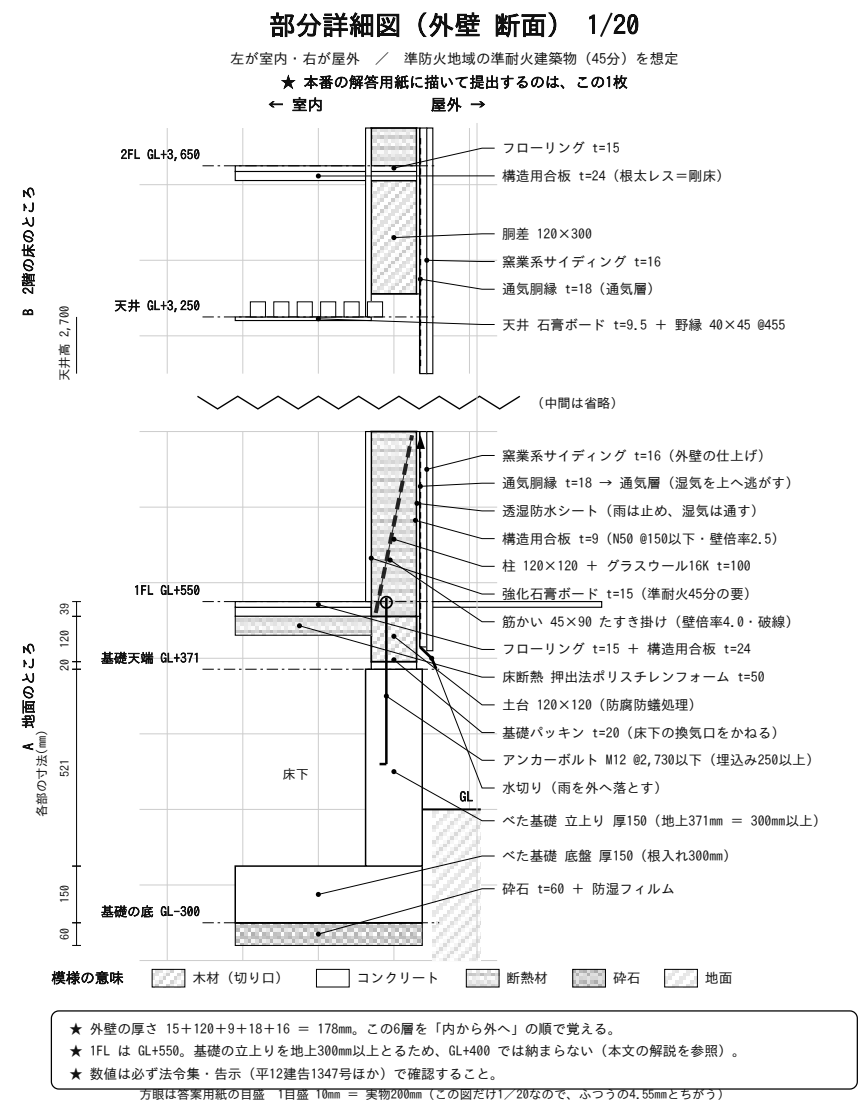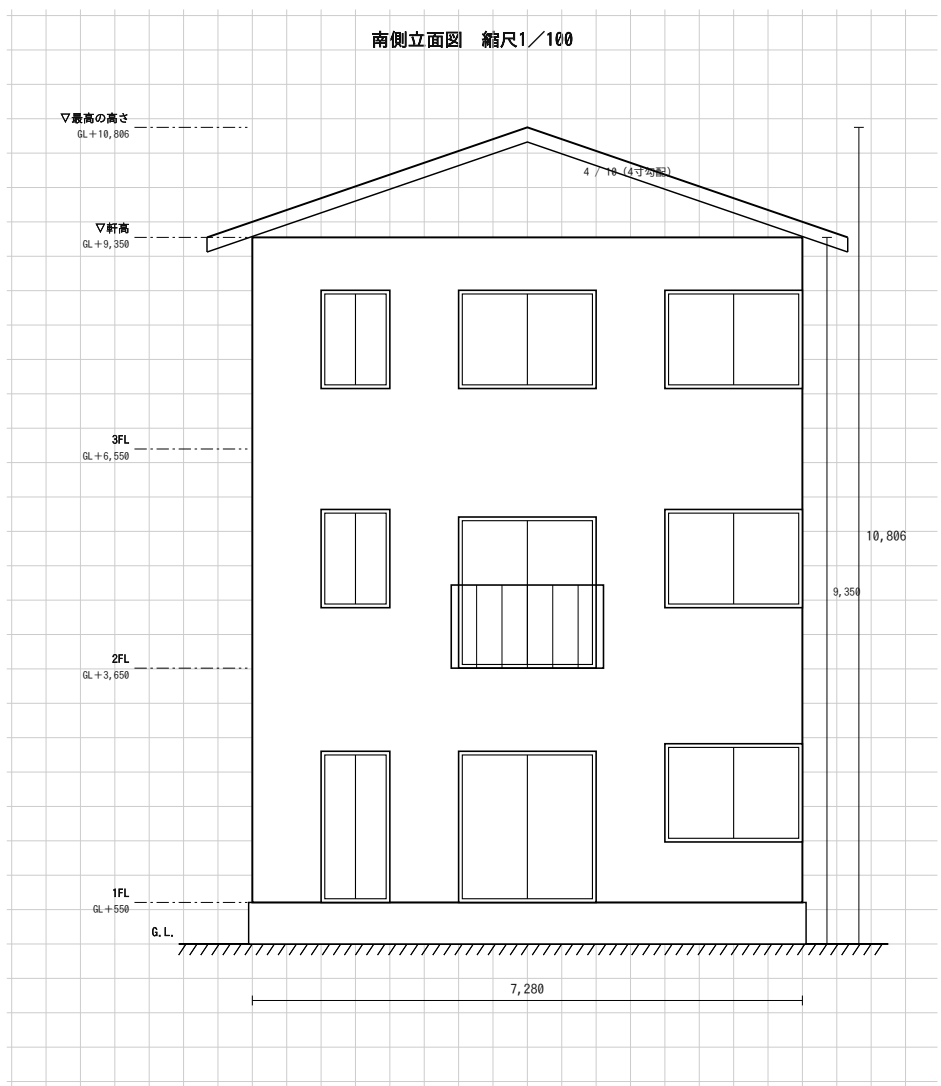

※ この2枚は「型（8マス×10マス）」のもの。問題B（9マス）・C（7マス）は間口が違うので寸法を読みかえる。

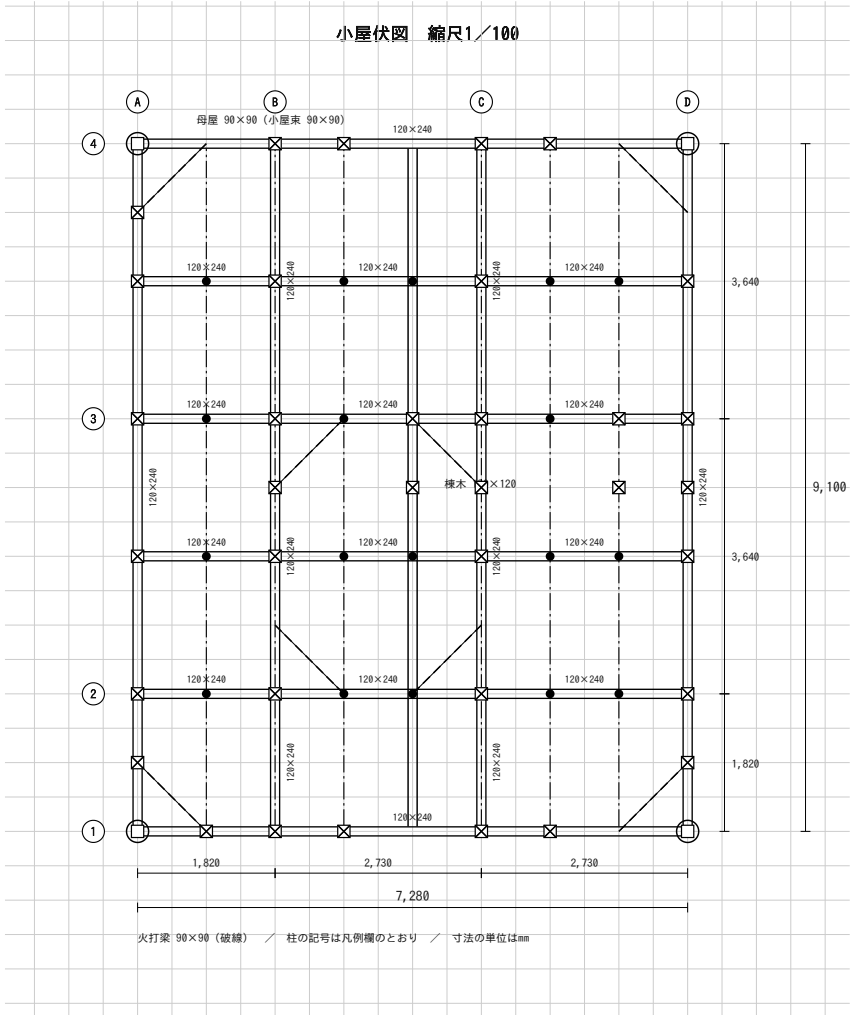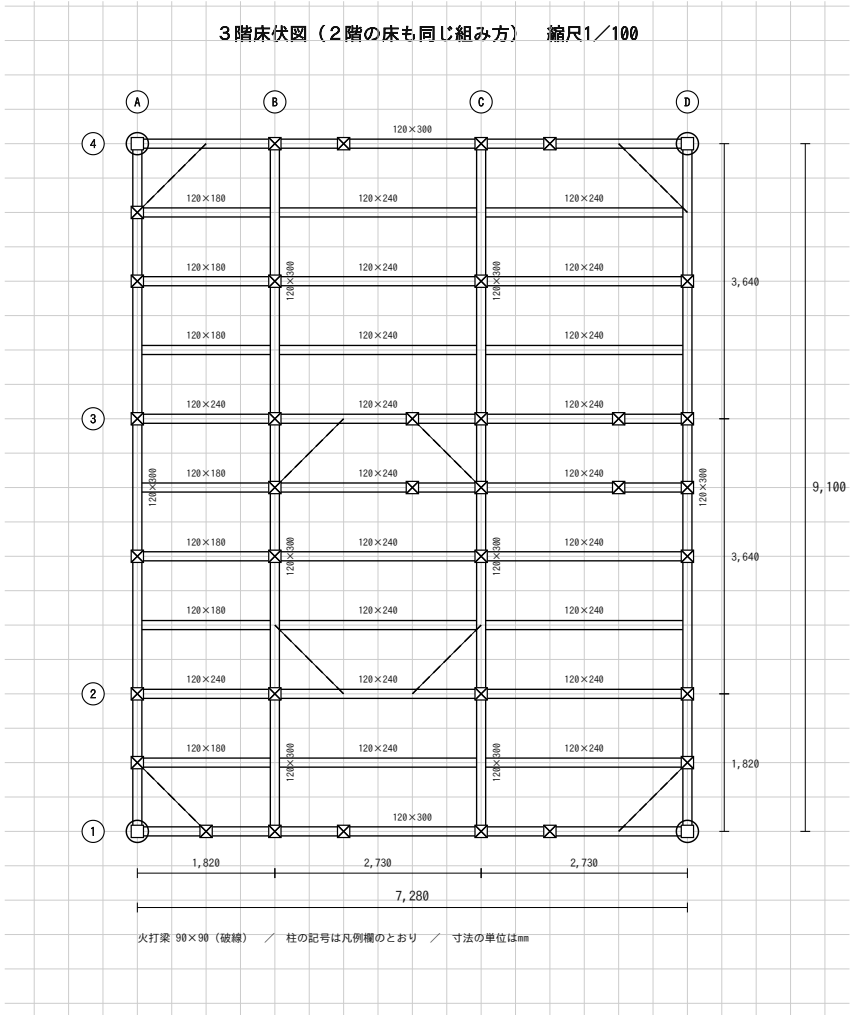

※ 2階の床伏図と3階の床伏図は同じ組み方でよい。小屋伏図は棟が南北方向・4寸勾配。