



(1) 1階平面図 兼 配置図 縮尺1/100

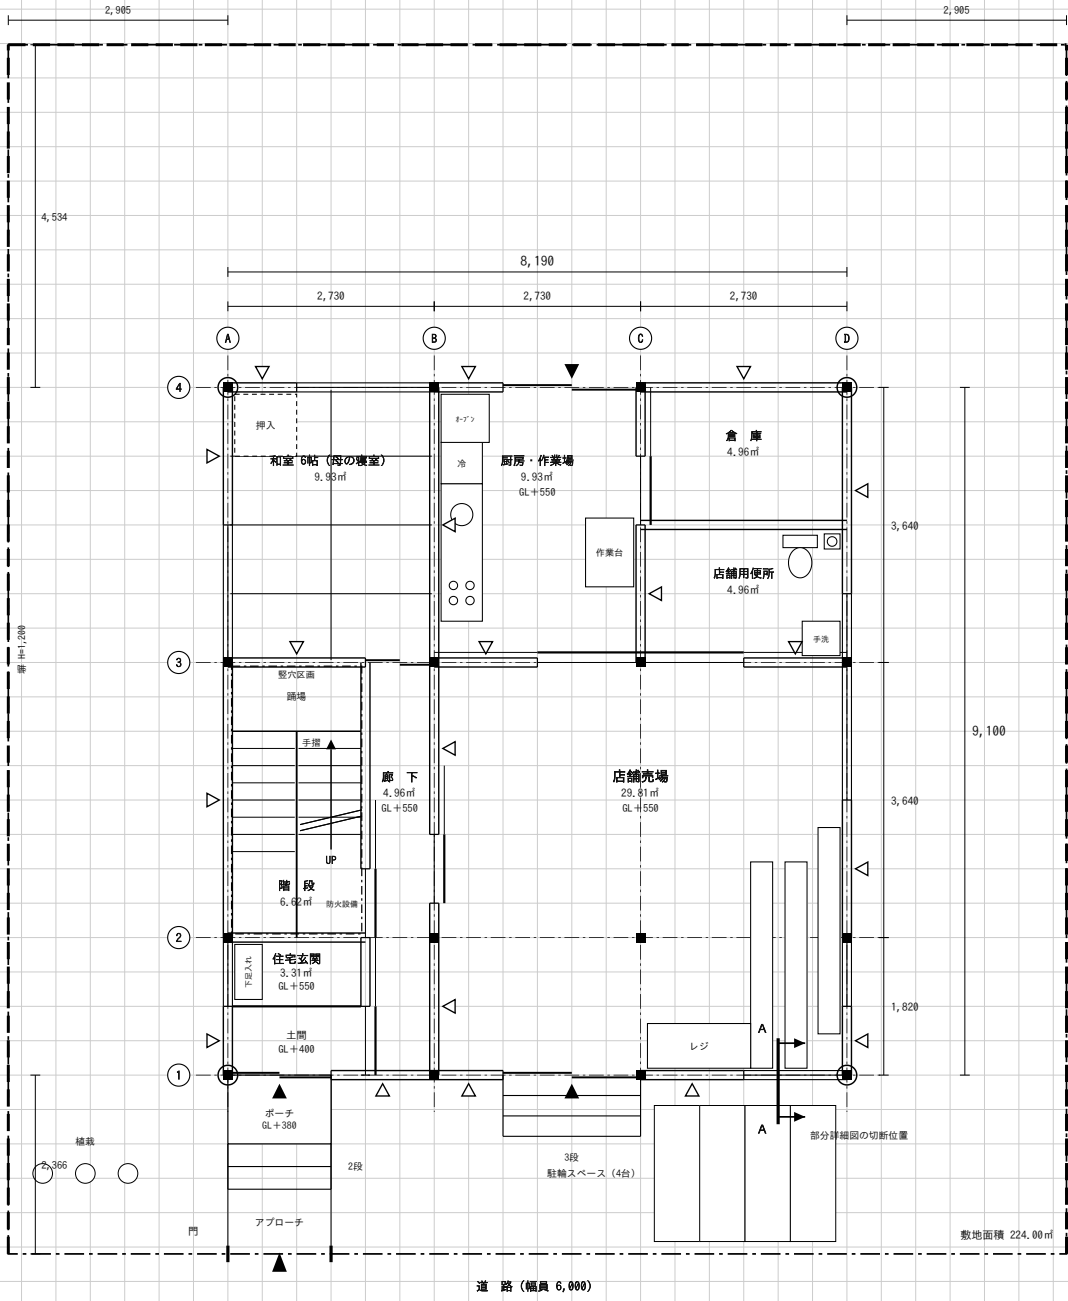


(2) 2階平面図 縮尺1/100

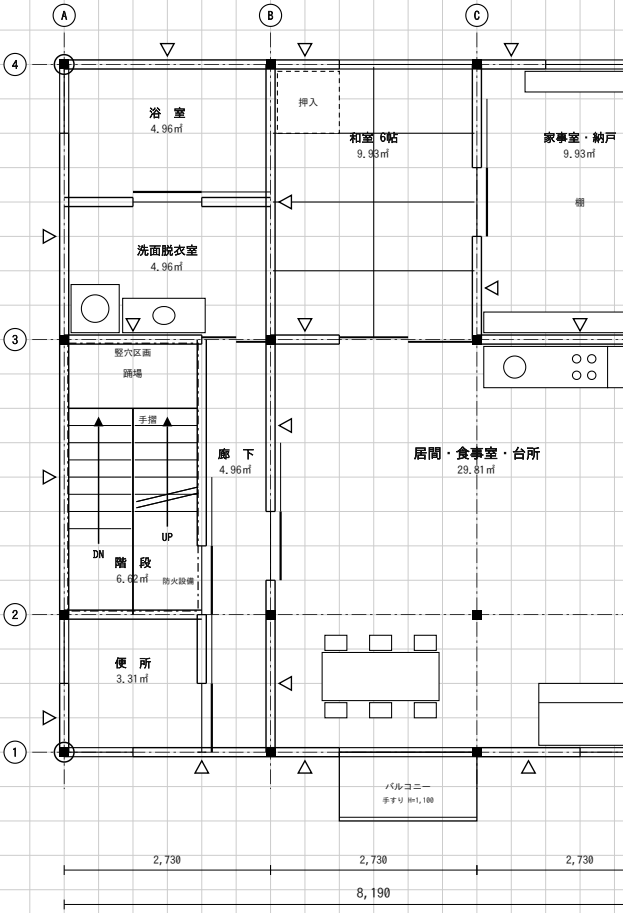


(4) 3階床伏図 (1/100)

予想問題 B 解答例 3階床伏図 縮尺1/100

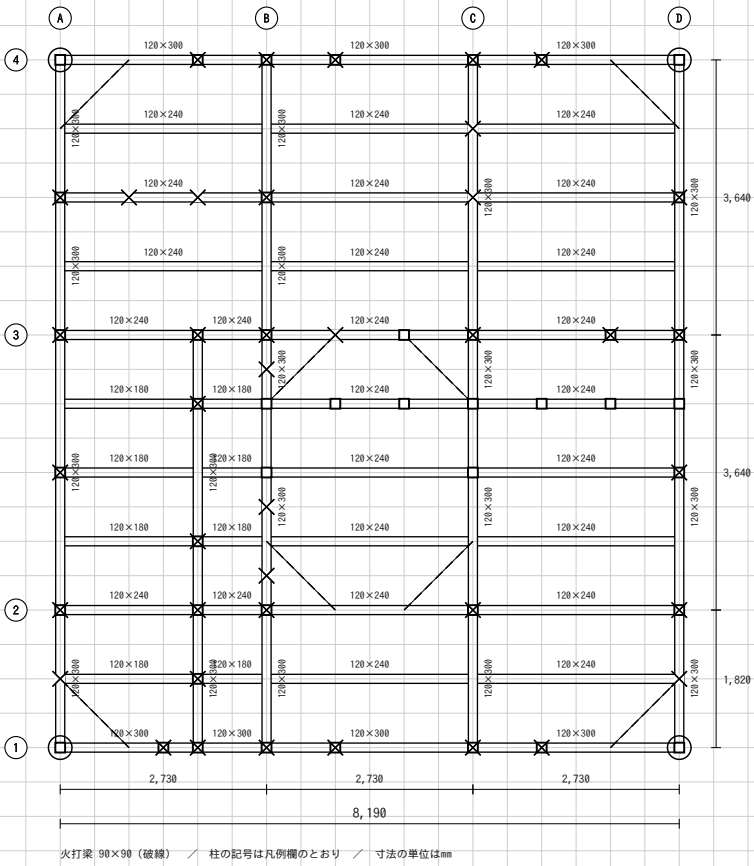


(4) 小屋伏図 (1/100)

予想問題 B 解答例 小屋伏図 縮尺1/100

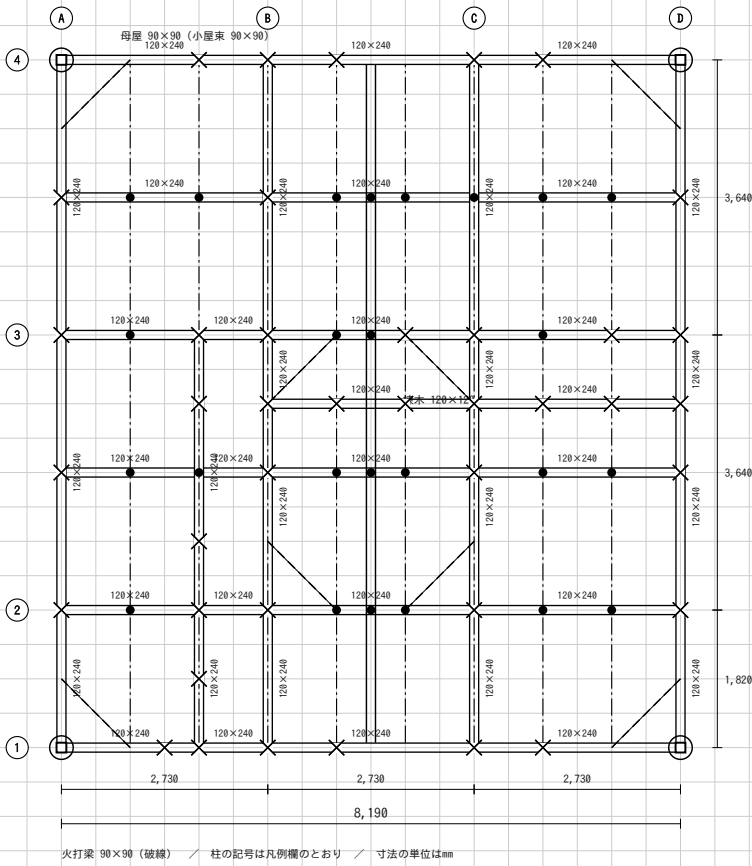

(5) 南側立面図 (1/100)



予想問題

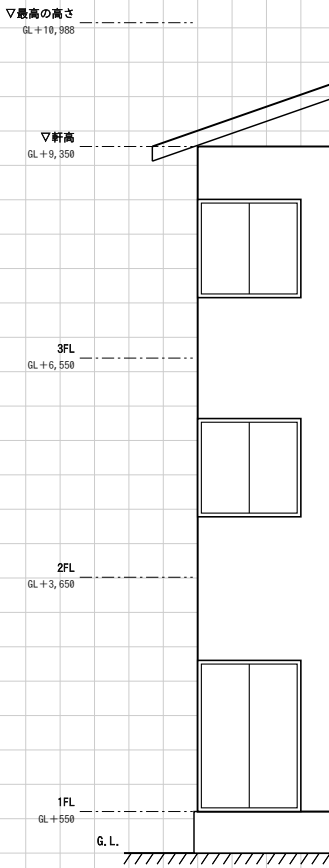

凡 例 (床伏図兼小屋伏図の表示記号)

	通し柱	1階の管柱	2階の管柱	重なる管柱	胴差・桁 (正角材)	同上 (平角材)	同上 (丸太材)	
記号								
寸法	120×120	120×120	120×120	—	120×120	図中に記入	図中に記入	



※ 平角材 (120×240 など) の断面寸法は、この欄ではなく 床伏図の中の梁1本ずつのわきに記入する。

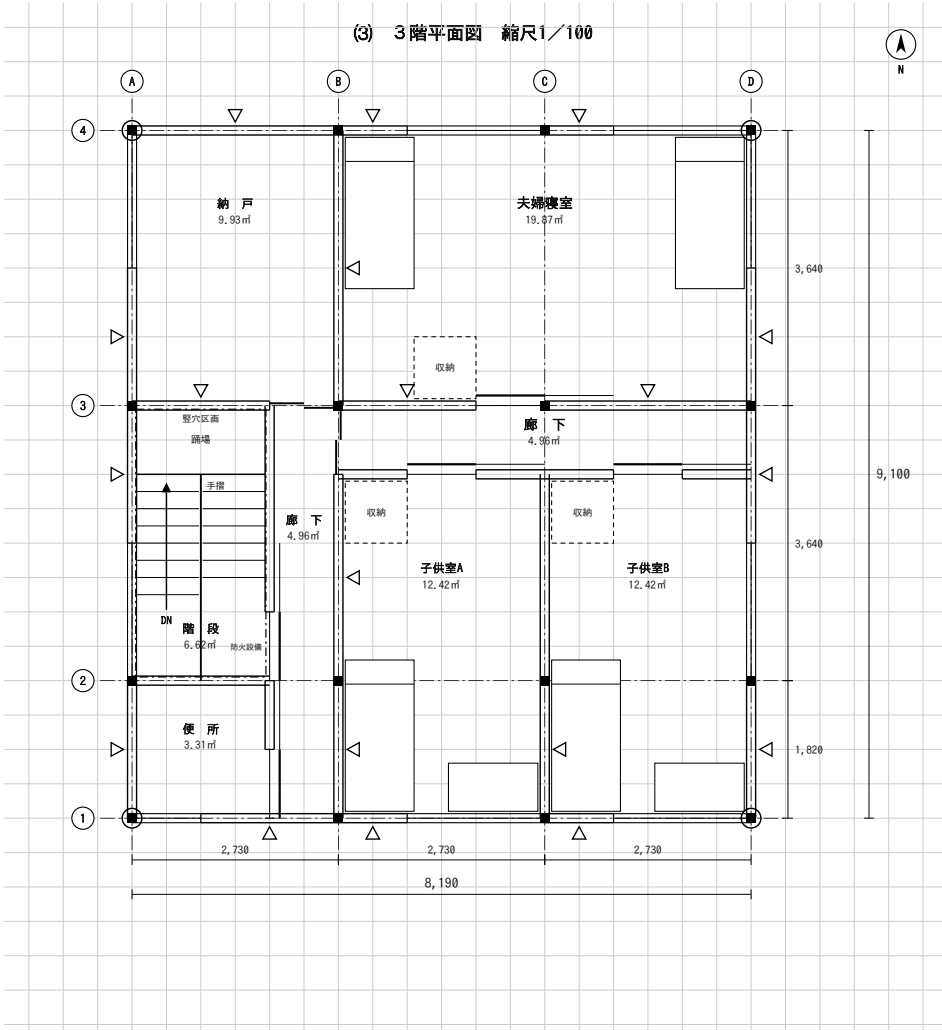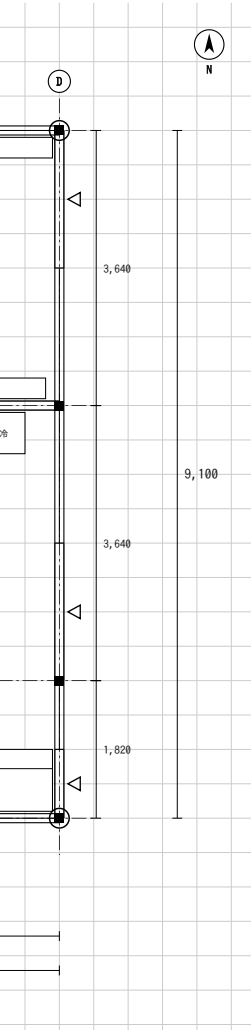

(7) 面 積 表

敷地面積	224.00	㎡
建築面積 (計算式) 8.19×9.10	74.52	㎡
床面積 1階 ア (計算式) 8.19×9.10	74.52	㎡
2階 イ (計算式) 8.19×9.10	74.52	㎡
3階 ウ (計算式) 8.19×9.10	74.52	㎡
延べ面積 ア+イ+ウ	223.56	㎡

※ 小数点以下第3位以下は切り捨て。計算式は㎡単位で書く。

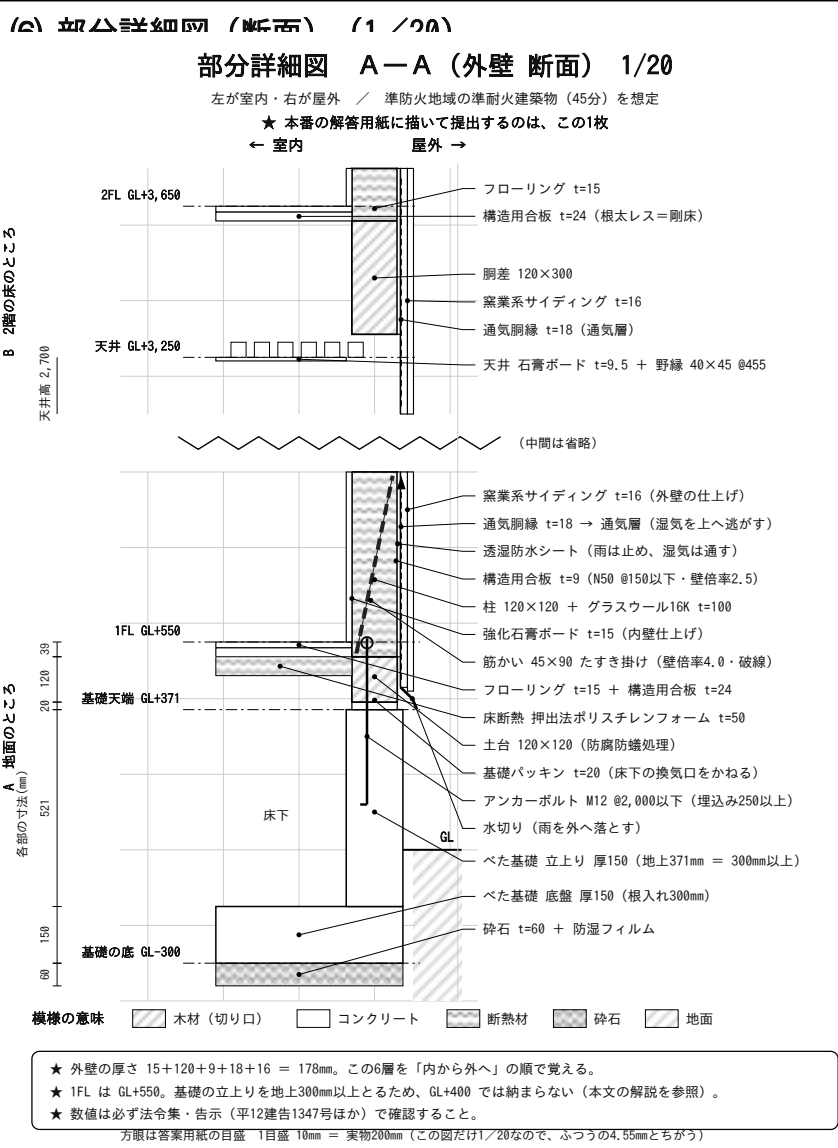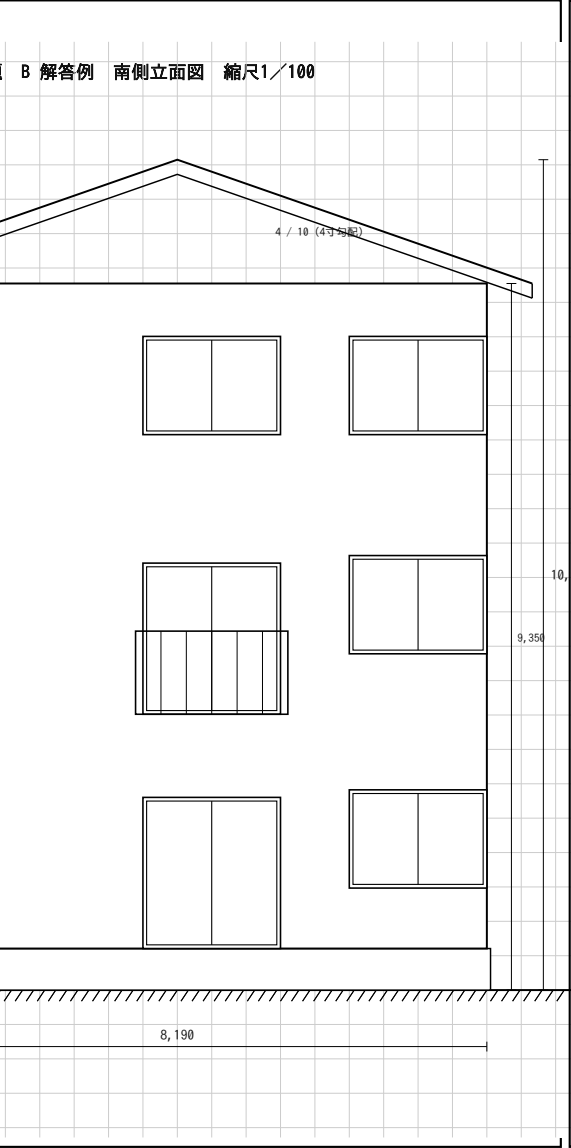

(8) 計画の要点等

① 高齢者の居室を1階に設けたことについて工夫した点
母の寝室である和室6畳を1階の北西に配置し、階段を使わずに生活できるようにした。住宅玄関から寝室までは幅910mm（有効約780mm）の廊下1本でつながり、途中で段差を設けていない。寝室のすぐ南に階段室があるため、2階・3階の家族がすぐに様子を見に行ける。廊下及び出入口の有効幅は780mm以上とし、将来手すりを取り付けられるよう壁に下地を入れている。
② 店舗部分と住宅部分の動線計画について工夫した点
店舗の出入口は道路に面して設け、来店客は店舗売場から店舗用便所へ至る動線とした。店舗用便所は売場の一部を区画して設け、厨房を通らずに利用できるようにしている。住宅の玄関は店舗の出入口と壁をへだてて別に設け、幅910mm（有効約780mm）の廊下ですぐ階段へ上がれる配置とした。これにより住まい手が売場を通らずに2階・3階へ行くことができ、営業時間中も両者の動線が交錯しない。商品及び材料の搬入は建築物背面の勝手口から厨房・倉庫へ直接行える。
③ 高齢者の避難について配慮した点
母の寝室を1階に置いたことで、火災時に階段を使わずに屋外へ避難できる。寝室は西面及び北面の2方向に窓を持ち、逃げ道が1方向にかたよらないようにした。廊下から玄関までの避難経路は幅910mm（有効約780mm）の直線で、途中で段差や狭くなる部分がない。階段室は準耐火構造の床及び壁で囲んだ縦穴区画としているため、上階からの煙が1階の廊下へ流れ込みにくく、高齢者でも落ち着いて屋外へ出られる。なお延べ面積が200㎡を超えるため、縦穴区画の緩和（令112条11項ただし書）は用いていない。

火打梁	棟木	母屋・小屋束
90×90	120×120	90×90

標準解答例

予想問題 B 母と暮らす併用住宅（和菓子店）
木造3階建て / 9マス × 10マス (8,190 × 9,100)

- ・1階の西側を3マス幅にして廊下を通し、その北に母の和室6帖を置いている。
- ・和室から便所・洗面へ廊下1本で行けるようにして、段差をなくしている。
- ・間口を9マスに広げたぶん、通り芯をA・B・C・Dの4本に組みかえている。