




(1) 1階平面図 兼 配置図 縮尺1/100

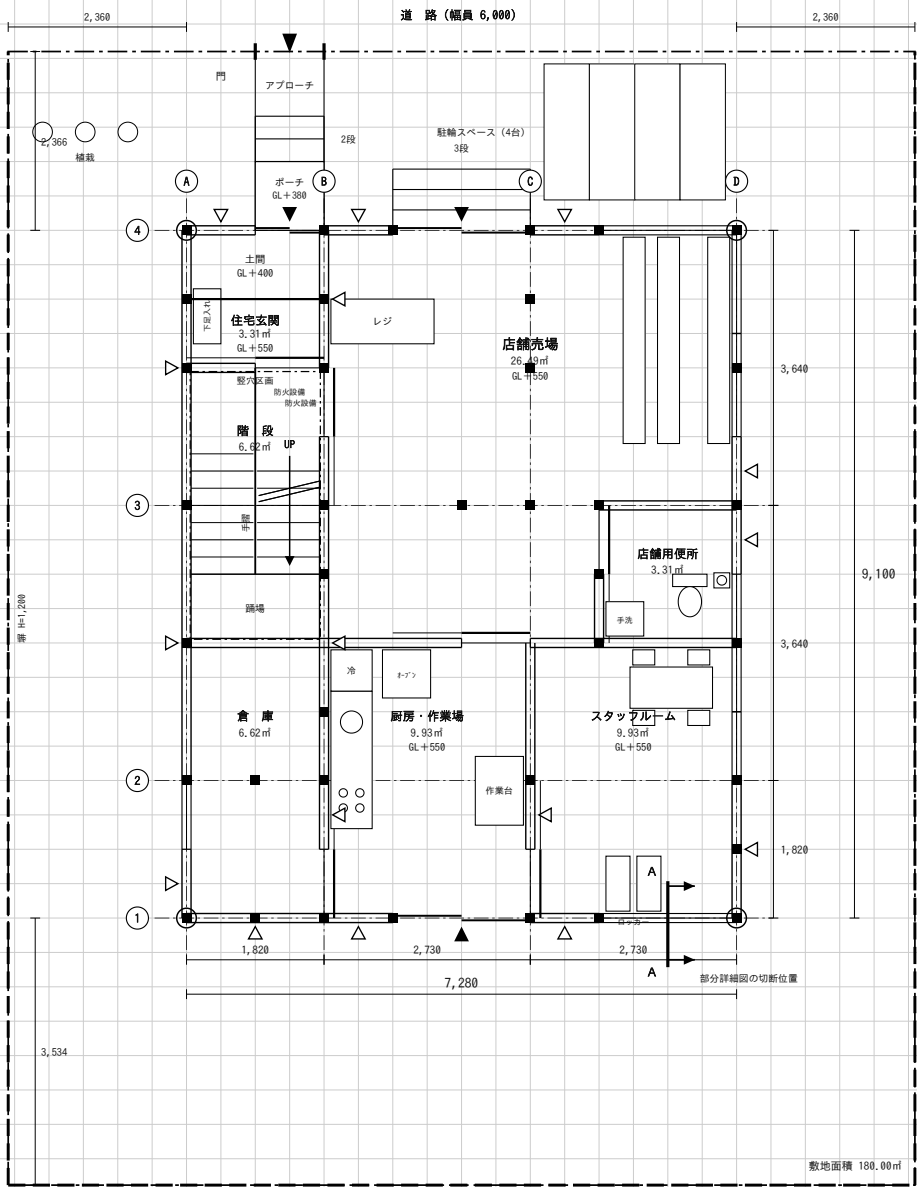

(2) 2階平面図 縮尺1/100

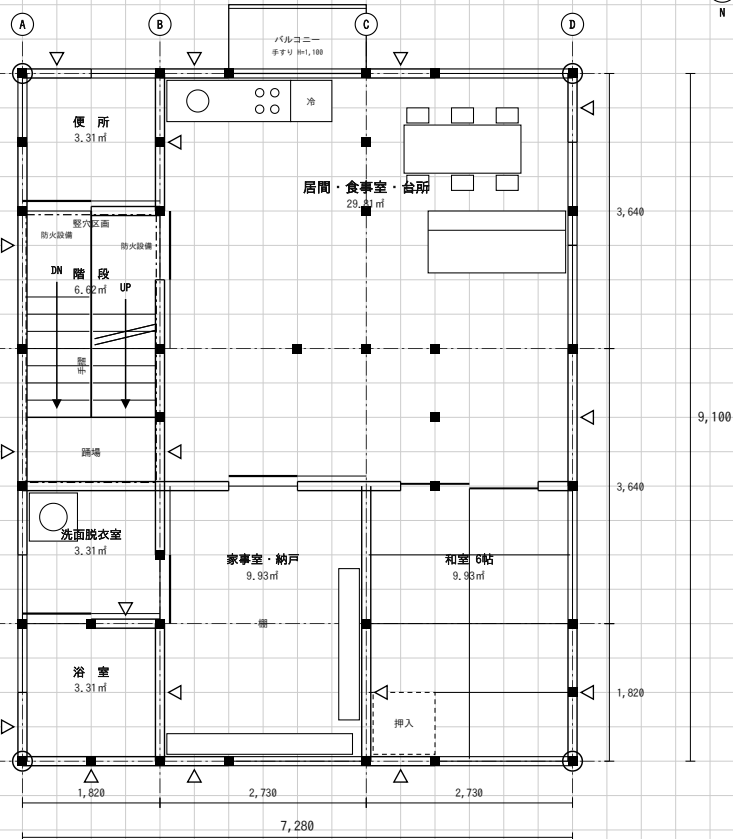

(3) 3階平面図 縮尺1/100

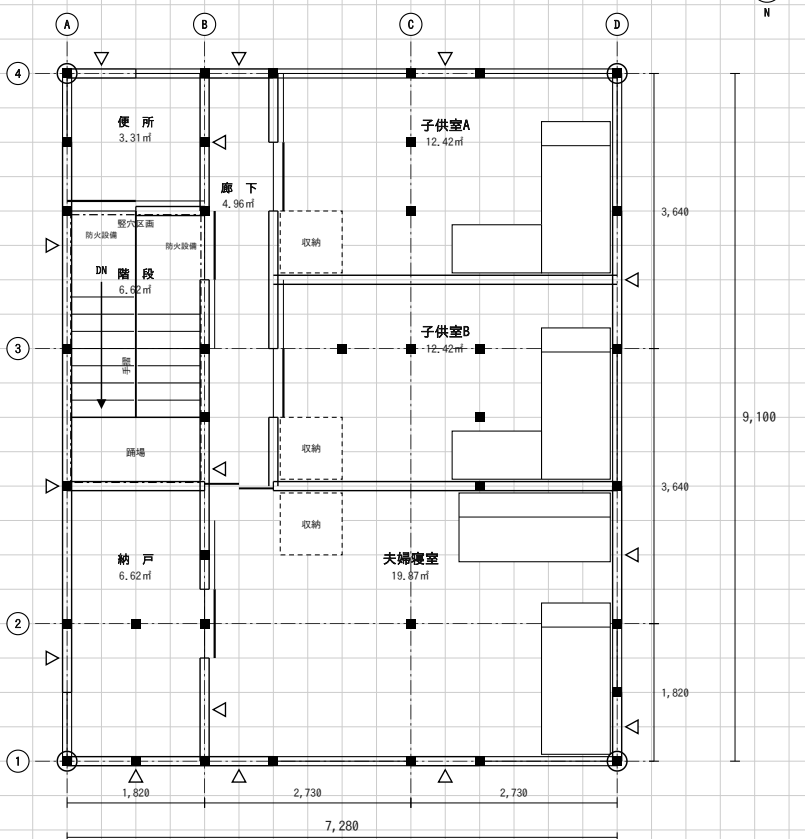


(7) 面積表


|                |        |   |
|----------------|--------|---|
| 敷地面積           | 180.00 | ㎡ |
| 建築面積           | 66.24  | ㎡ |
| （計算式）7.28×9.10 |        |   |
| 床面積 1階 ア       | 66.24  | ㎡ |
| （計算式）7.28×9.10 |        |   |
| 2階 イ           | 66.24  | ㎡ |
| （計算式）7.28×9.10 |        |   |
| 3階 ウ           | 66.24  | ㎡ |
| （計算式）7.28×9.10 |        |   |
| 延べ面積 ア+イ+ウ     | 198.72 | ㎡ |

※ 小数点以下第3位以下は切り捨て。計算式は㎡単位で書く。


(4) 3階床伏図 (1/100)

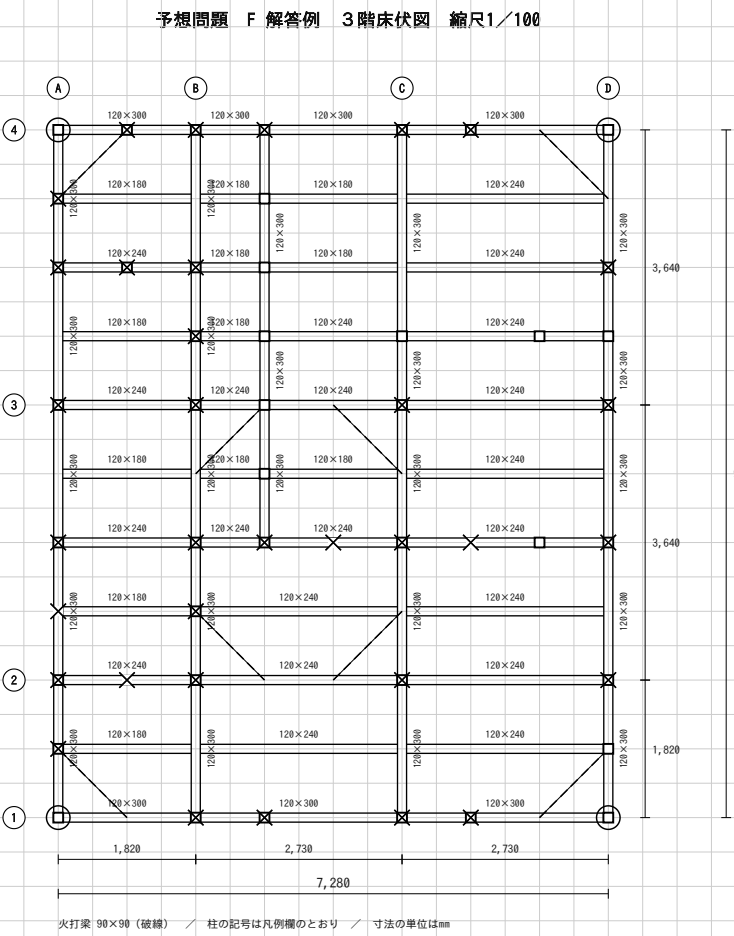


(4) 小屋伏図 (1/100)

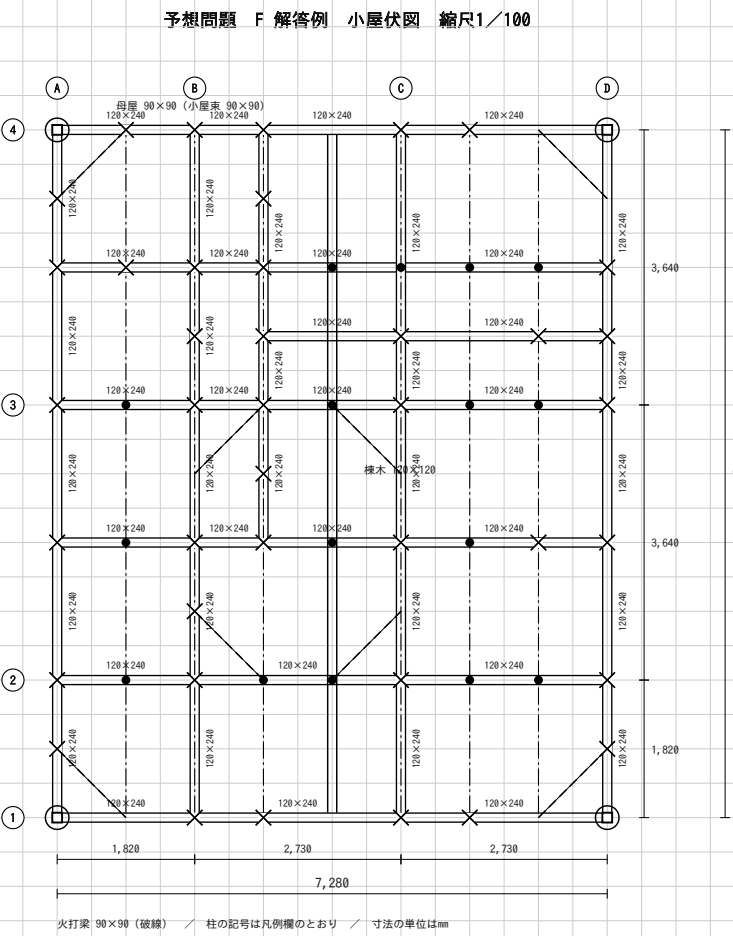

(5) 南側立面図 (1/100)

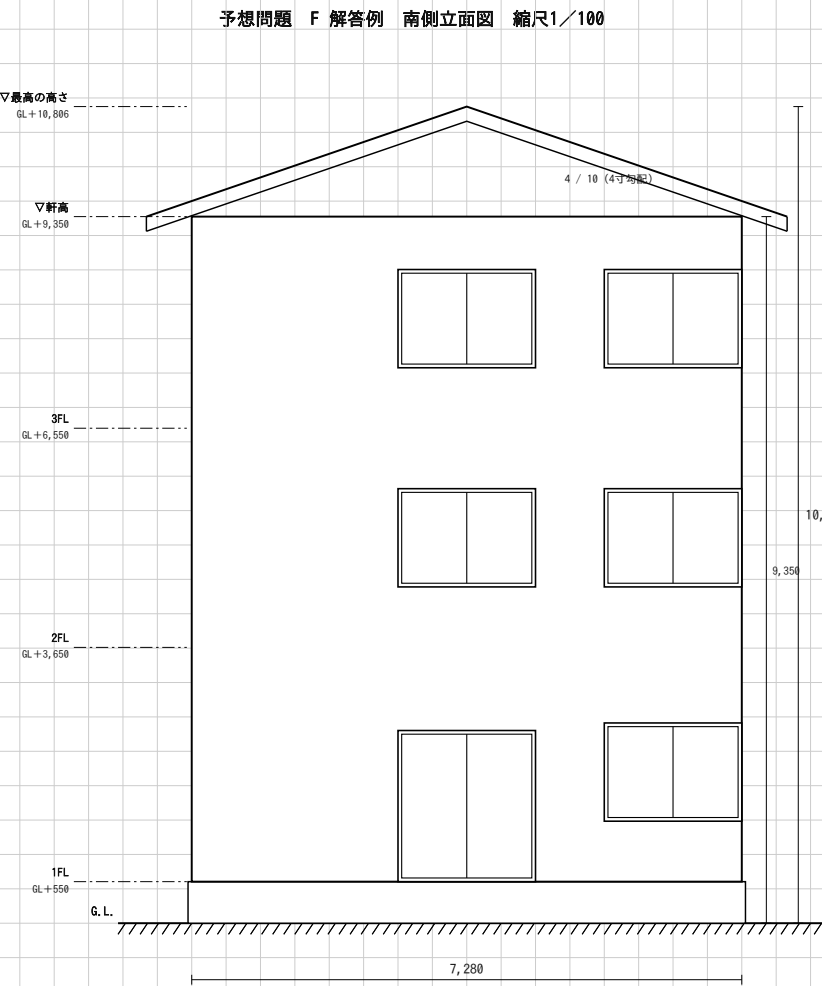

(6) 部分詳細図 (断面) (1/20)

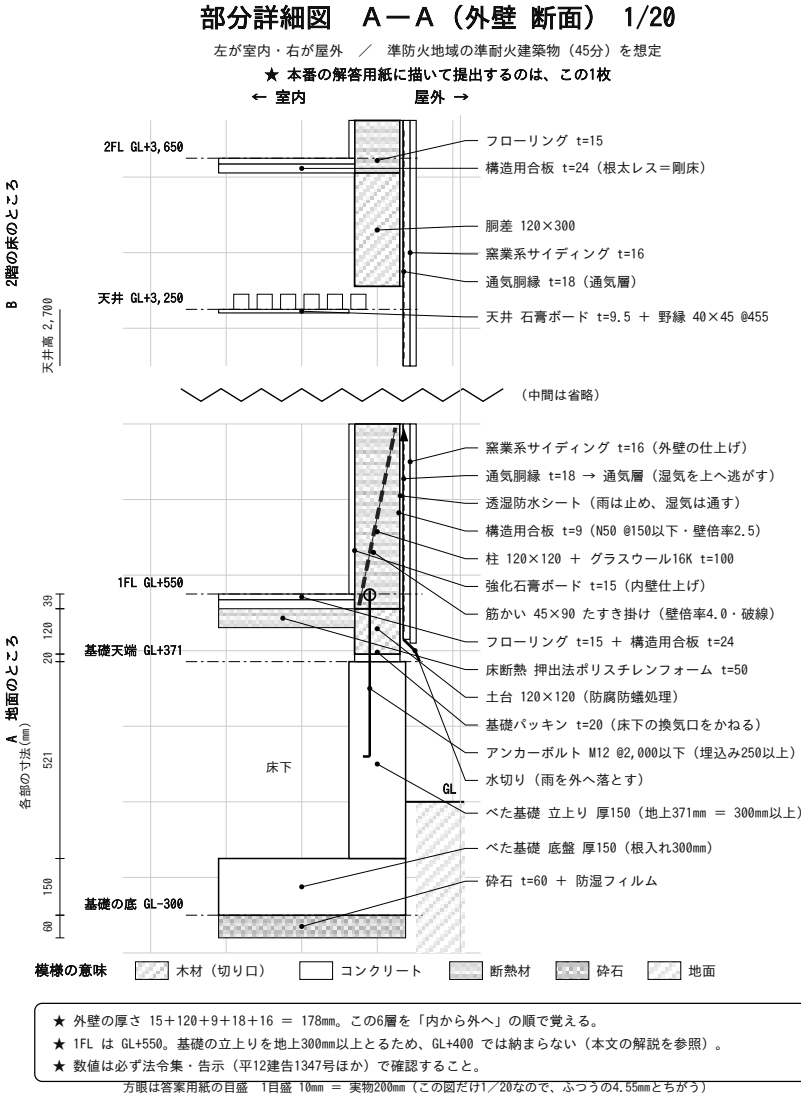

(8) 計画の要点等

① 北側道路に対して、住宅部分の日照をどのように確保したか

店舗は道路に面する必要があるため1階の北側に店舗売場を配置し、厨房・スタッフルームなど日照を必要としない諸室を南側にまとめた。一方、住宅部分は2階・3階に配置し、居間・食事室・台所及び子ども室はいずれも南面に開口部を設けて日照を確保している。住宅の玄関は北西に設け、幅910mm（有効約780mm）の廊下1本で階段に達する動線とした。これにより、店舗は北の通りに面しながら、住宅の主要な居室はすべて南からの日照を受けられる。

② 階段の位置について工夫した点

1階のみ南北の配置を入れかえ、階段の位置は1階から3階まで変えていない。これにより2階・3階は南面に居室を並べた計画をそのまま採用でき、柱の位置も各階共通となって直下率を高く保っている。なお店舗売場の中には通り芯上の柱が1本現れるが、梁のスパンを3,640mm以下に抑えるために必要なものである。

③ 防火及び避難について配慮した点

準防火地域に建つ延べ面積198.72㎡・地上3階の木造であるため、45分準耐火建築物とした。外壁は屋内側から強化石膏ボードt=15、柱120（グラスウール16K t=100充填）、構造用合板t=9、透湿防水シート、通気胴縁t=18、窯業系サイディングt=16の構成とし、軒裏はケイ酸カルシウム板としている。3階に居室を有するため、階段室を準耐火構造の床及び壁で囲み、階段室に面する開口部を防火設備として堅穴区画とした。各居室から階段までの歩行距離を短くし、避難経路を単純にしている。

凡 例（床伏図兼小屋伏図の表示記号）

|    | 通し柱     | 1階の管柱   | 2階の管柱   | 重なる管柱 | 胴差・桁（正角材） | 同上（平角材） | 同上（丸太材） | 火打梁   | 棟木      | 母屋・小屋束 |
|----|---------|---------|---------|-------|-----------|---------|---------|-------|---------|--------|
| 記号 |         |         |         |       |           |         |         |       |         |        |
| 寸法 | 120×120 | 120×120 | 120×120 | —     | 120×120   | 図中に記入   | 図中に記入   | 90×90 | 120×120 | 90×90  |

※ 平角材（120×240 など）の断面寸法は、この欄ではなく 床伏図の中の梁1本ずつのわきに記入する。

## 標準解答例

予想問題 F 北側道路の併用住宅（書店）

木造3階建て / 8マス × 10マス（7,280 × 9,100）

- ・道路が北なので、1階だけ南北を入れかえて店舗を北（道路側）に向けた。
- ・階段の位置は動かさないので、2階・3階は型のまま使える。
- ・住宅の居室は南側に集め、日当たりを確保している。