

小学生でもわかる 答案の描き方

むずかしい言葉は使いません。「何を」「どの順番で」「どんな線で」描くかだけ。図は、この教材の本命（A型）の答案そのものを切り抜いています。

0. 答案用紙に描くのは、この8つ

名前	ひとことで言うと	時間
1階平面図 兼 配置図	1階の床から1mくらいの高さで家を水平に切って、上から見た絵。敷地（土地）も描く	40分
2階平面図	2階を同じように切って上から見た絵	30分
3階平面図	3階を同じように切って上から見た絵	25分
床伏図 兼 小屋伏図	床と屋根の骨（梁）だけを上から見た絵。壁も家具も描かない	35分
立面図	家を南から横に見た絵。屋根・窓・地面と高さの数字	20分
部分詳細図 1/20	外の壁を包丁で切った断面を5倍に大きくした絵。材料の名前と厚さ	25分
面積表	マス数を数えて掛け算	3分
計画の要点等（記述）	「なにをした・数字・なぜ・どうなる」の作文3つ	22分


いちばん大事なこと。うまく描く試験ではなく、全部描く試験です。1枚でも白紙があると不合格。線が曲がっても点は減りません。

1. マスの話（これだけ覚える）

- 答案用紙には4.55mmの方眼が印刷されています。方眼2つで910mm＝家の「1マス」。

- この家は横8マス (7,280) × たて10マス (9,100) 。1階は80マス = 66.24㎡。
- 1マス = 0.8281㎡。部屋の広さは「マスの数 × 0.8281」でおしまい。

2. 1階平面図を描く順番 (10手)

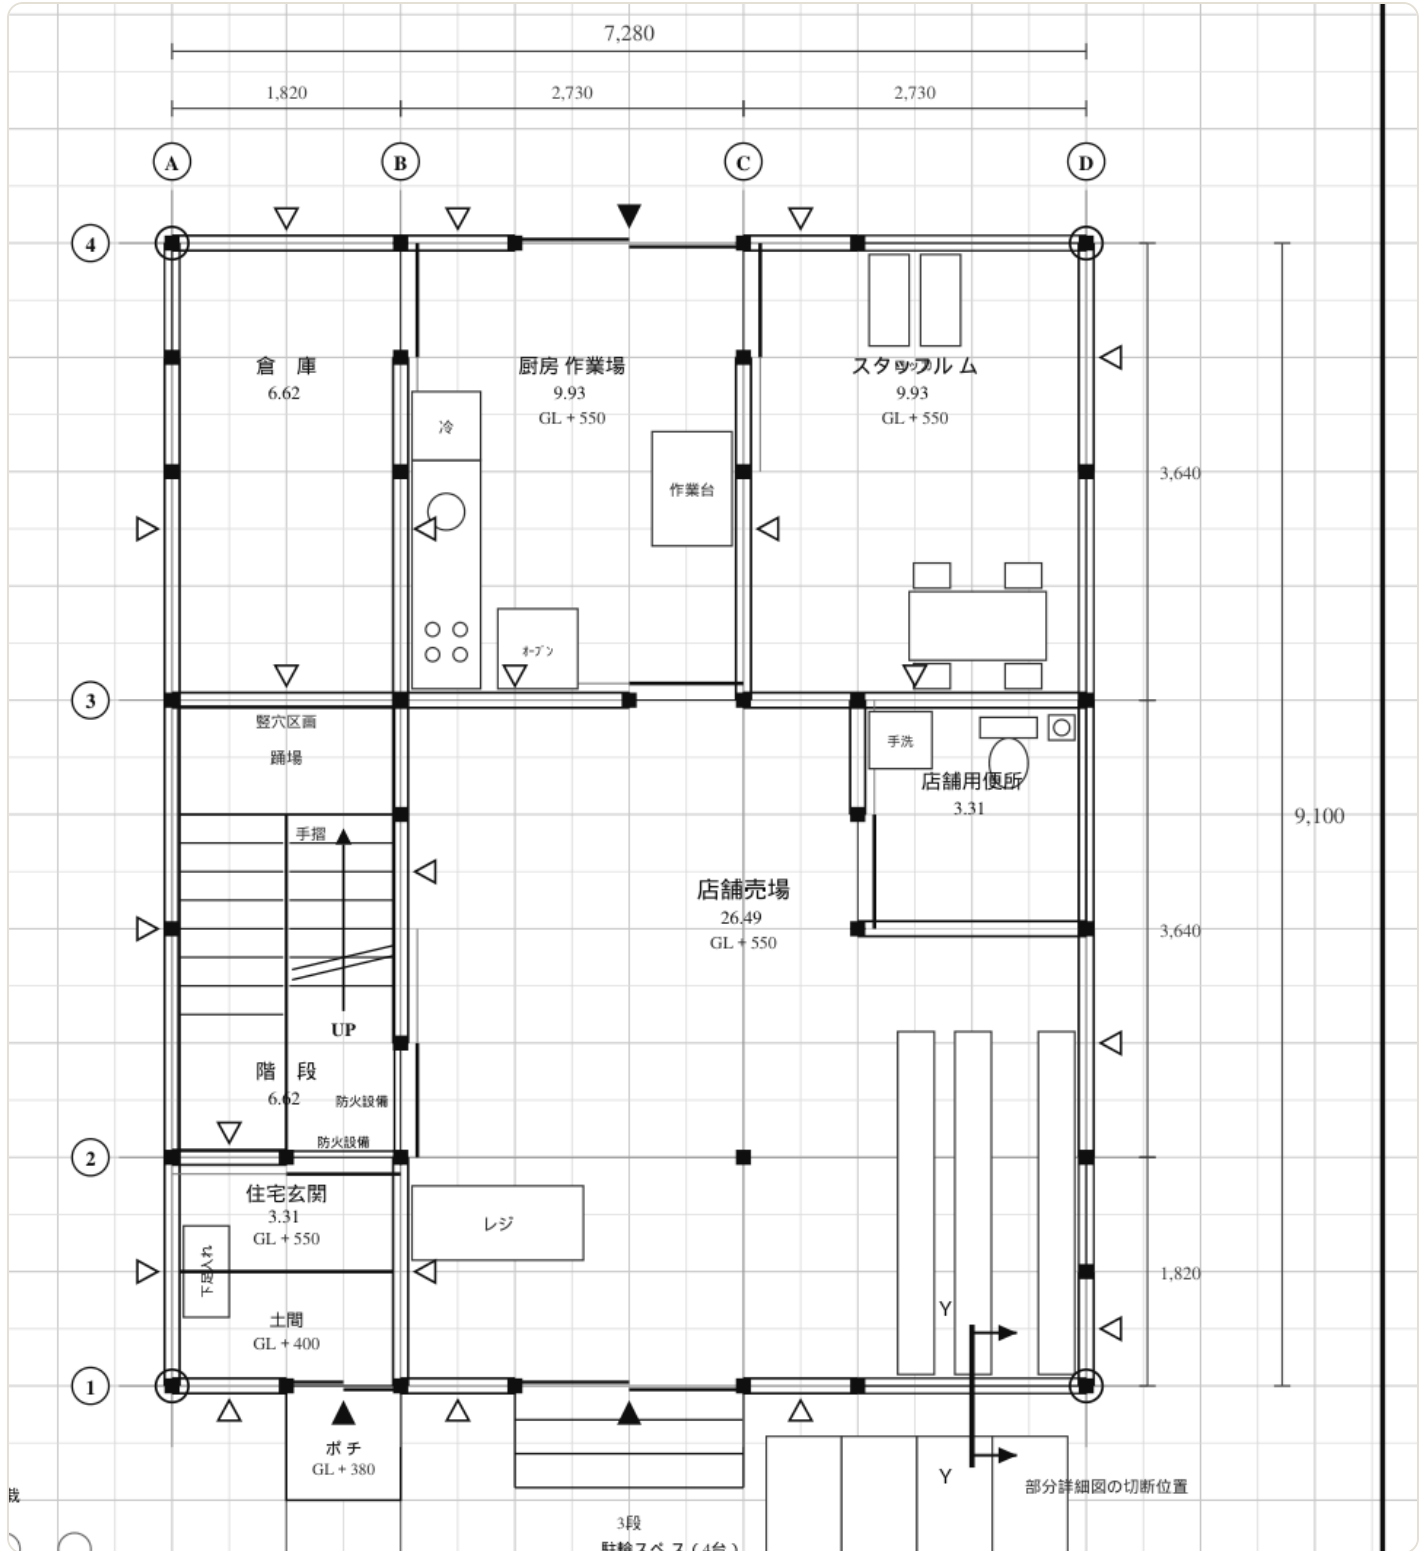

できあがり。上が北、下が南（道路）。左下が住宅の玄関、その北が階段、右の大きな部屋がお店。

1 通り芯 (細い線)

たて4本・よこ4本。柱と壁が並ぶ線。A・B・C・Dと1・2・3・4の名前を丸で書く。

2 柱 (黒い四角)

通り芯が交わる所16か所を先に。四隅の4本は**通し柱**なので、あとで○で囲む。

3 外まわりの壁 (2本線)

ぐるっと1周。壁の厚さは120なので、2本の線の間は方眼の1/4くらい。

4 中の壁 (2本線)

部屋の区切り。玄関・階段・倉庫・便所・厨房・スタッフルーム。

5 窓と戸 (記号)

壁に穴をあけて、そこに記号を描く。窓は細い線3本。戸は下の「3. 線と記号のいみ」を見る。

6 階段

横線を段の数だけ。まん中に手摺の線。矢印と **UP**。踊場と書く。

7 家具と設備 (四角と文字)

問題文に「設ける」と書いてあるものを全部。陳列棚・レジ・流し台・調理台・作業台・オープン・便器・手洗い器・下足入れ・ロッカー。**戸の前には置かない。**

8 室名・面積・床の高さ

部屋の名前、㎡、**GL+550**。玄関の土間は **GL+400**、ポーチは **GL+380**。


9 印をまとめて打つ

△（耐力壁、白ぬき、4つの面）・▲（出入口、黒ぬり、道路→敷地・→玄関・→お店）・通し柱の○・部分詳細図の切断位置（Yと矢印）。

10 寸法と敷地


寸法は2段（通りの間と全体）。敷地の線、境界までの距離4つ、道路と幅員、アプローチ・門・塀・植栽・駐輪4台・お店の前の3段、方位のN。

3. 線と記号のいみ (聞かれたものの全部)

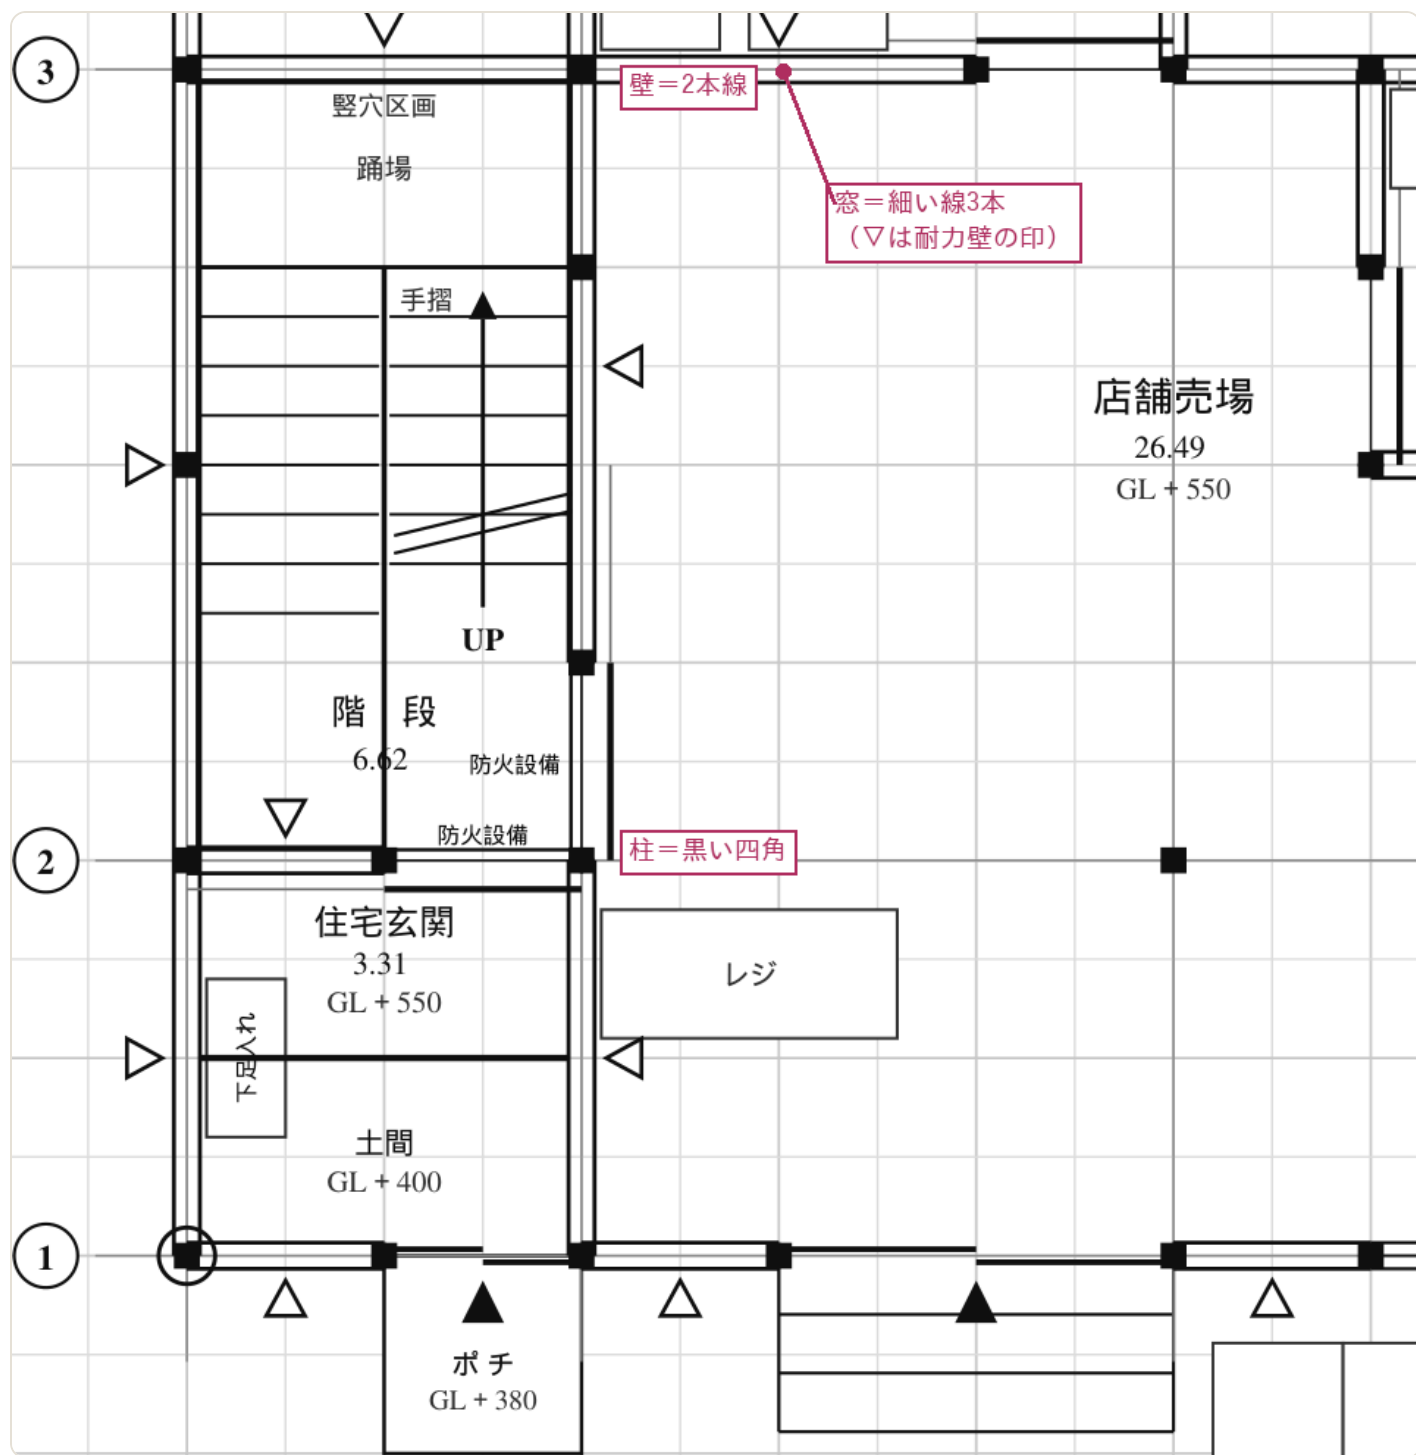

壁は2本線、柱は黒い四角、窓は細い線3本。壁のわきの▽△は耐力壁（地震にがんばる壁）の印。


引き戸（部屋の戸はぜんぶこれ）

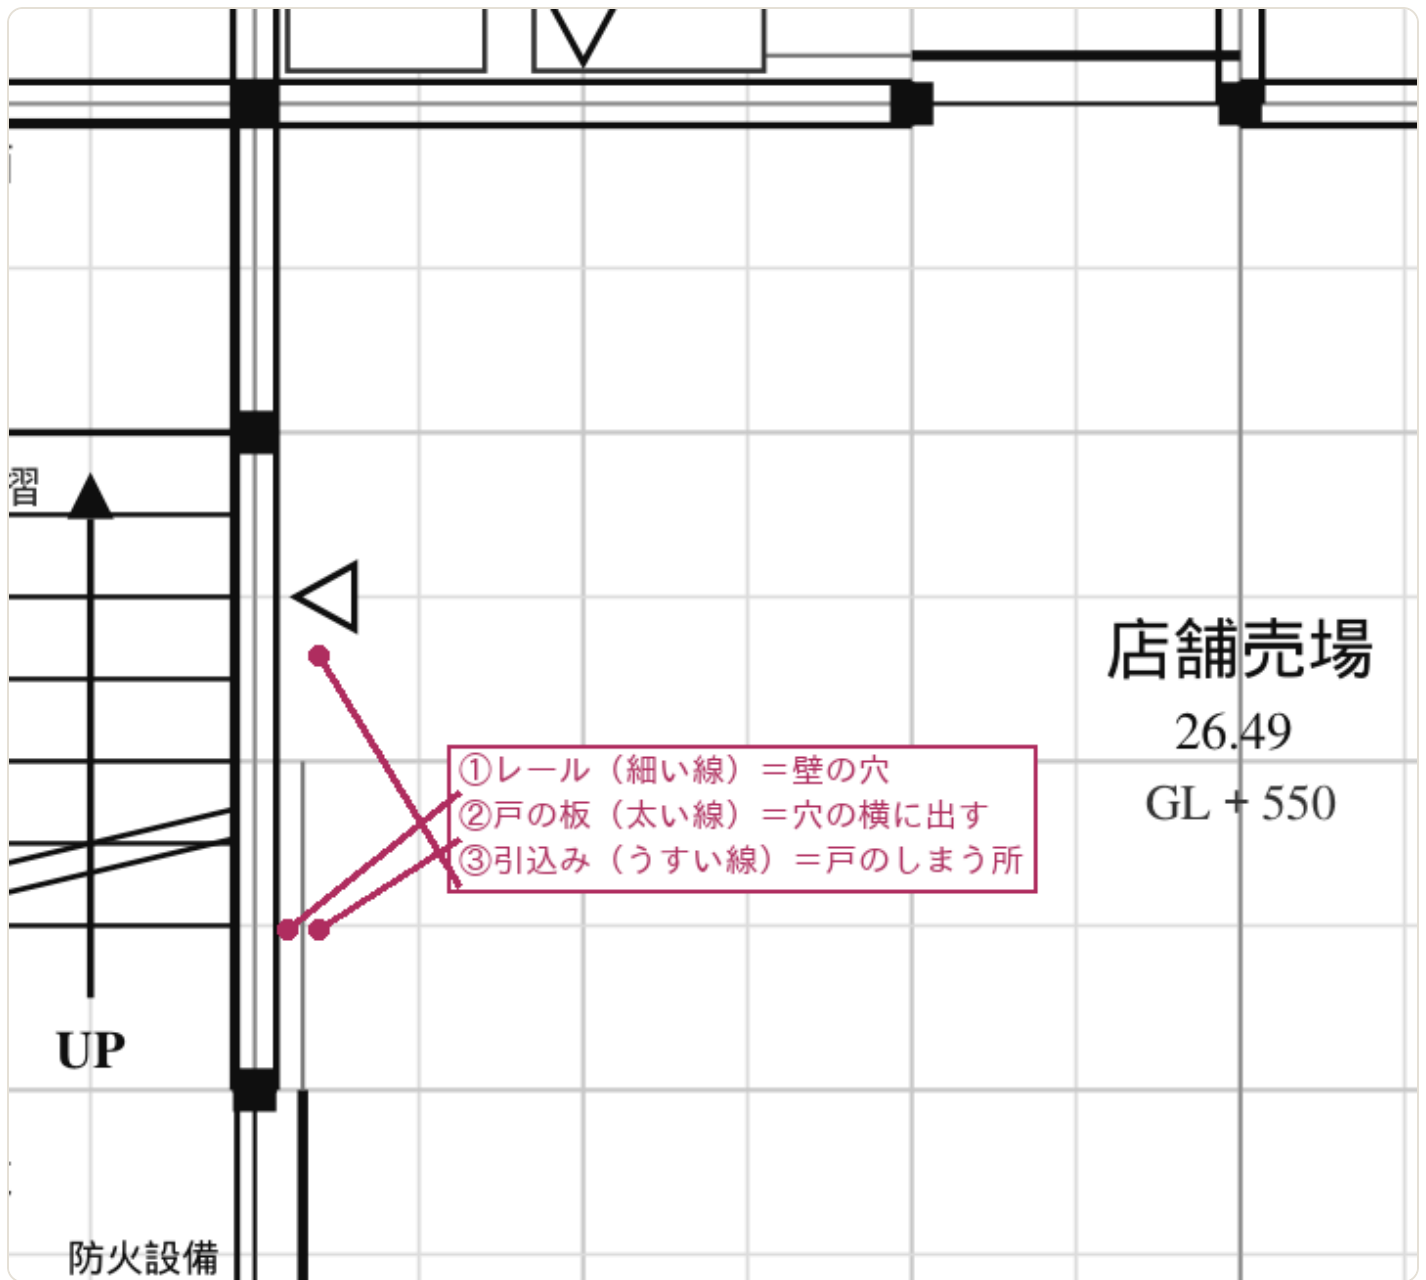

①壁の穴の中の細い線＝レール。②壁の面から少し出た太い線＝戸の板1枚。③その横に続くうすい線＝引込み（戸がしまう場所）。


引き戸のきまり。引込みの壁（戸1枚ぶん）に窓や柱を置かない。だから戸は壁の端に寄せる。1,820の穴（和室）は戸2枚を少しずらす「引違い戸」。

玄関の太い1本線＝上がり框（かまち）

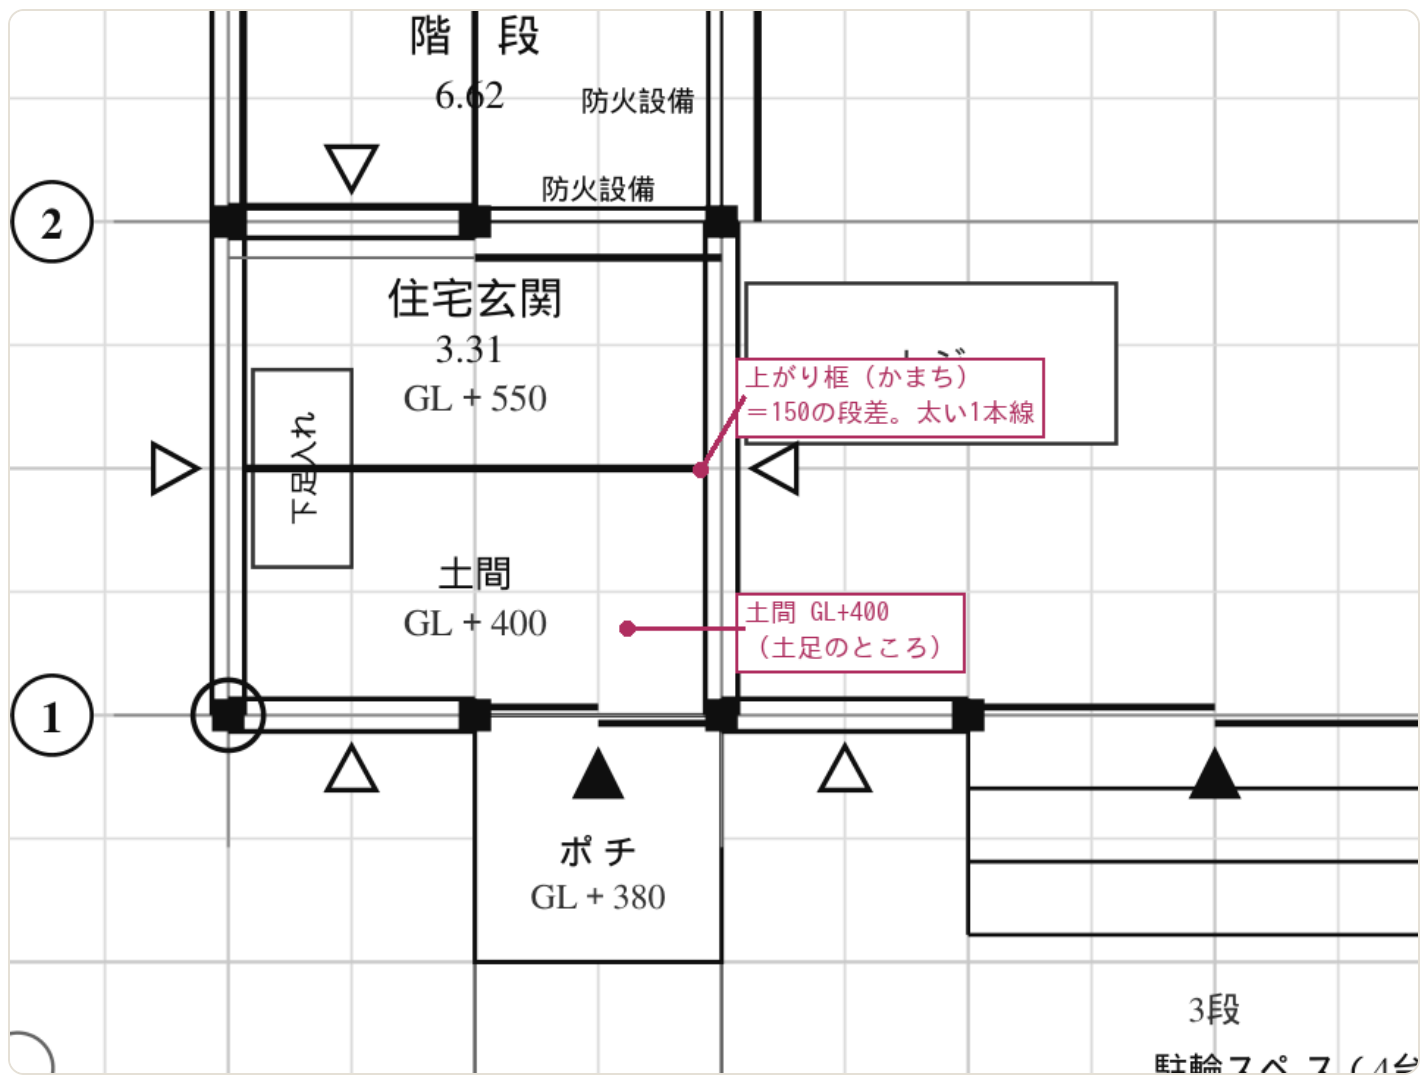


道路がわ1マスは土間（土足）GL+400。太い1本線が150の段差＝上がり框。その奥がホール GL+550。壁ではないので2本線にしない。

階段室の中身（廊下はいらない）

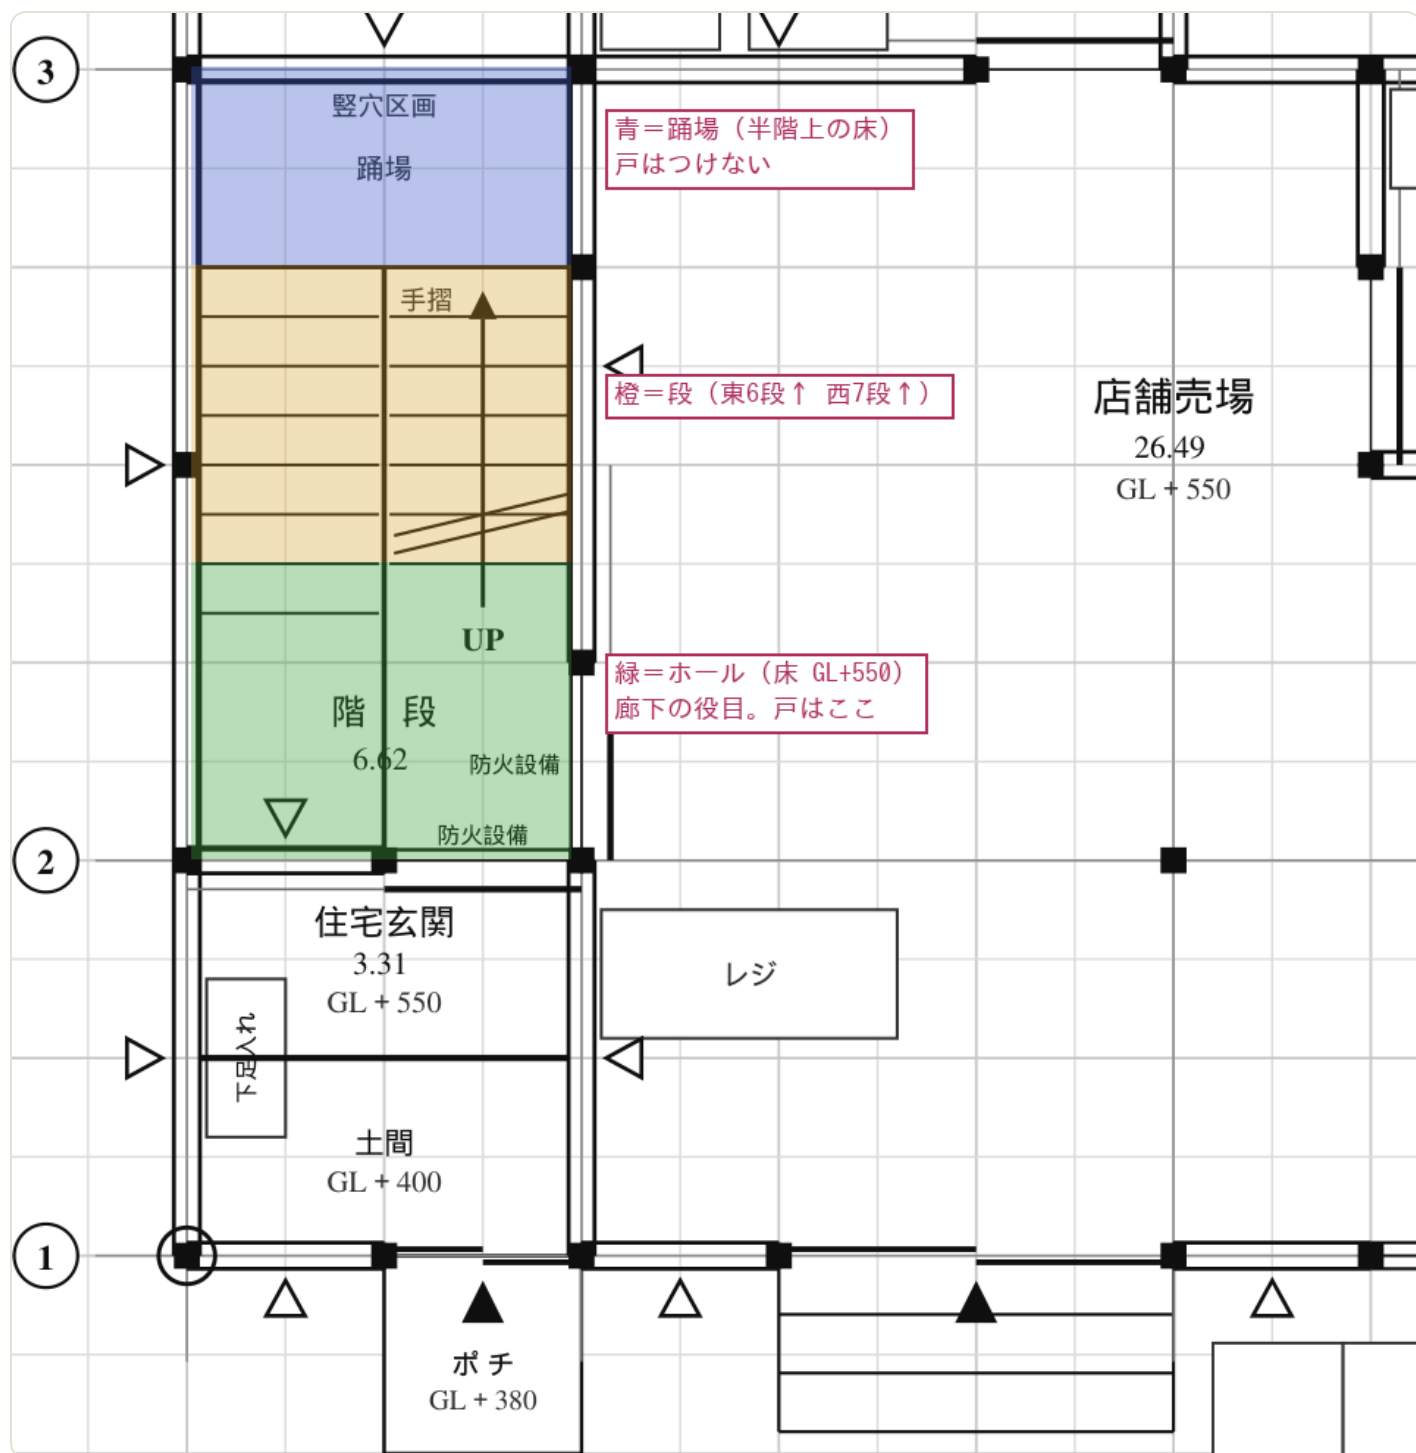

階段室 2×4マスの中は3つ。緑のホール（床）が廊下の役目で、戸はぜんぶここに付く。青の踊場は半階上の床なので、戸を付けると床のない所に出てしまう。

縦穴区画（たてあなくかく）と防火設備

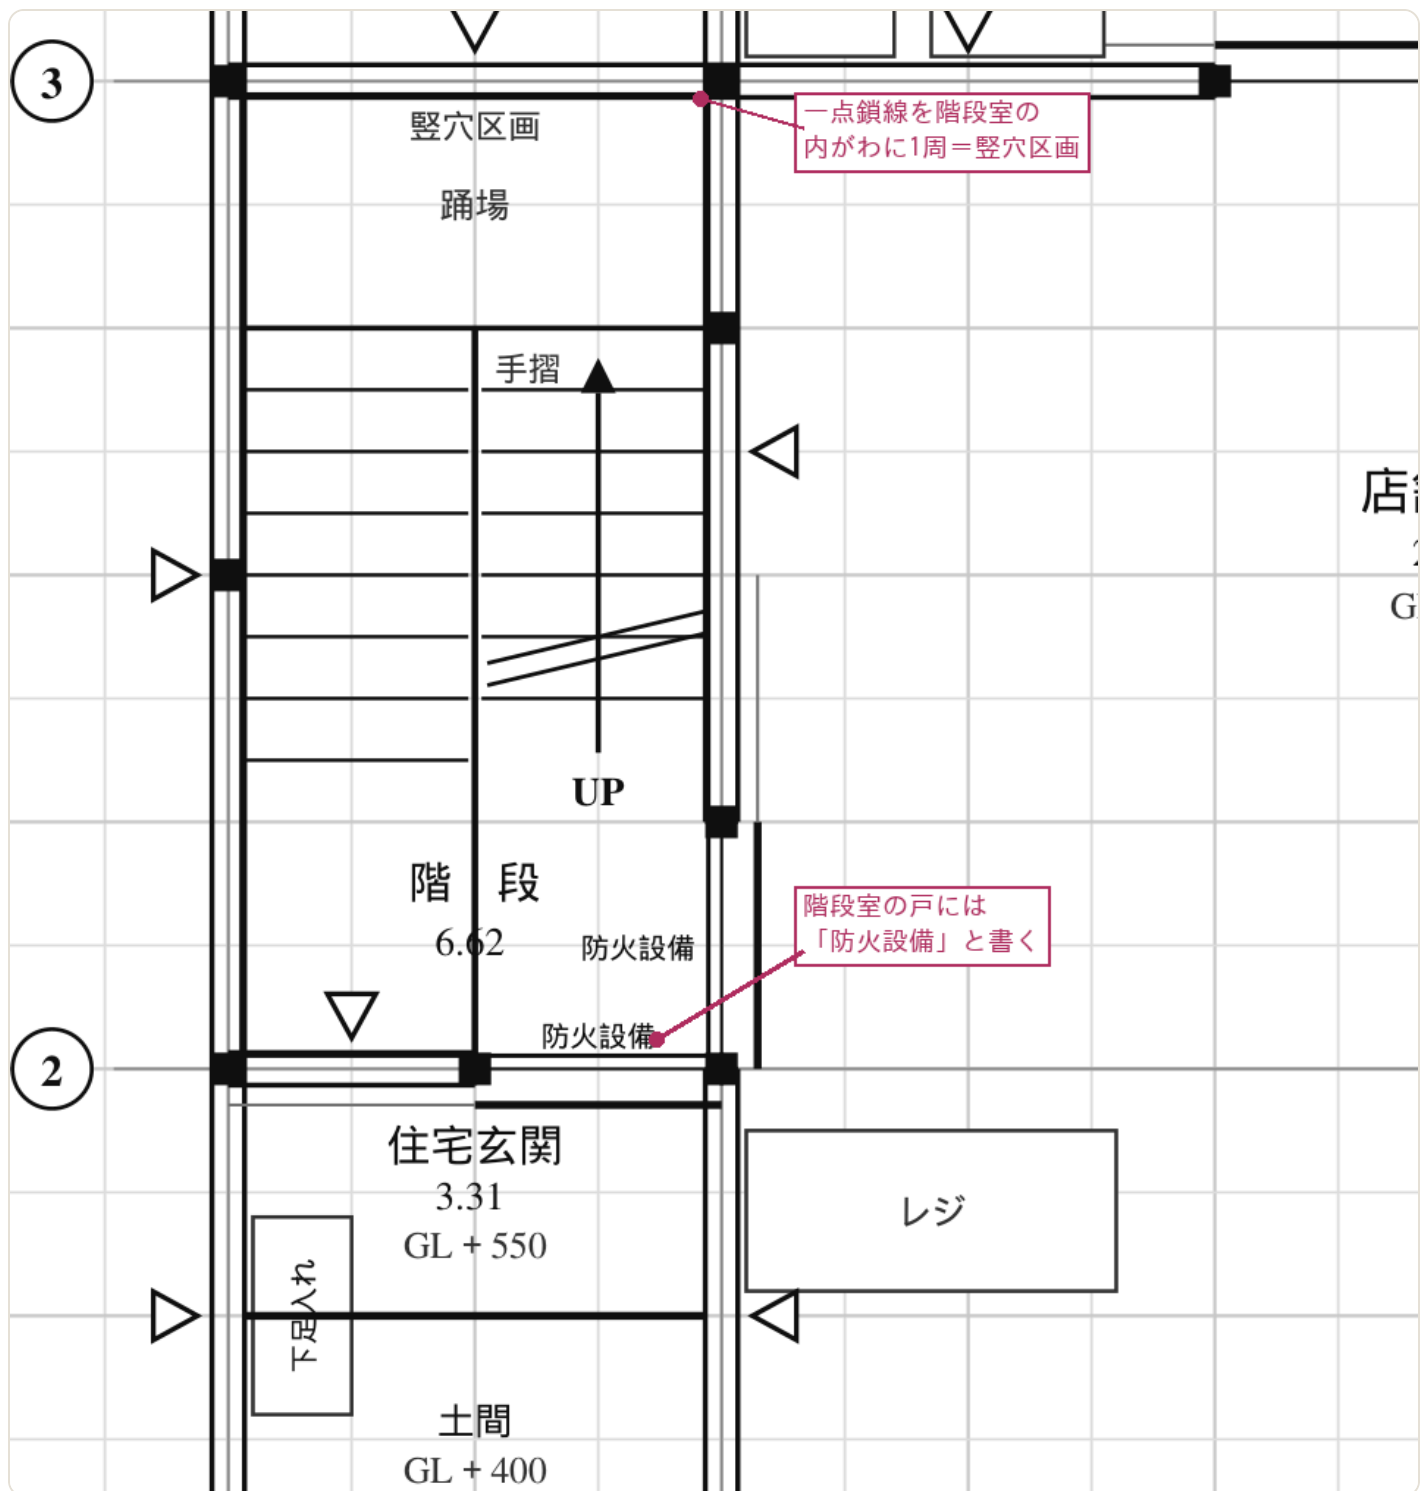


階段は1階から3階までつながった大きな穴。火事の煙が上がらないように、まわりを燃えにくい壁で囲い、戸を火に強い戸にする。答案では①一点鎖線を階段室の内がわに1周 ②「防火設備」と書く ③戸のそばに「防火設備」と書く。

そのほか


記号	いみ
△ (白ぬき)	耐力壁。壁の外がわに、4つの面ぜんぶ、各階に

▲（黒ぬり）	出入口。道路から敷地へ・玄関へ・お店へ（型なら3か所）
□を○で囲む	通し柱（1階から3階まで1本の柱）。四隅の4本
Y →	部分詳細図の切断位置と、見る向き。1階平面図に描く
GL+550	地面（GL）から550mm高い床、という意味。1階の床はぜんぶこれ（土間だけ+400）
UP／DN	階段の矢印。上る／下りる。1階はUPだけ、2階はUPとDN、3階はDNだけ

4. 2階・3階は「1階を写す」

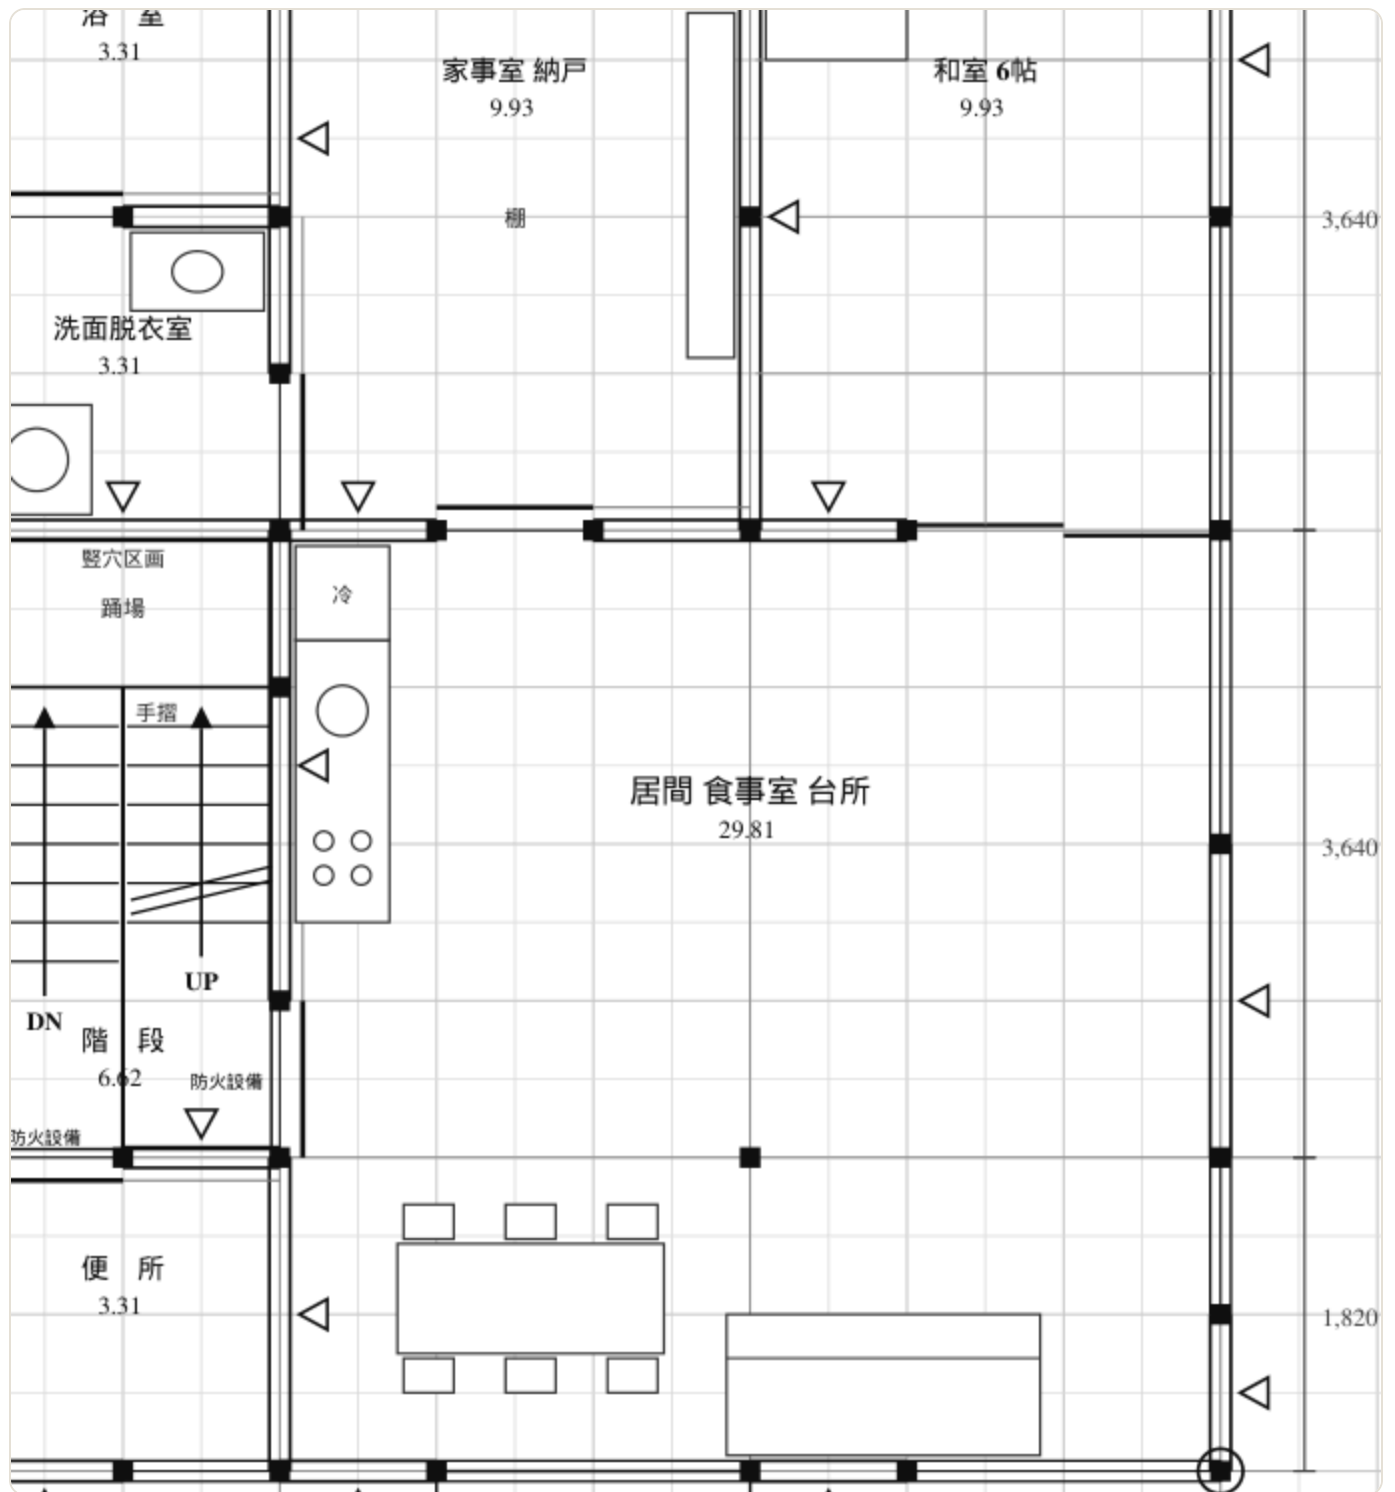


2階。柱と外壁は1階と同じ位置に写す。西の列に便所・階段・洗面脱衣室・浴室。大きな居間は南。

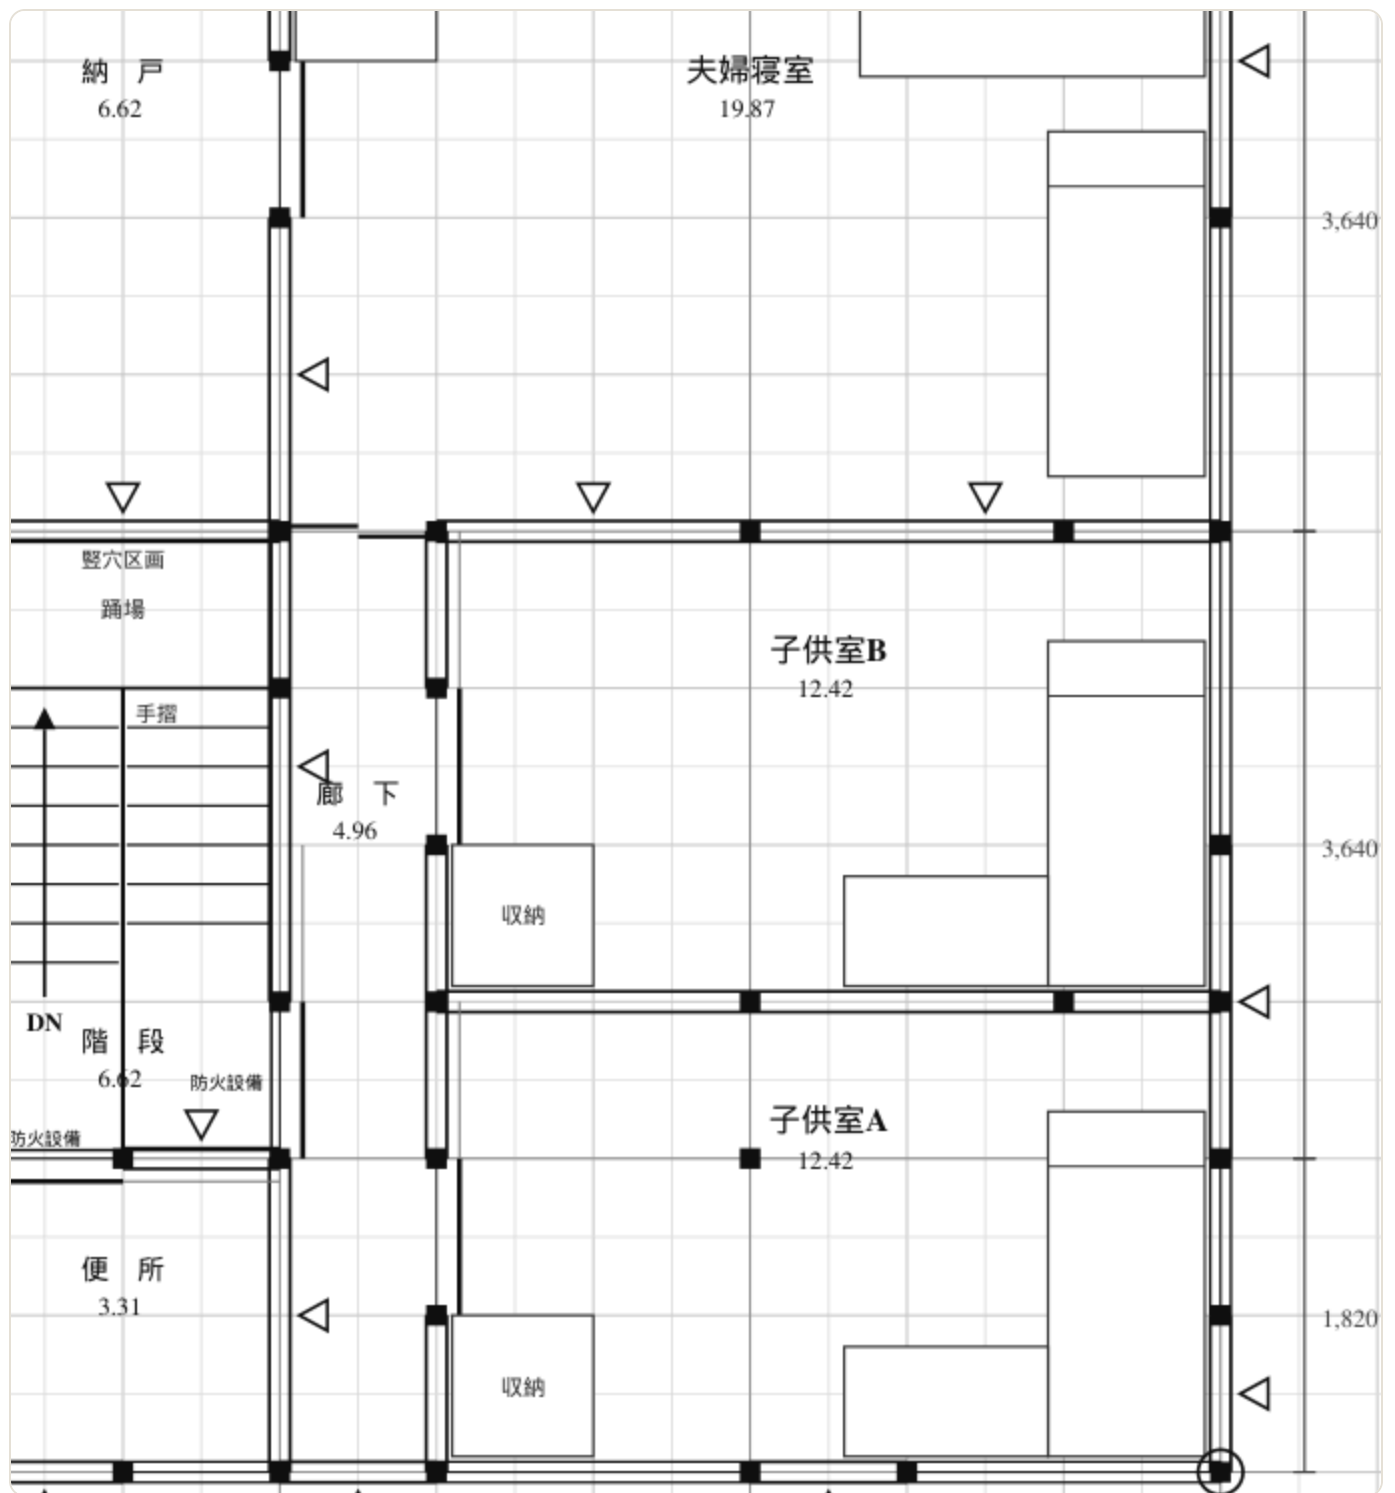

3階。階段から廊下に出て、子供室2つ（同じ広さ）と寝室へ。道路がわの窓は直径1mの丸が入る大きさ（消防が入る窓）。

- 1階とちがう所は3つだけ：敷地を描かない・階段の矢印（2階は2本、3階はDN）・家具（ソファ・テーブル・椅子4・台所・畳・押入・浴槽・洗面台・洗濯機・ベッド・机・収納）。
- 2階の床の高さは書かなくてよい（指定があれば書く）。


5. 伏図 = 骨だけの絵

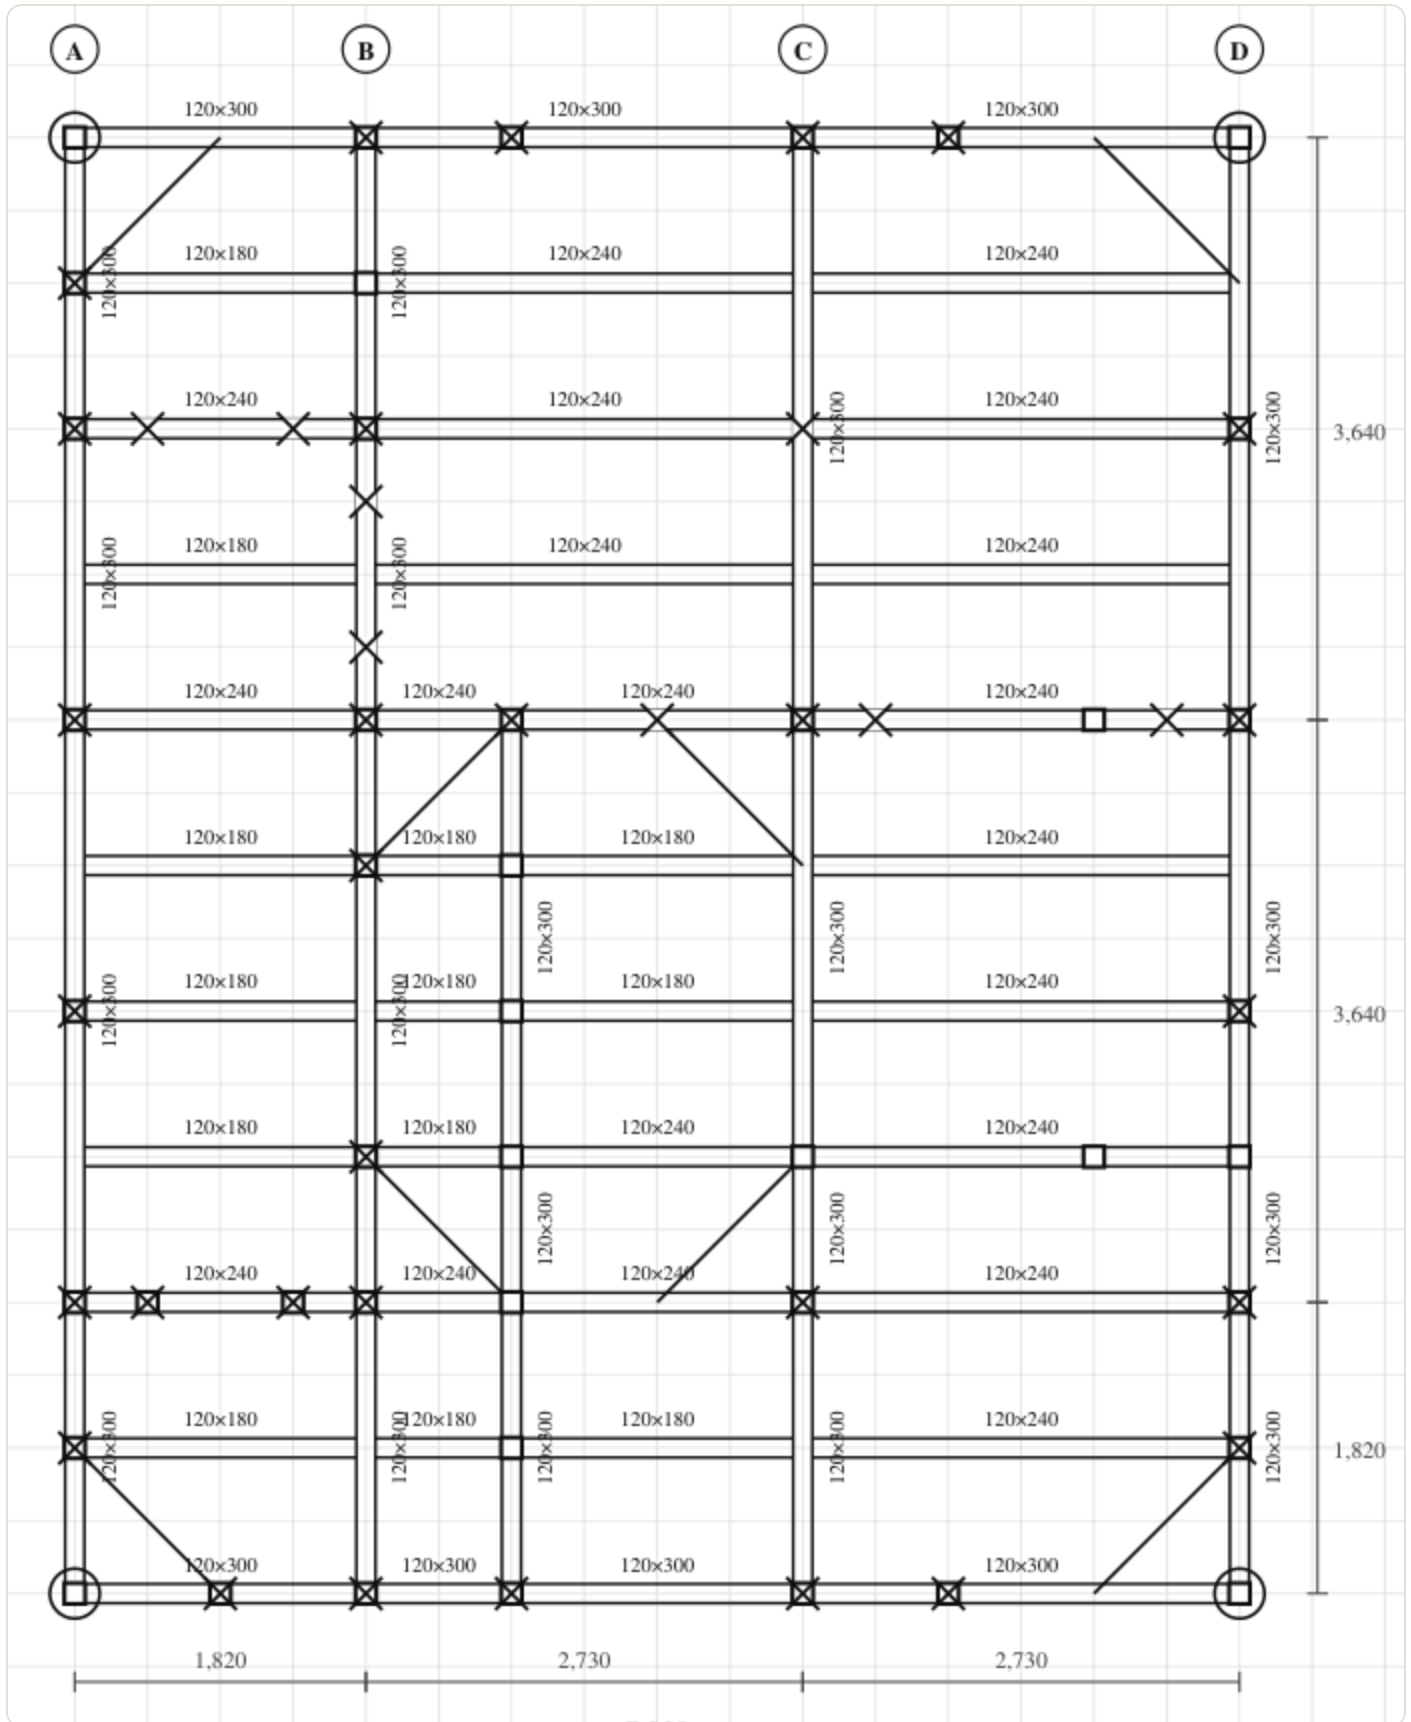


3階床伏図。壁も家具も描かない。柱の記号と梁（棒）と数字だけ。

- 壁の下には必ず梁。2階の壁の上・3階の壁の下・通り芯・その間は910おきに床梁。
- 柱の記号は4つ：通し柱＝□を○で囲む、下の階（2階）の柱＝×、上の階（3階）の柱＝□、上下とも＝⊠。
- 梁の太さは幅120で、せい（たて）はスパンで決める：1,820→180、2,730→240、3,640→300。数字は⊠の中の梁のわきに1本ずつ。
- 凡例欄には 通し柱120×120／管柱120×120／正角材120×120／火打梁90×90／棟木120×120／母屋90×90 を書く。表は自分で作らない。

3階の廊下の壁の下梁。
壁が終わる所で梁も終わり、
横の梁に載って止まる

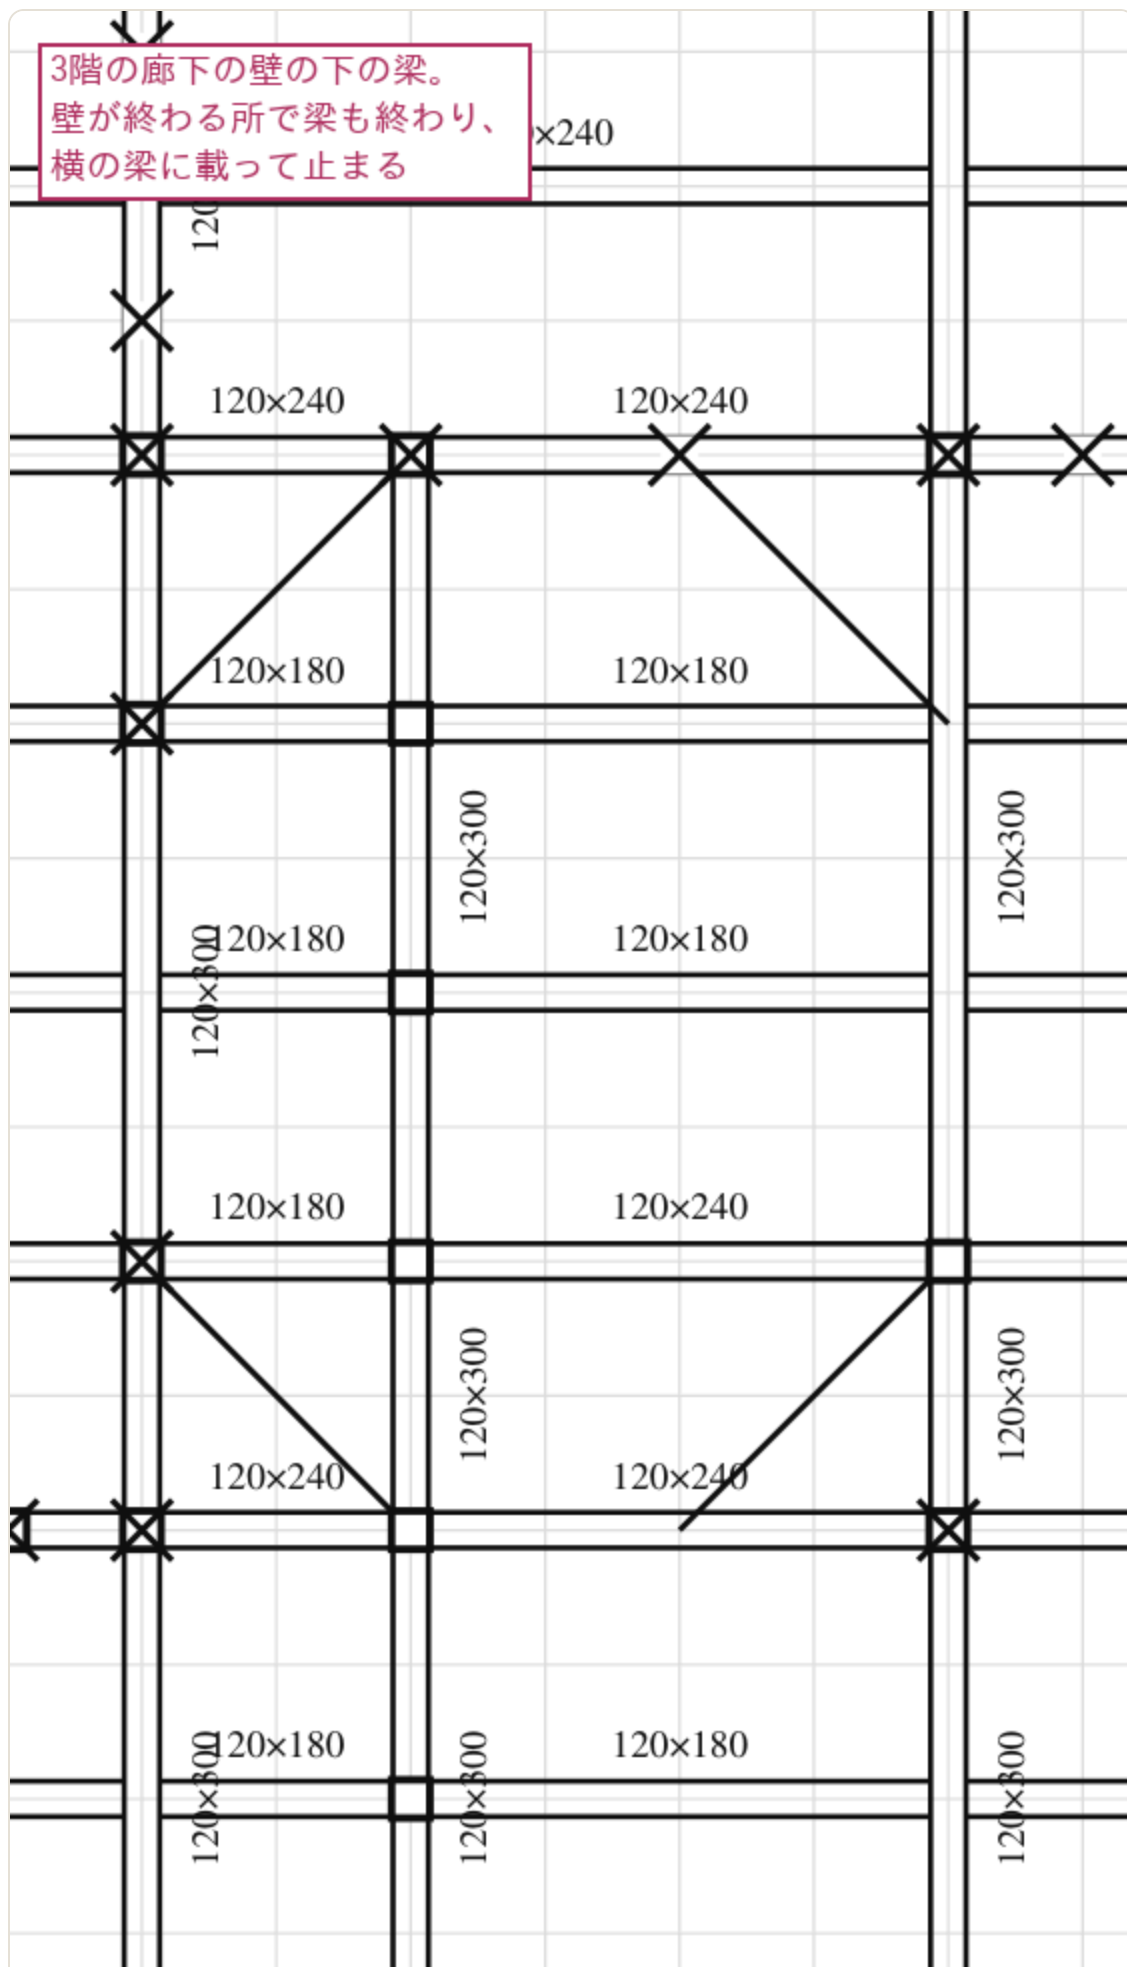


梁が途中で終わっているのは、壁がそこまでだから。梁は別の梁に載って止まってよい。

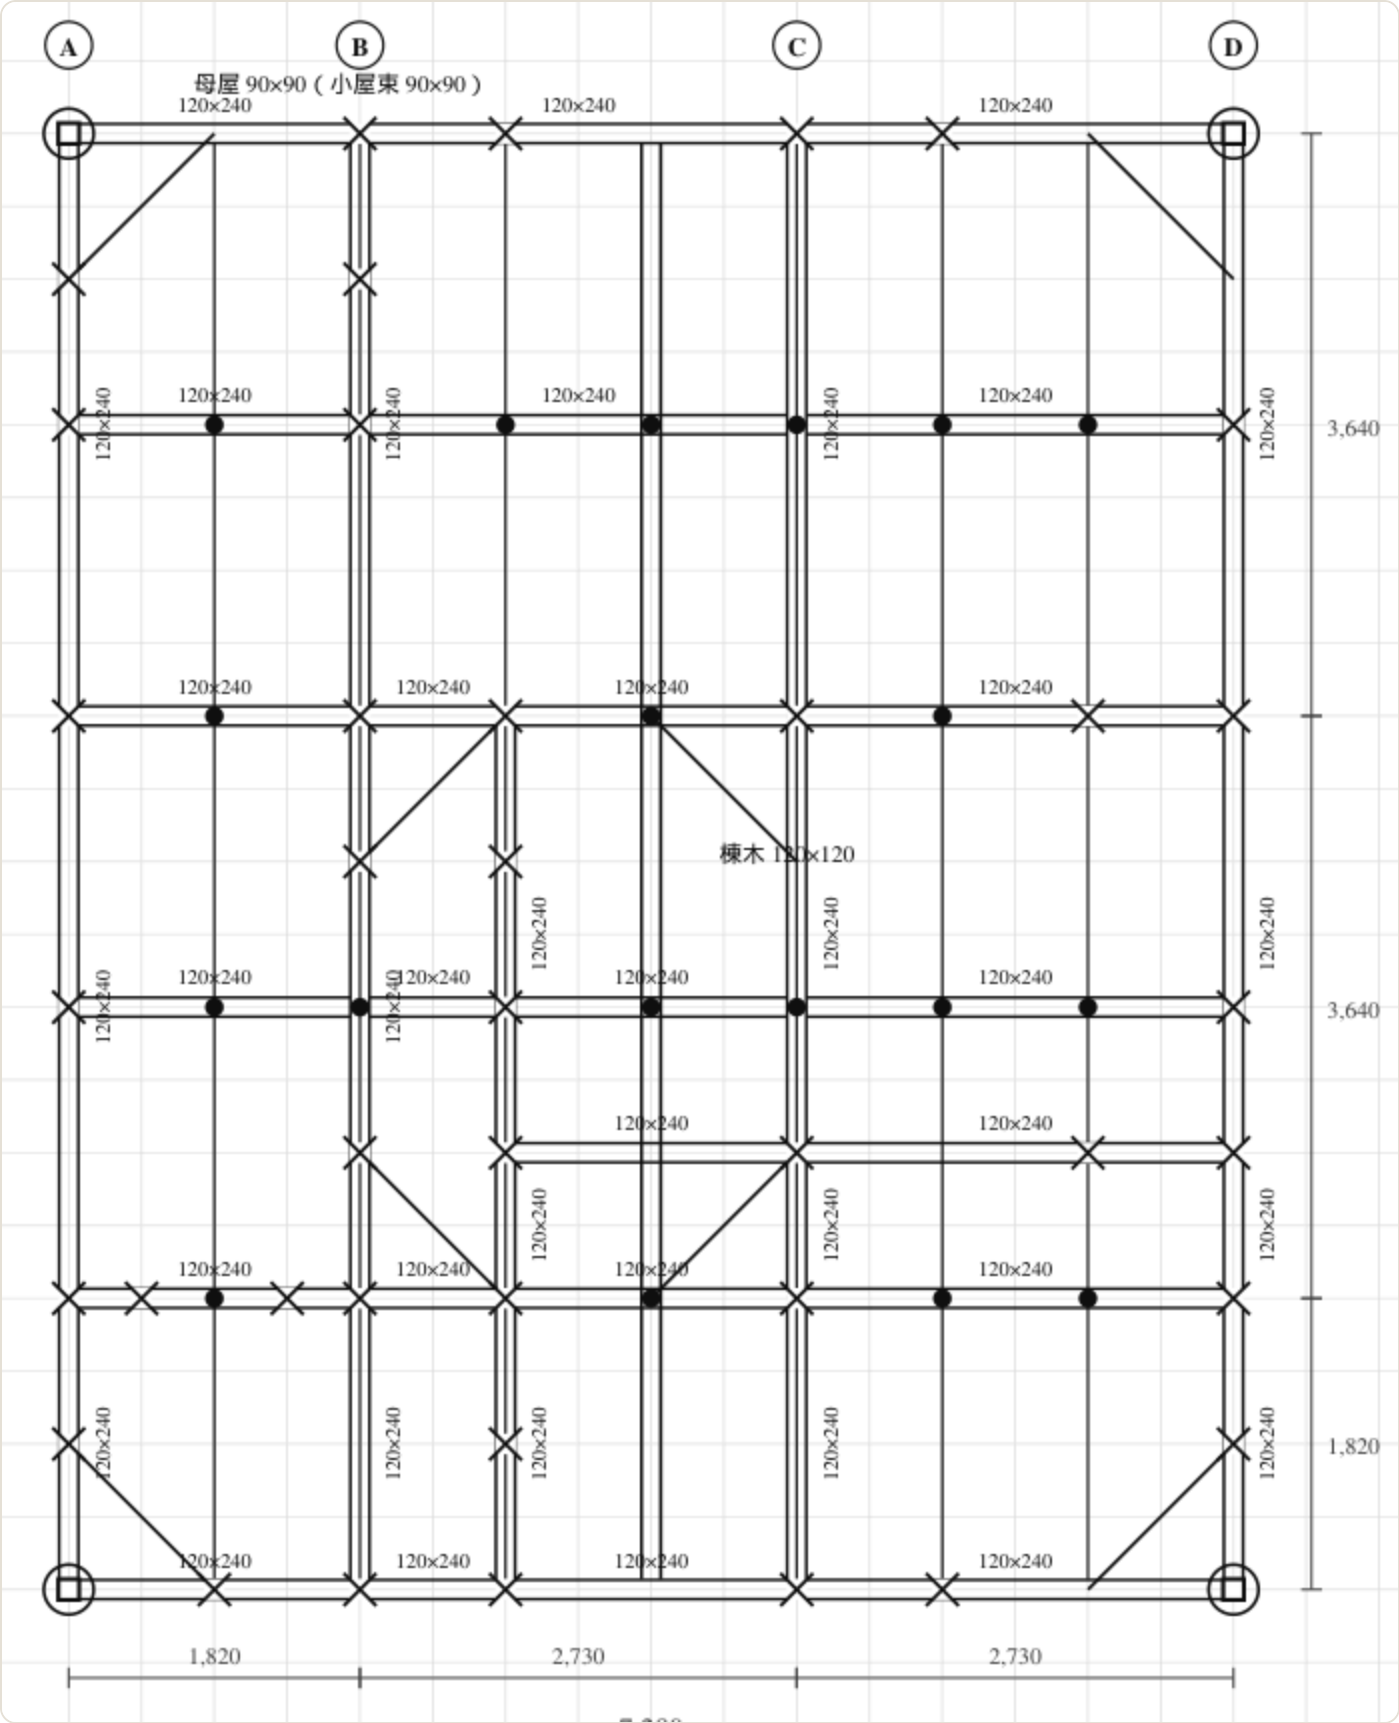

小屋伏図（屋根の骨）。まん中のたて線が棟木（実線2本）、その両側に母屋（一点鎖線）、●は小屋束、四隅の破線が火打梁。

6. 立面図＝地面から足し算

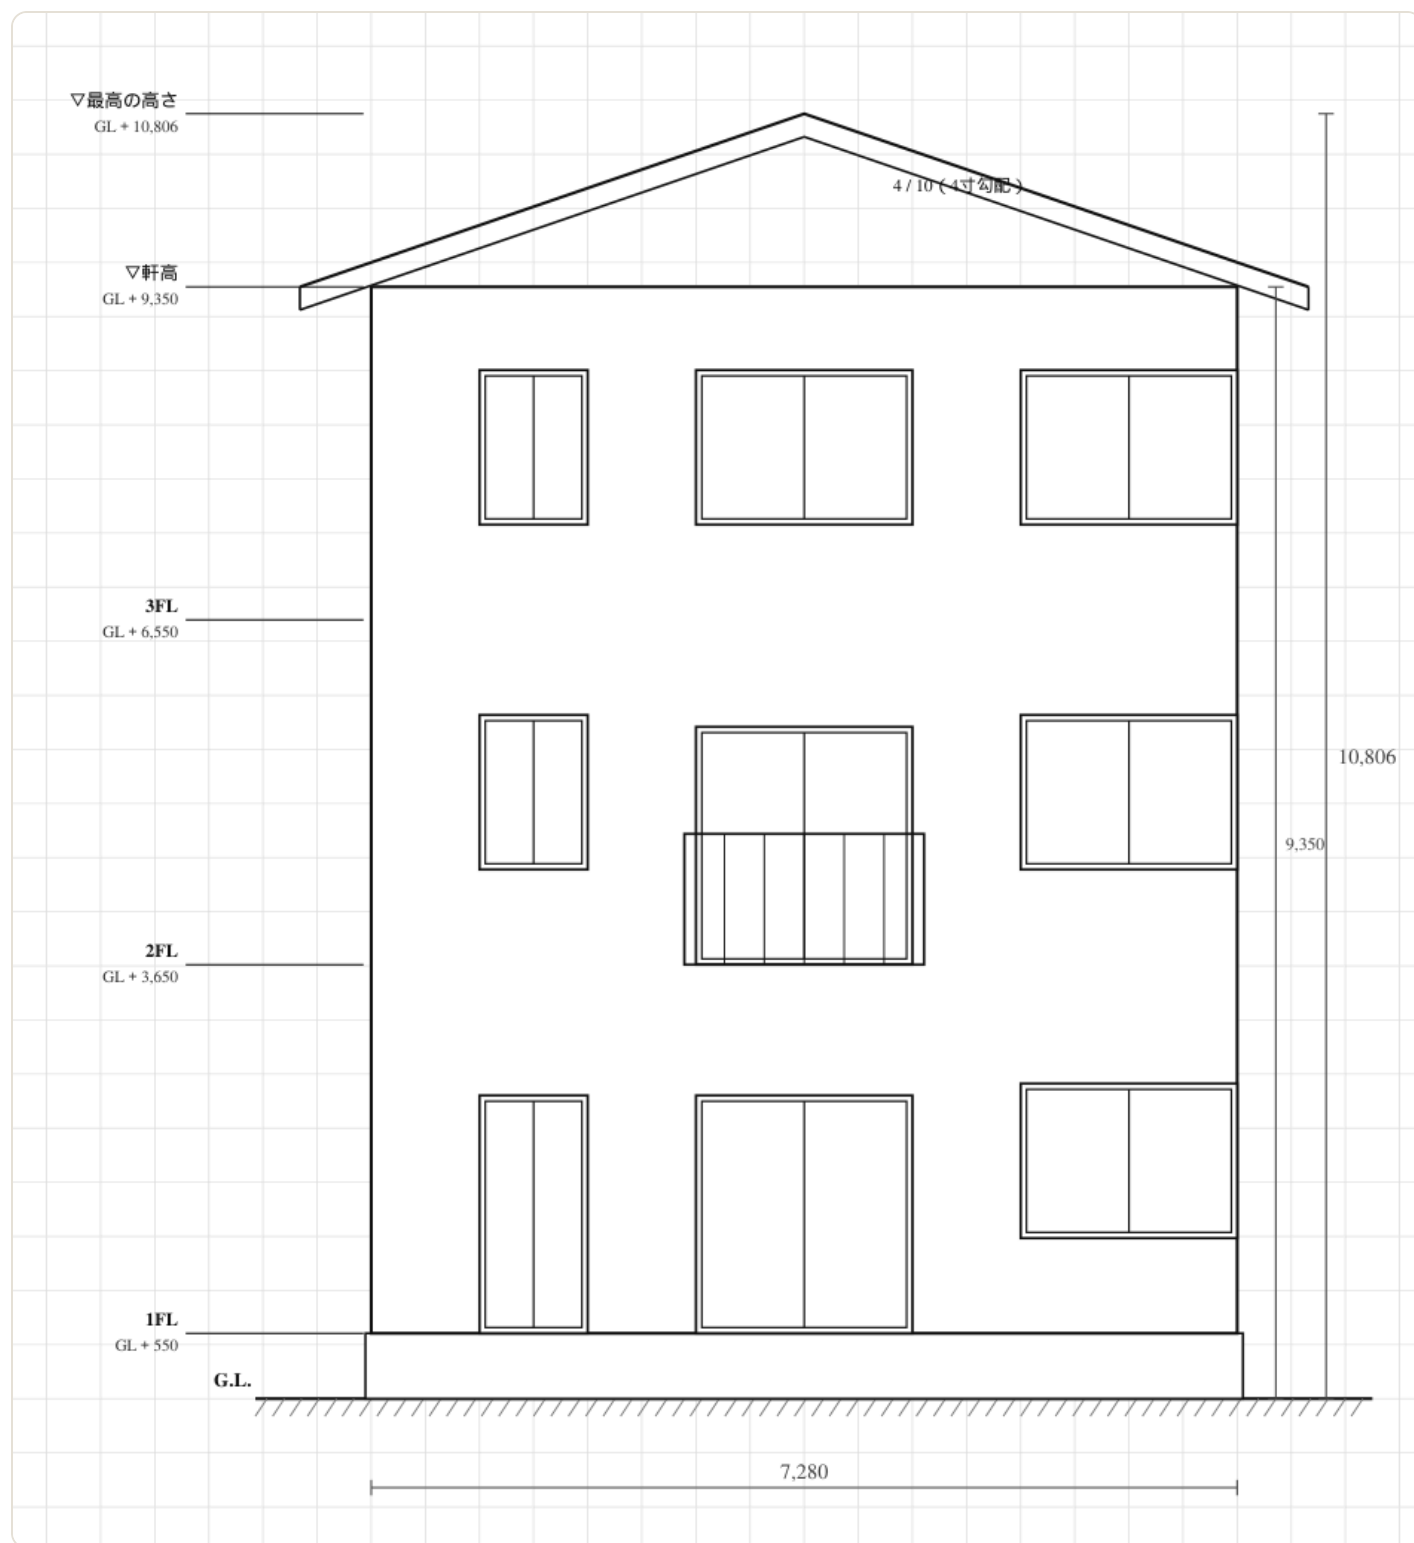

南から見た絵。屋根の棟が南北なので三角に見える。

- まず**地面の線 (GL)** を1本。そこから上へ足し算： $1\text{FL} + 550 \rightarrow 2\text{FL} + 3,650 \rightarrow 3\text{FL} + 6,550 \rightarrow \text{軒} + 9,350 \rightarrow \text{てっぺん} + 10,806$ 。
- 窓は平面図の窓の真上に**糸を垂らす**ように写す。腰窓は床から800～2,100、掃き出し窓は0～2,100。
- 「▽最高の高さ 10,806」など、問題文が要求した数字を必ず書く。


7. 部分詳細図＝壁を包丁で切った絵（5倍）

部分詳細図（外壁 断面） 1/20

左が室内・右が屋外 / 準防火地域の準耐火建築物（45分）を想定

★ 本番の解答用紙に描いて提出するのは、この1枚

← 室内 屋外 →

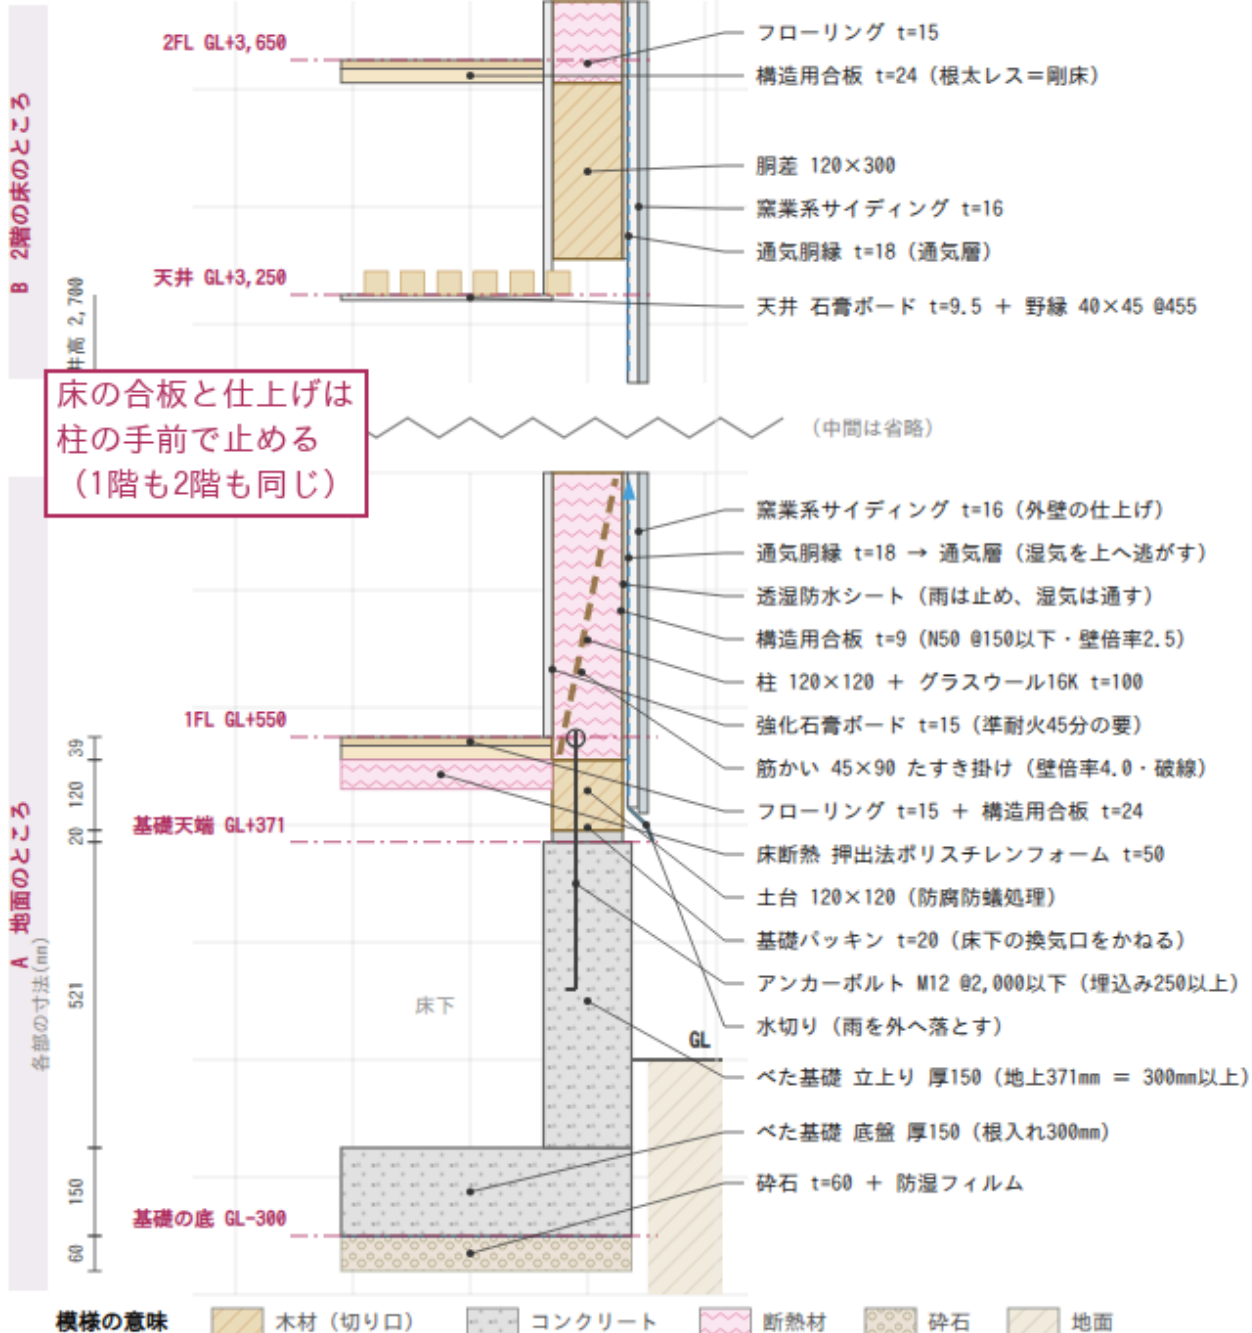

★ 外壁の厚さ $15+120+9+18+16 = 178\text{mm}$ 。この6層を「内から外へ」の順で覚える。

左が部屋の中、右が外。上が2階の床のところ、下が地面のところ。

- この図だけ方眼が10mm（1目盛＝実物200mm）。
- 材料より先によこ線**5本**：GL・基礎の上（+371）・1FL（+550）・天井（+3,250）・2FL（+3,650）。
- 下から積む：碎石→基礎（底盤150・立上り150、地面の上371・下300）→基礎パッキン20→土台120→合板24→フローリング15＝**550**。
- 外壁は内から外へ6層：強化石膏ボード15→柱120（中に断熱材）→構造用合板9→透湿防水シート→通気胴縁18→サイディング16。
- 床の合板と仕上げは、柱の手前で止める。1階も2階も同じ。
- 最後に材料の名前と厚さを右に引出線で。ここを書かないと点にならない。

8. 面積表と記述

面積表：建築面積＝ $7.28 \times 9.10 = 66.24$ 。各階も66.24。延べ面積＝ $66.24 \times 3 = 198.72$ 。小数第3位は切り捨て。ポーチ・バルコニー・駐輪は入れない。

記述：1問は「①なにをした→②数字→③なぜ→④どうなる」の4つをつなぐだけ。数字（120角・3,640・t=24・有効780）を必ず入れる。自分の図面を見ながら書く。白紙は全損なので、図面より先に書く。

9. 最後の15分は「描き足さない」

1. 図面が8つ全部ある
2. 問題文の部屋の表を指でなぞって、全部ある・階が合っている
3. 面積が範囲内
4. 各階に階段・どの部屋にも戸から入れる
5. △・▲・○・切断位置・高さの数字・室名・面積・方位・縮尺
6. 受験番号・氏名

やってはいけない3つ。 白紙の図面／要求された部屋がない／延べ面積が範囲の外。これだけで不合格になります。