


凡 例 (床伏図兼小屋伏図の表示記号)

| 通し柱                                                                                   | 1階の管柱                                                                                 | 2階の管柱                                                                                 | 重なる管柱 胴差・桁（正角材）                                                                       | 同上（平角材）                                                                               | 同上（丸太材）                                                                               | 火打梁                                                                                   | 棟木                                                                                    | 母屋・小屋束                                                                                |       |
|---------------------------------------------------------------------------------------|---------------------------------------------------------------------------------------|---------------------------------------------------------------------------------------|---------------------------------------------------------------------------------------|---------------------------------------------------------------------------------------|---------------------------------------------------------------------------------------|---------------------------------------------------------------------------------------|---------------------------------------------------------------------------------------|---------------------------------------------------------------------------------------|-------|
|  |  |  |  |  |  |  |  |  |       |
| 120×120                                                                               | 120×120                                                                               | 120×120                                                                               | —                                                                                     | 120×120                                                                               | 図中に記入                                                                                 | 図中に記入                                                                                 | 90×90                                                                                 | 120×120                                                                               | 90×90 |

※ 平角材（100×60、60×40）の断面は、床下図中の梁1本を、丸太に記入する。

※ 平角材（120×240 など）の断面寸法は、床伏図の中の梁1本ずつのわきに記入する。

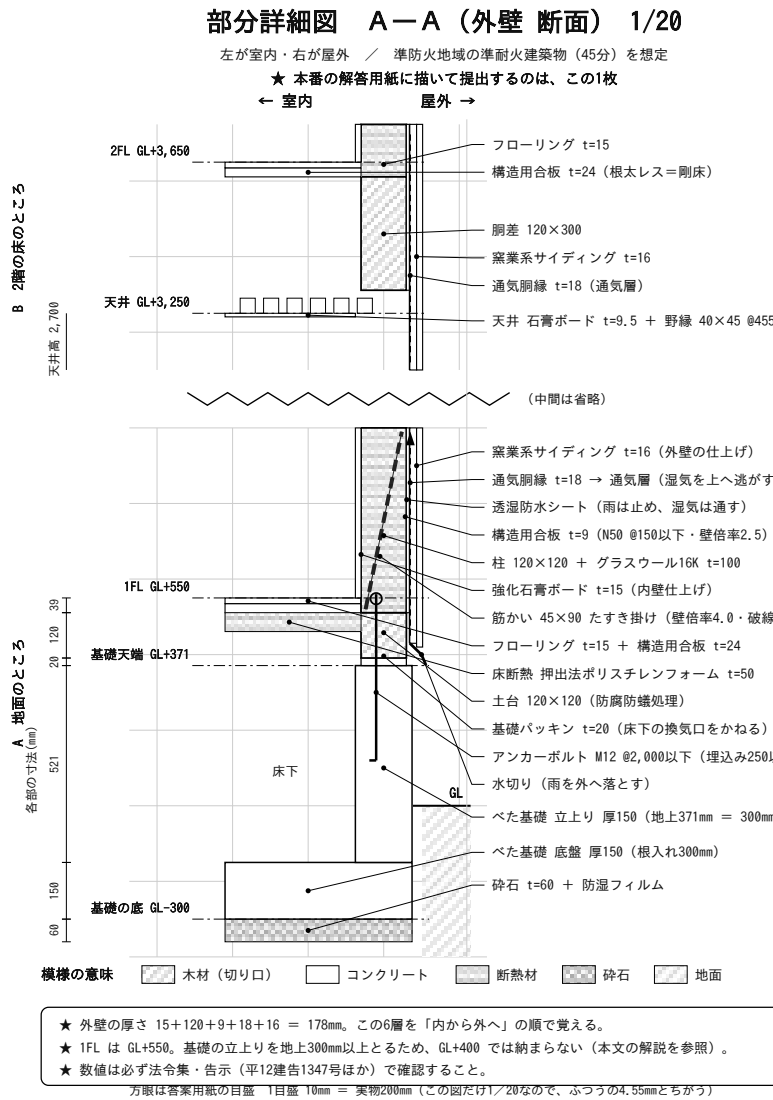

### 標準解答例


受験番号

氏名


予想問題 A 商店街に建つ併用住宅（物販店舗）

木造3階建て / 8マス × 10マス (7,280 × 9,100)


(1) 1階平面図 兼 配置図 縮尺1／100 (目盛4.55mm)

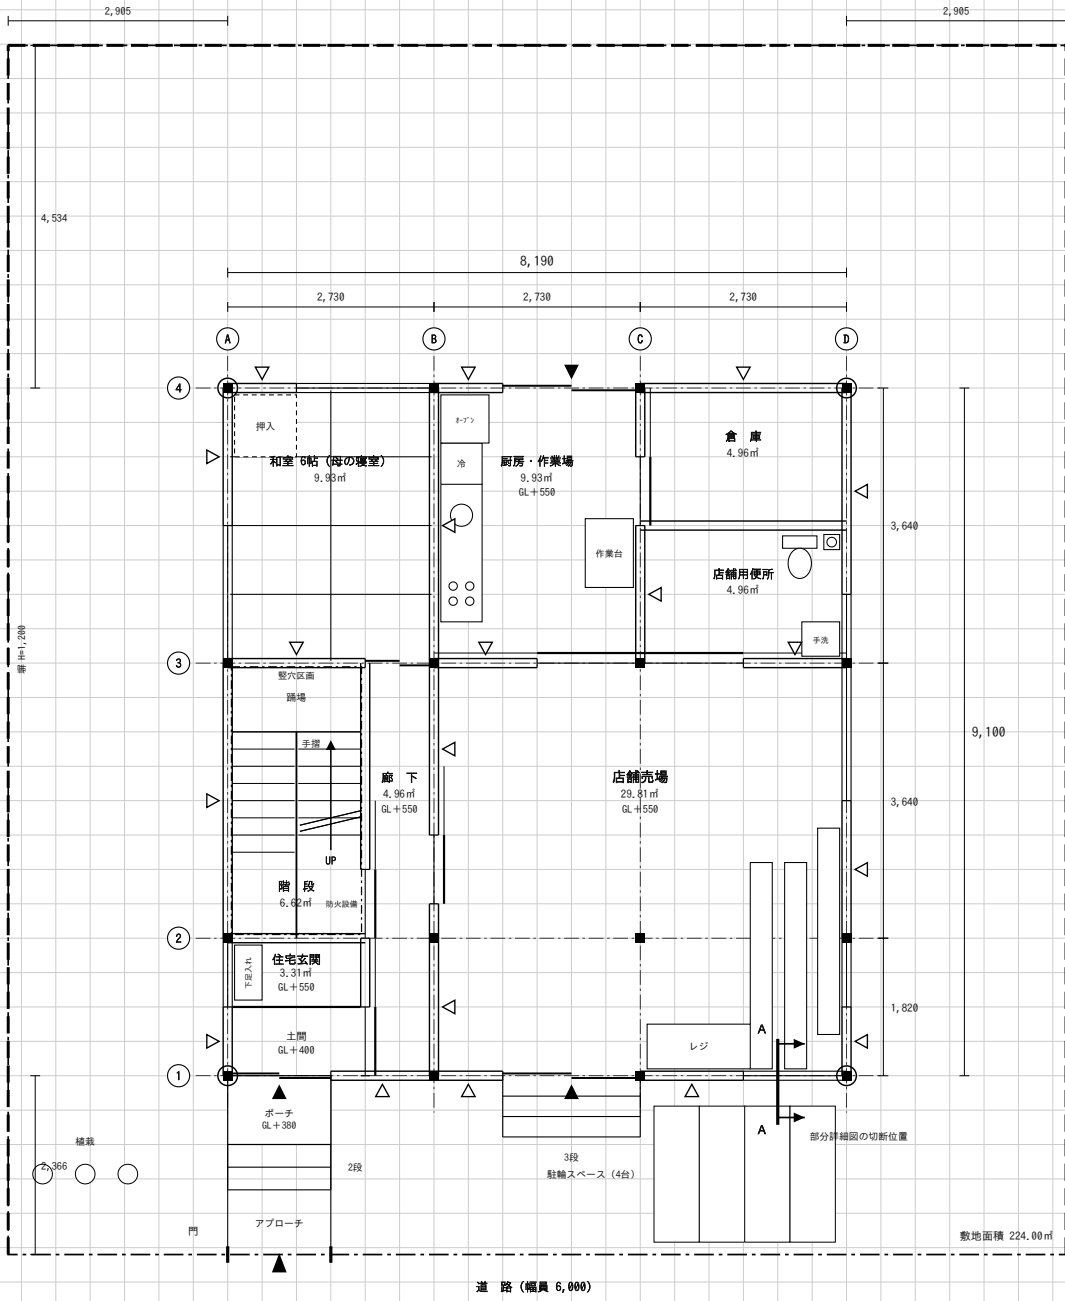


(2) 2階平面図 縮尺1／100 (目盛4.55mm)

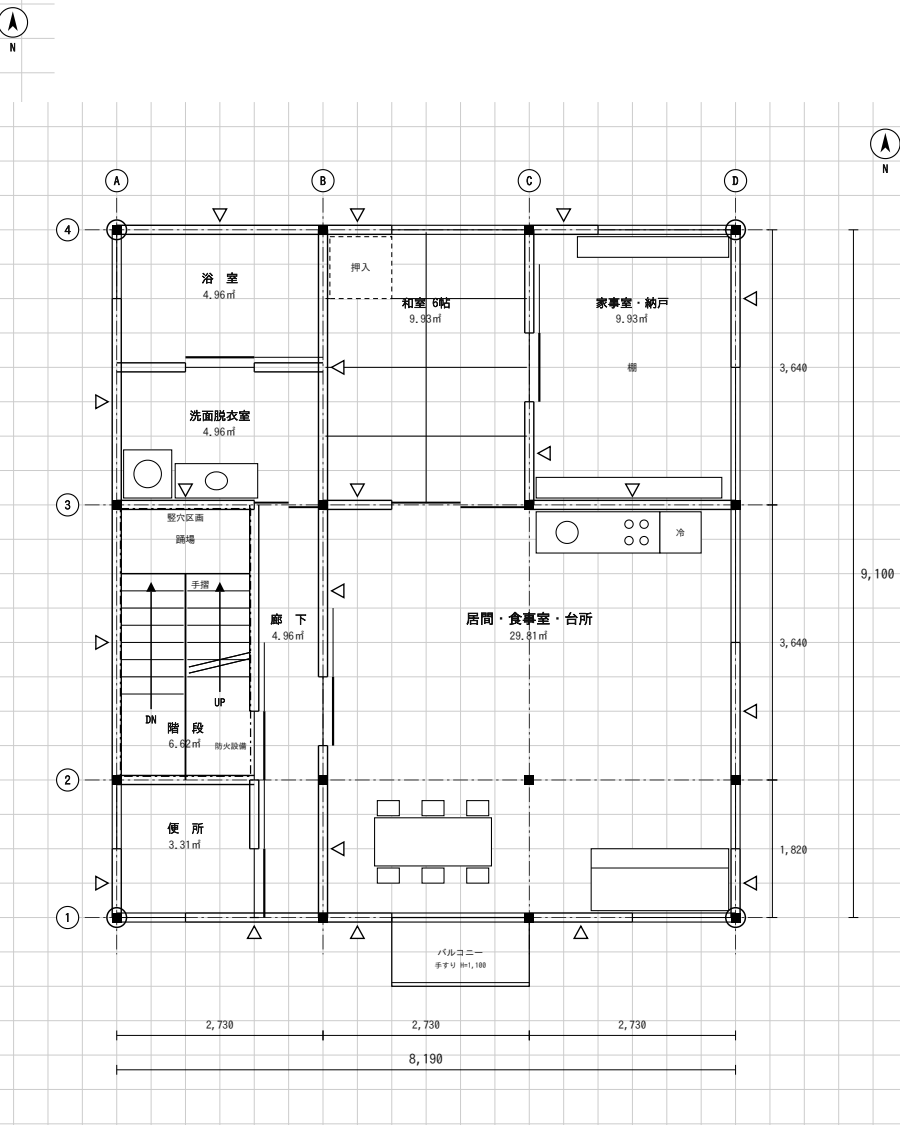


(3) 3階平面図 縮尺1／100 (目盛4.55mm)

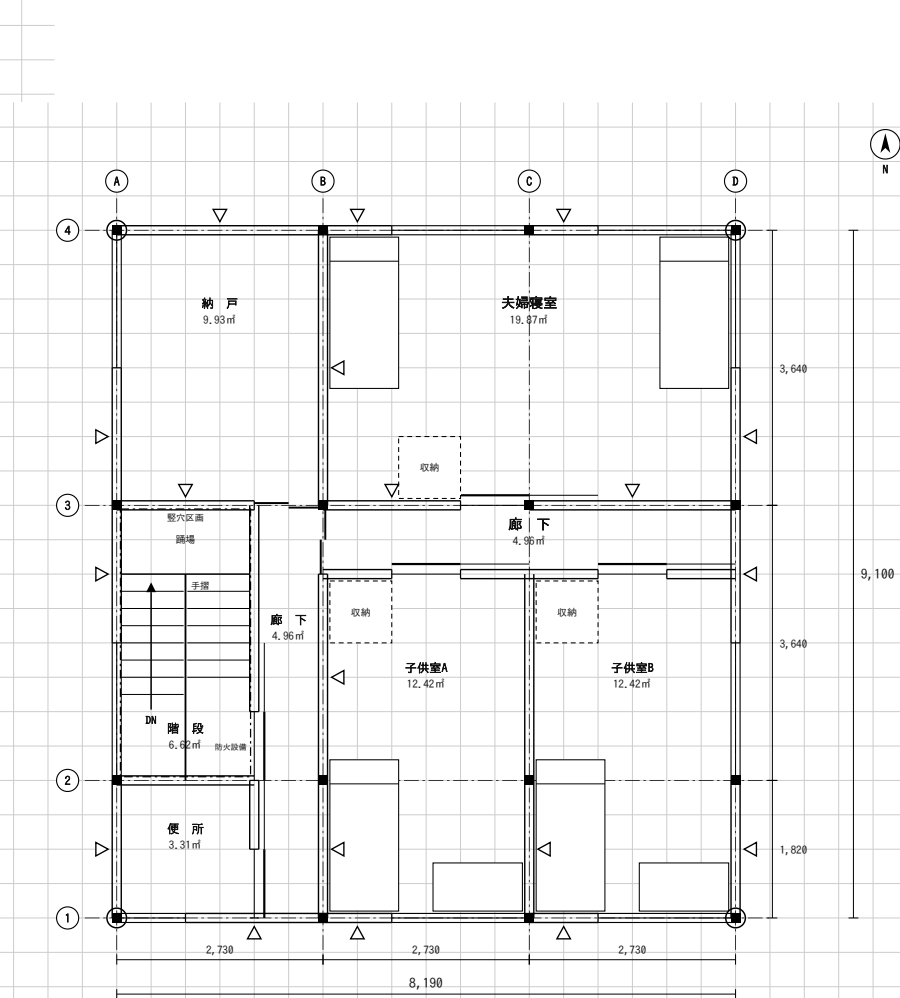

(4) 3階床伏図

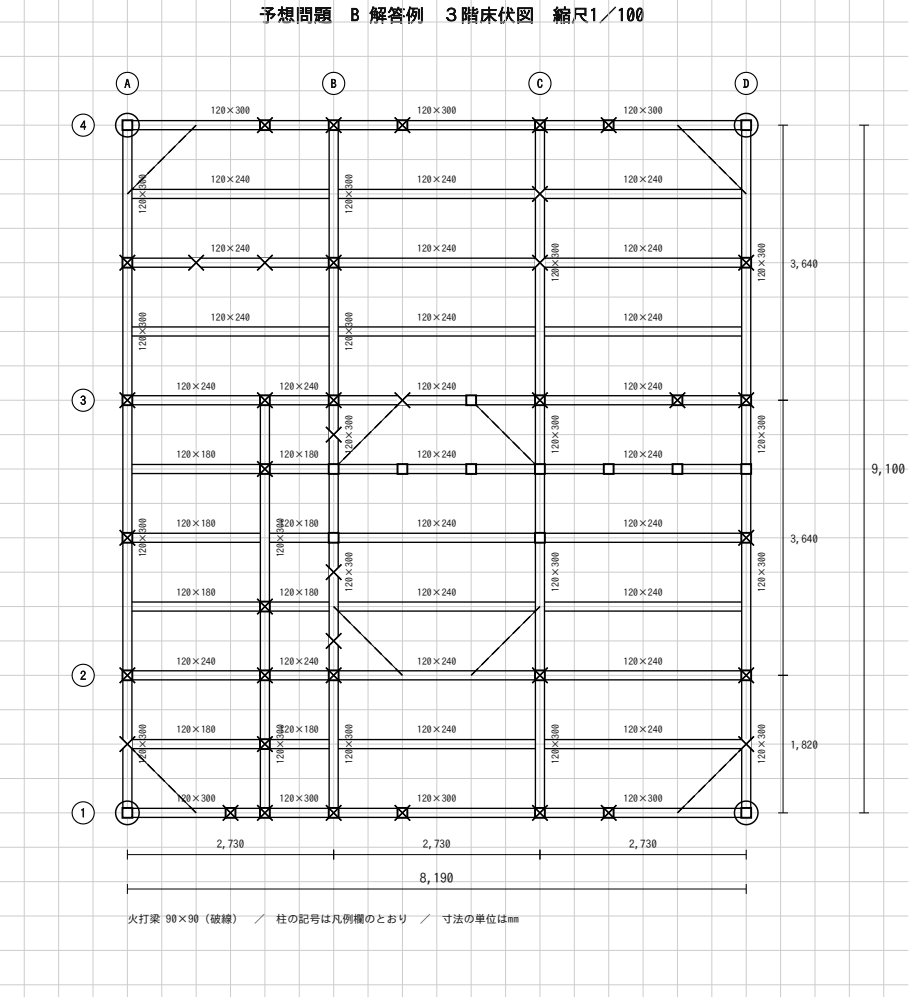

(4) 小屋伏図

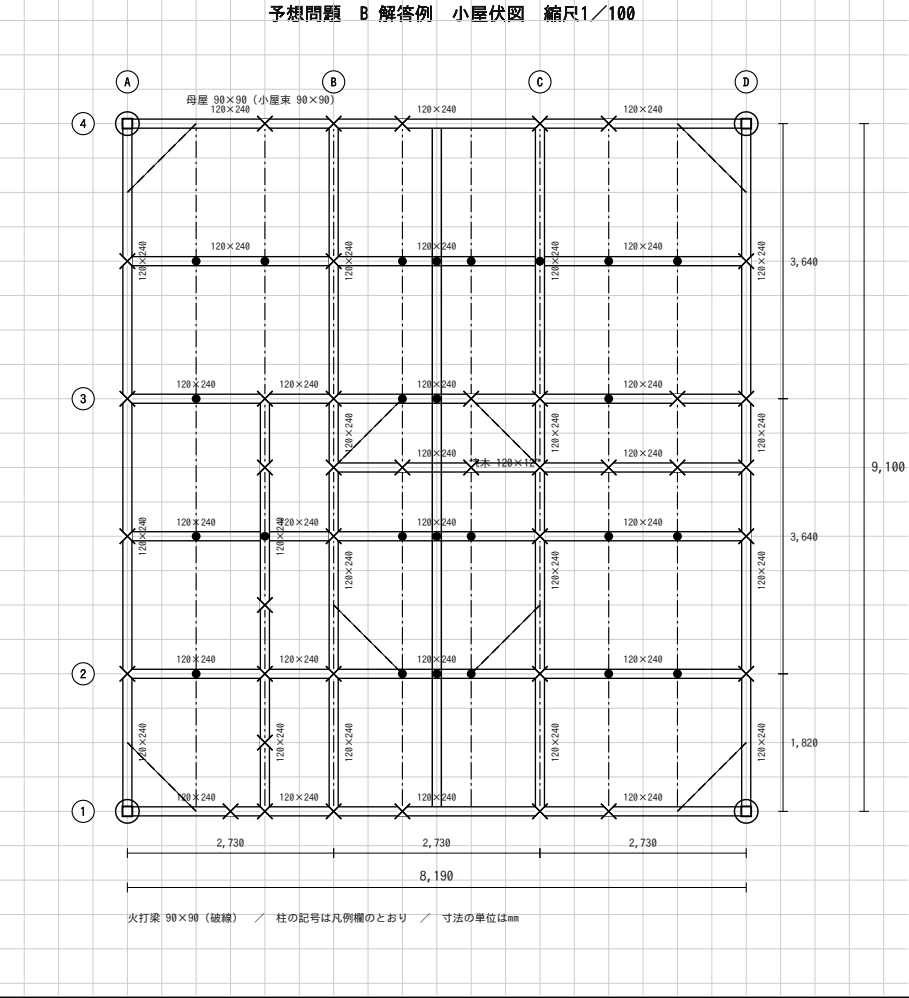

(8) 計画の要点等


① 高齢者の居室を1階に設けたことについて工夫した点

② 店舗部分と住宅部分の動線計画について工夫した点


③ 高齢者の避難について配慮した点

※ 解答例の本文は別紙「計画の要点等」(記述だけ)にて

(6) 部分詳細図 (断面) (目盛10mm)

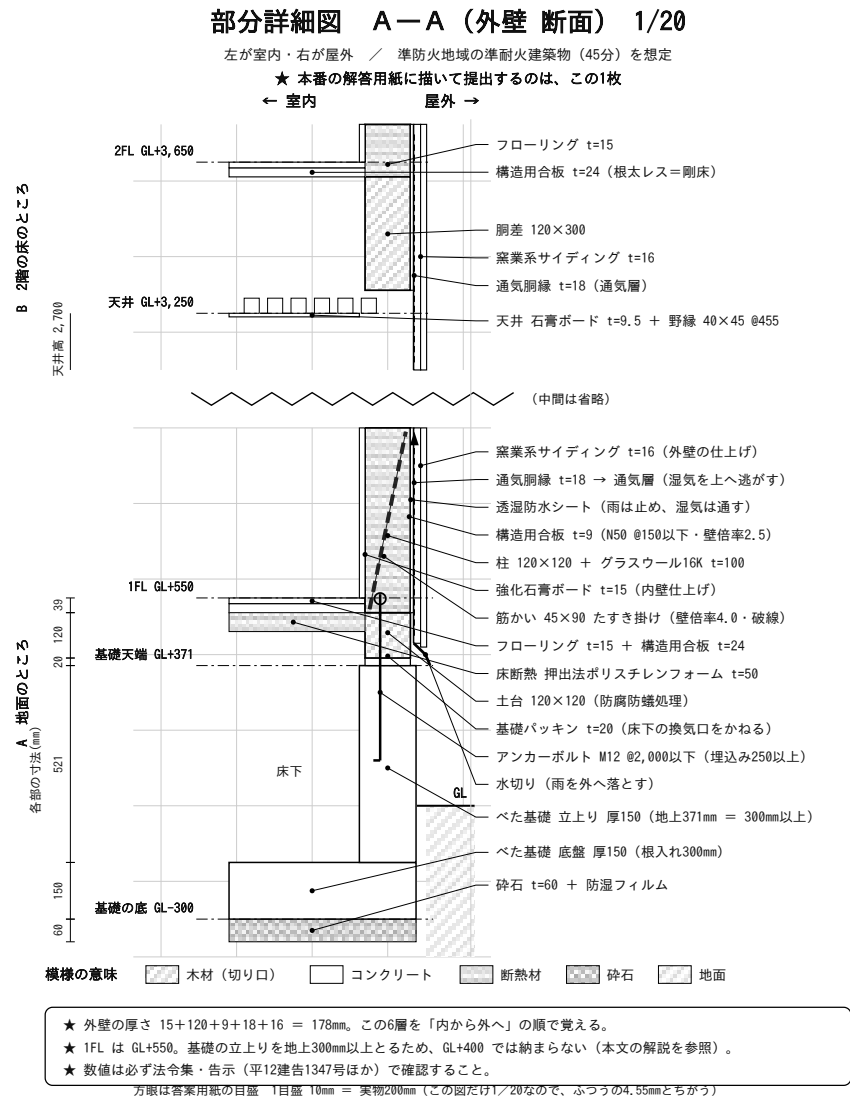

(5) 南側立面図

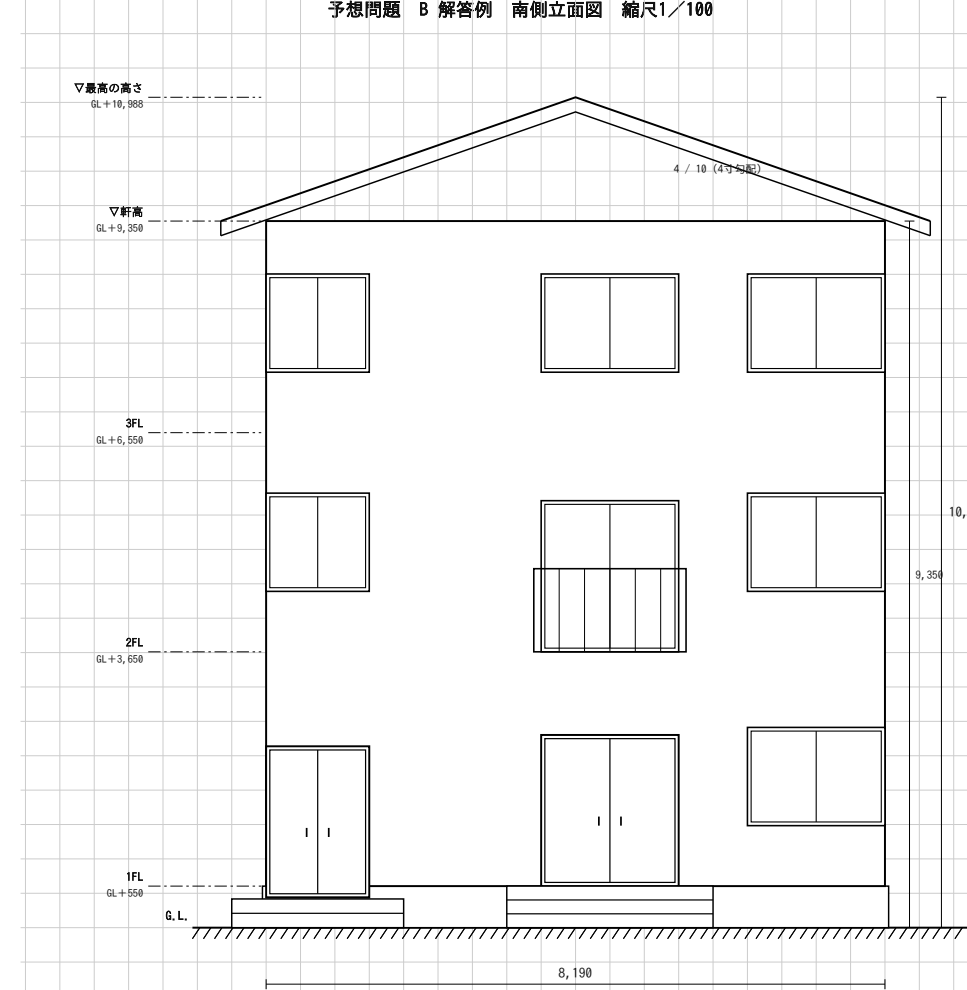

(7) 面積表

|            |                 |         |
|------------|-----------------|---------|
| 敷地面積       |                 | 224.00㎡ |
| 建築面積       | (計算式) 8.19×9.10 | 74.52㎡  |
| 床面積 1階 ア   | (計算式) 8.19×9.10 | 74.52㎡  |
| 2階 イ       | (計算式) 8.19×9.10 | 74.52㎡  |
| 3階 ウ       | (計算式) 8.19×9.10 | 74.52㎡  |
| 延べ面積 ア+イ+ウ |                 | 223.56㎡ |

※ 小数点以下第3位以下は切り捨て。計算式はm単位。

凡 例 (床伏図兼小屋伏図の表示記号)

| 記号 | 通し柱     | 1階の管柱   | 2階の管柱   | 重なる管柱 差・桁 (正角材) | 同上 (平角材) | 同上 (丸太材) | 火打梁   | 棟木    | 母屋・小屋束        |
|----|---------|---------|---------|-----------------|----------|----------|-------|-------|---------------|
| 寸法 | 120×120 | 120×120 | 120×120 | —               | 120×120  | 図中に記入    | 図中に記入 | 90×90 | 120×120 90×90 |

※ 平角材 (120×240 など) の断面寸法は、床伏図の中の梁1本ずつのわきに記入する。


標準解答例

受験番号 氏名


予想問題 B 母と暮らす併用住宅 (和菓子店)

木造3階建て / 9マス × 10マス (8,190 × 9,100)


(1) 1階平面図 兼 配置図 縮尺1／100 (目盛4.55mm)

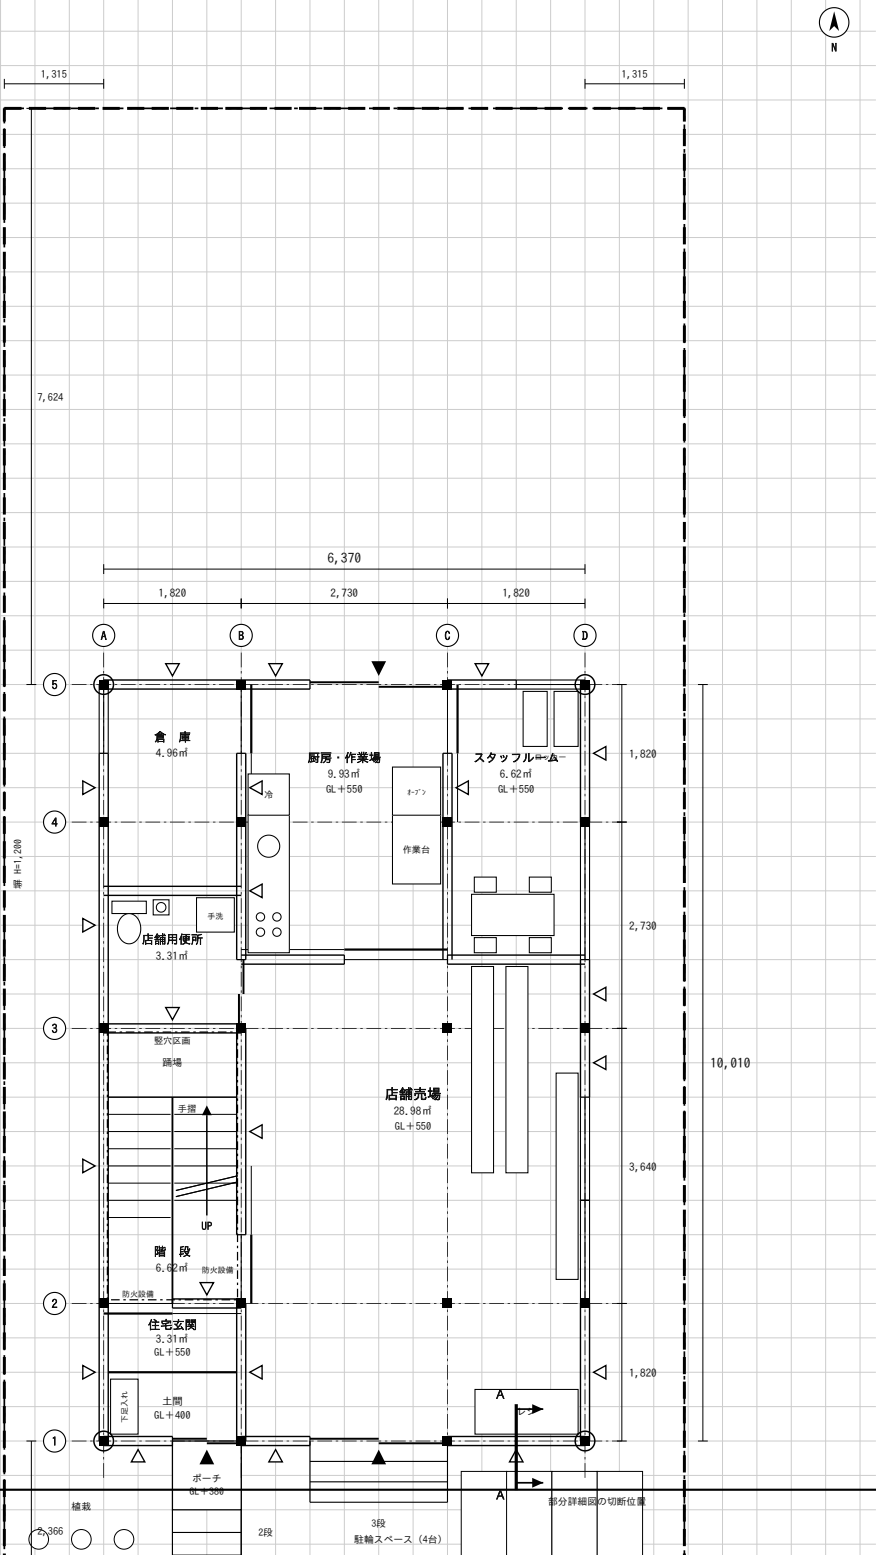


(5) 南側立面図

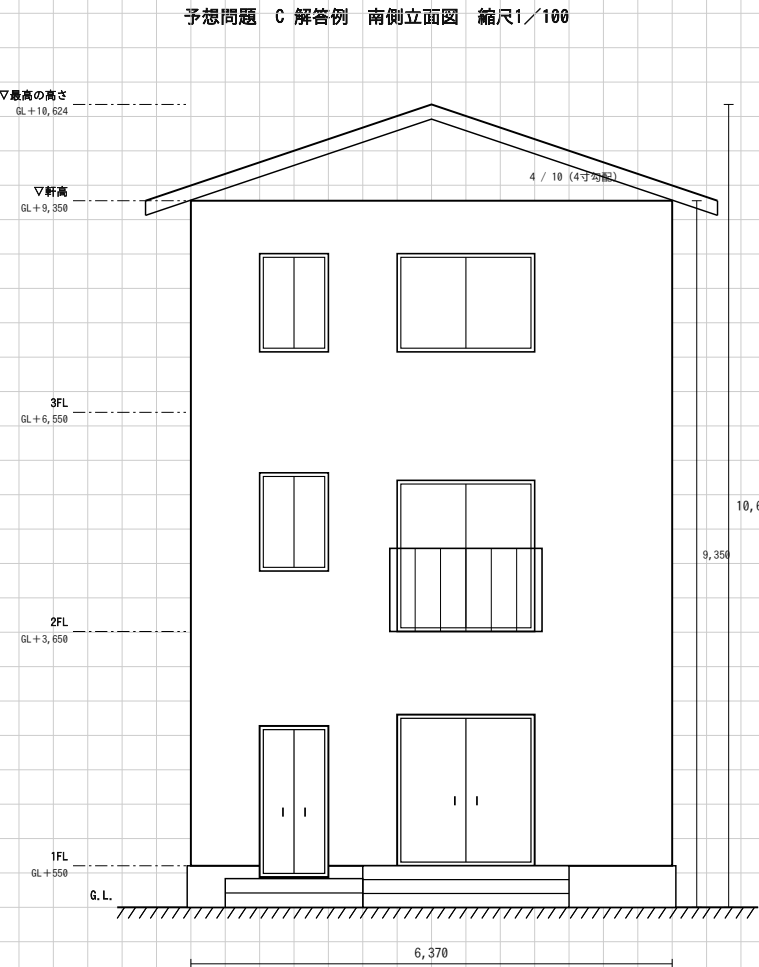


(2) 2階平面図 縮尺1／100 (目盛4.55mm)

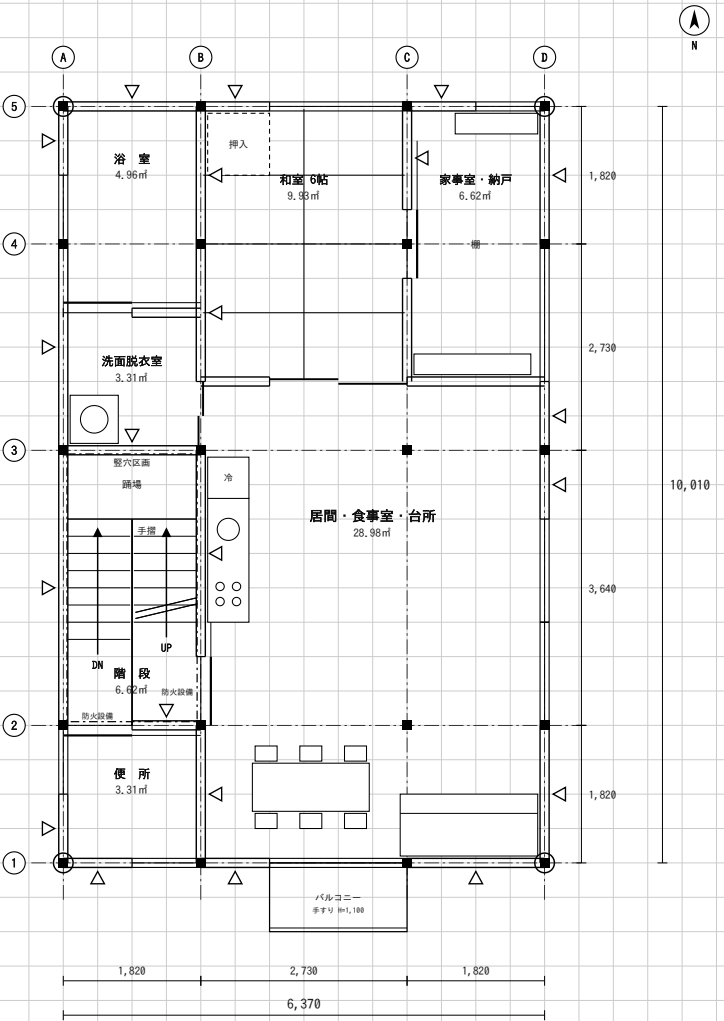


(3) 3階平面図 縮尺1／100 (目盛4.55mm)

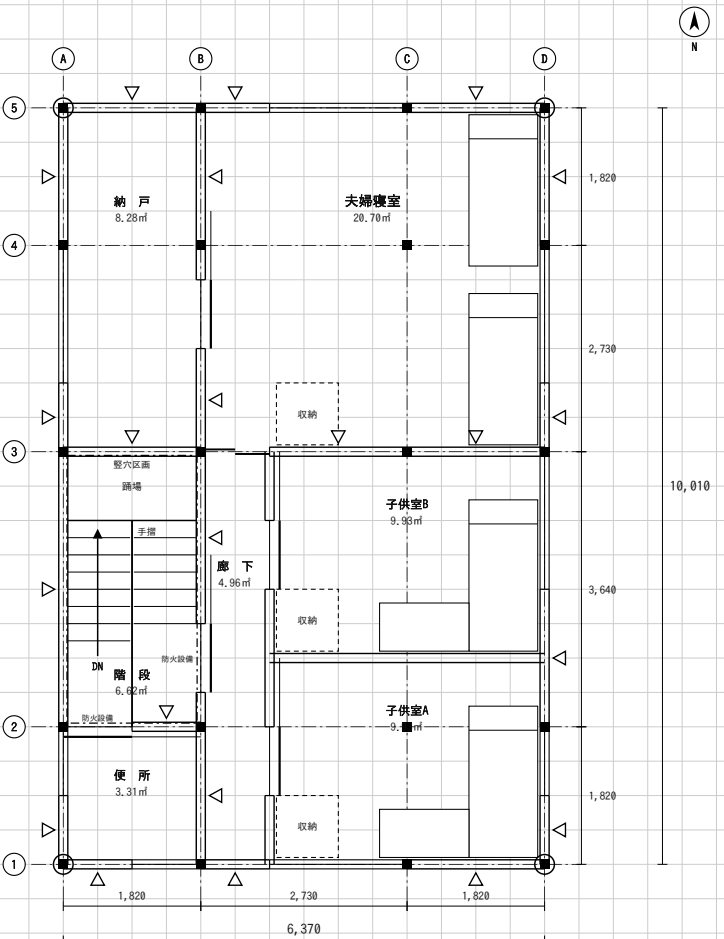

(4) 3階床伏図

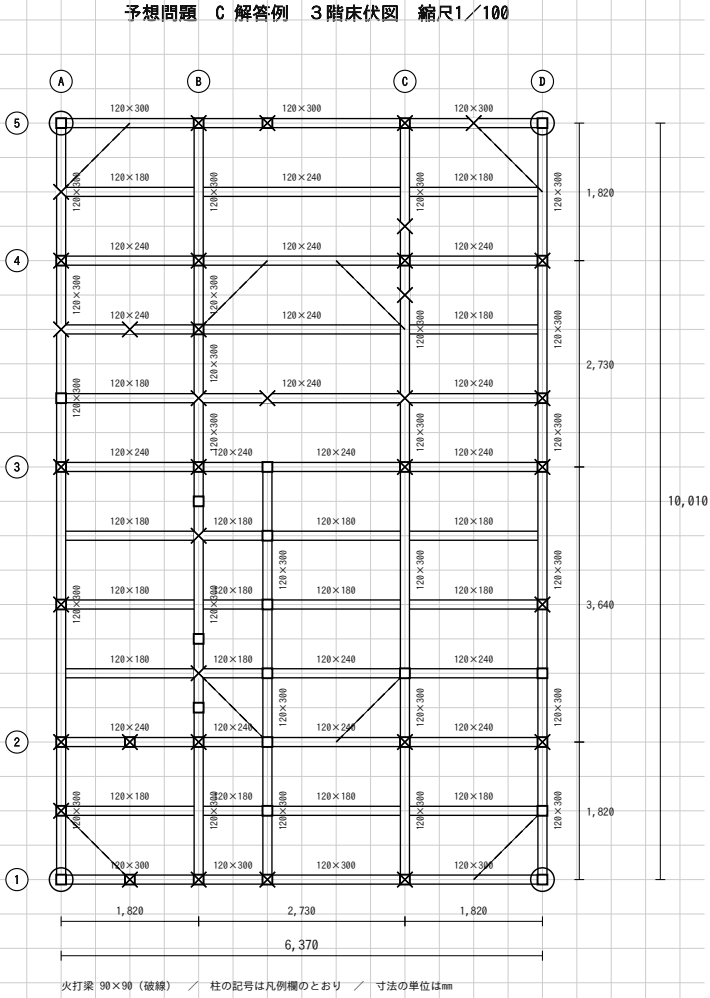


(4) 小屋伏図

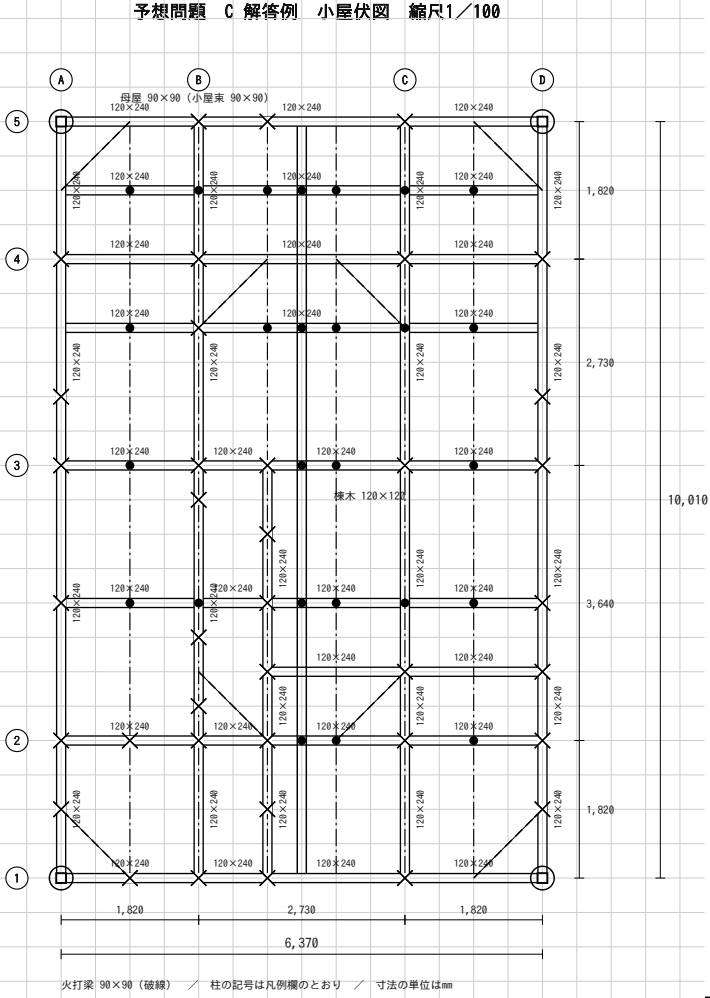

(8) 計画の要点等

- ① 間口が狭い敷地に対して、平面計画上工夫した点
- ② 奥行きの深い店舗売場の採光及び通風について工夫した点
- ③ 木造3階建てとするに当たり、構造計画上工夫した点

(6) 部分詳細図 (断面) (目盛10mm)

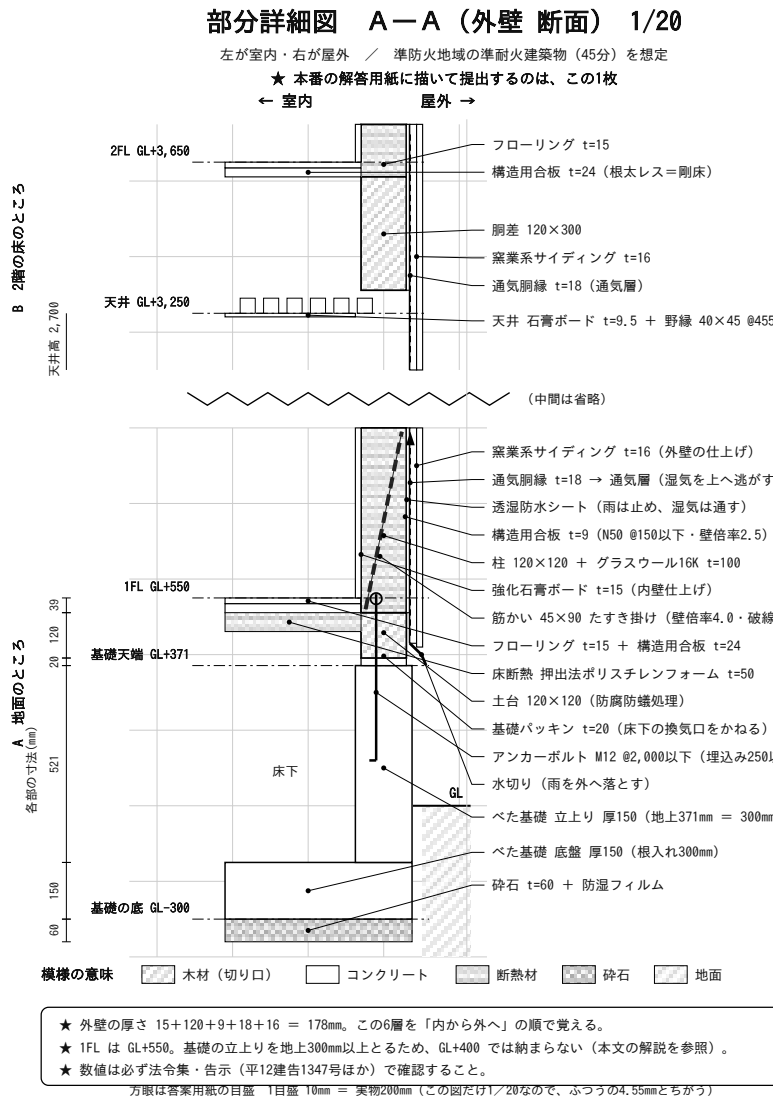

(7) 面積表

|            |                  |          |
|------------|------------------|----------|
| 敷地面積       |                  | 180.00 ㎡ |
| 建築面積       | (計算式) 6.37×10.01 | 63.76 ㎡  |
| 床面積 1階 ア   | (計算式) 6.37×10.01 | 63.76 ㎡  |
| 2階 イ       | (計算式) 6.37×10.01 | 63.76 ㎡  |
| 3階 ウ       | (計算式) 6.37×10.01 | 63.76 ㎡  |
| 延べ面積 ア+イ+ウ |                  | 191.28 ㎡ |

※ 小数点以下第3位以下は切り捨て。計算式はm単位。

凡 例 (床伏図兼小屋伏図の表示記号)

| 通し柱 | 1階の管柱   | 2階の管柱   | 重なる管柱 胴差・桁 (正角材) | 同上 (平角材) | 同上 (丸太材) | 火打梁   | 棟木    | 母屋・小屋束 |
|-----|---------|---------|------------------|----------|----------|-------|-------|--------|
|     |         |         |                  |          |          |       |       |        |
| 記号  |         |         |                  |          |          |       |       |        |
| 寸法  | 120×120 | 120×120 | 120×120          | —        | 120×120  | 図中に記入 | 図中に記入 | 90×90  |

※ 平角材 (120×240 など) の断面寸法は、床伏図の中の梁1本ずつのわきに記入する。

標準解答例

受験番号


氏名

予想問題 C 間口の狭い敷地の併用住宅 (喫茶店)


木造3階建て / 7マス × 11マス (6,370 × 10,010)




(1) 1階平面図 兼 配置図 縮尺1/100 (目盛4.55mm)

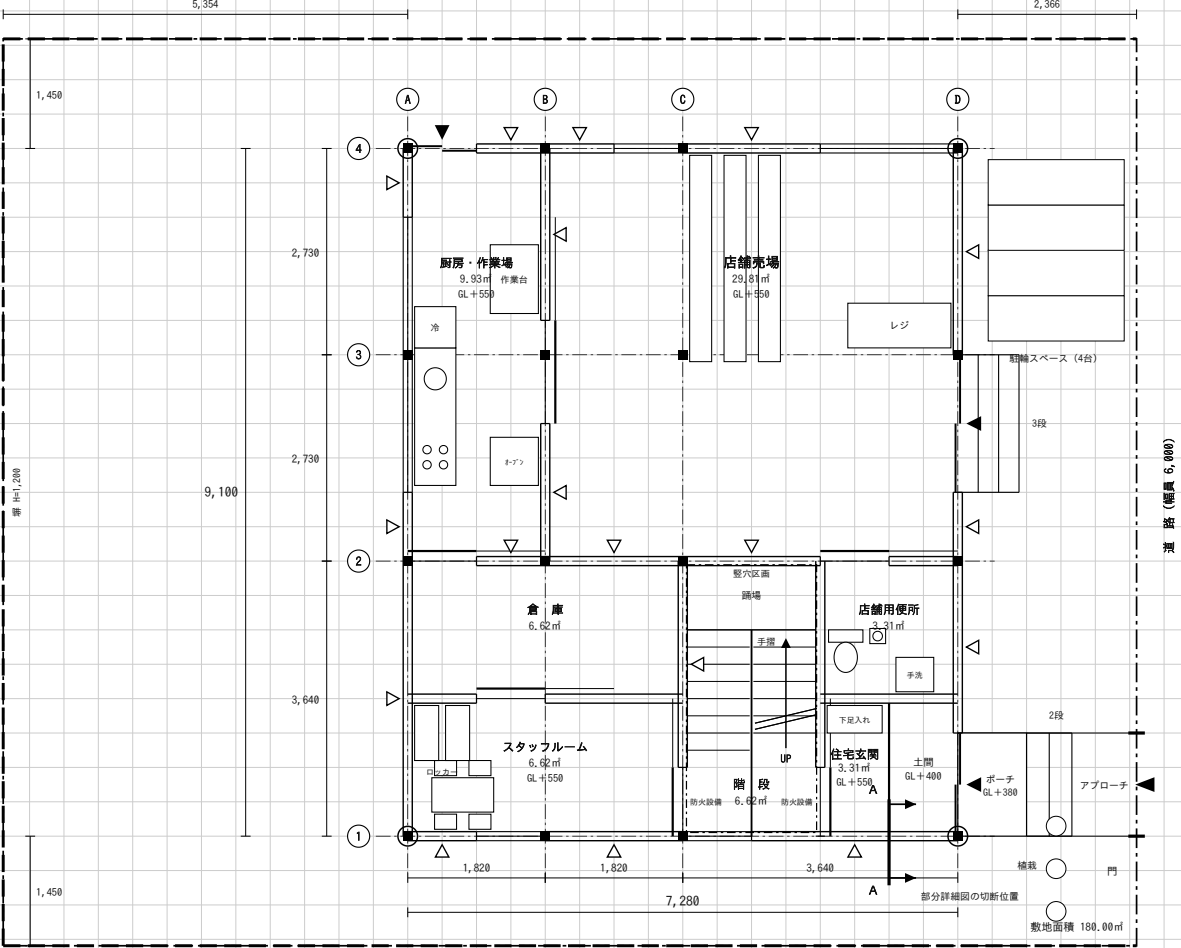


(2) 2階平面図 縮尺1/100 (目盛4.55mm)

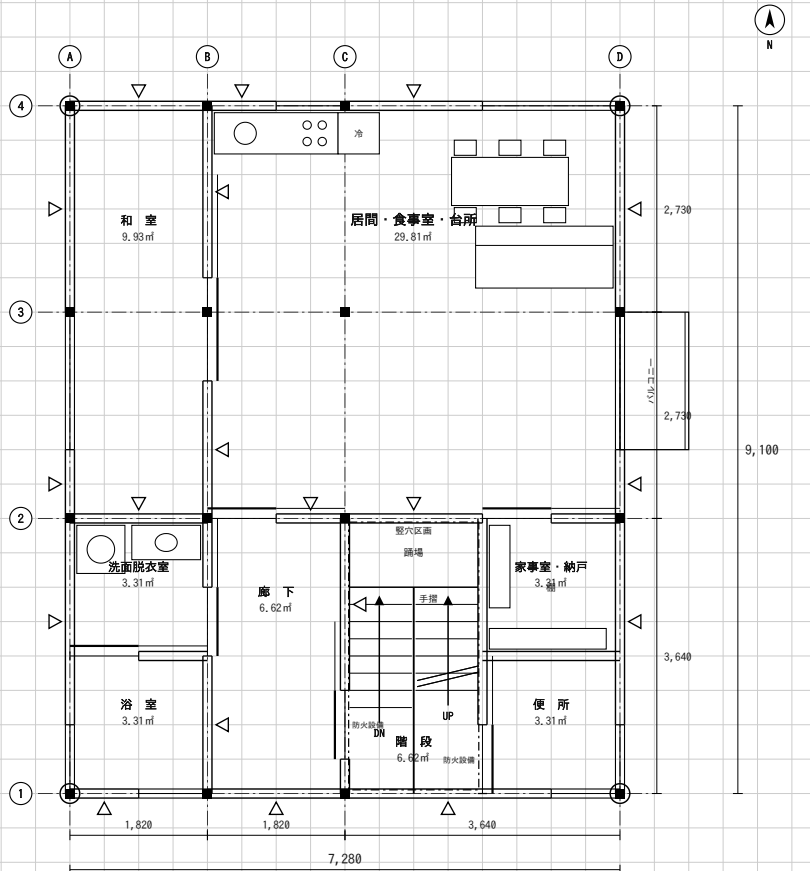


(3) 3階平面図 縮尺1/100 (目盛4.55mm)

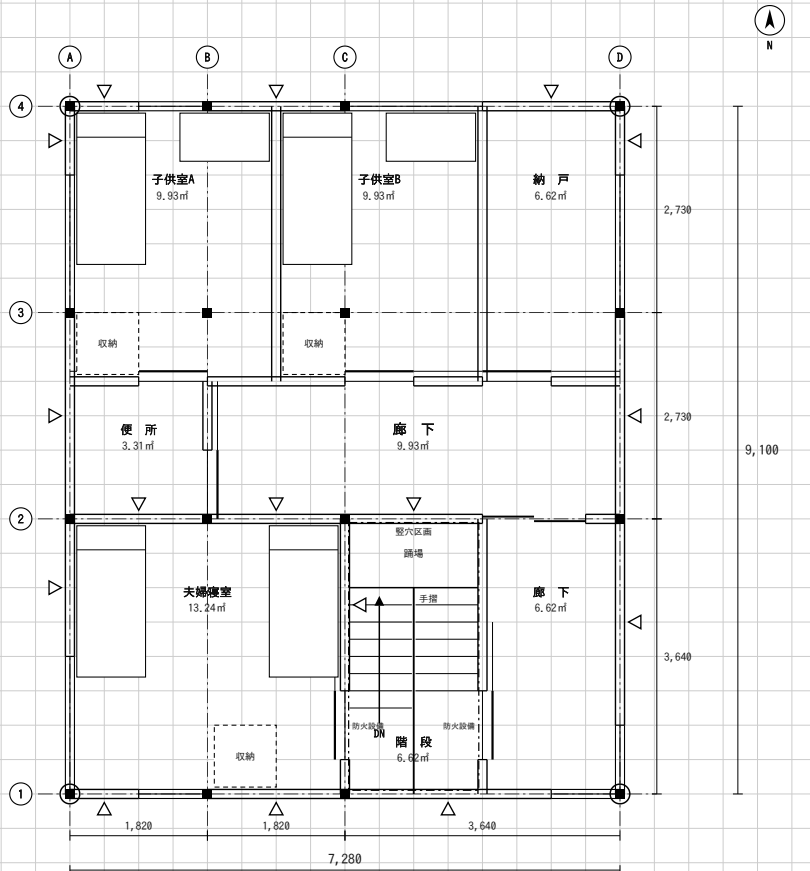


(4) 3階床伏図

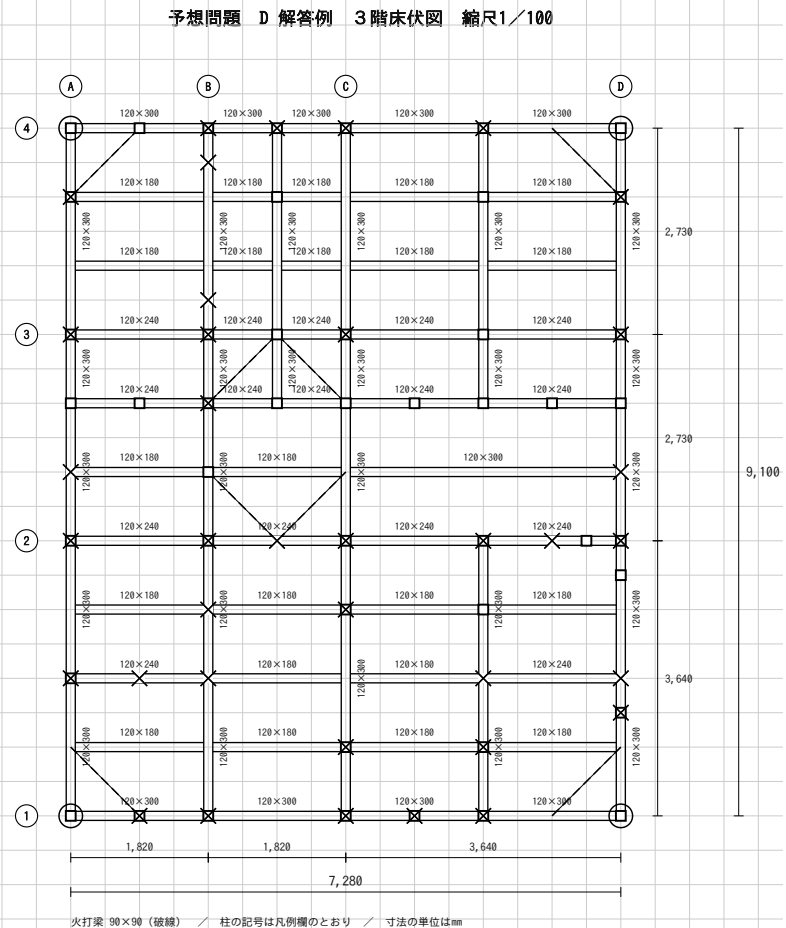

(4) 小屋伏図

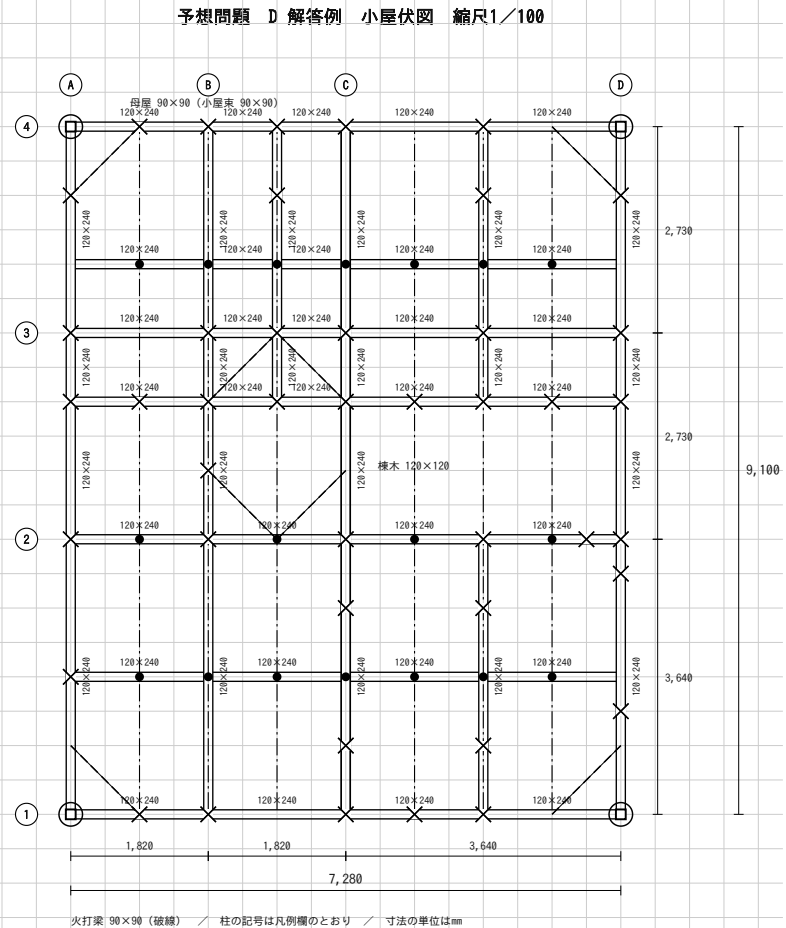


(6) 部分詳細図 (断面) (目盛10mm)

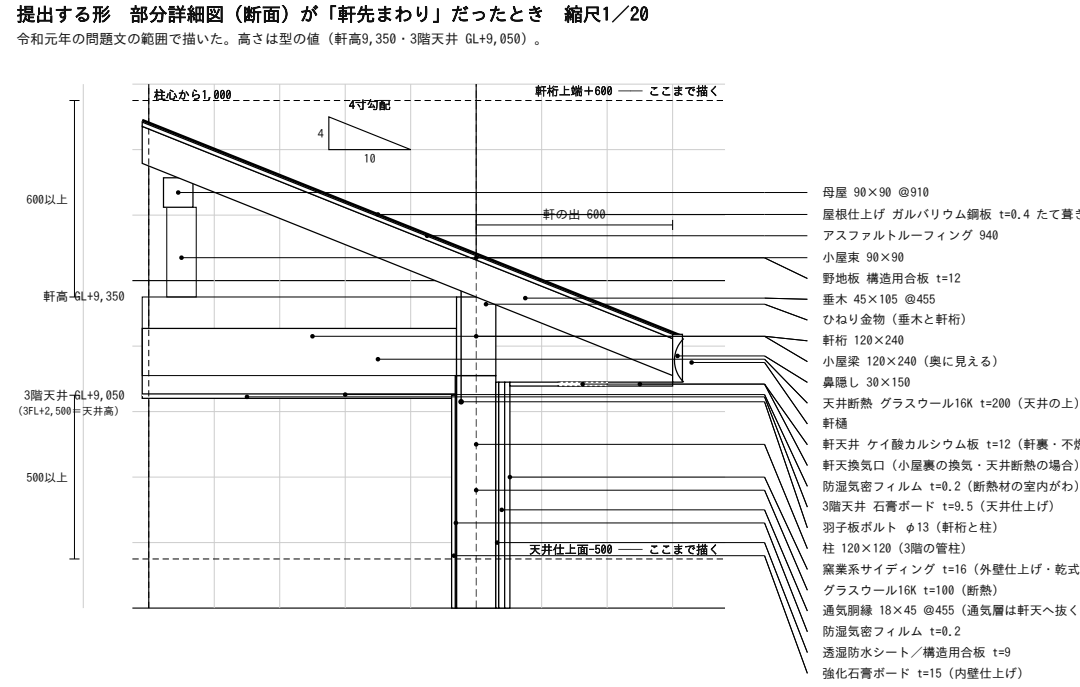

★ 令和元年の要求：屋根の勾配／主要部の寸法／軒桁・小屋梁・母屋・墨木の名称と断面寸法／羽子板ボルト等の金物／  
屋根 (天井) と外壁の断熱・防湿・外壁・内壁・天井の仕上材料名／外壁は乾式工法。  
★ 高梁・土台・1階の床は出てこない。かわりに屋根の裏 (墨木→野地板→ルーフィング→仕上げ) を4つ順に書く。

(5) 東側立面図

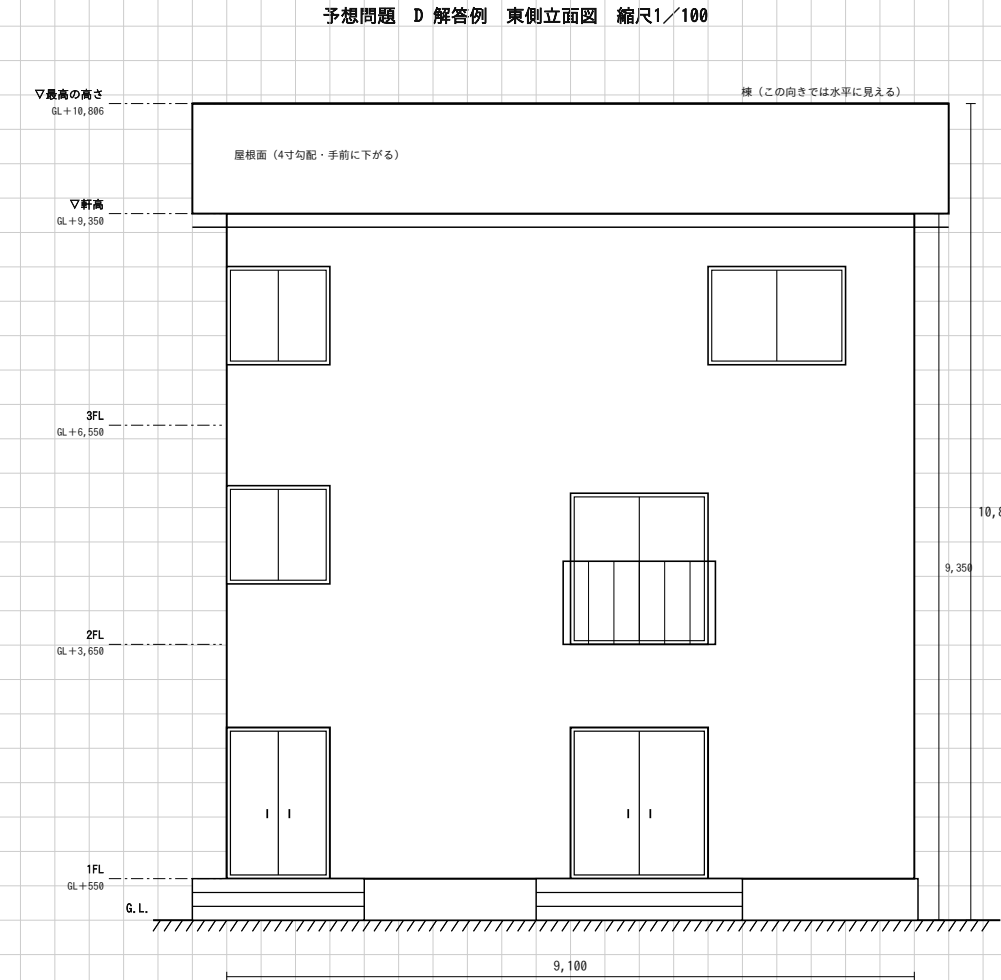

(8) 計画の要点等

- ① 東側道路に対して、平面計画上工夫した点
- ② 階段の位置と直下率について工夫した点
- ③ 店舗部分と住宅部分の動線計画について工夫した点

(7) 面積表

|            |                 |         |
|------------|-----------------|---------|
| 敷地面積       |                 | 180.00㎡ |
| 建築面積       | (計算式) 7.28×9.10 | 66.24㎡  |
| 床面積 1階 ア   | (計算式) 7.28×9.10 | 66.24㎡  |
| 2階 イ       | (計算式) 7.28×9.10 | 66.24㎡  |
| 3階 ウ       | (計算式) 7.28×9.10 | 66.24㎡  |
| 延べ面積 ア+イ+ウ |                 | 198.72㎡ |

※ 小数点以下第3位以下は切り捨て。計算式はm単位。

凡 例 (床伏図兼小屋伏図の表示記号)

| 記号 | 通し柱     | 1階の管柱   | 2階の管柱   | 重なる管柱 | 差・桁 (正角材) | 同上 (平角材) | 同上 (丸太材) | 火打梁   | 棟木      | 母屋・小屋束 |
|----|---------|---------|---------|-------|-----------|----------|----------|-------|---------|--------|
| 寸法 | 120×120 | 120×120 | 120×120 | —     | 120×120   | 図中に記入    | 図中に記入    | 90×90 | 120×120 | 90×90  |

※ 平角材 (120×240 など) の断面寸法は、床伏図の中の梁1本ずつのわきに記入する。


標準解答例

受験番号 氏名


予想問題 D 東側道路の併用住宅 (美容室)

木造3階建て / 8マス × 10マス (7,280 × 9,100)


(1) 1階平面図 兼 配置図 縮尺1／100 (目盛4.55mm)

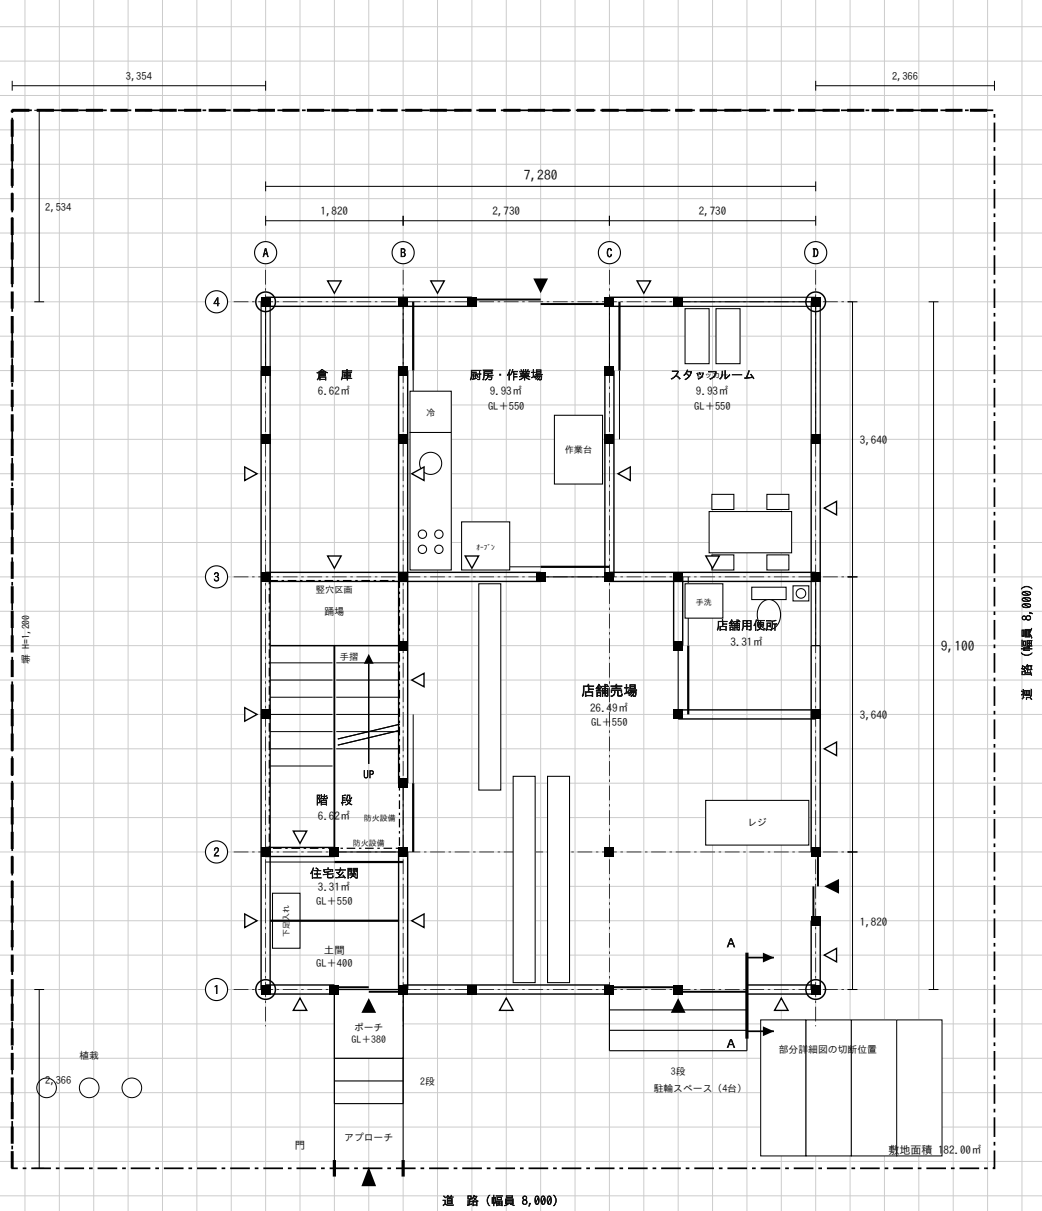


(2) 2階平面図 縮尺1／100 (目盛4.55mm)

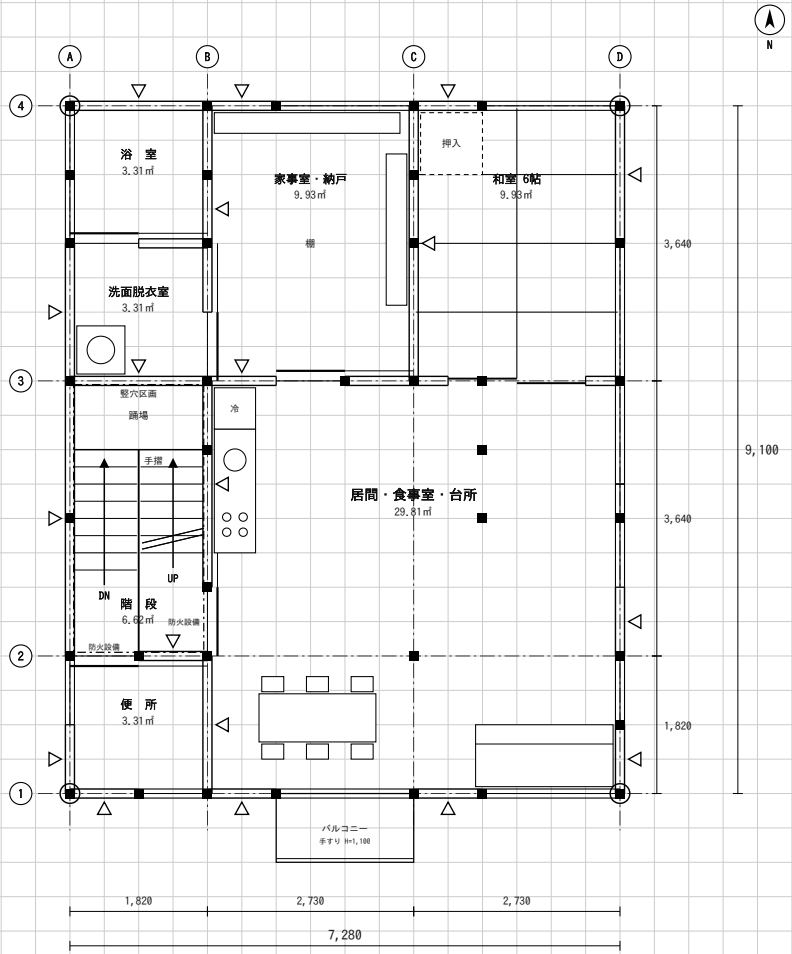


(4) 3階床伏図

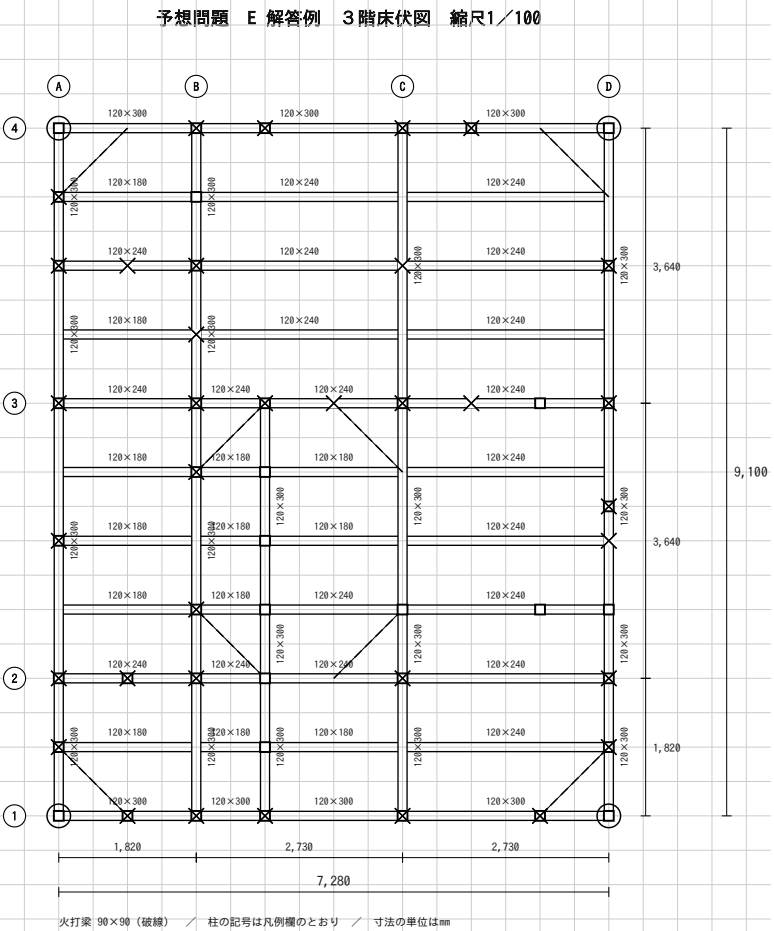


(6) 部分詳細図 (断面) (目盛10mm)

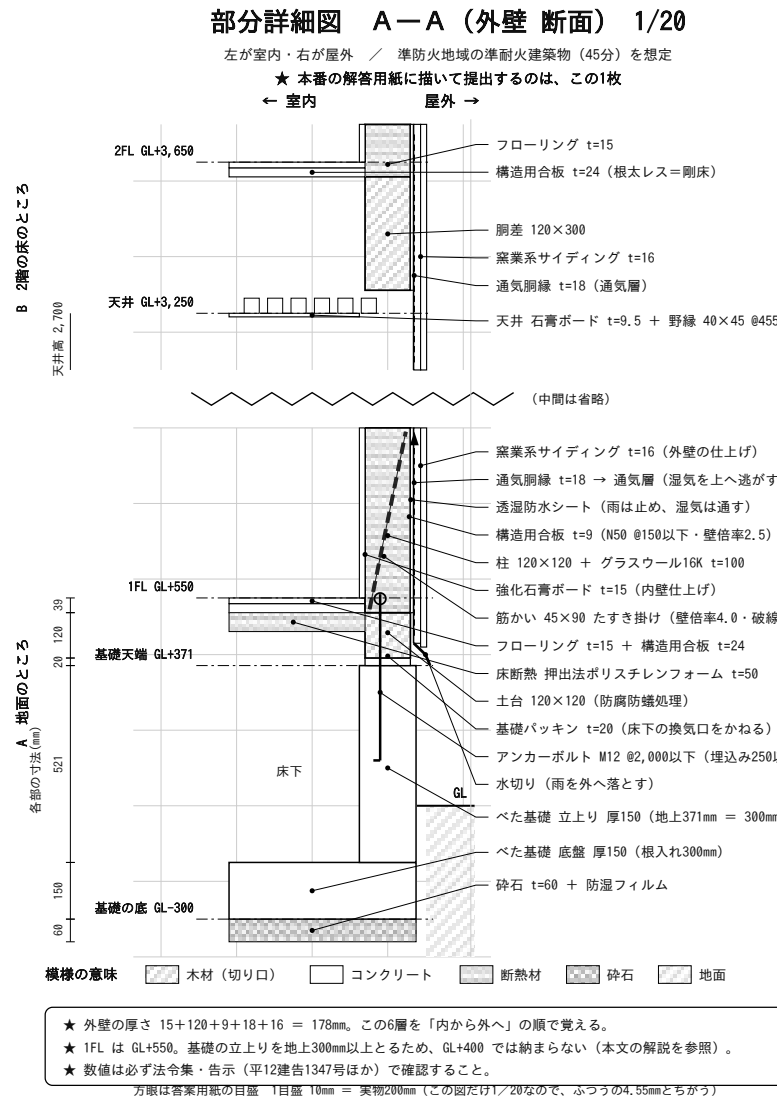


(5) 南側立面図

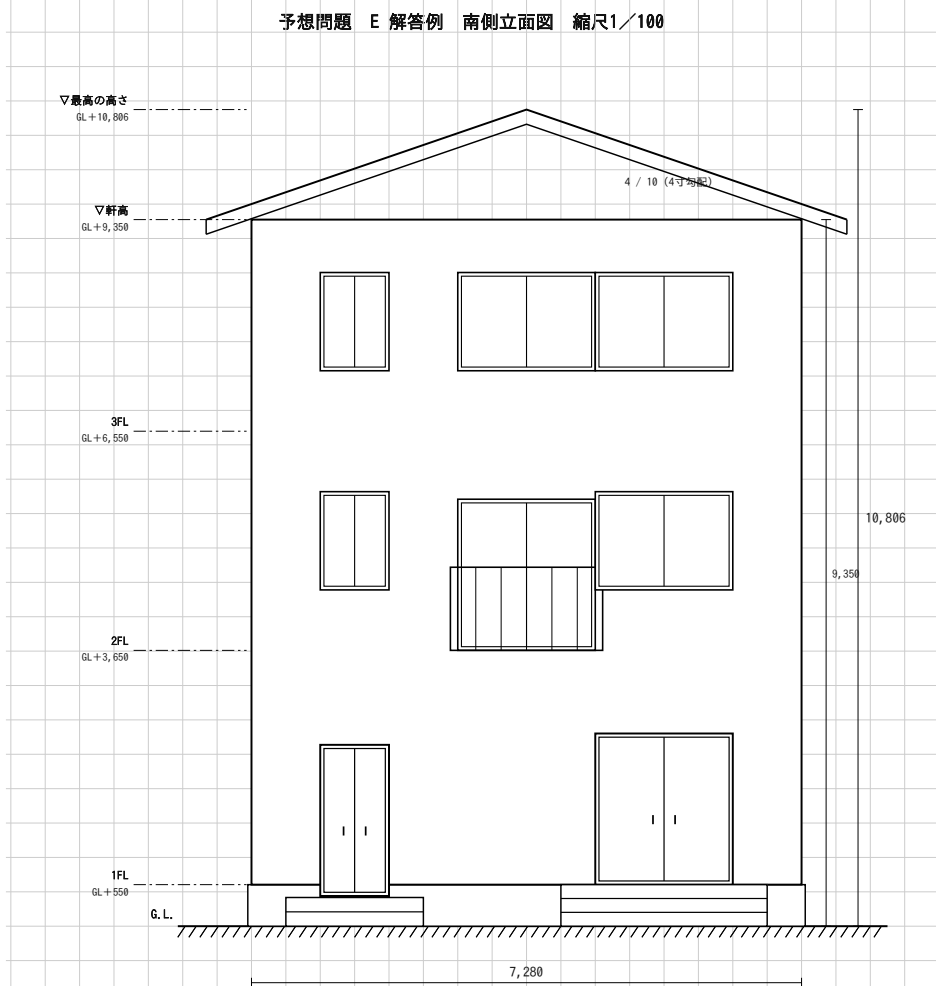

(3) 3階平面図 縮尺1／100 (目盛4.55mm)

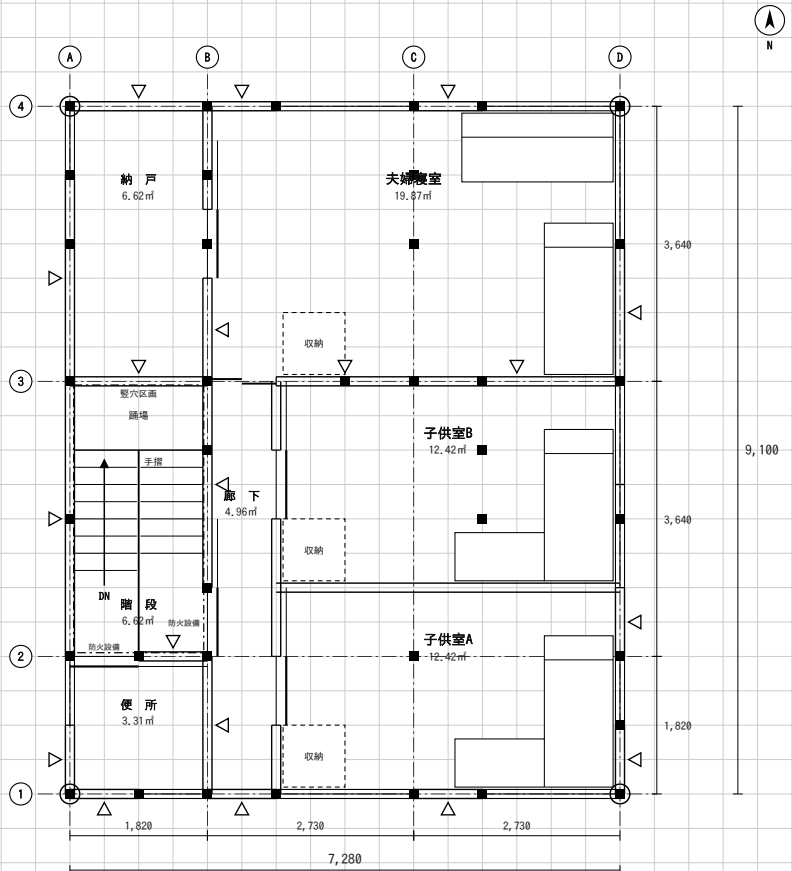

(4) 小屋伏図

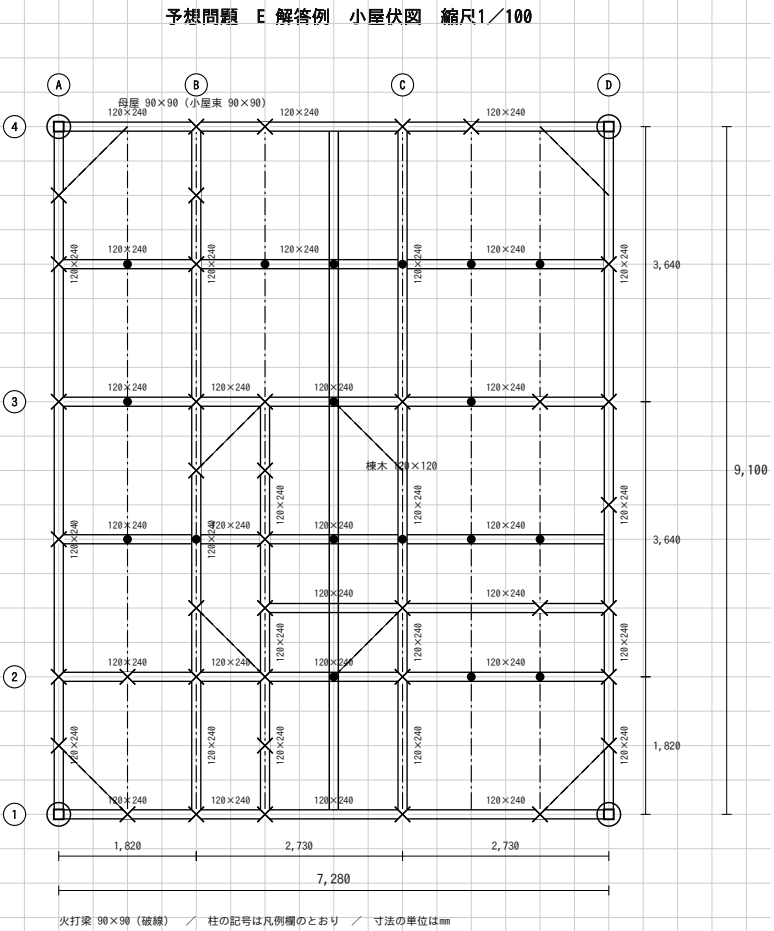

(8) 計画の要点等

- ① 角地であることを活かして工夫した点
- ② 容積率及び建蔽率の算定について
- ③ 防火及び避難について配慮した点

(7) 面積表

|            |                 |          |
|------------|-----------------|----------|
| 敷地面積       |                 | 182.00 ㎡ |
| 建築面積       | (計算式) 7.28×9.10 | 66.24 ㎡  |
| 床面積 1階 ア   | (計算式) 7.28×9.10 | 66.24 ㎡  |
| 2階 イ       | (計算式) 7.28×9.10 | 66.24 ㎡  |
| 3階 ウ       | (計算式) 7.28×9.10 | 66.24 ㎡  |
| 延べ面積 ア+イ+ウ |                 | 198.72 ㎡ |

※ 小数点以下第3位以下は切り捨て。計算式はm単位。

凡 例 (床伏図兼小屋伏図の表示記号)

| 通し柱 | 1階の管柱   | 2階の管柱   | 重なる管柱 胴差・桁 (正角材) | 同上 (平角材) | 同上 (丸太材) | 火打梁   | 棟木    | 母屋・小屋束 |
|-----|---------|---------|------------------|----------|----------|-------|-------|--------|
| 記号  |         |         |                  |          |          |       |       |        |
| 寸法  | 120×120 | 120×120 | 120×120          | —        | 120×120  | 図中に記入 | 図中に記入 | 90×90  |

※ 平角材 (120×240 など) の断面寸法は、床伏図の中の梁1本ずつのわきに記入する。

## 標準解答例


受験番号

氏名


予想問題 E 南東の角地に建つ併用住宅 (パン店)

木造3階建て / 8マス × 10マス (7,280 × 9,100)


(1) 1階平面図 兼 配置図 縮尺1／100 (目盛4.55mm)

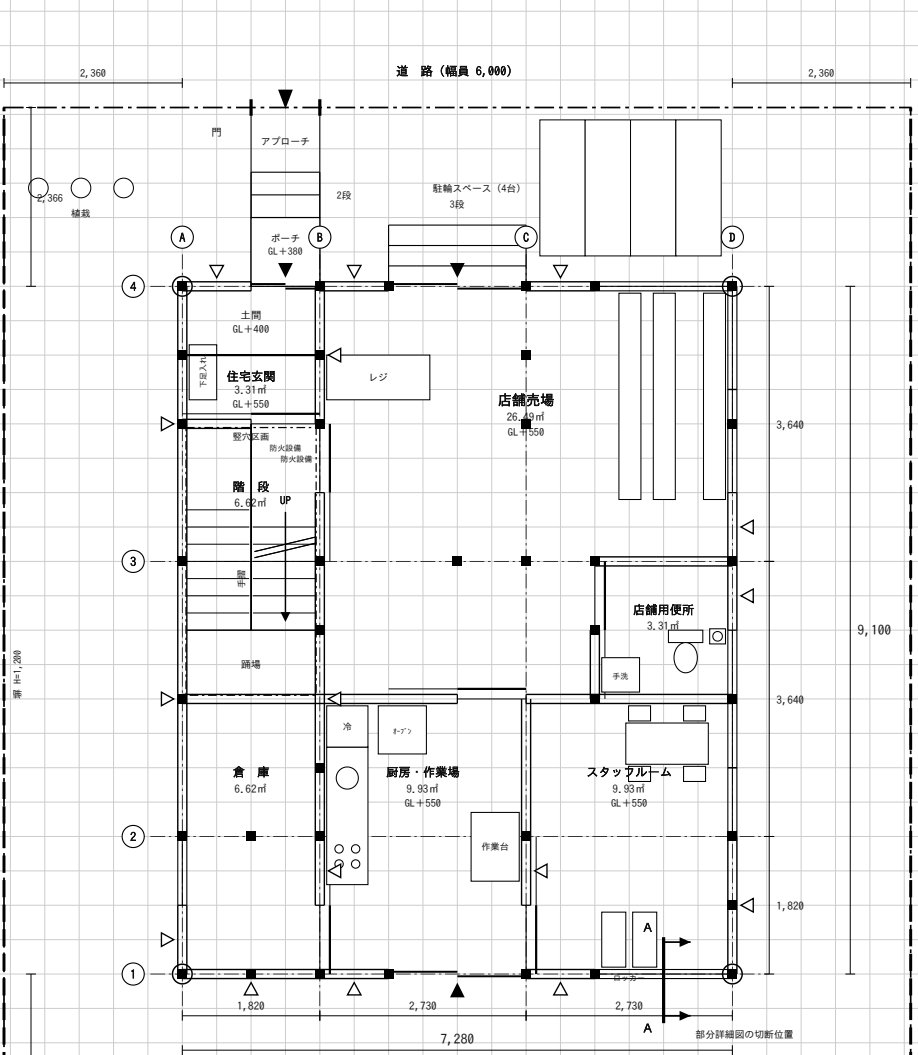


(5) 北側立面図

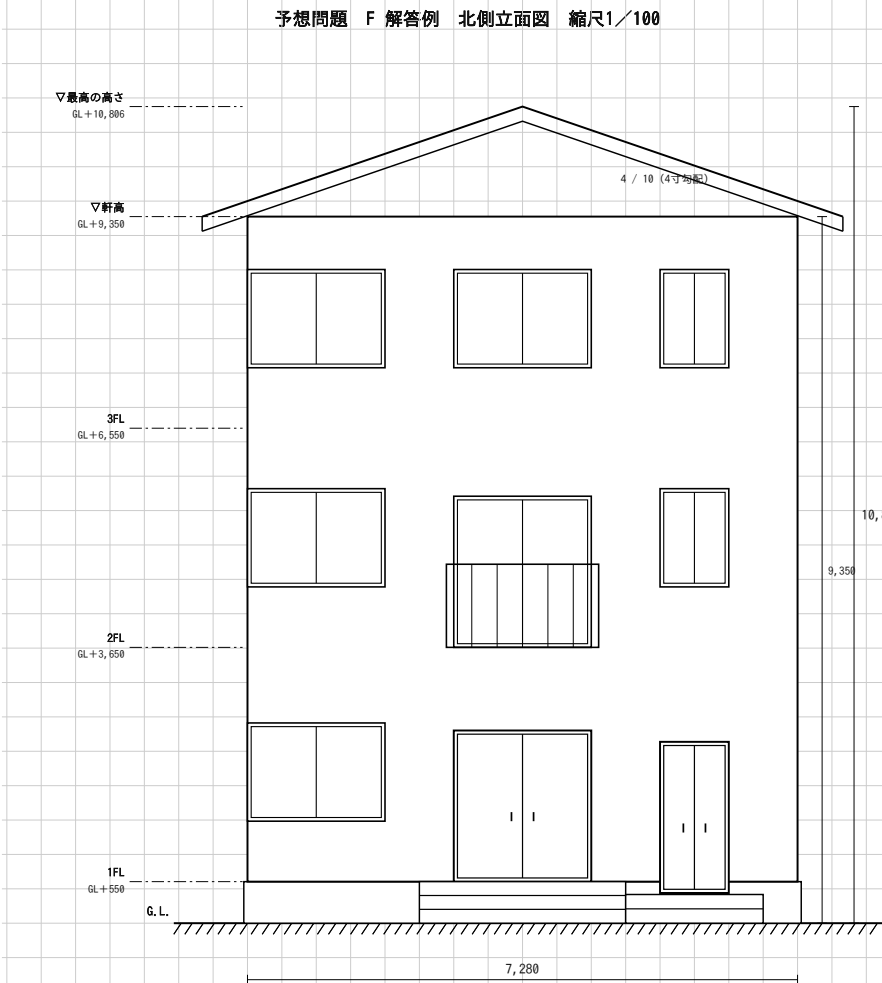


(2) 2階平面図 縮尺1／100 (目盛4.55mm)

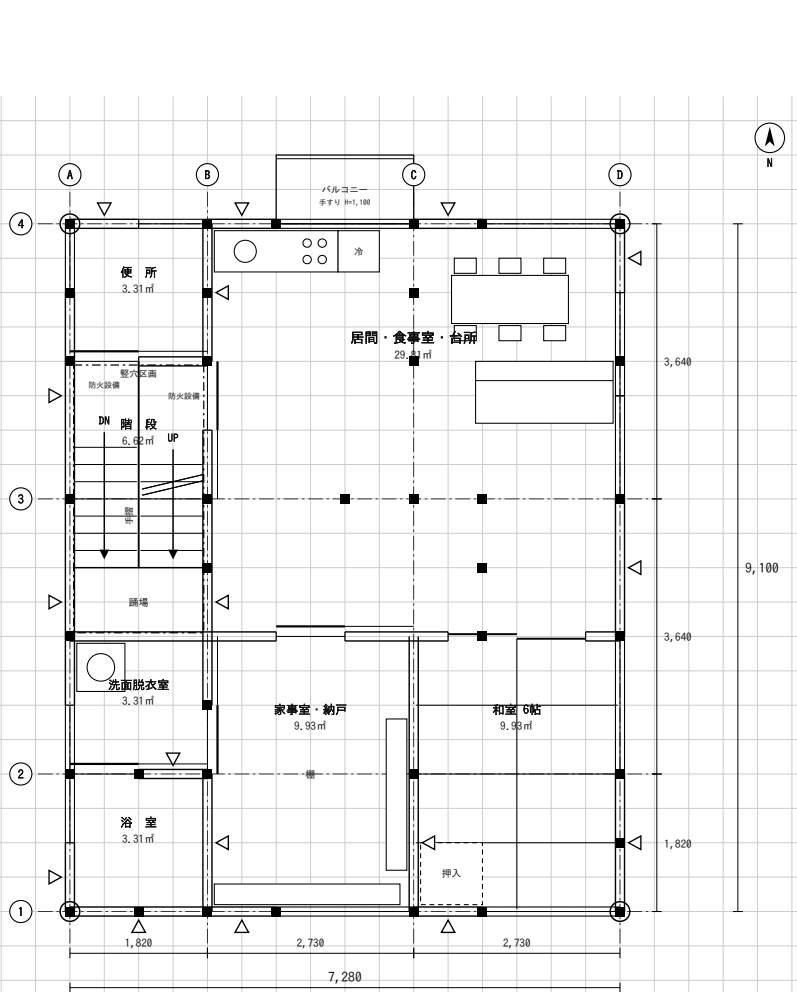


(3) 3階平面図 縮尺1／100 (目盛4.55mm)

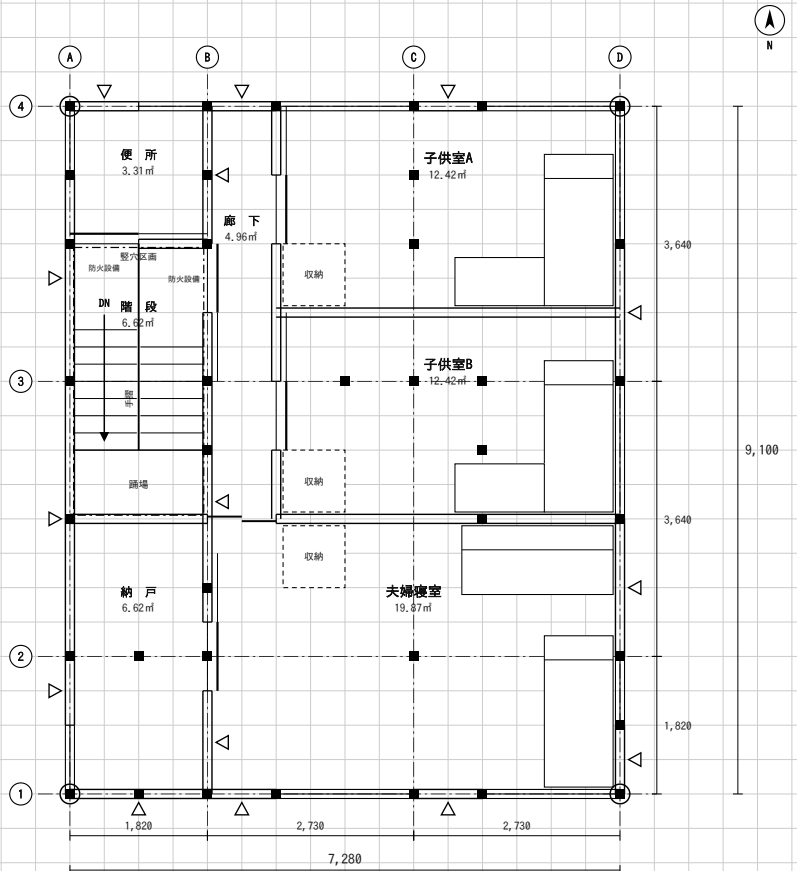

(4) 3階床伏図

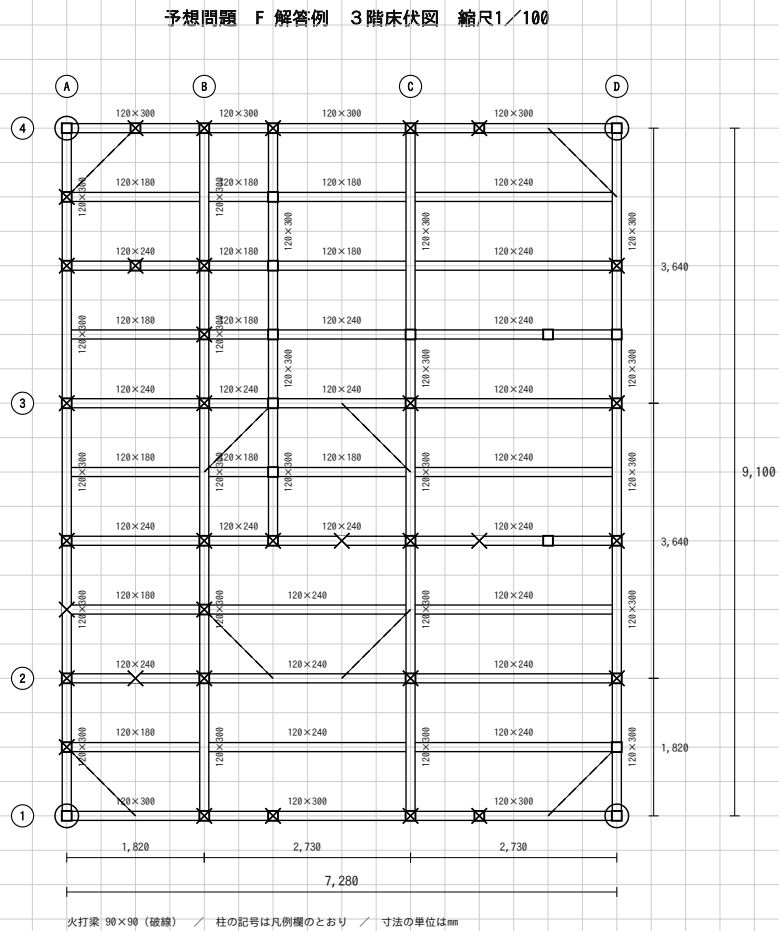


(4) 小屋伏図

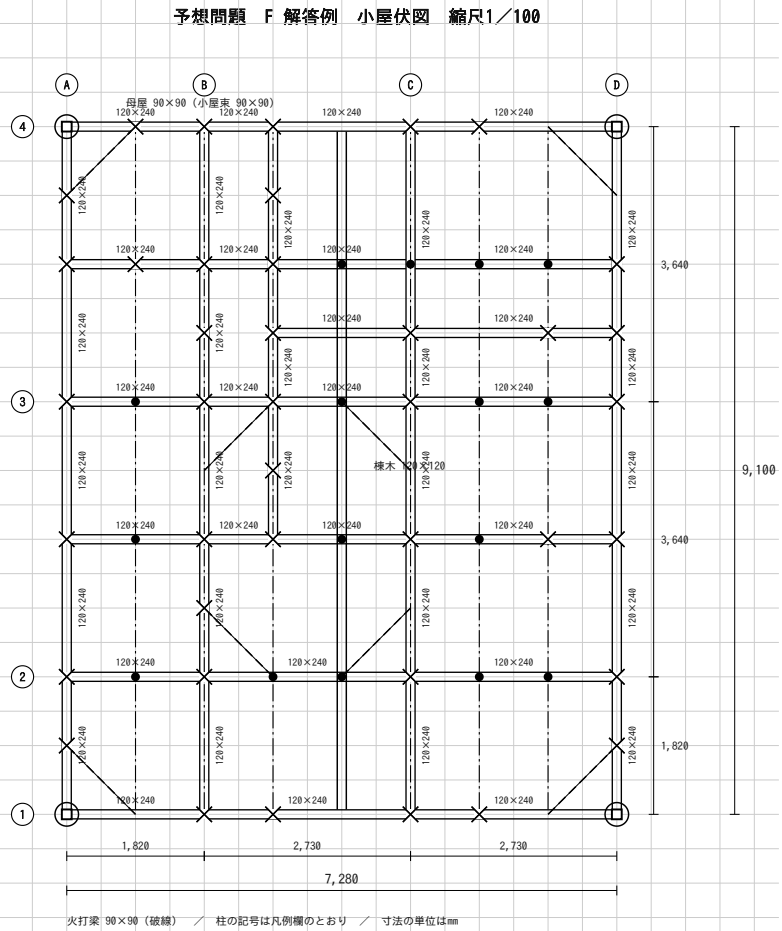

(8) 計画の要点等

- ① 北側道路に対して、住宅部分の日照をどのように確保したか
- ② 階段の位置について工夫した点
- ③ 防火及び避難について配慮した点
- ※ 解答例の本文は別紙「計画の要点等」(記述だけ)にて

(6) 部分詳細図 (断面) (目盛10mm)

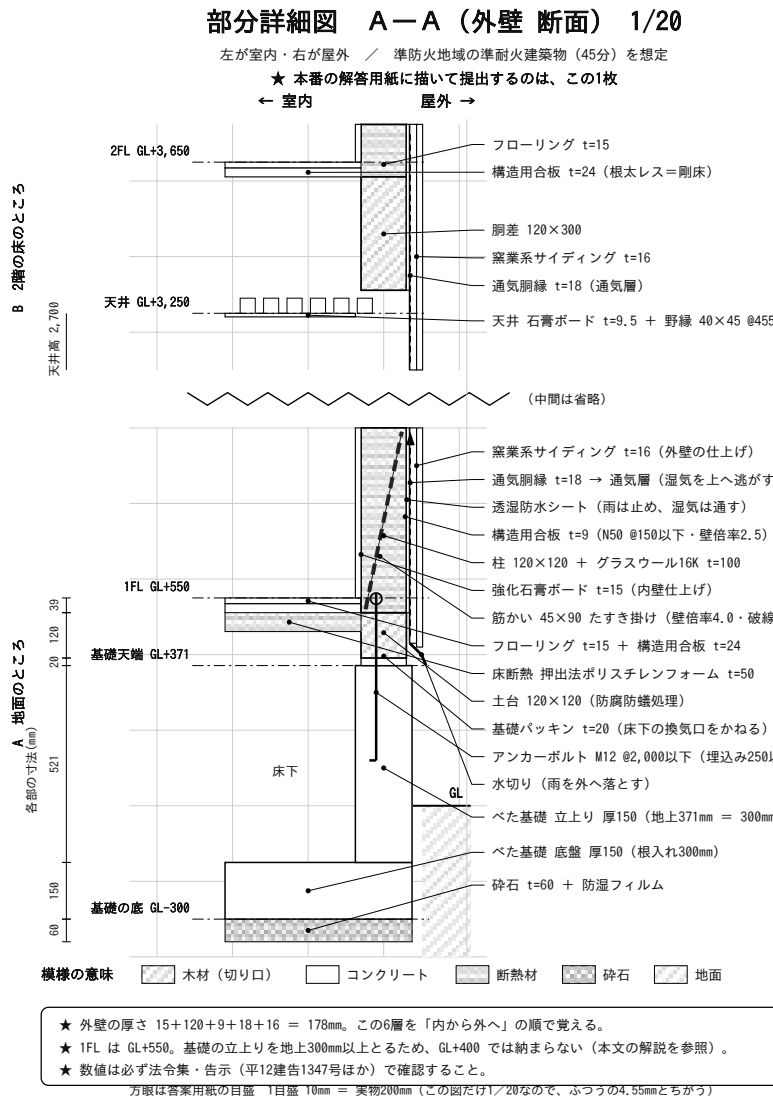

(7) 面積表

|            |                 |         |
|------------|-----------------|---------|
| 敷地面積       |                 | 180.00㎡ |
| 建築面積       | (計算式) 7.28×9.10 | 66.24㎡  |
| 床面積 1階 ア   | (計算式) 7.28×9.10 | 66.24㎡  |
| 2階 イ       | (計算式) 7.28×9.10 | 66.24㎡  |
| 3階 ウ       | (計算式) 7.28×9.10 | 66.24㎡  |
| 延べ面積 ア+イ+ウ |                 | 198.72㎡ |

※ 小数点以下第3位以下は切り捨て。計算式はm単位。

凡 例 (床伏図兼小屋伏図の表示記号)

|    | 通し柱     | 1階の管柱   | 2階の管柱   | 重なる管柱 胴差・桁 (正角材) | 同上 (平角材) | 同上 (丸太材) | 火打梁   | 棟木    | 母屋・小屋束        |
|----|---------|---------|---------|------------------|----------|----------|-------|-------|---------------|
| 記号 |         |         |         |                  |          |          |       |       |               |
| 寸法 | 120×120 | 120×120 | 120×120 | —                | 120×120  | 図中に記入    | 図中に記入 | 90×90 | 120×120 90×90 |

※ 平角材 (120×240 など) の断面寸法は、床伏図の中の梁1本ずつのわきに記入する。

## 標準解答例

受験番号

氏名

予想問題 F 北側道路の併用住宅 (書店)

木造3階建て / 8マス × 10マス (7,280 × 9,100)