




(1) 1階平面図 兼 配置図 縮尺1／100 (目盛4.55mm)

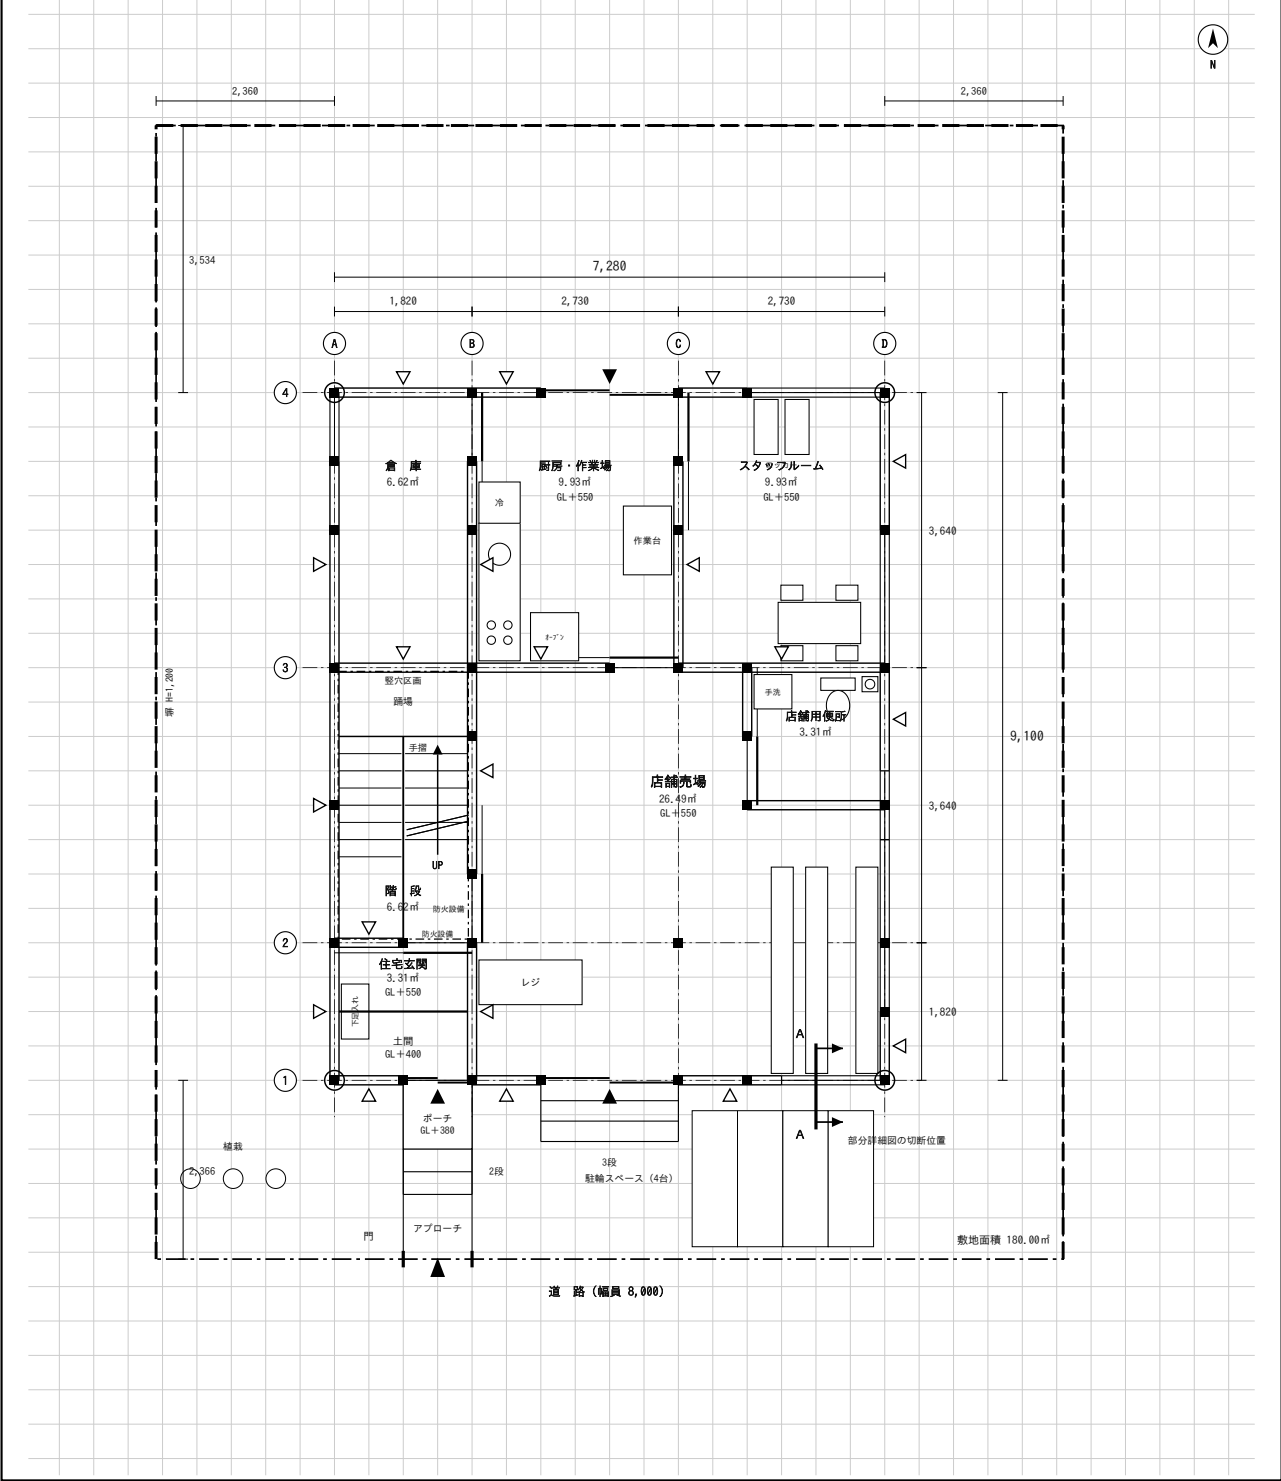


(2) 2階平面図 縮尺1／100 (目盛4.55mm)

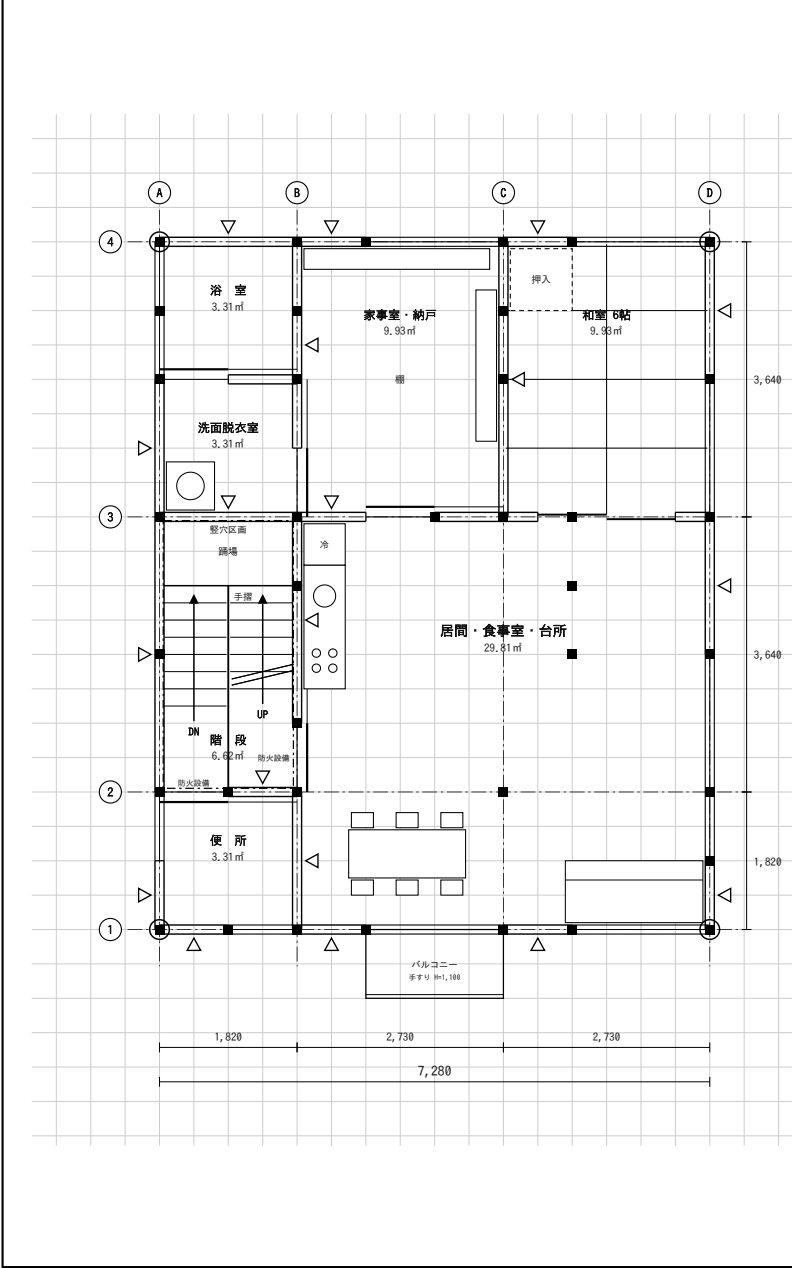

(3) 3階平面図 縮尺1／100 (目盛4.55mm)

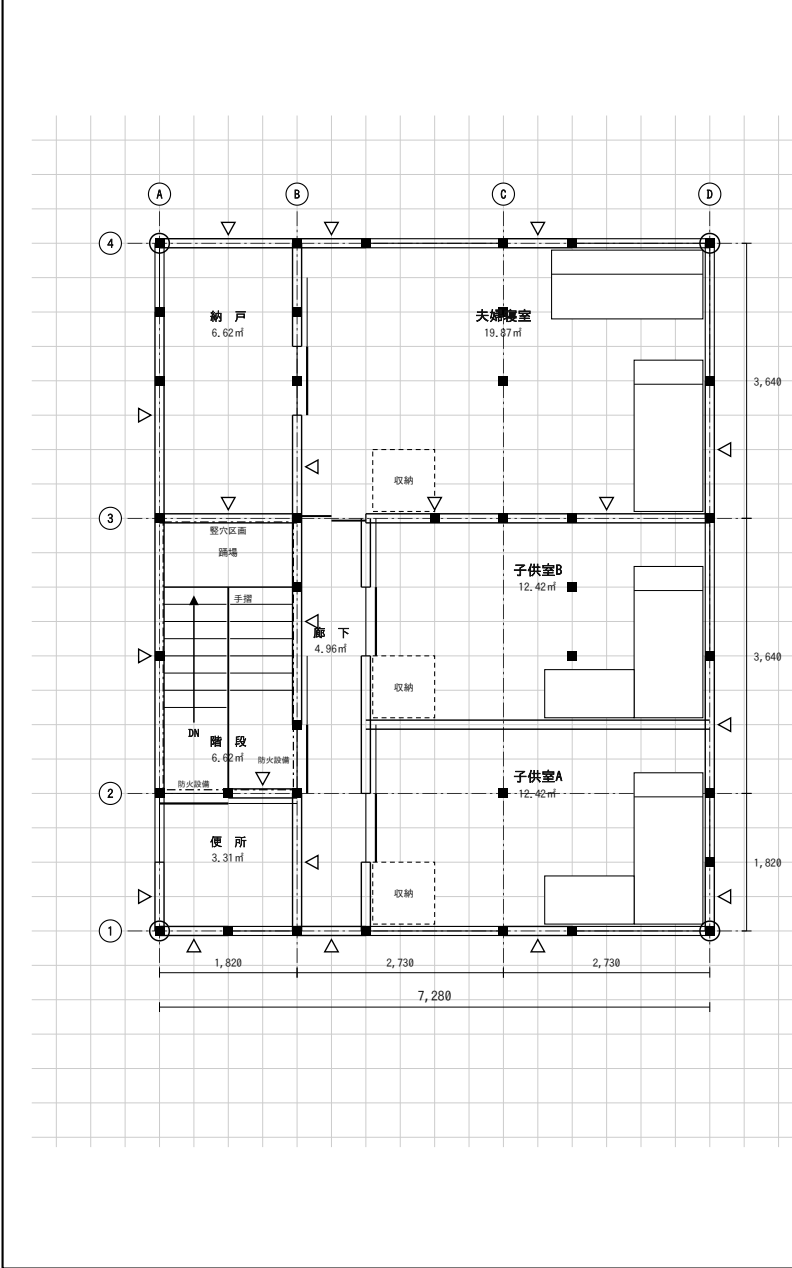

(5) 南側立面図

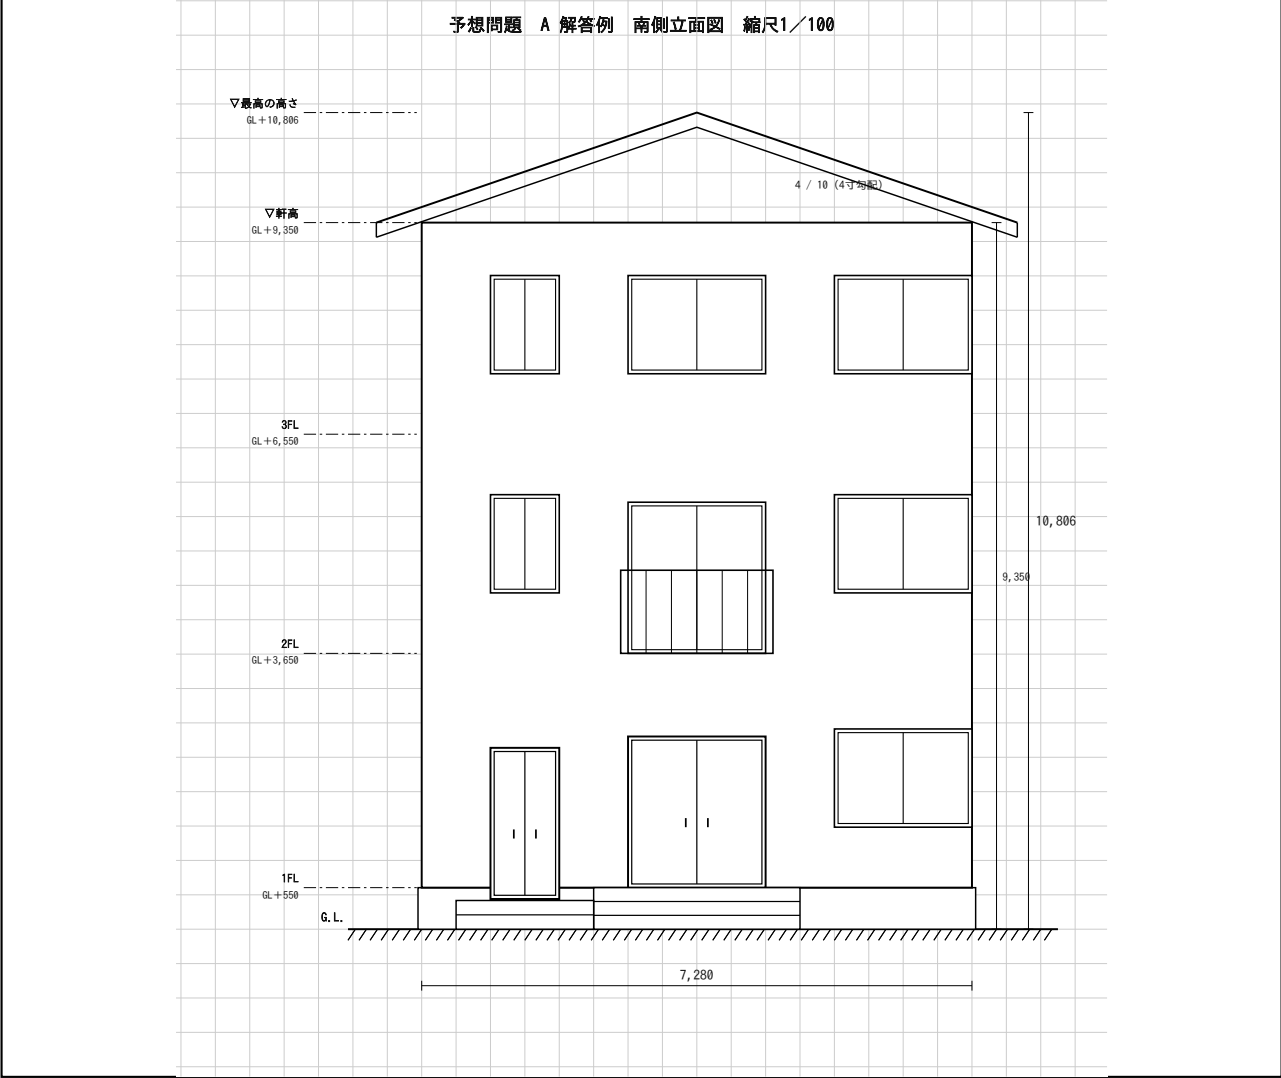

(7) 面積表

敷地面積		180.00	㎡
建築面積	(計算式) 7.28×9.10	66.24	㎡
床面積 1階 ア	(計算式) 7.28×9.10	66.24	㎡
2階 イ	(計算式) 7.28×9.10	66.24	㎡
3階 ウ	(計算式) 7.28×9.10	66.24	㎡
延べ面積 ア+イ+ウ		198.72	㎡


※ 小数点以下第3位以下は切り捨て。計算式はm単位。

凡 例 (床伏図兼小屋伏図の)


通し柱	1階の管柱	2階の管柱
記号		
寸法	120×120	120×120

※ 平角材 (120×240 など) の断面寸法は、床伏図

(4) 3階床伏図

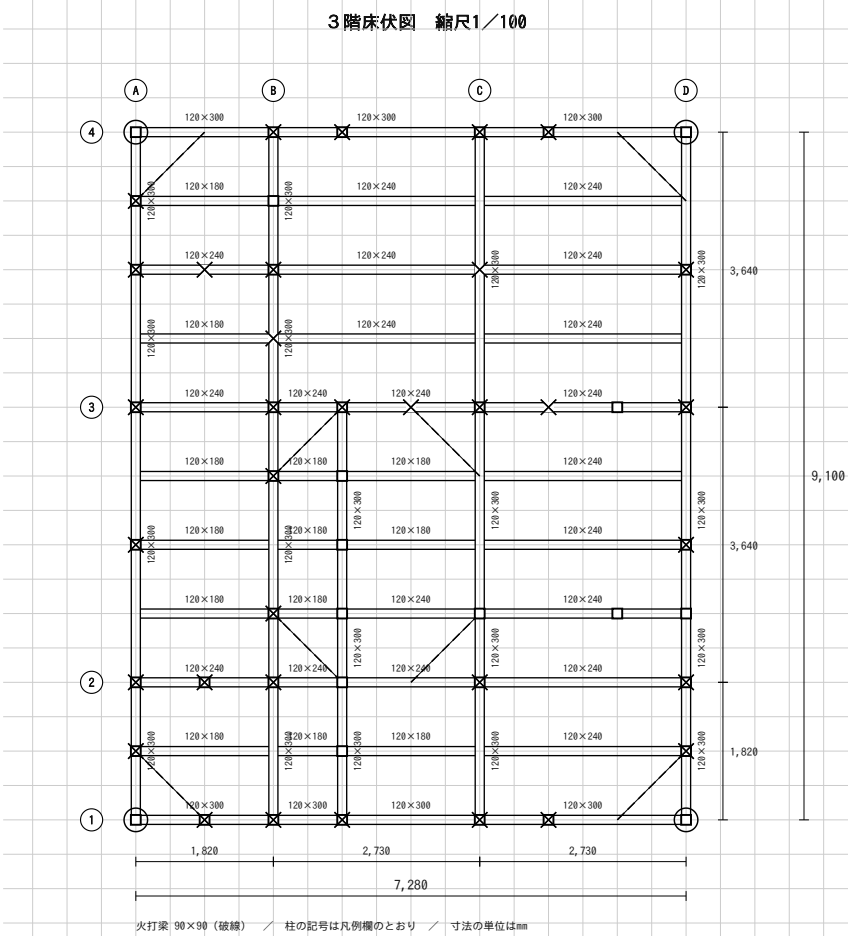

(4) 小屋伏図

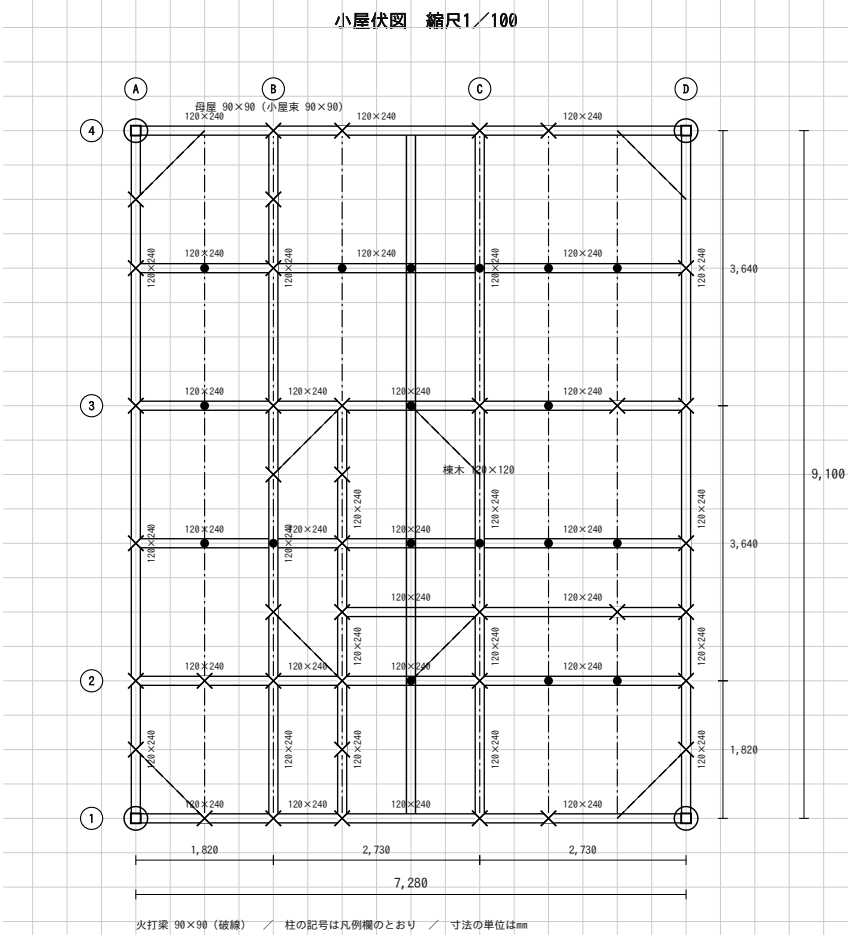

(8) 計画の要点等

① 木造3階建てとするに当たり、構造計画上工夫した点

② 店舗部分と住宅部分の動線計画について工夫した点

③ 防火及び避難について配慮した点

※ 解答例の本文は別紙「計画の要点等（記述だけ）」に


(6) 部分詳細図（断面）（目盛10mm）

部分詳細図 A-A（外壁 断面） 1/20

左が室内・右が屋外／準防火地域の準耐火建築物（45分）を想定

★ 本番の解答用紙に描いて提出するのは、この1枚

← 室内 屋外 →

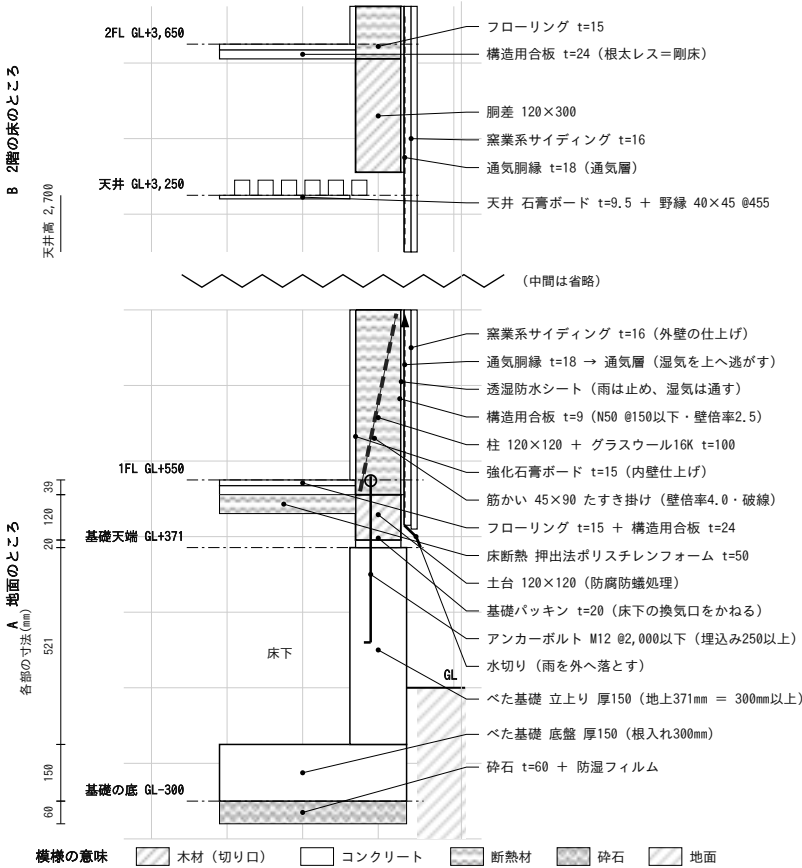

- ★ 外壁の厚さ 15+120+9+18+16 = 178mm。この6層を「内から外へ」の順で覚える。
- ★ 1FL は GL+550。基礎の立上りを地上300mm以上とるため、GL+400 では納まらない（本文の解説を参照）。
- ★ 数値は必ず法令集・告示（平12建告1347号ほか）で確認すること。

万眼は答案用紙の目盛 1目盛 10mm = 実物200mm（この図だけ1/20なので、ふつうの4.55mmとちがう）

標準解答例

受験番号	氏名
------	----

予想問題 A 商店街に建つ併用住宅（物販店舗）

木造3階建て／8マス×10マス（7,280×9,100）

図の中の梁1本ずつのわきに記入する。