




(1) 1階平面図 兼 配置図 縮尺1／100 (目盛4.55mm)

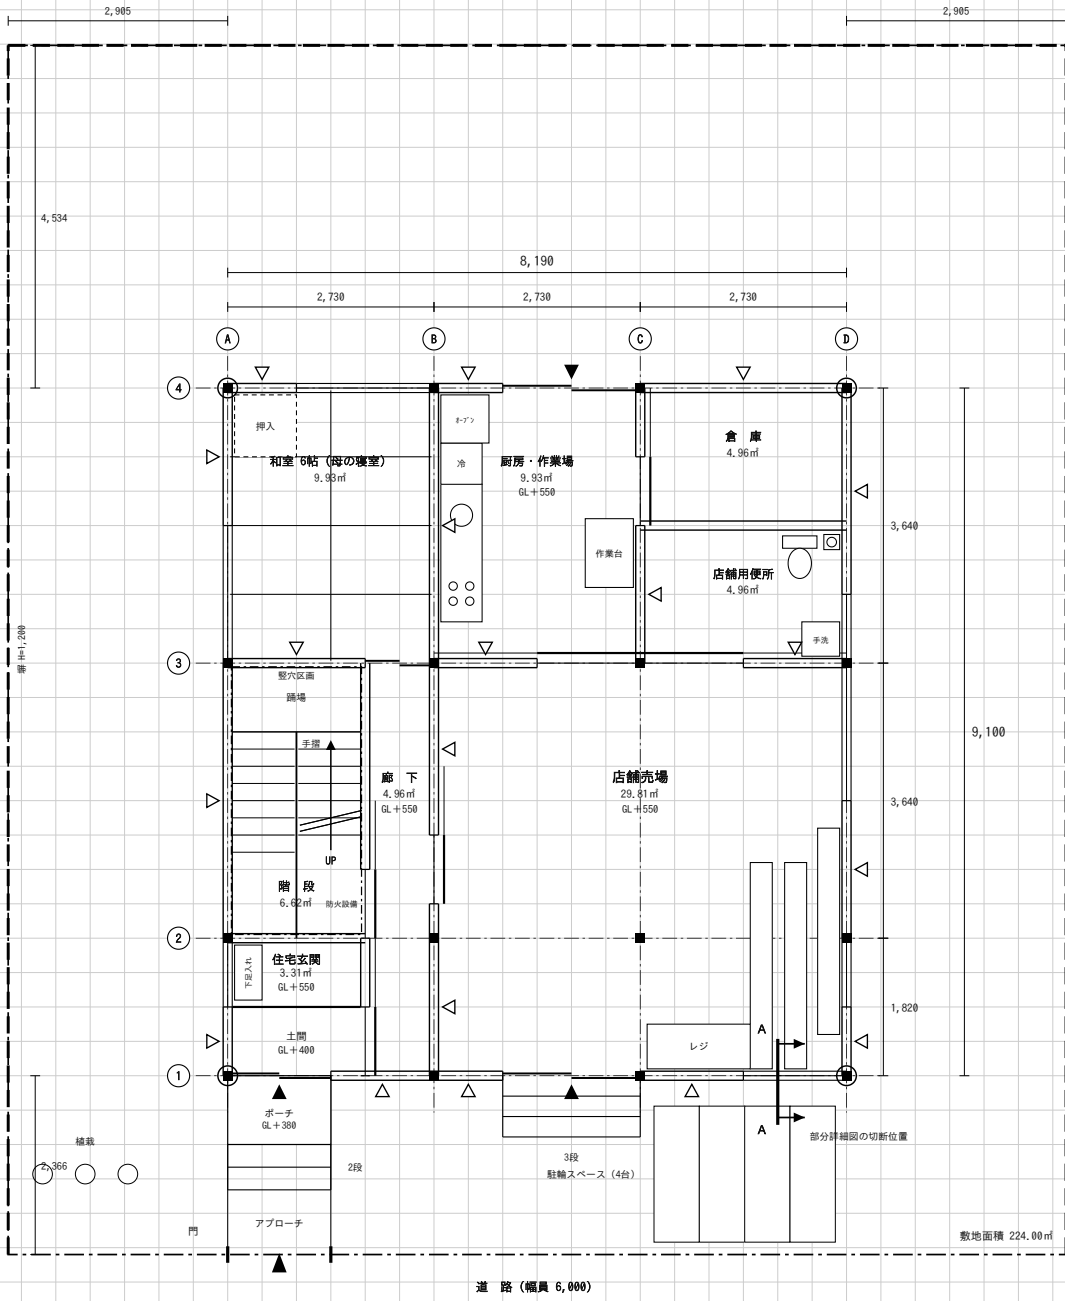


(2) 2階平面図 縮尺1／100 (目盛4.55mm)

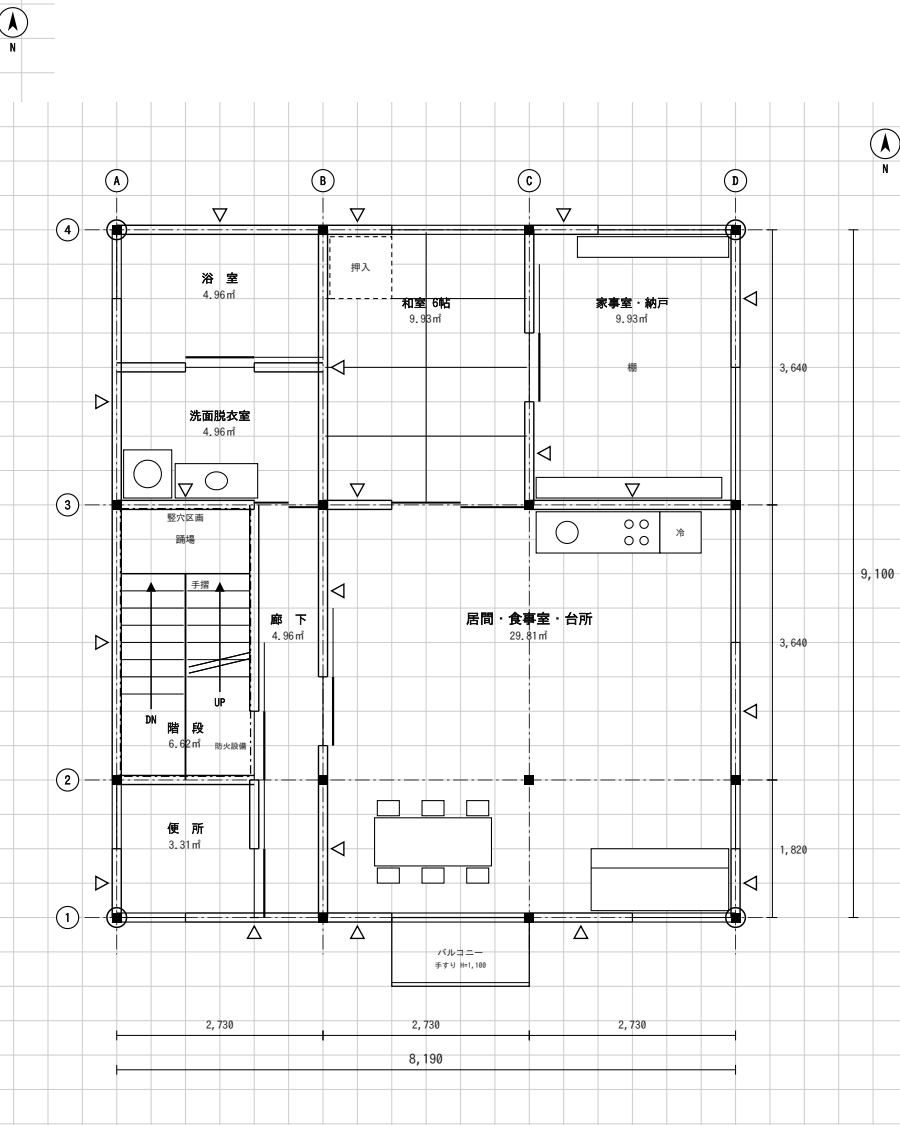


(3) 3階平面図 縮尺1／100 (目盛4.55mm)

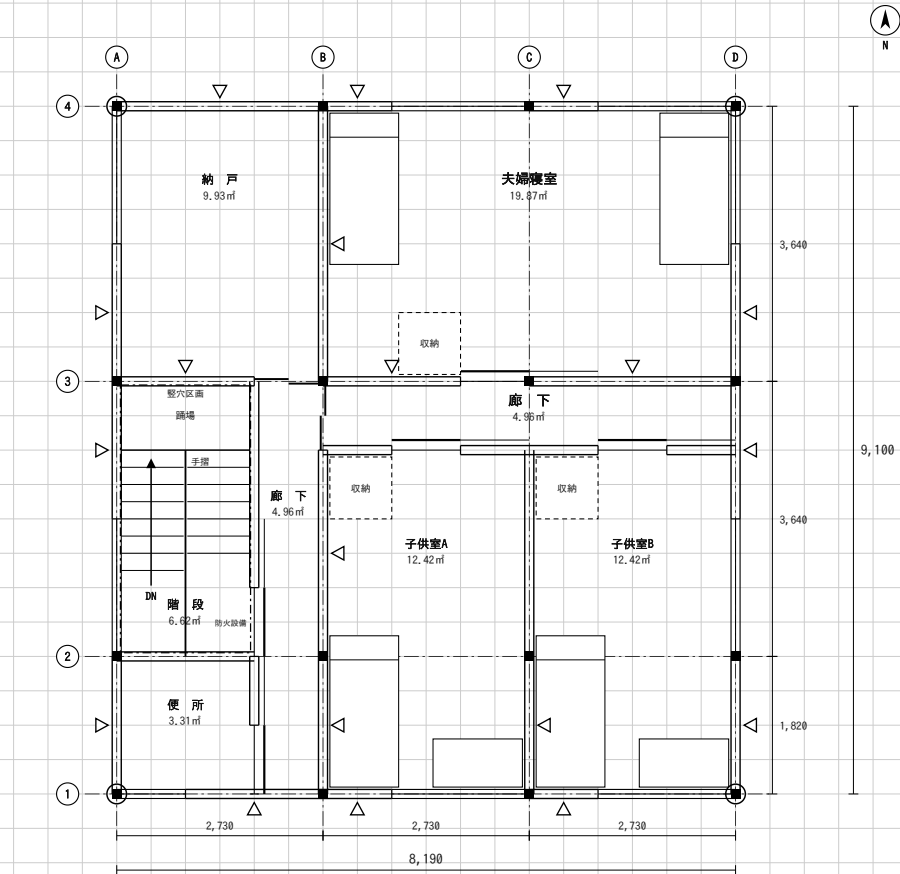

(4) 3階床伏図

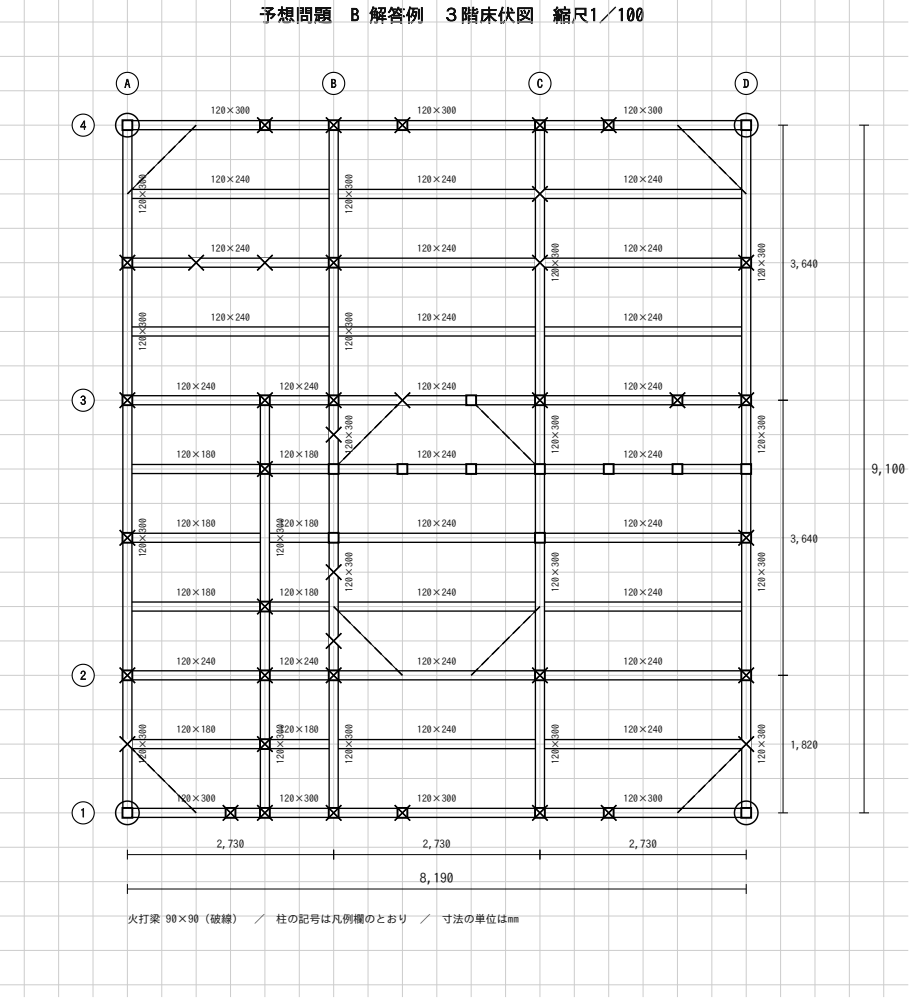

(4) 小屋伏図

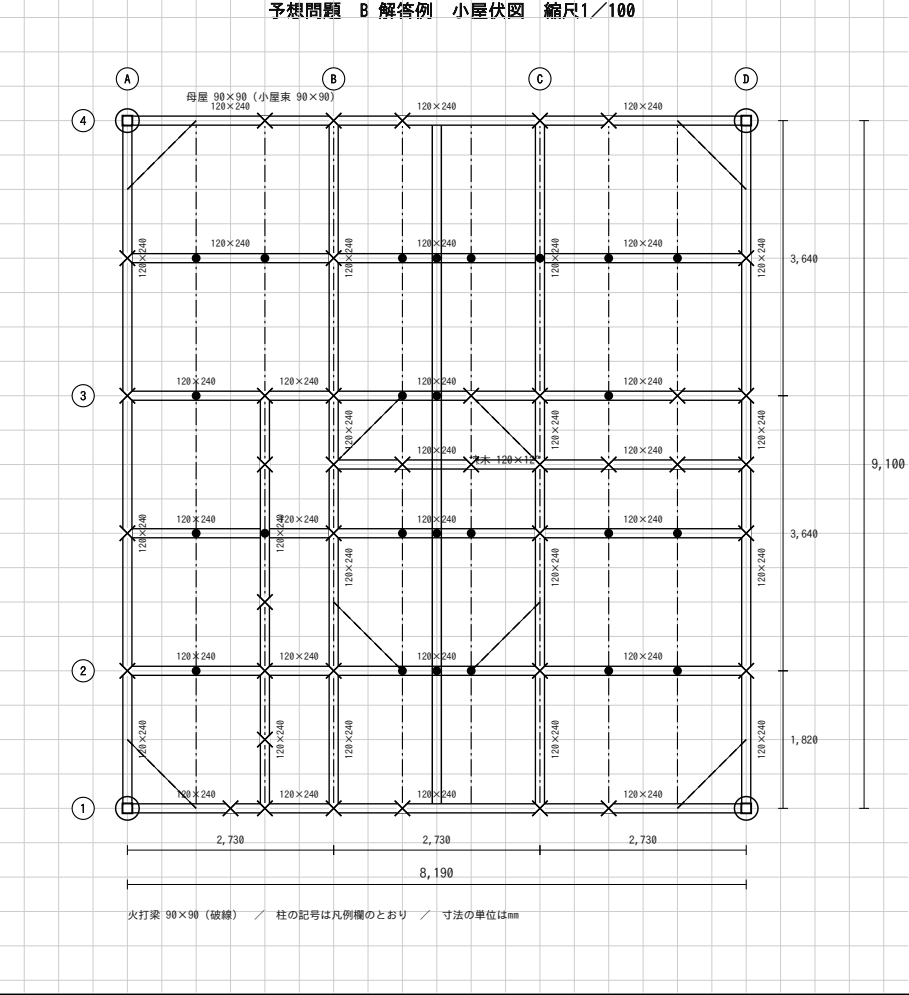

(8) 計画の要点等


① 高齢者の居室を1階に設けたことについて工夫した点

② 店舗部分と住宅部分の動線計画について工夫した点


③ 高齢者の避難について配慮した点

※ 解答例の本文は別紙「計画の要点等」(記述だけ)にて

(6) 部分詳細図 (断面) (目盛10mm)

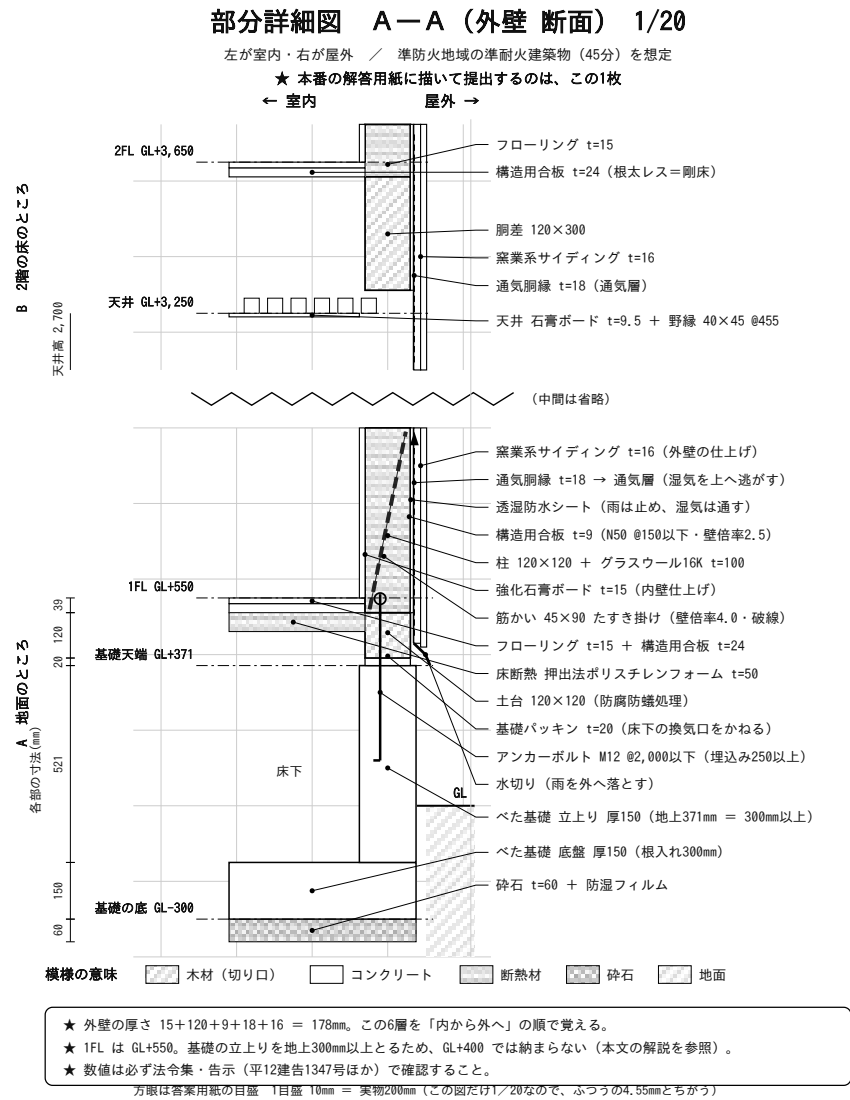

(5) 南側立面図

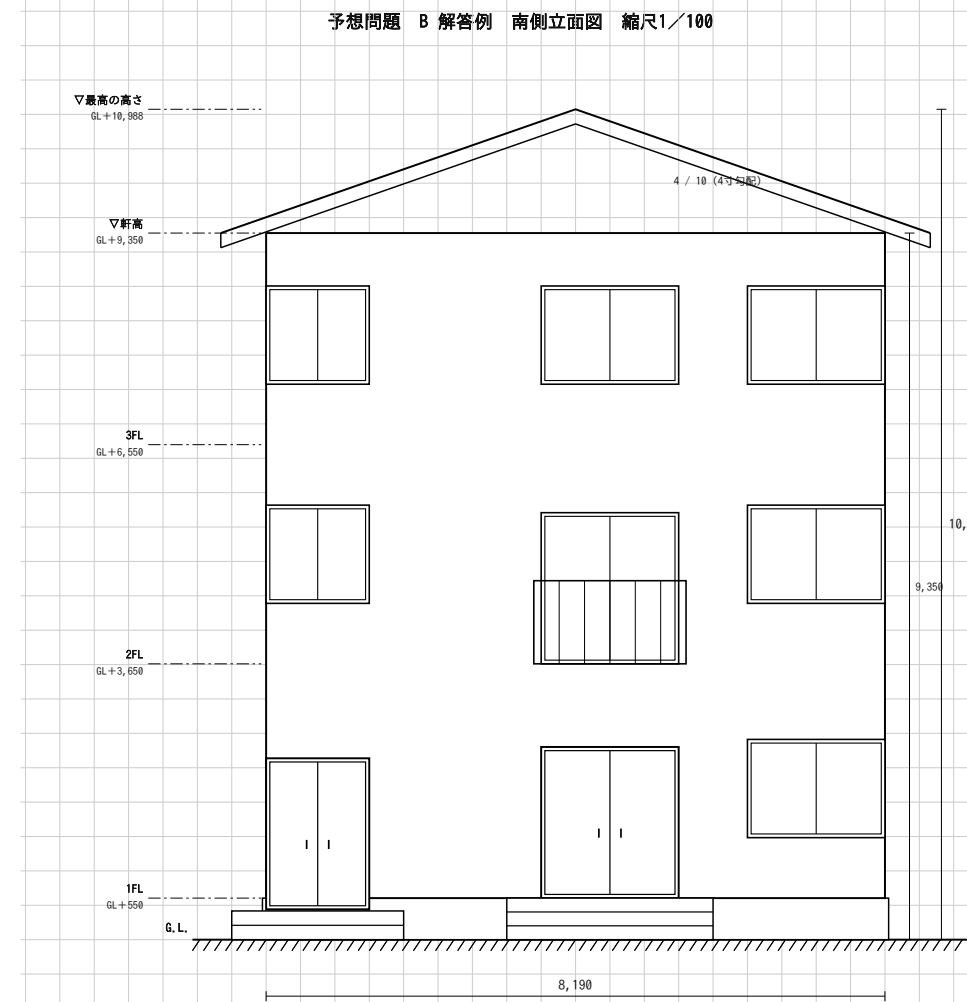

(7) 面積表

敷地面積		224.00㎡
建築面積	(計算式) 8.19×9.10	74.52㎡
床面積 1階 ア	(計算式) 8.19×9.10	74.52㎡
2階 イ	(計算式) 8.19×9.10	74.52㎡
3階 ウ	(計算式) 8.19×9.10	74.52㎡
延べ面積 ア+イ+ウ		223.56㎡

※ 小数点以下第3位以下は切り捨て。計算式はm単位。

凡 例 (床伏図兼小屋伏図の表示記号)

記号	通し柱	1階の管柱	2階の管柱	重なる管柱 差・桁 (正角材)	同上 (平角材)	同上 (丸太材)	火打梁	棟木	母屋・小屋束
寸法	120×120	120×120	120×120	—	120×120	図中に記入	図中に記入	90×90	120×120 90×90

※ 平角材 (120×240 など) の断面寸法は、床伏図の中の梁1本ずつのわきに記入する。

標準解答例

受験番号 氏名

予想問題 B 母と暮らす併用住宅 (和菓子店)

木造3階建て / 9マス × 10マス (8,190 × 9,100)