




(1) 1階平面図 兼 配置図 縮尺1／100 (目盛4.55mm)

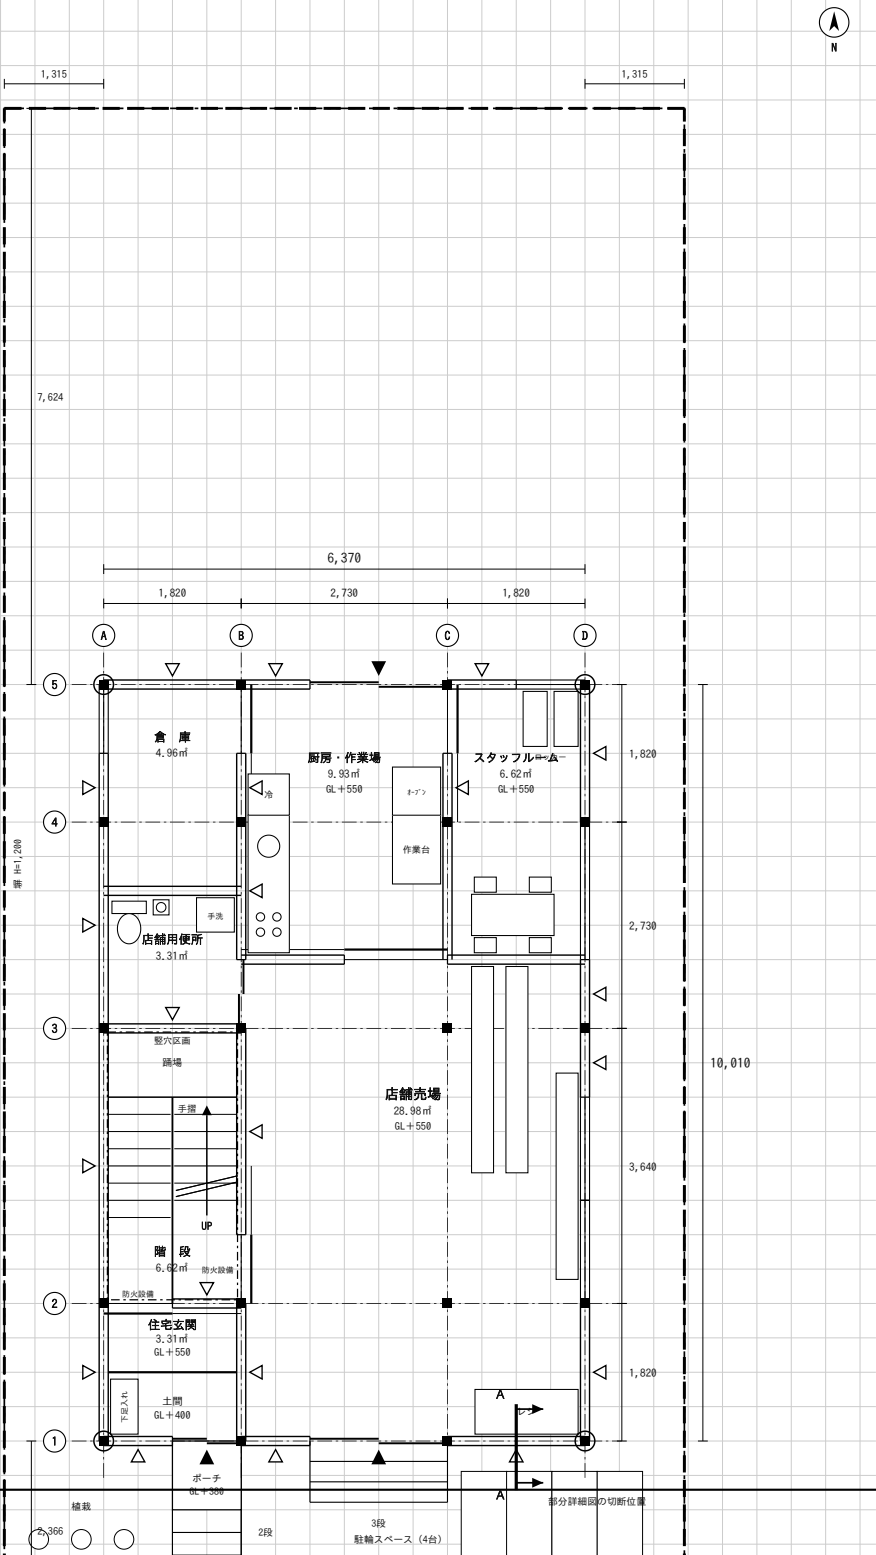


(5) 南側立面図

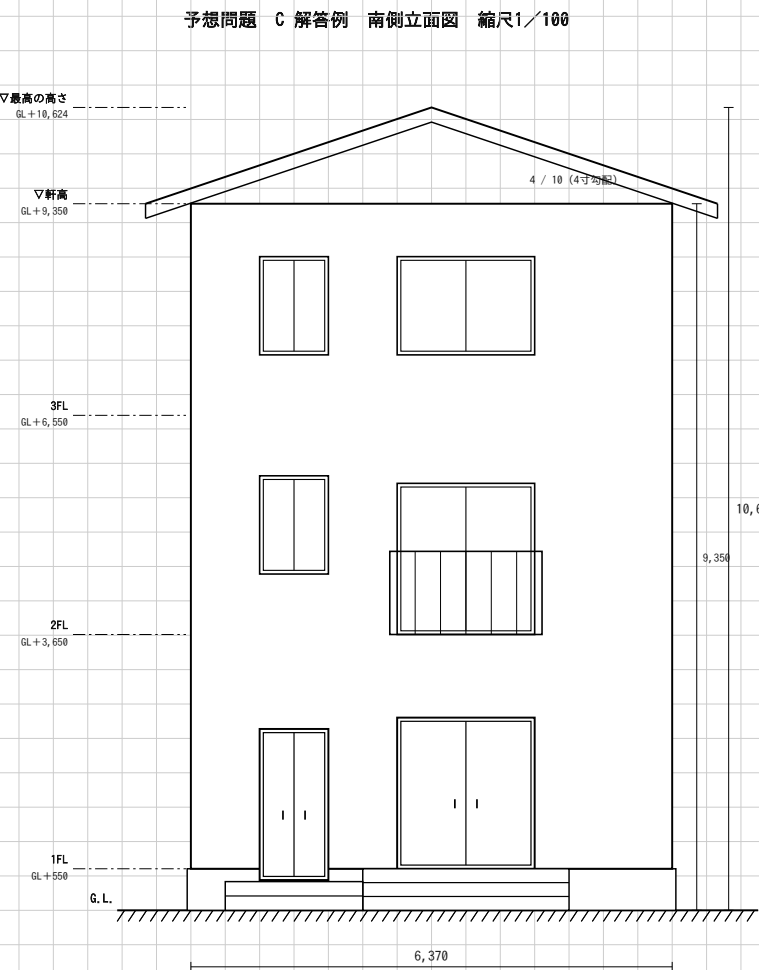


(2) 2階平面図 縮尺1／100 (目盛4.55mm)

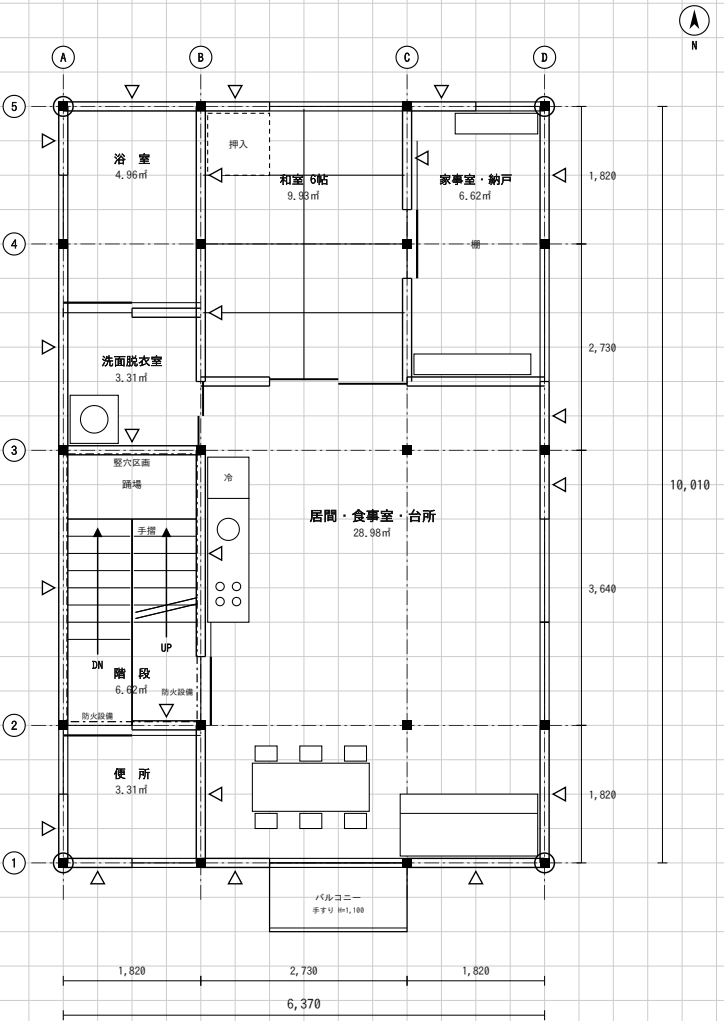


(3) 3階平面図 縮尺1／100 (目盛4.55mm)

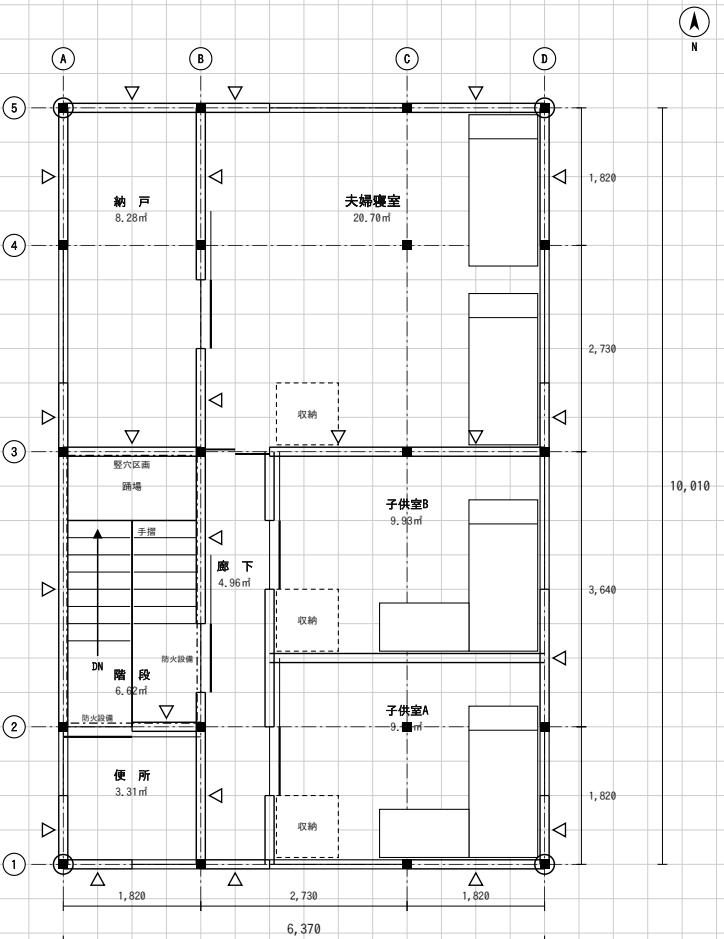

(4) 3階床伏図

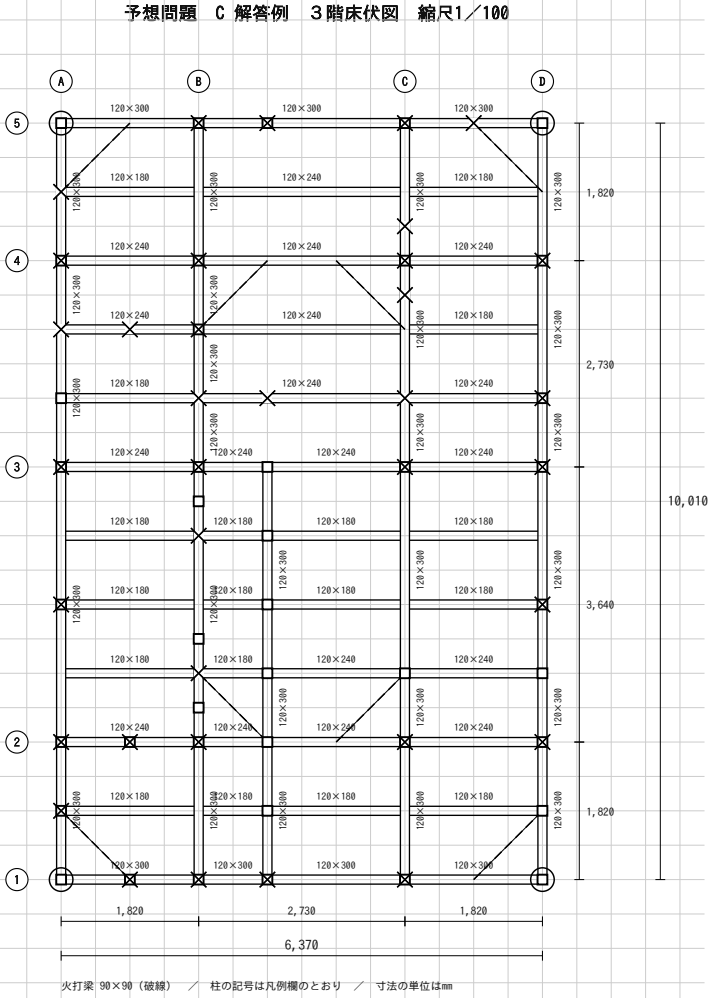


(4) 小屋伏図

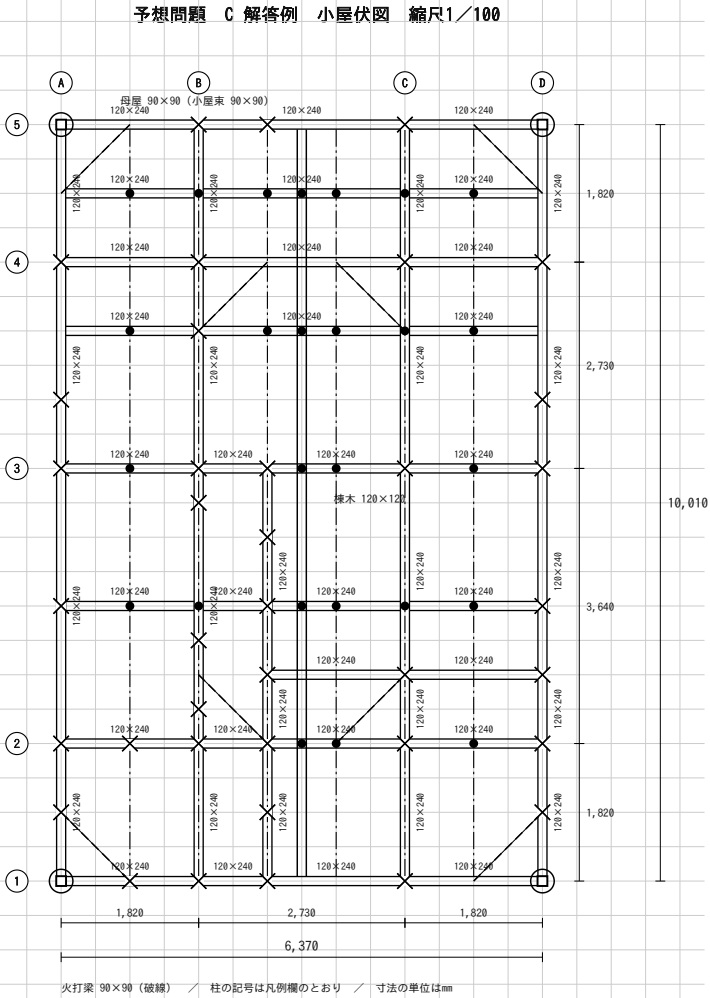

(8) 計画の要点等

- ① 間口が狭い敷地に対して、平面計画上工夫した点
- ② 奥行きの深い店舗売場の採光及び通風について工夫した点
- ③ 木造3階建てとするに当たり、構造計画上工夫した点

(6) 部分詳細図 (断面) (目盛10mm)

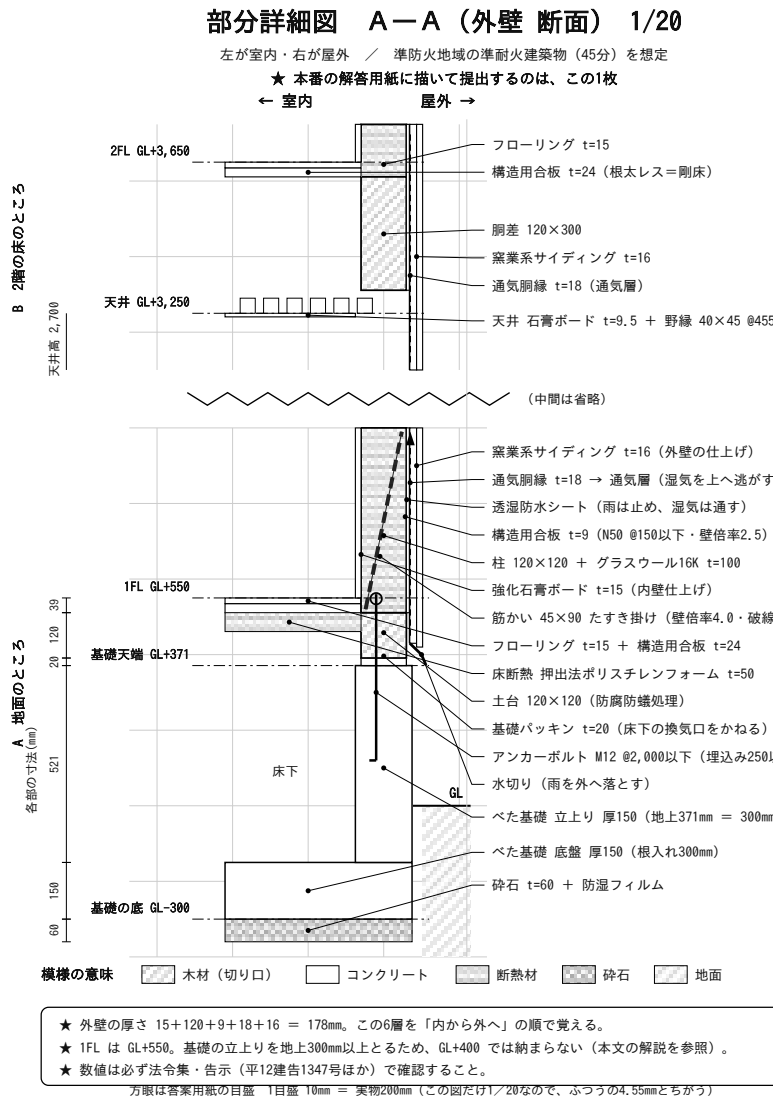

(7) 面積表

敷地面積		180.00 ㎡
建築面積	(計算式) 6.37×10.01	63.76 ㎡
床面積 1階 ア	(計算式) 6.37×10.01	63.76 ㎡
2階 イ	(計算式) 6.37×10.01	63.76 ㎡
3階 ウ	(計算式) 6.37×10.01	63.76 ㎡
延べ面積 ア+イ+ウ		191.28 ㎡

※ 小数点以下第3位以下は切り捨て。計算式はm単位。

凡 例 (床伏図兼小屋伏図の表示記号)

	通し柱	1階の管柱	2階の管柱	重なる管柱 胴差・桁 (正角材)	同上 (平角材)	同上 (丸太材)	火打梁	棟木	母屋・小屋束
記号									
寸法	120×120	120×120	120×120	—	120×120	図中に記入	図中に記入	90×90	120×120 90×90

※ 平角材 (120×240 など) の断面寸法は、床伏図の中の梁1本ずつのわきに記入する。

標準解答例

受験番号

氏名

予想問題 C 間口の狭い敷地の併用住宅 (喫茶店)

木造3階建て / 7マス × 11マス (6,370 × 10,010)