




(1) 1階平面図 兼 配置図 縮尺1／100 (目盛4.55mm)

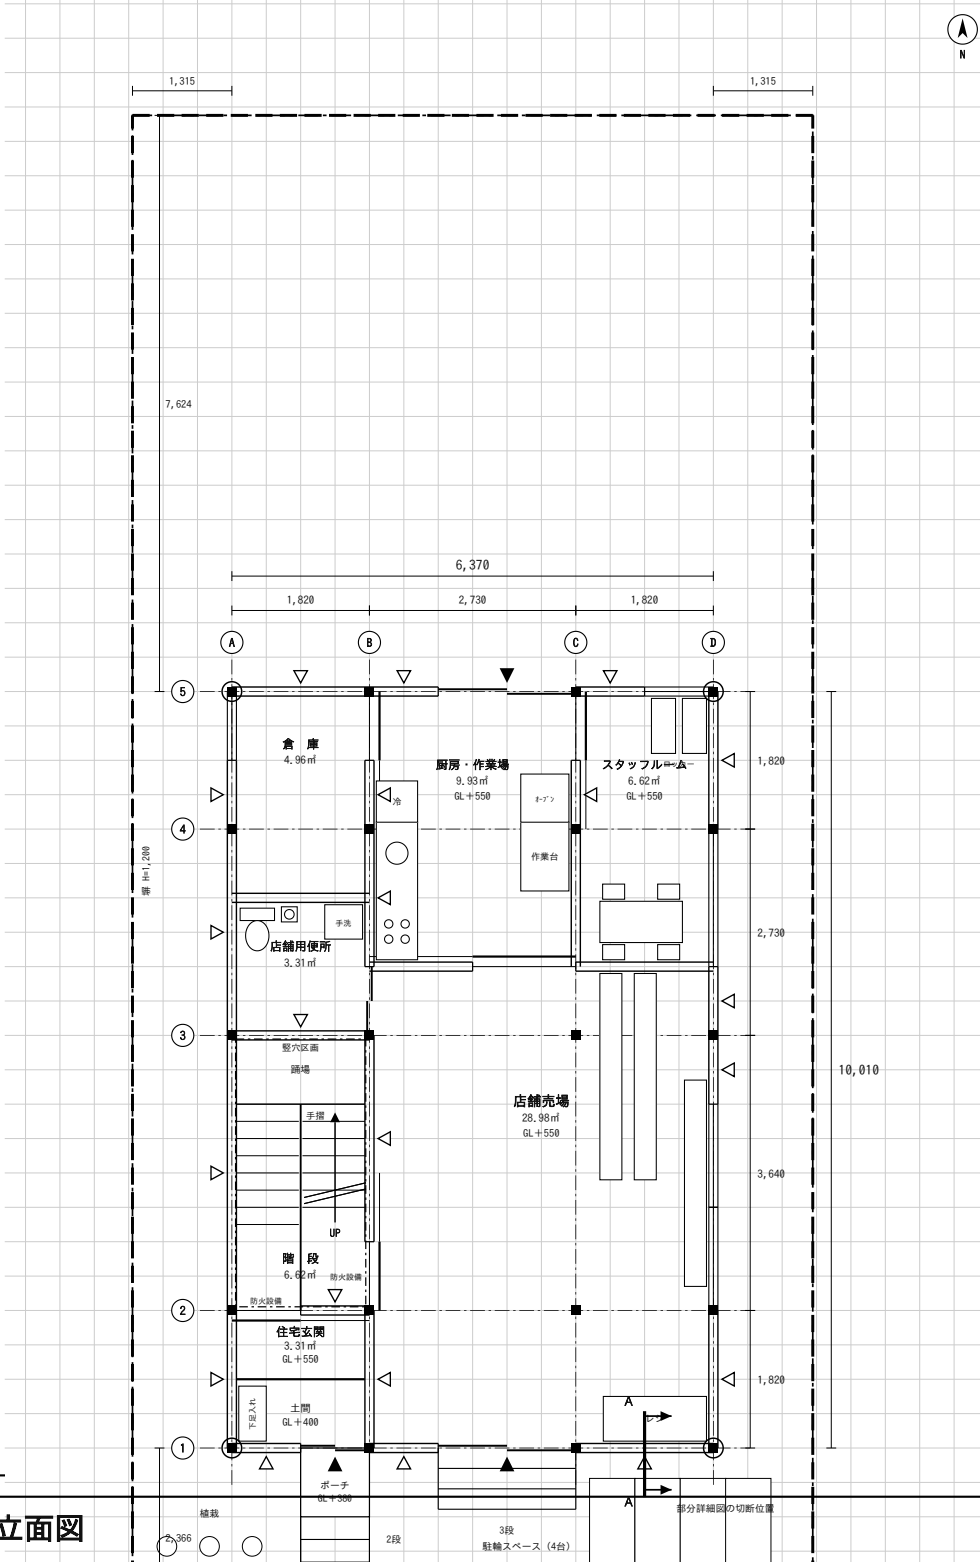


(5) 南側立面図

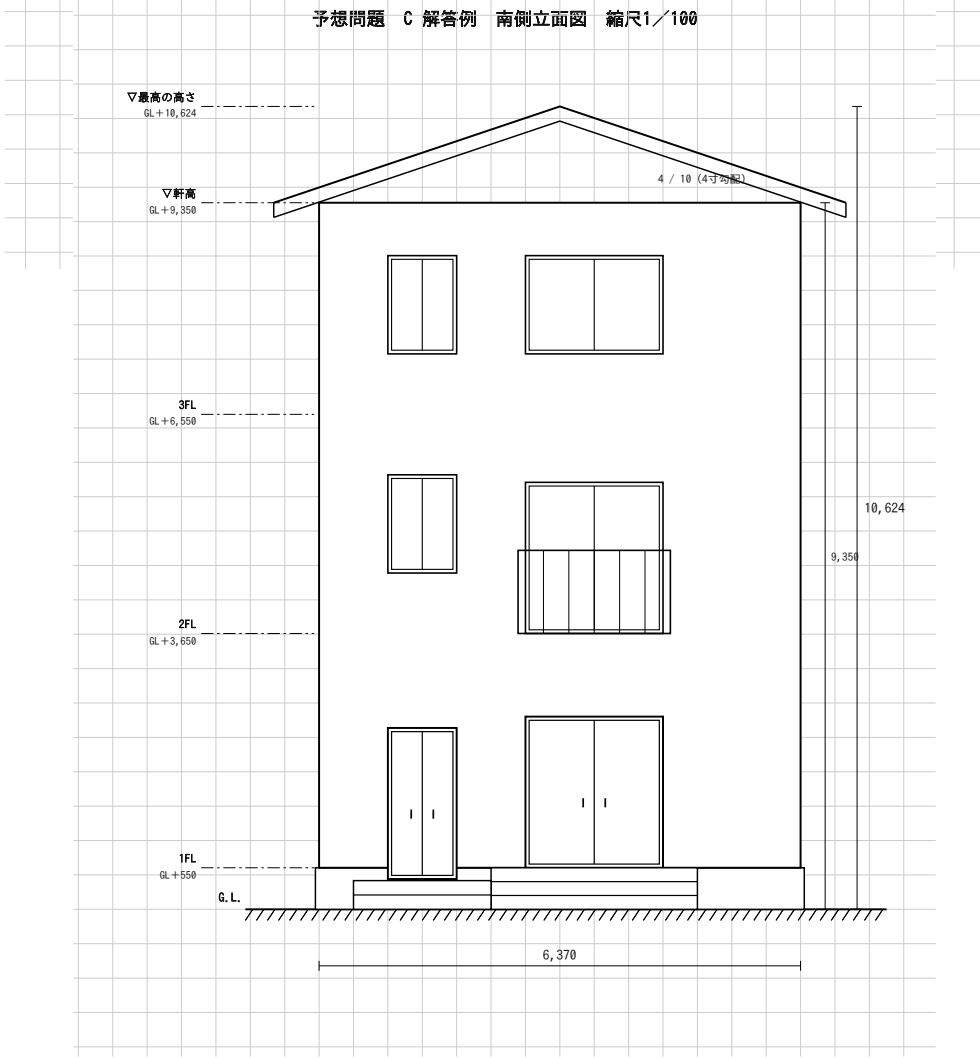

(2) 2階平面図 縮尺1／100 (目盛4.55mm)

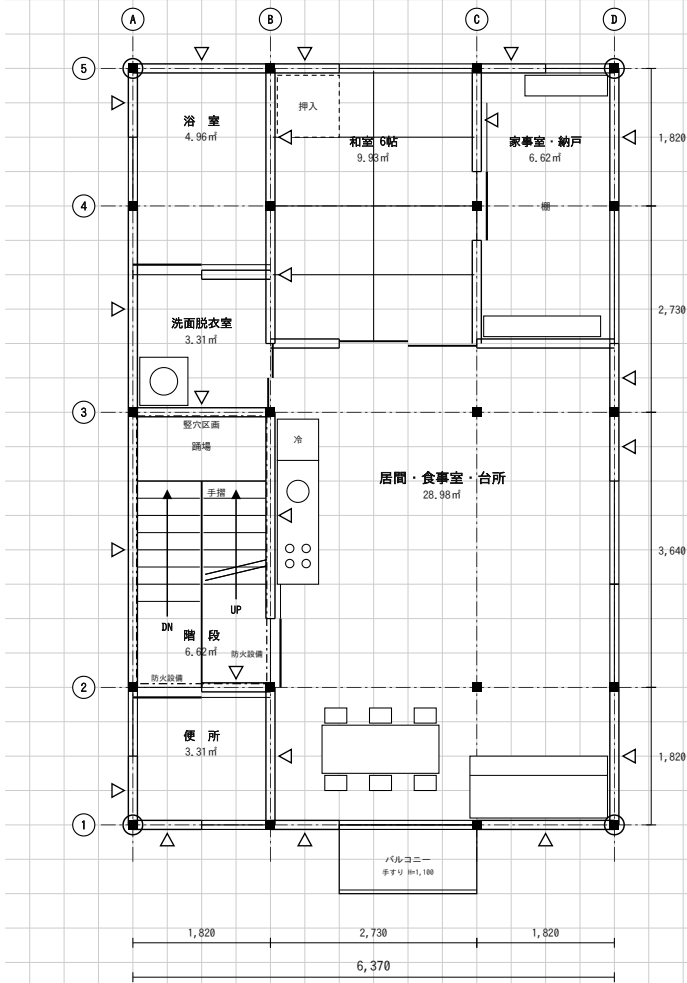

(3) 3階平面図 縮尺1／100 (目盛4.55mm)

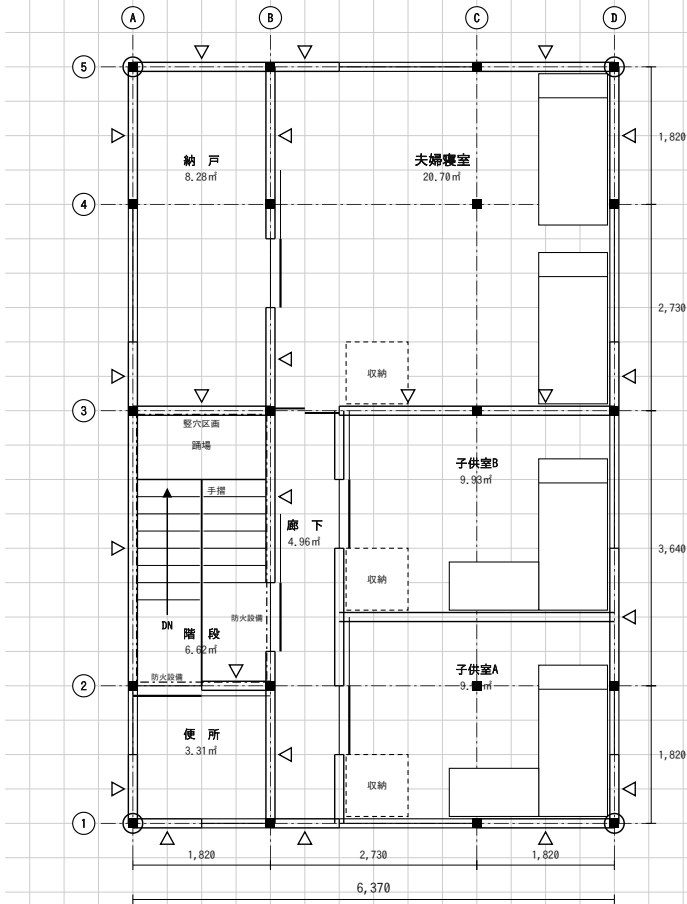

(7) 面積表

敷地面積		180.00	㎡
建築面積	(計算式) 6.37×10.01	63.76	㎡
床面積 1階 ア	(計算式) 6.37×10.01	63.76	㎡
2階 イ	(計算式) 6.37×10.01	63.76	㎡
3階 ウ	(計算式) 6.37×10.01	63.76	㎡
延べ面積 ア+イ+ウ		191.28	㎡

※ 小数点以下第3位以下は切り捨て。計算式はm単位。


凡 例 (床伏図兼小屋伏図の)

	通し柱	1階の管柱	2階の管柱
記号			
寸法	120×120	120×120	120×120

※ 平角材 (120×240 など) の断面寸法は、床伏


(4) 3階床伏図

予想問題 C 解答例 3階床伏図 縮尺1／100

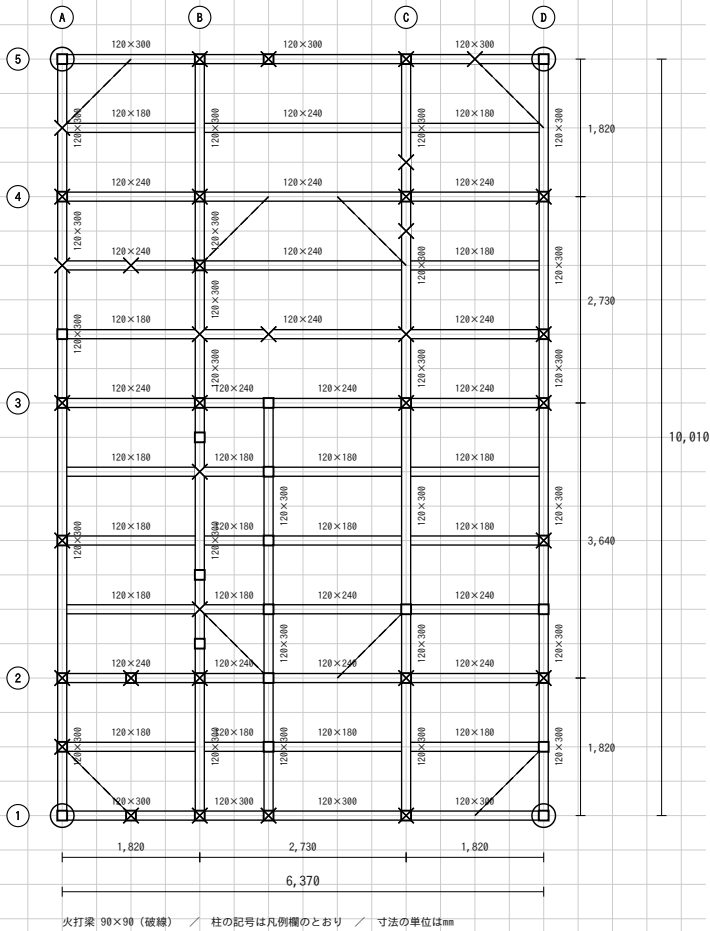

(4) 小屋伏図

予想問題 C 解答例 小屋伏図 縮尺1／100

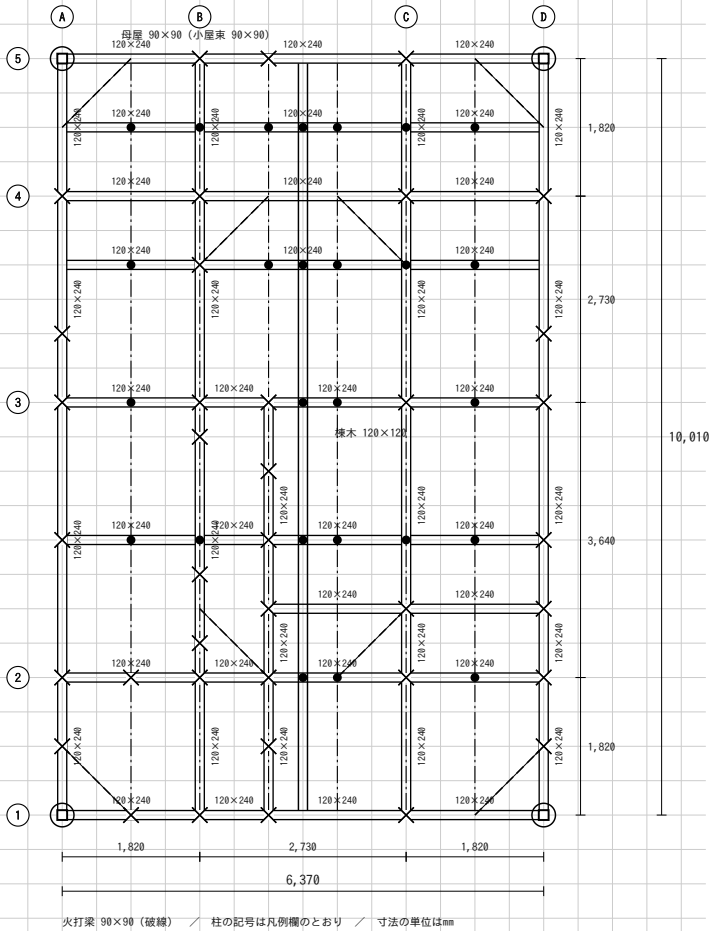

(8) 計画の要点等

① 間口が狭い敷地に対して、平面計画上工夫した点

② 奥行きの深い店舗売場の採光及び通風について工夫した点

③ 木造3階建てとするに当たり、構造計画上工夫した点


※ 解答例の本文は別紙「計画の要点等（記述だけ）」に

(6) 部分詳細図（断面） （目盛10mm）

部分詳細図 A－A（外壁 断面） 1/20

左が室内・右が屋外 / 準防火地域の準耐火建築物（45分）を想定

★ 本番の解答用紙に描いて提出するのは、この1枚
← 室内 屋外 →

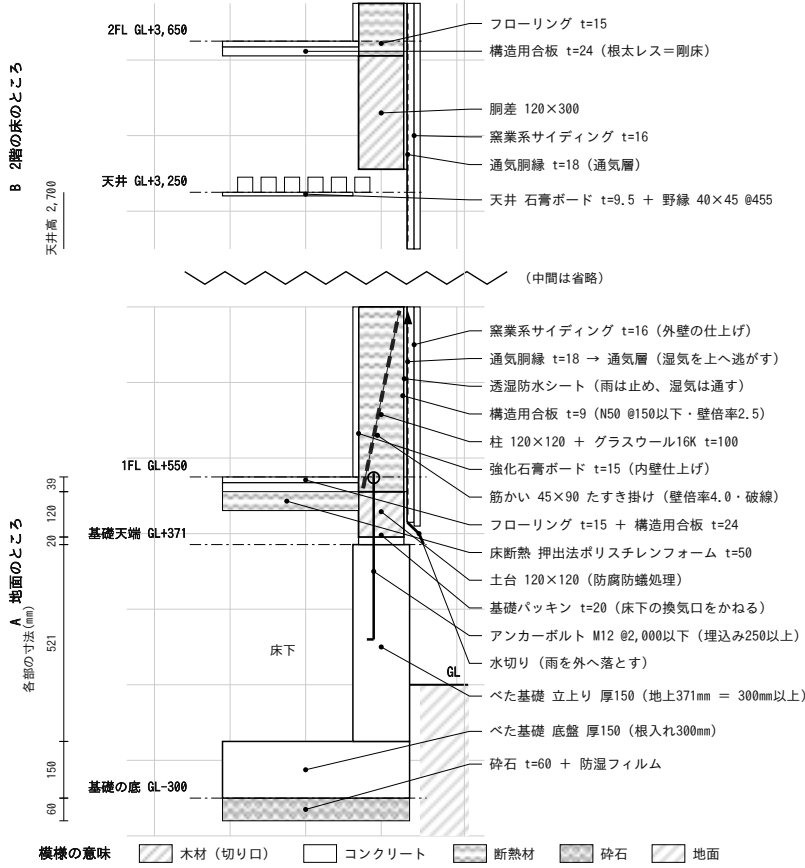

★ 外壁の厚さ 15+120+9+18+16 = 178mm。この6層を「内から外へ」の順で覚える。
★ 1FL は GL+550。基礎の立上りを地上300mm以上とるため、GL+400 では納まらない（本文の解説を参照）。
★ 数値は必ず法令集・告示（平12建告1347号ほか）で確認すること。
万眼は答案用紙の目盛 1目盛 10mm = 実物200mm（この図だけ1／20なので、ふつうの4.55mmとちがう）

標準解答例

受験番号

氏名

予想問題 C 間口の狭い敷地の併用住宅（喫茶店）

木造3階建て / 7マス × 11マス (6,370 × 10,010)

の表示記号)

重なる管柱	胴差・桁（正角材）	同上（平角材）	同上（丸太材）	火打梁	棟木	母屋・小屋束
—	120×120	図中に記入	図中に記入	90×90	120×120	90×90

図の中の梁1本ずつのわきに記入する。