




(1) 1階平面図 兼 配置図 縮尺1/100 (目盛4.55mm)

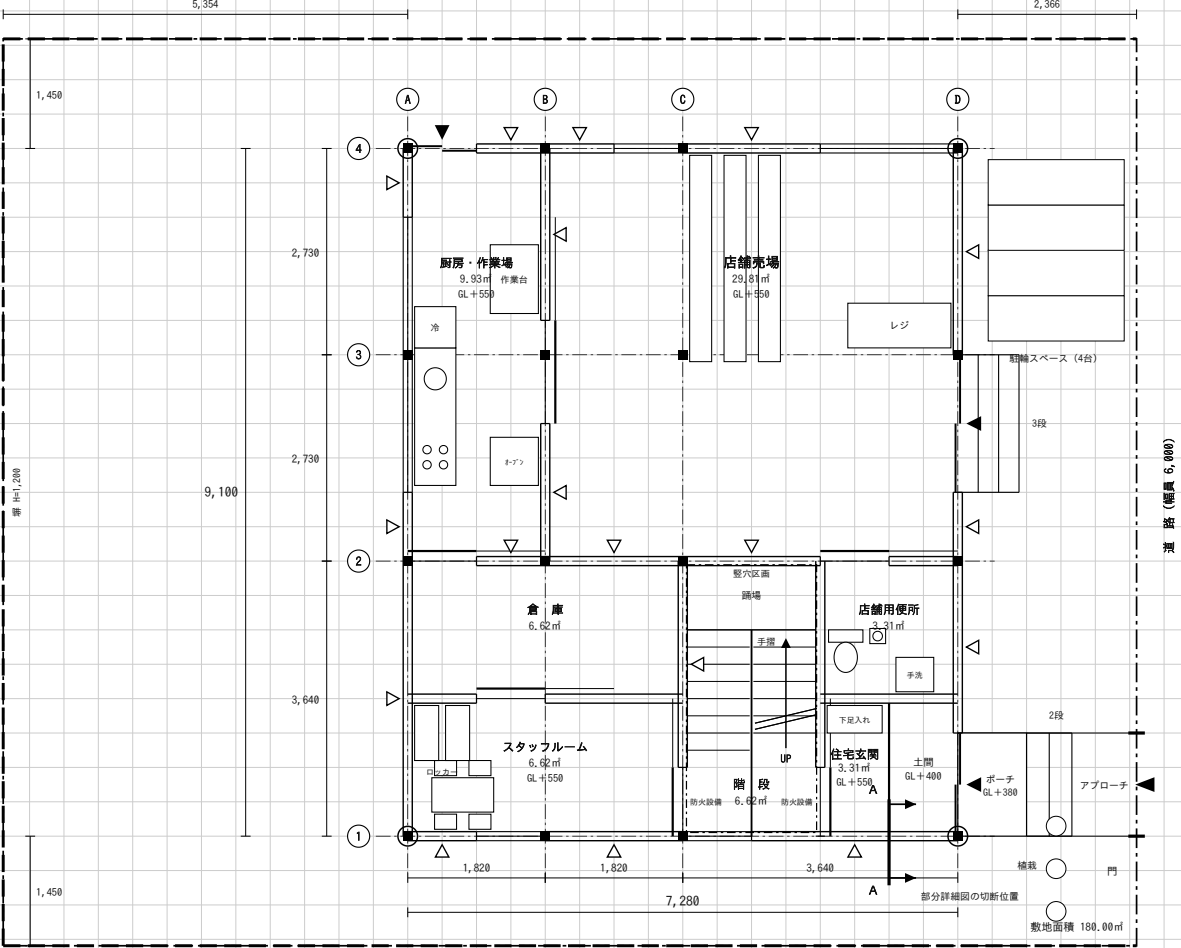


(2) 2階平面図 縮尺1/100 (目盛4.55mm)

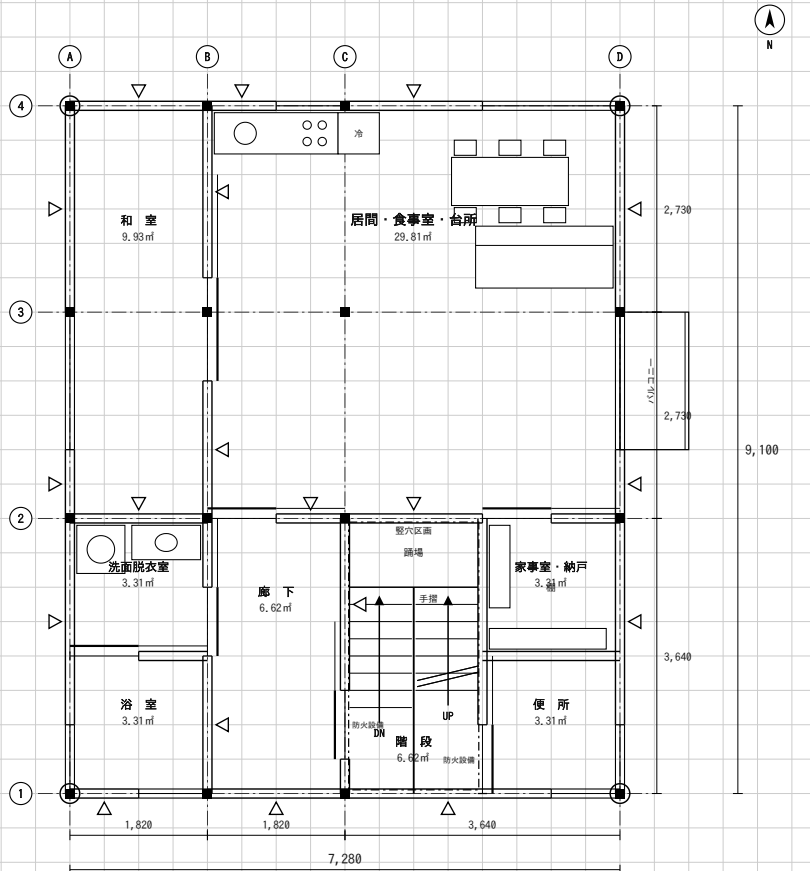


(3) 3階平面図 縮尺1/100 (目盛4.55mm)

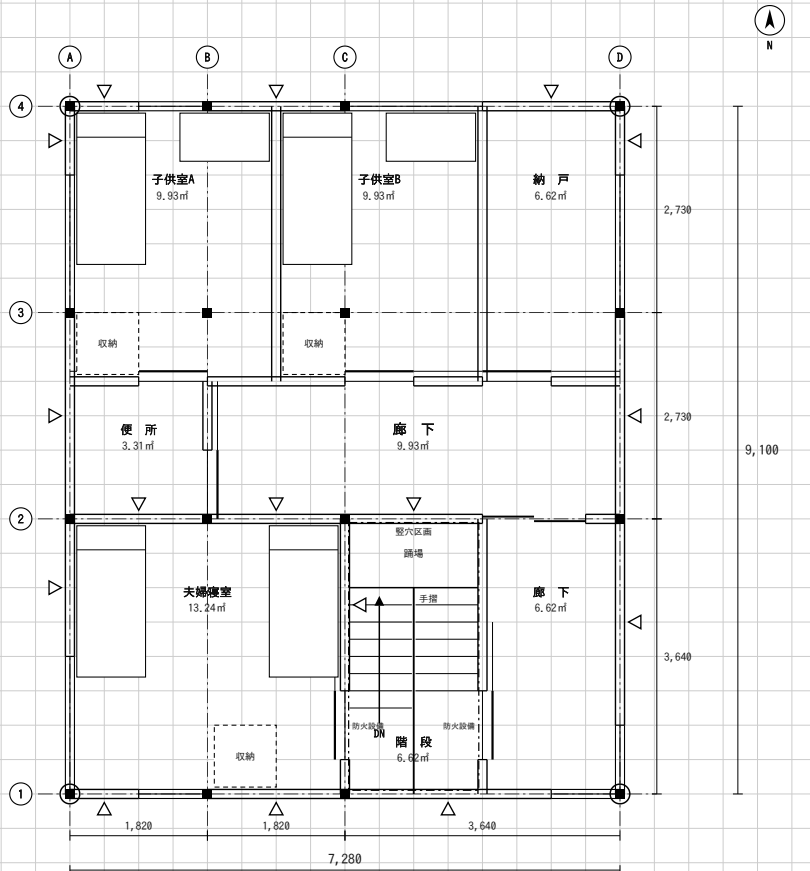


(4) 3階床伏図

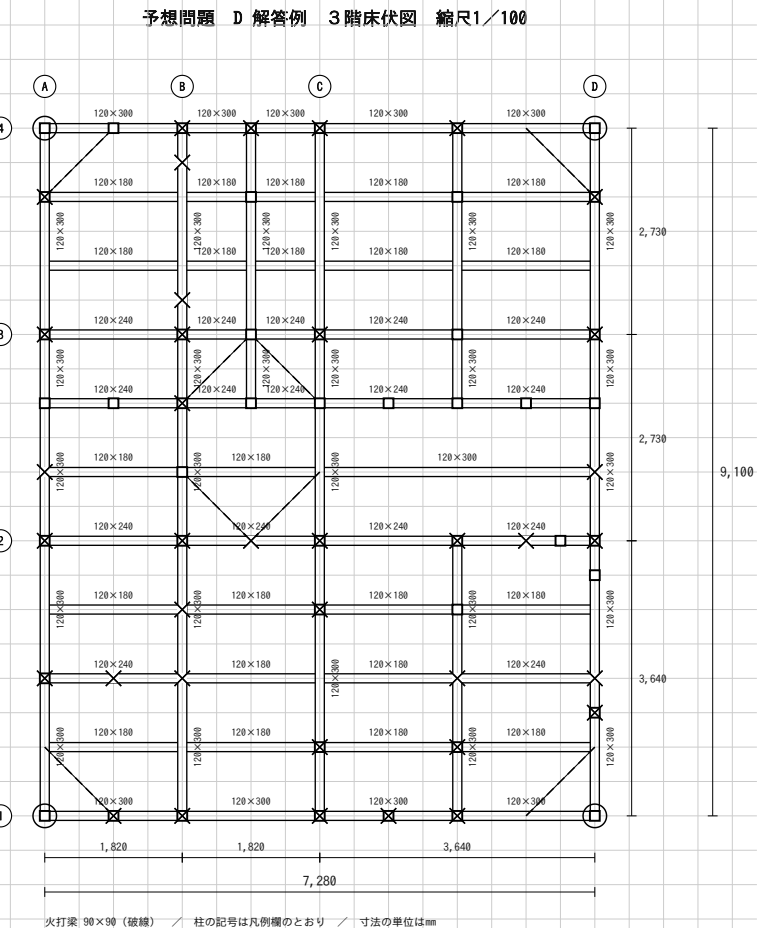

(4) 小屋伏図

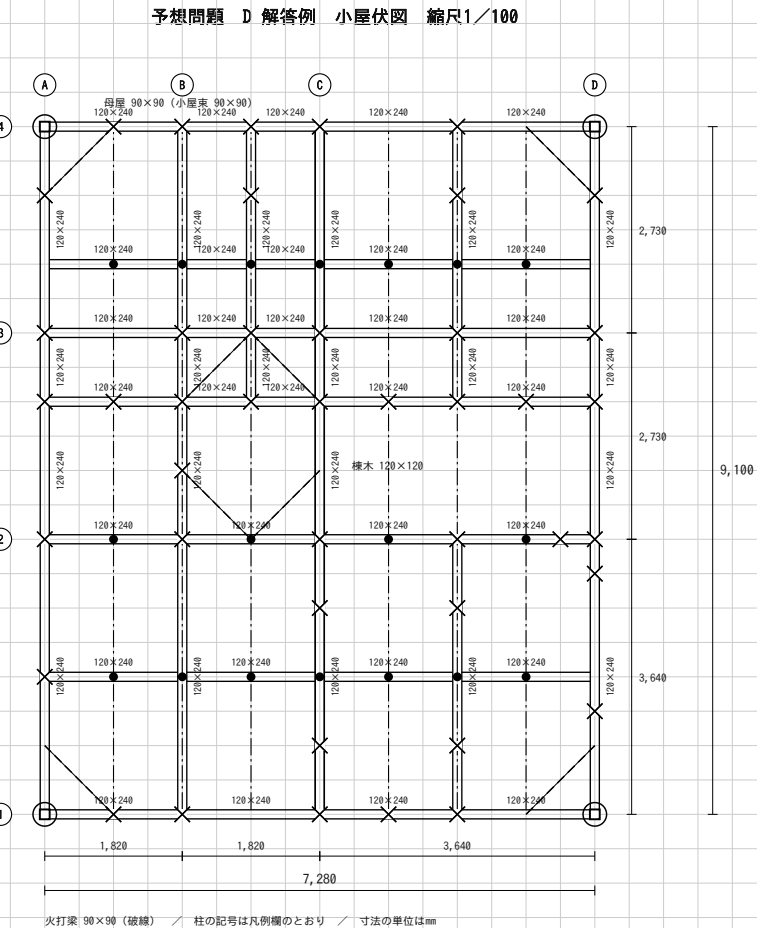


(6) 部分詳細図 (断面) (目盛10mm)

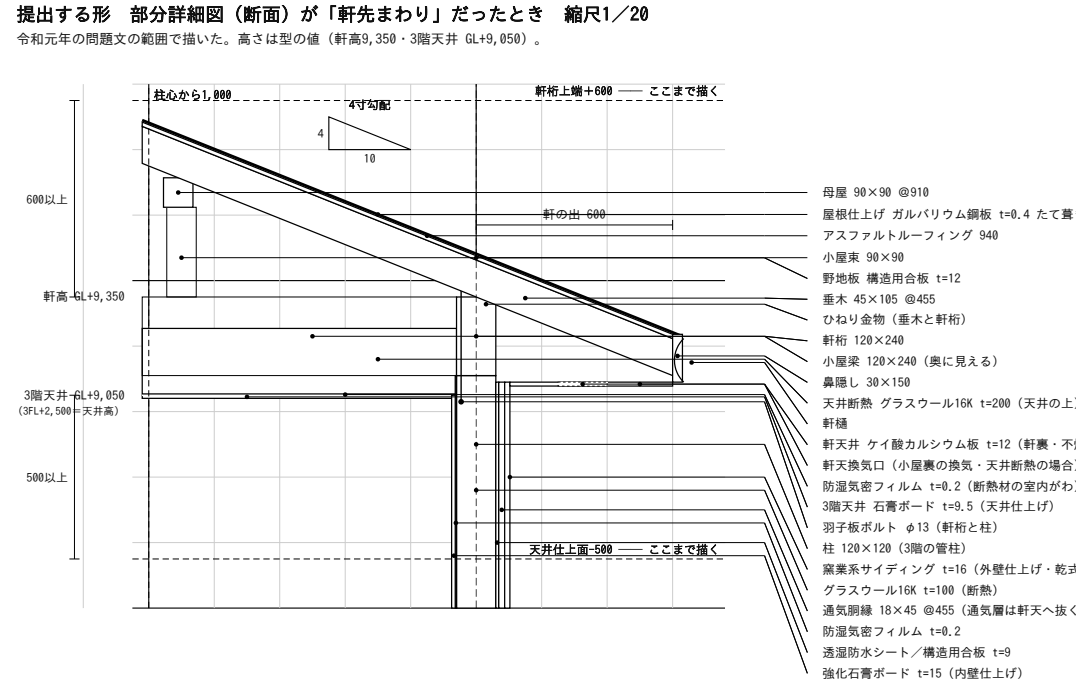

★ 令和元年の要求：屋根の勾配／主要部の寸法／軒桁・小屋梁・母屋・垂木の名称と断面寸法／羽子板ボルト等の金物／
屋根（天井）と外壁の断熱・防湿／屋根・外壁・内壁・天井の仕上材料名／外壁は乾式工法。
★ 高層・土台・1階の床は出てこない。かわりに屋根の裏（墨木→野地板→ルーフィング→仕上げ）を4つ順に書く。

(5) 東側立面図

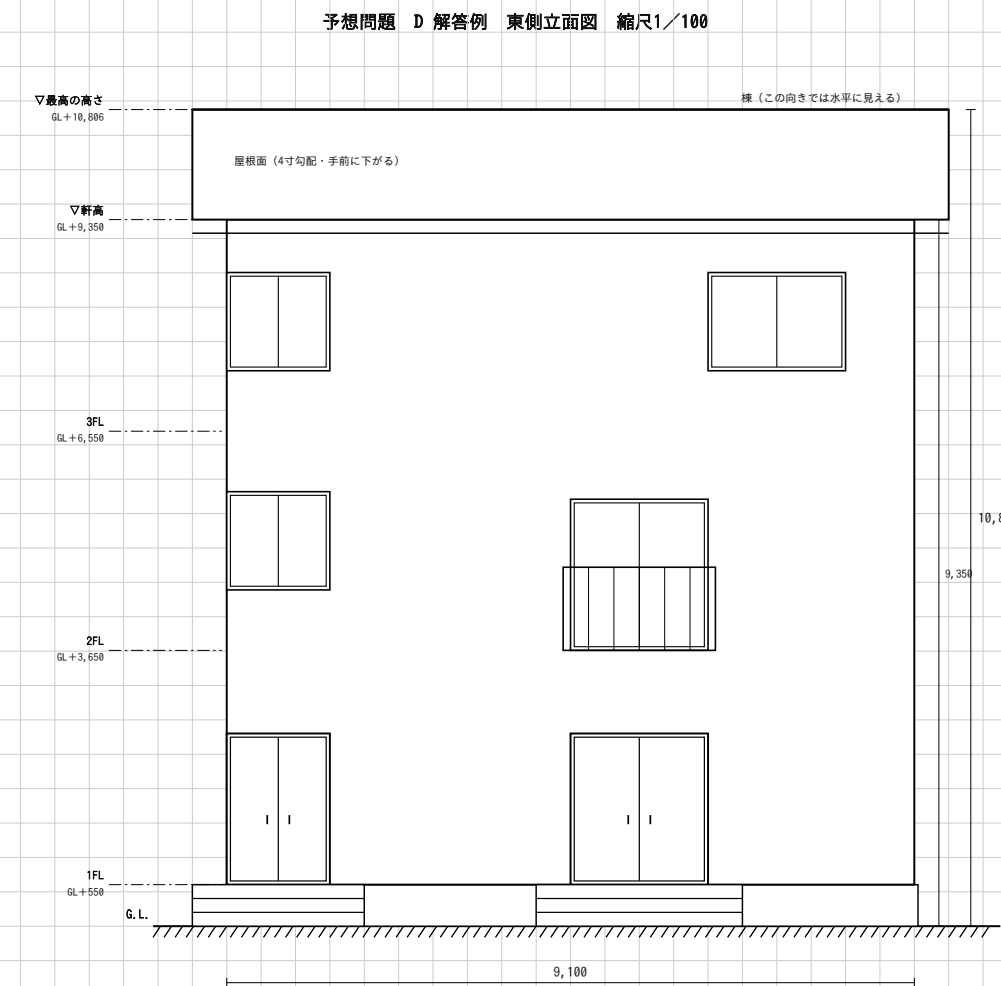

(7) 面積表

敷地面積		180.00㎡
建築面積	(計算式) 7.28×9.10	66.24㎡
床面積 1階 ア	(計算式) 7.28×9.10	66.24㎡
2階 イ	(計算式) 7.28×9.10	66.24㎡
3階 ウ	(計算式) 7.28×9.10	66.24㎡
延べ面積 ア+イ+ウ		198.72㎡

※ 小数点以下第3位以下は切り捨て。計算式はm単位。

凡 例 (床伏図兼小屋伏図の表示記号)

通し柱	1階の管柱	2階の管柱	重なる管柱 胴差・桁 (正角材)	同上 (平角材)	同上 (丸太材)	火打梁	棟木	母屋・小屋束
記号								
寸法	120×120	120×120	120×120	—	120×120	図中に記入	図中に記入	90×90

※ 平角材 (120×240 など) の断面寸法は、床伏図の中の梁1本ずつのわきに記入する。

標準解答例

受験番号

氏名

予想問題 D 東側道路の併用住宅 (美容室)

木造3階建て / 8マス × 10マス (7,280 × 9,100)