




(1) 1階平面図 兼 配置図 縮尺1／100 (目盛4.55mm)

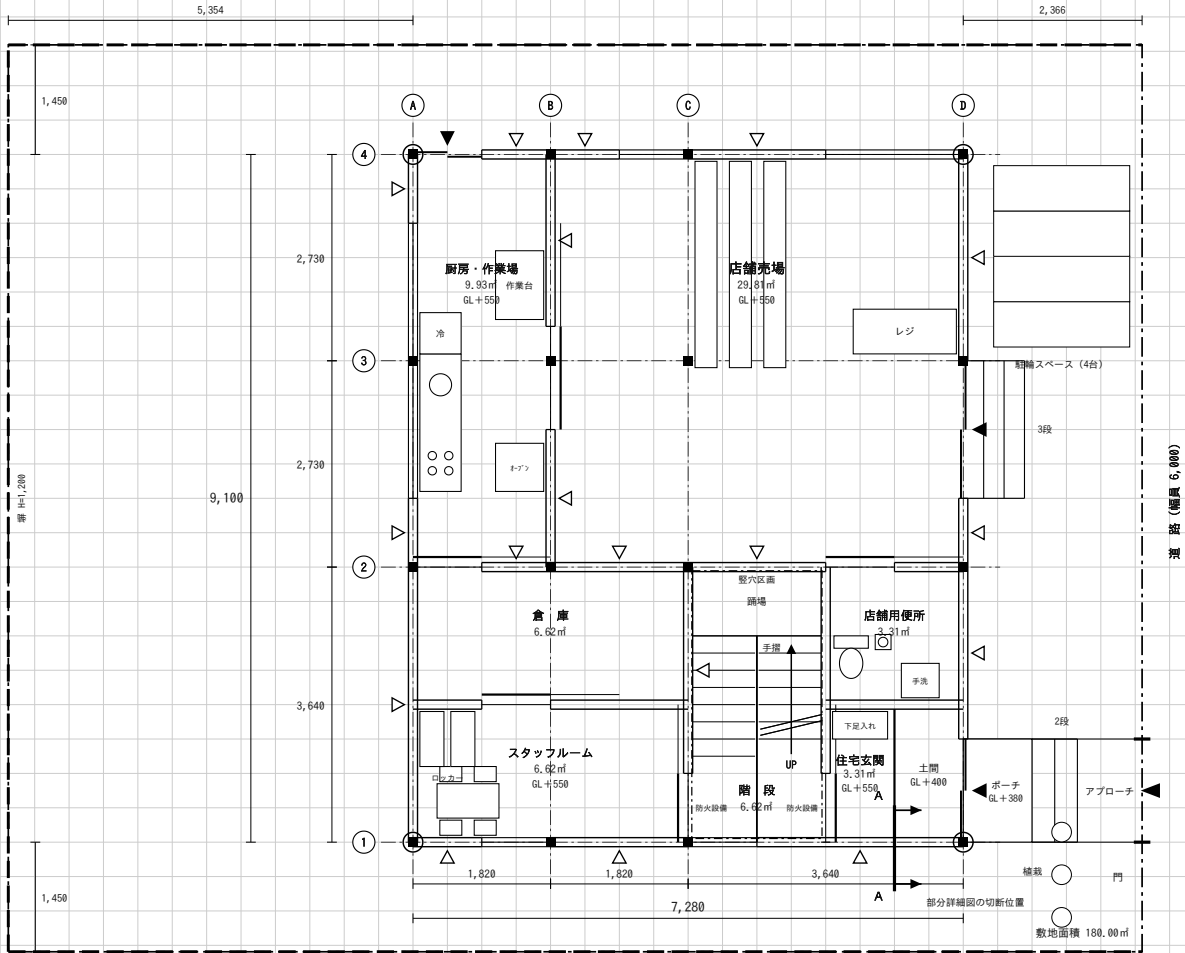


(2) 2階平面図 縮尺1／100 (目盛4.55mm)

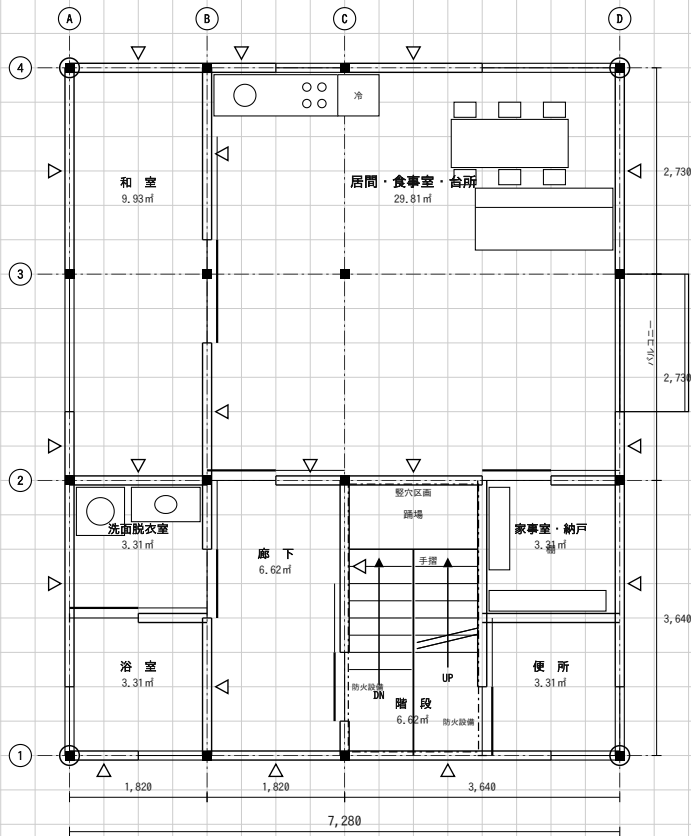

(3) 3階平面図 縮尺1／100 (目盛4.55mm)

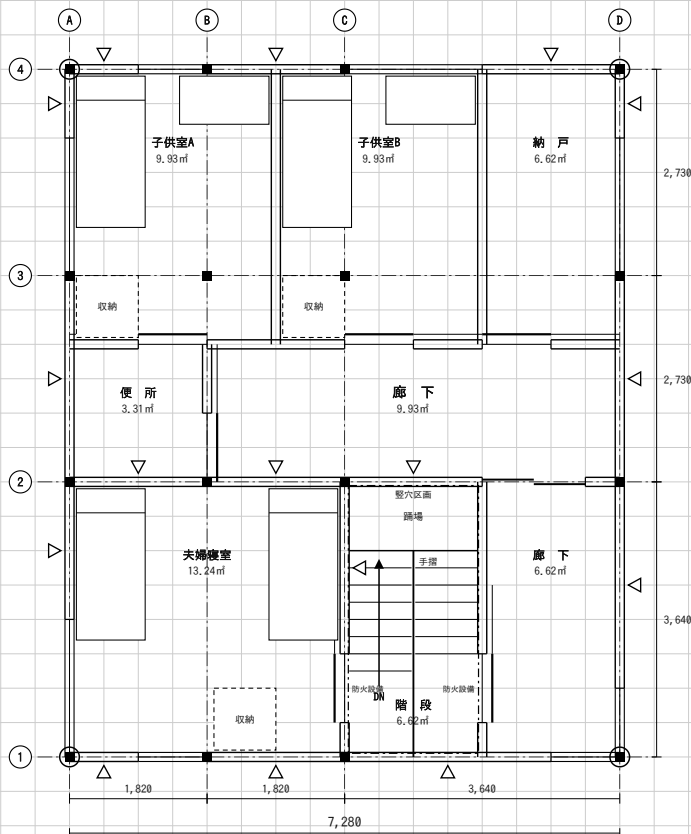

(5) 東側立面図

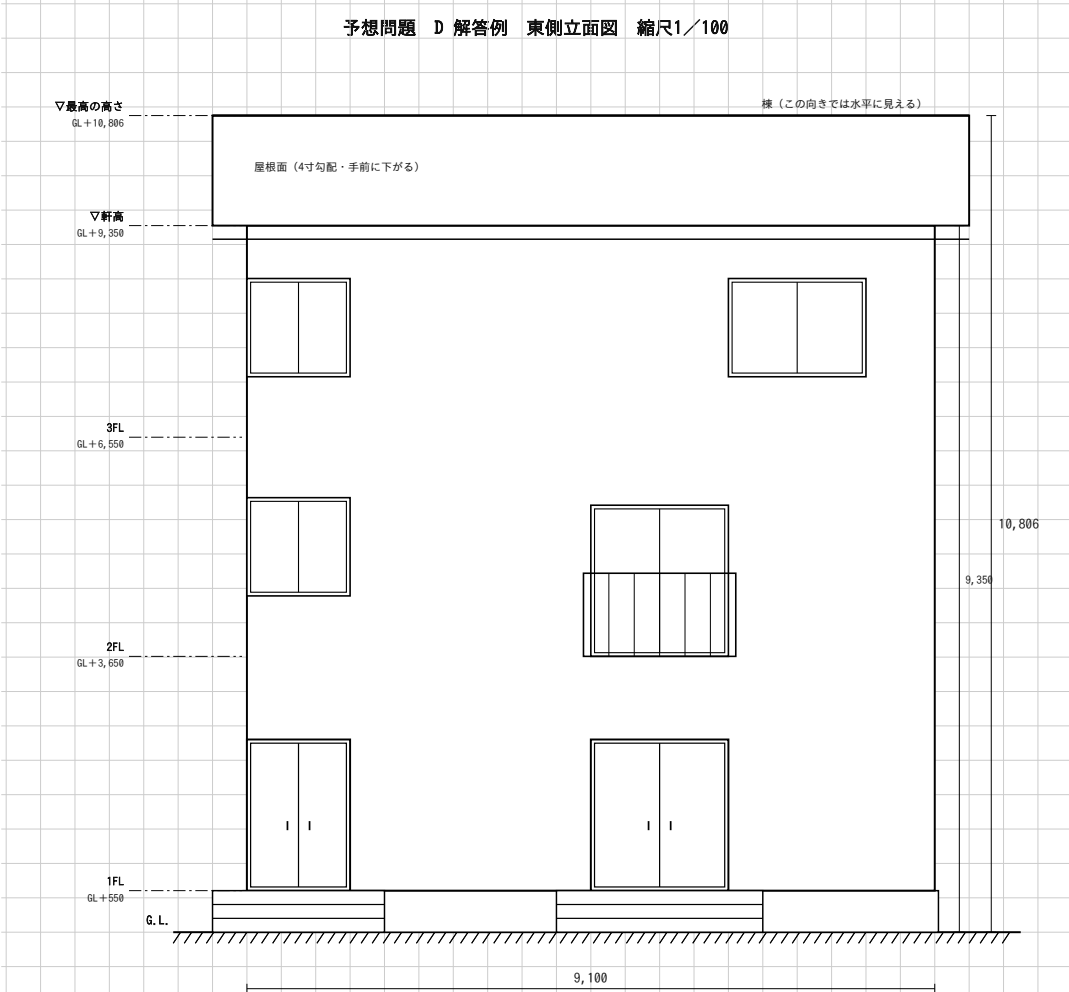

(7) 面積表

敷地面積		180.00	㎡
建築面積	(計算式) 7.28×9.10	66.24	㎡
床面積 1階 ア	(計算式) 7.28×9.10	66.24	㎡
2階 イ	(計算式) 7.28×9.10	66.24	㎡
3階 ウ	(計算式) 7.28×9.10	66.24	㎡
延べ面積 ア+イ+ウ		198.72	㎡



※ 小数点以下第3位以下は切り捨て。計算式は㎡単位。

凡 例 (床伏図兼小屋伏図の



通し柱	1階の管柱	2階の管柱
記号		
寸法	120×120	120×120

※ 平角材 (120×240 など) の断面寸法は、床伏

(4) 3階床伏図

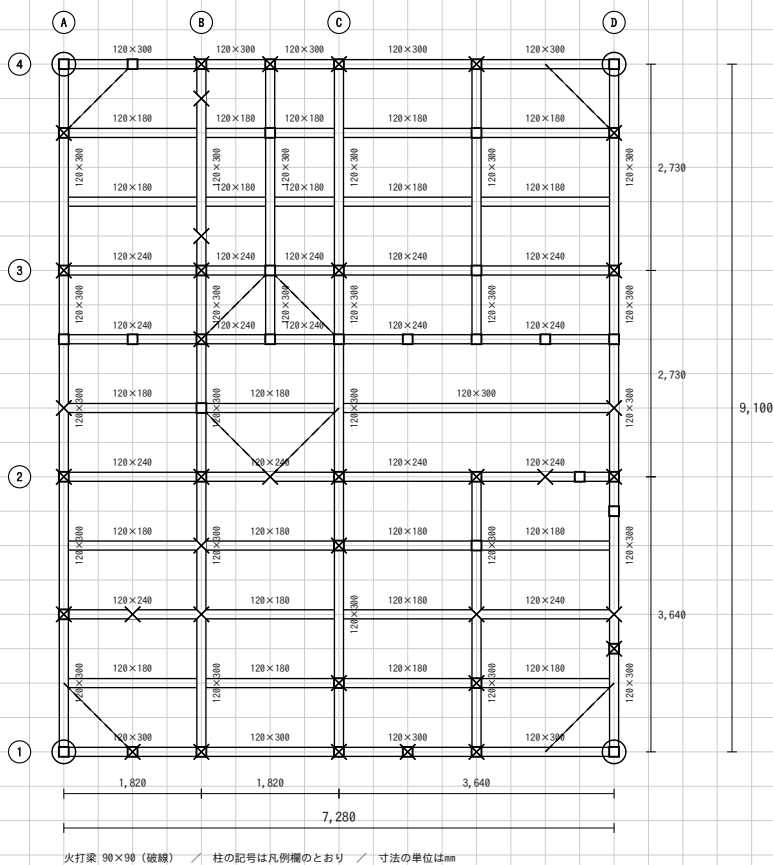 

(4) 小屋伏図

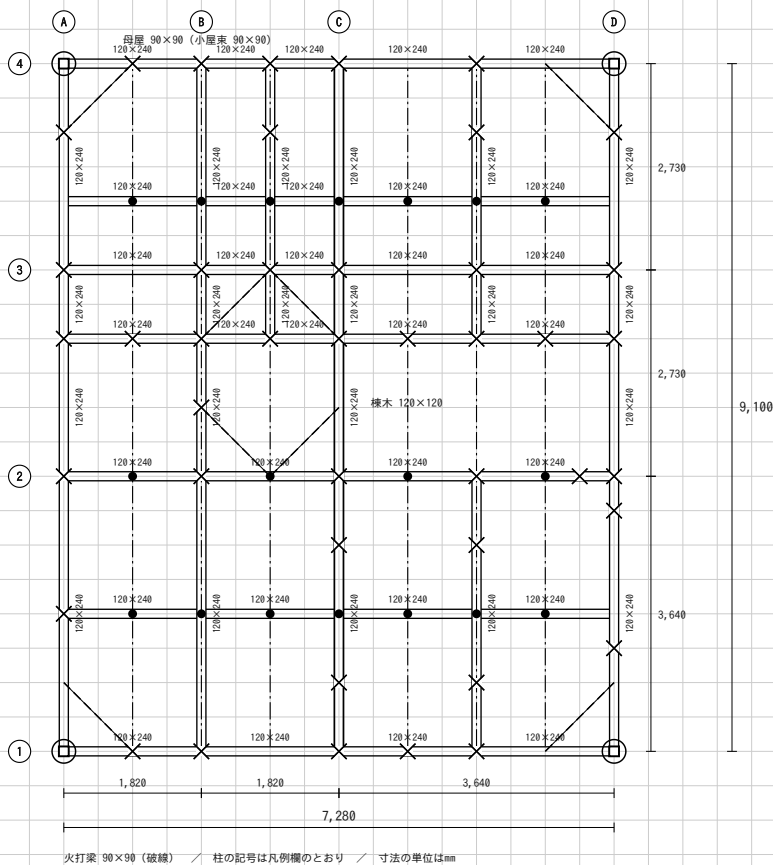 

(8) 計画の要点等

① 東側道路に対して、平面計画上工夫した点

② 階段の位置と直下率について工夫した点

③ 店舗部分と住宅部分の動線計画について工夫した点


※ 解答例の本文は別紙「計画の要点等（記述だい）」に

※ 解答例の本文は別紙「計画の要点等（記述だけ）」に

(6) 部分詳細図 (断面) (目盛10mm)

提出する形 部分詳細図（断面）が「軒先まわり」だったとき 縮尺1/20

令和元年の問題文の範囲で描いた。高さは型の値（軒高9,350・3階天井 GL+9,050）。


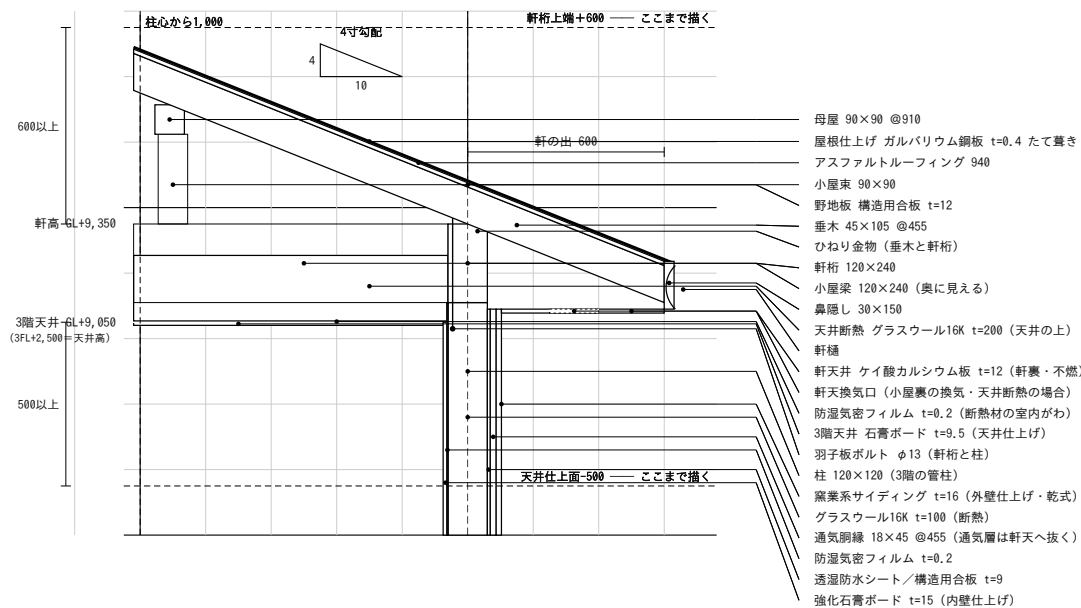


★ 令和元年の要求：屋根の勾配／主要部の寸法／軒桁・小屋梁・母屋・垂木の名称と断面寸法／羽子板ボルト等の金物／

屋根（天井）と外壁の断熱・防湿／屋根・外壁・内壁・天井の仕上材料名／外壁は乾式工法。

★ 基礎・土台・1階の床は出てこない。かわりに屋根の層（垂木→野地板→ルーフィング→仕上げ）を4つ順に書く。

○表示記号)

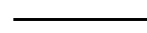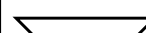重なる管柱	差・桁（正角材）	同上（平角材）	同上（丸太材）	火打梁	棟木	母屋・小屋束
						
—	120×120	図中に記入	図中に記入	90×90	120×120	90×90

図の中の梁1本ずつのわきに記入する。

標準解答例

受験番号	氏名
------	----

予想問題 D 東側道路の併用住宅（美容室）

木造3階建て / 8マス × 10マス (7,280 × 9,100)