




(1) 1階平面図 兼 配置図 縮尺1／100 (目盛4.55mm)

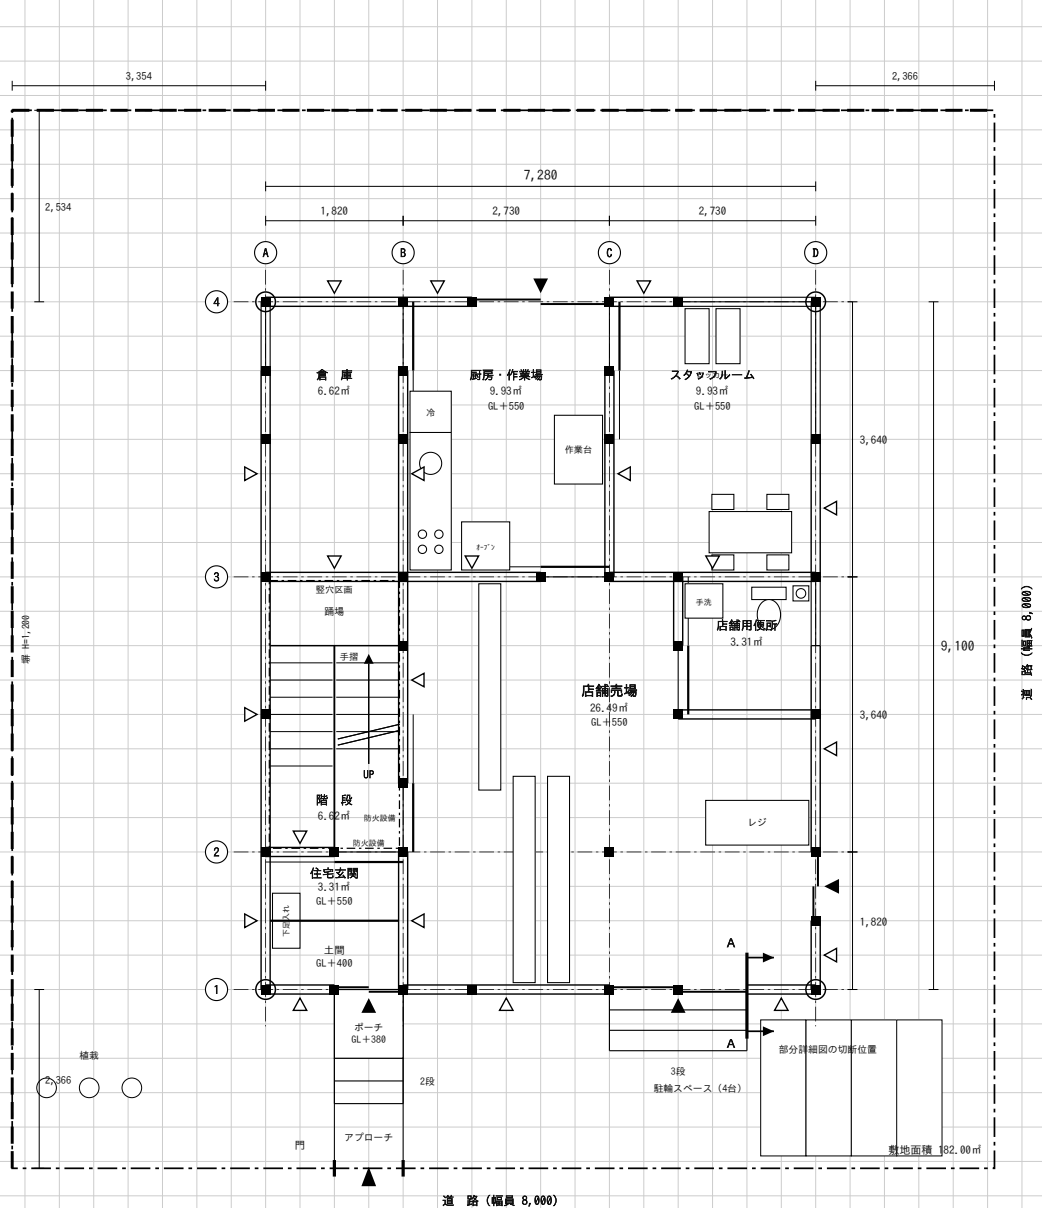


(2) 2階平面図 縮尺1／100 (目盛4.55mm)

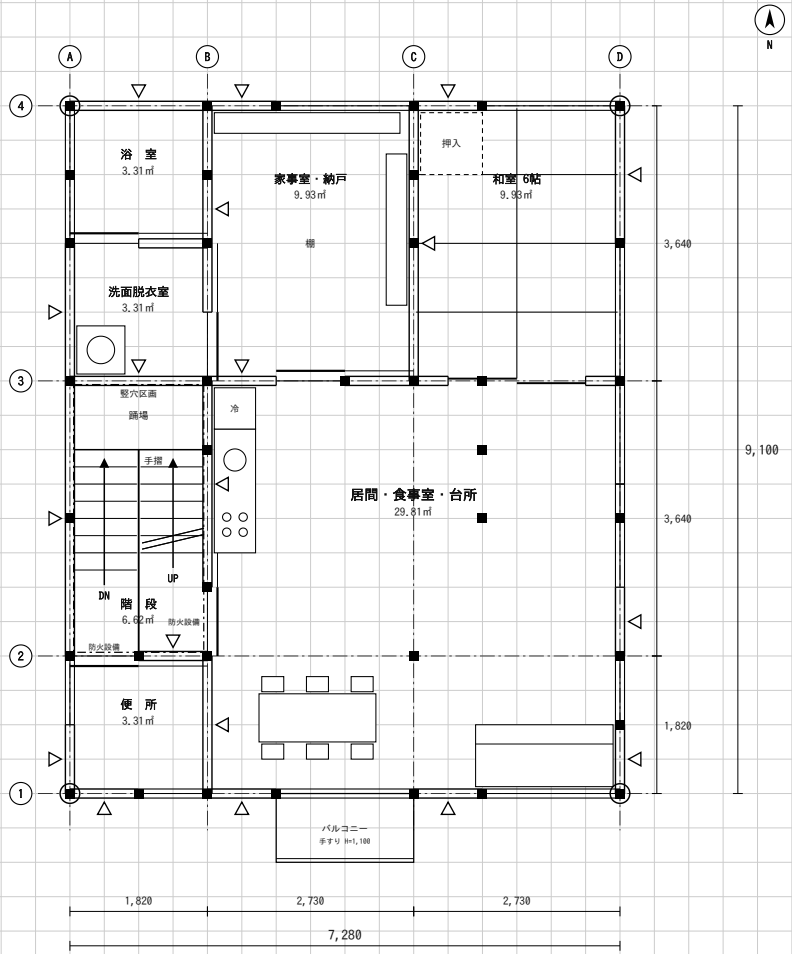


(3) 3階平面図 縮尺1／100 (目盛4.55mm)

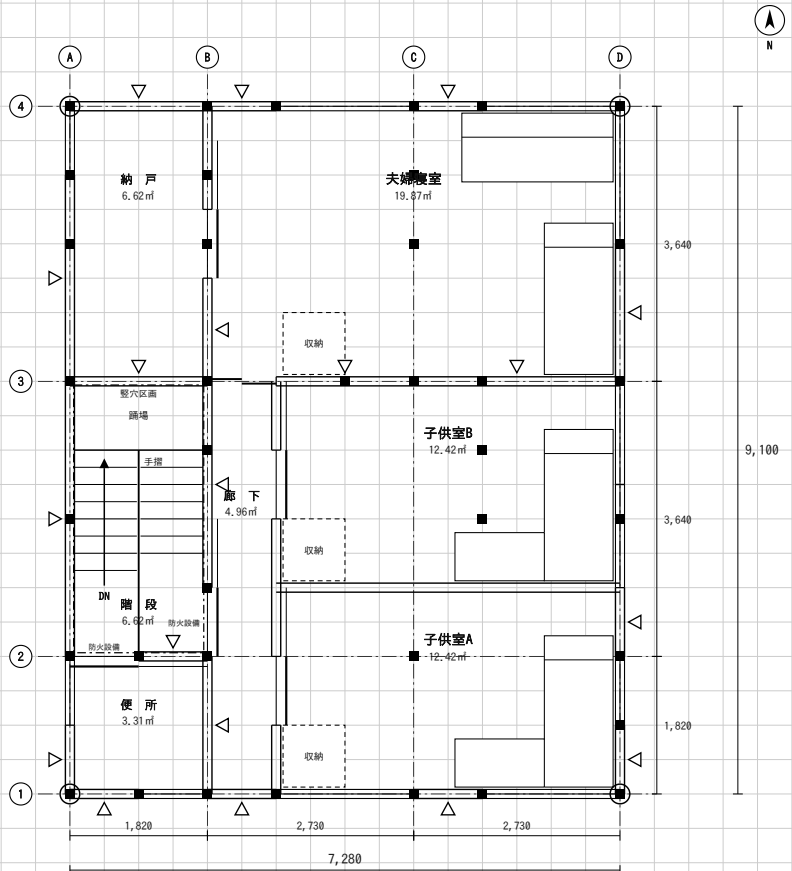

(4) 3階床伏図

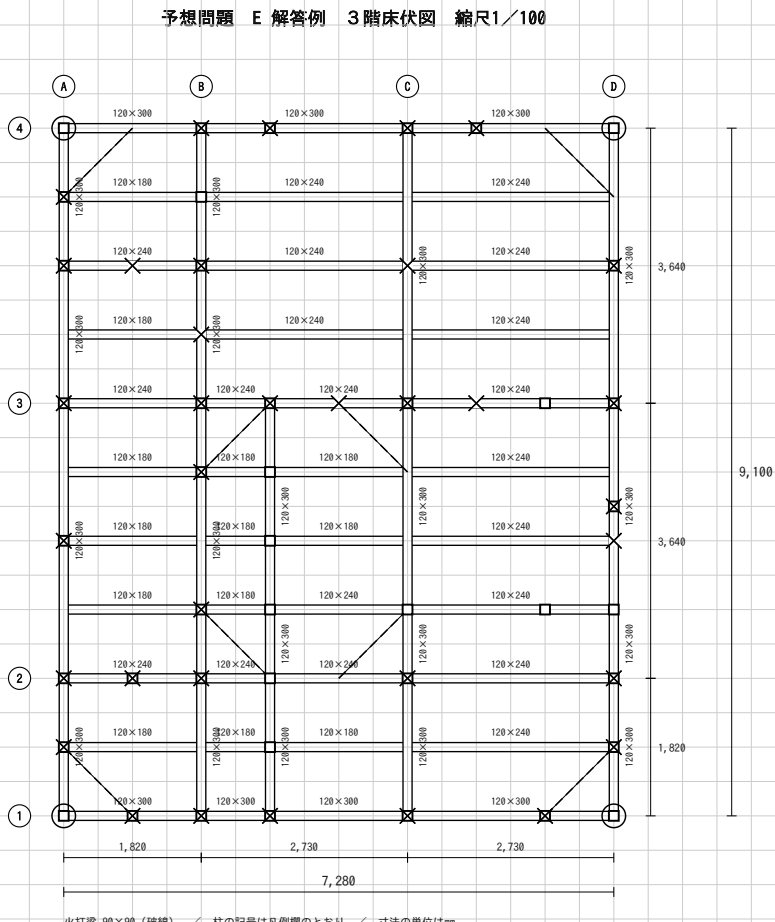

(4) 小屋伏図

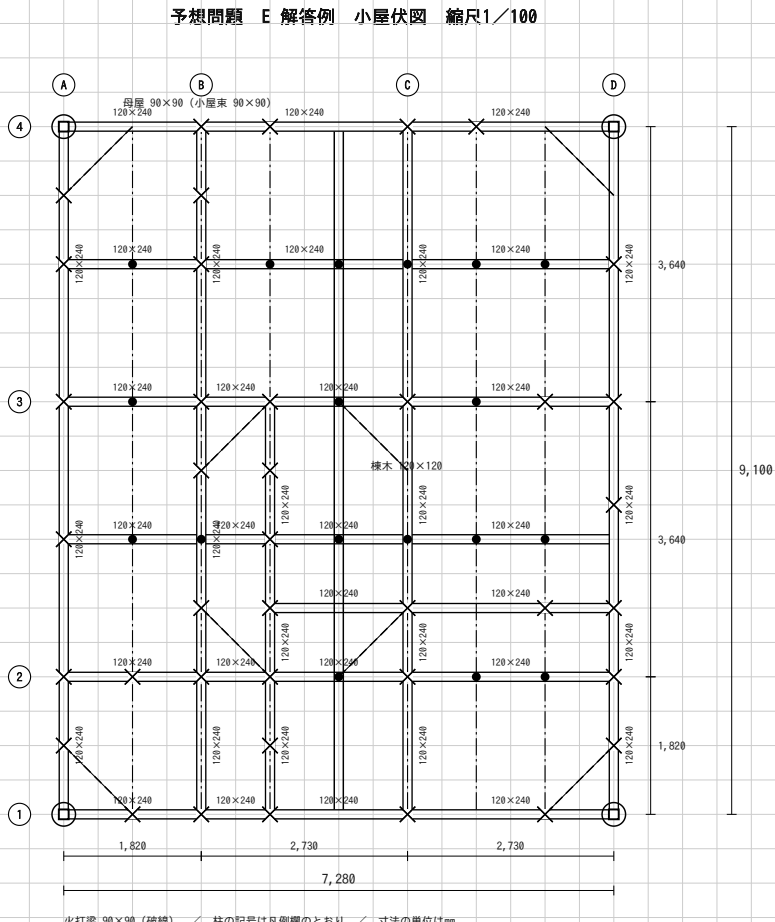


(8) 計画の要点等


- ① 角地であることを活かして工夫した点
- ② 容積率及び建蔽率の算定について
- ③ 防火及び避難について配慮した点

※ 解答例の本文は別紙「計画の要点等」(記述だけ)にて

(6) 部分詳細図 (断面) (目盛10mm)

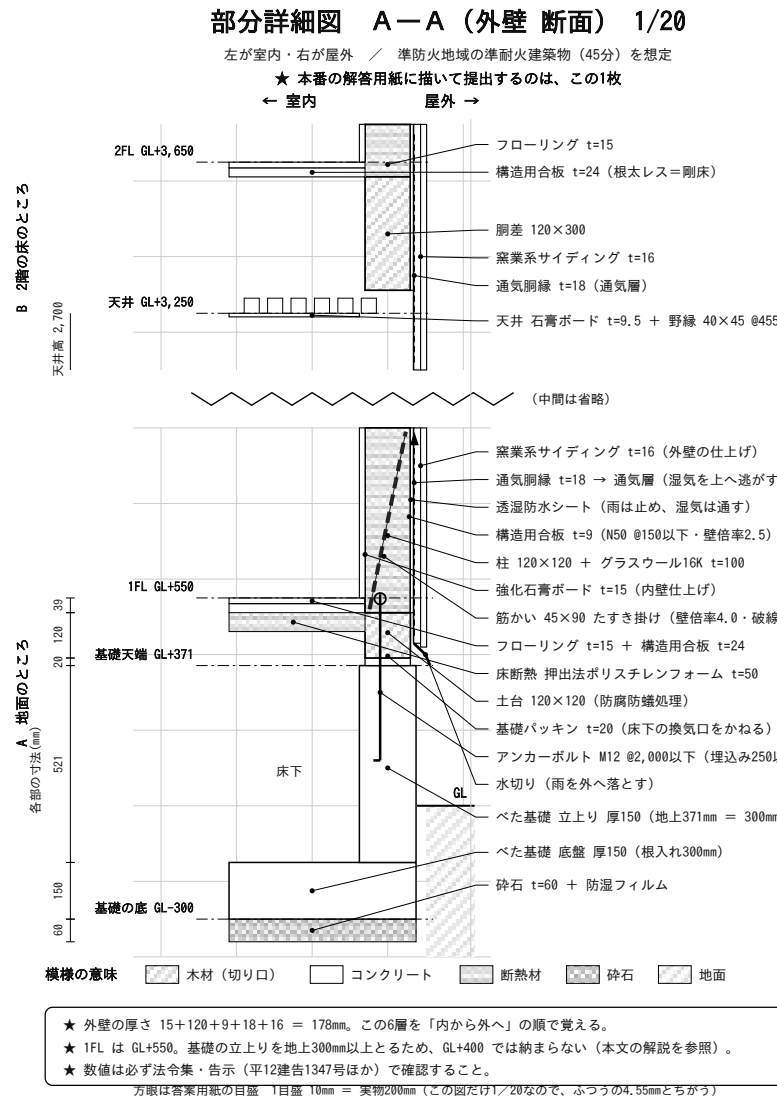

(5) 南側立面図

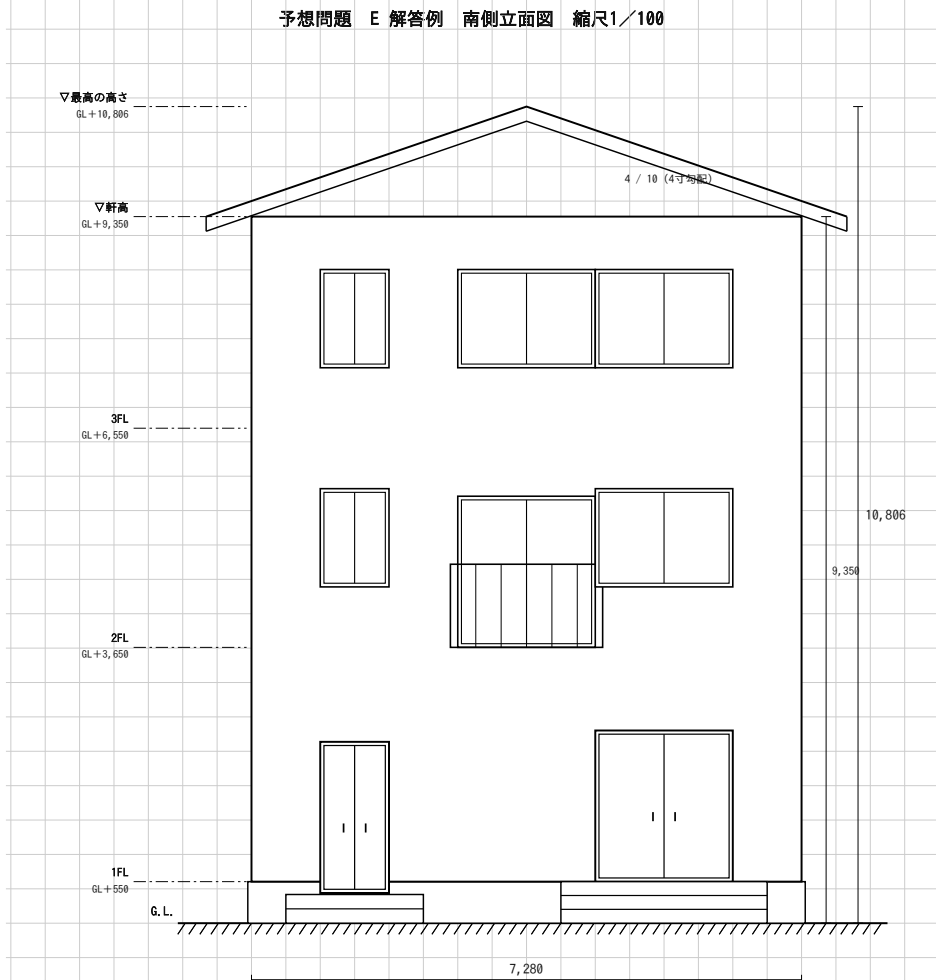

(7) 面積表

|            |                 |          |
|------------|-----------------|----------|
| 敷地面積       |                 | 182.00 ㎡ |
| 建築面積       | (計算式) 7.28×9.10 | 66.24 ㎡  |
| 床面積 1階 ア   | (計算式) 7.28×9.10 | 66.24 ㎡  |
| 2階 イ       | (計算式) 7.28×9.10 | 66.24 ㎡  |
| 3階 ウ       | (計算式) 7.28×9.10 | 66.24 ㎡  |
| 延べ面積 ア+イ+ウ |                 | 198.72 ㎡ |

※ 小数点以下第3位以下は切り捨て。計算式はm単位。

凡 例 (床伏図兼小屋伏図の表示記号)

| 通し柱 | 1階の管柱   | 2階の管柱   | 重なる管柱 胴差・桁 (正角材) | 同上 (平角材) | 同上 (丸太材) | 火打梁   | 棟木    | 母屋・小屋束 |
|-----|---------|---------|------------------|----------|----------|-------|-------|--------|
| 記号  |         |         |                  |          |          |       |       |        |
| 寸法  | 120×120 | 120×120 | 120×120          | —        | 120×120  | 図中に記入 | 図中に記入 | 90×90  |

※ 平角材 (120×240 など) の断面寸法は、床伏図の中の梁1本ずつのわきに記入する。

## 標準解答例

受験番号

氏名

予想問題 E 南東の角地に建つ併用住宅 (パン店)

木造3階建て / 8マス × 10マス (7,280 × 9,100)