


(2) 2階平面図 縮尺1/100 (目盛4.55mm)

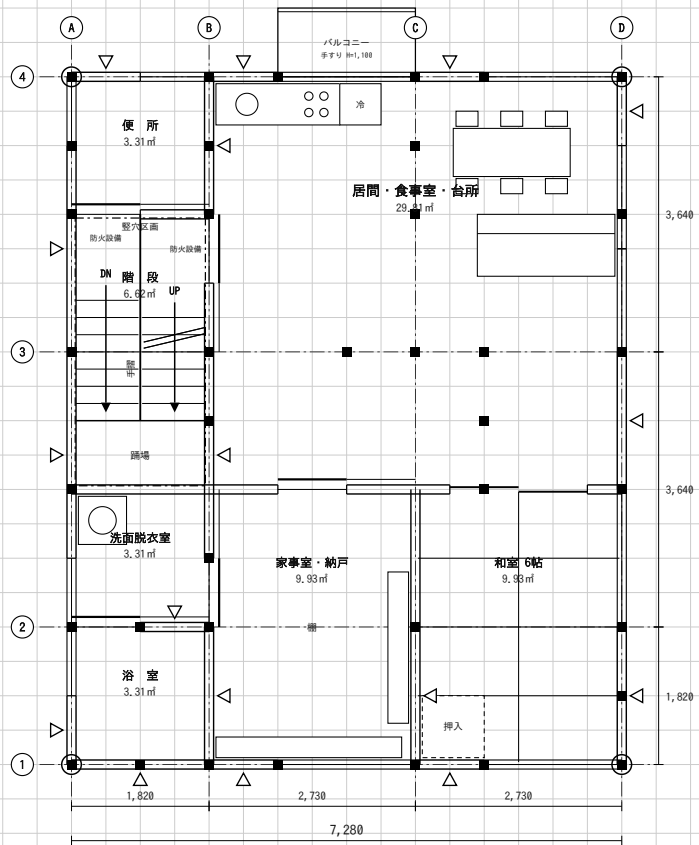

1F

便所 3.31㎡

廊下 4.96㎡

階段 5.62㎡

子供室A 12.42㎡

子供室B 12.42㎡

夫婦寝室 19.87㎡

納戸 6.62㎡

1,820 2,730 2,730 7,280

11,820


凡 例（床伏図兼小屋伏図の

通し柱	1階の管柱	2階の管柱
		
120×120	120×120	120×120

※ 平角材 (120×240 など) の断面寸法は、床伏


(4) 3階床伏図

予想問題 F 解答例 3階床伏図 縮尺1／100

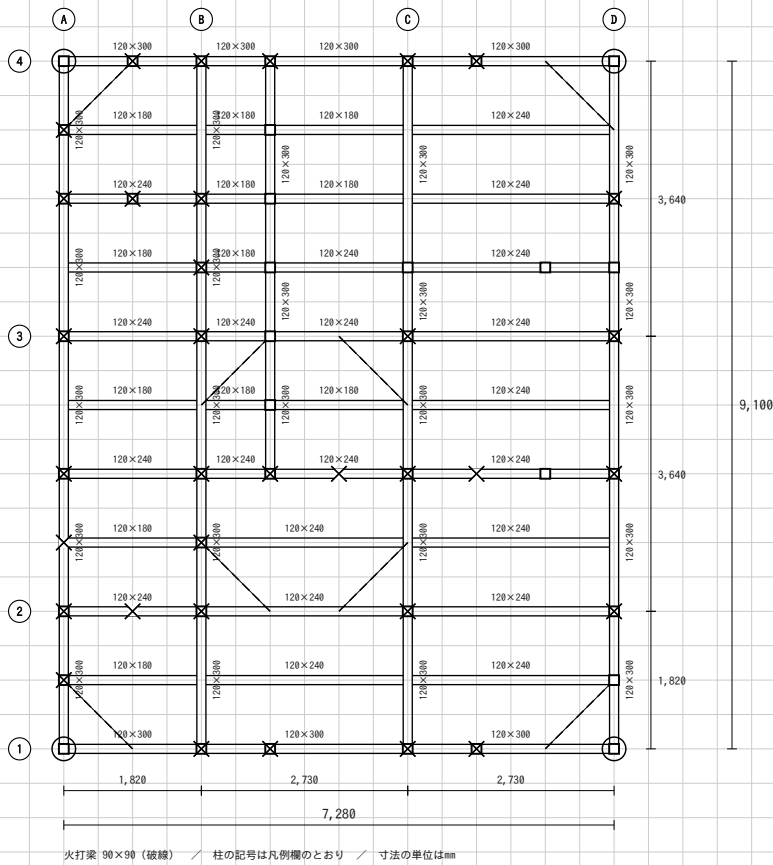

(4) 小屋伏図

予想問題 F 解答例 小屋伏図 縮尺1／100

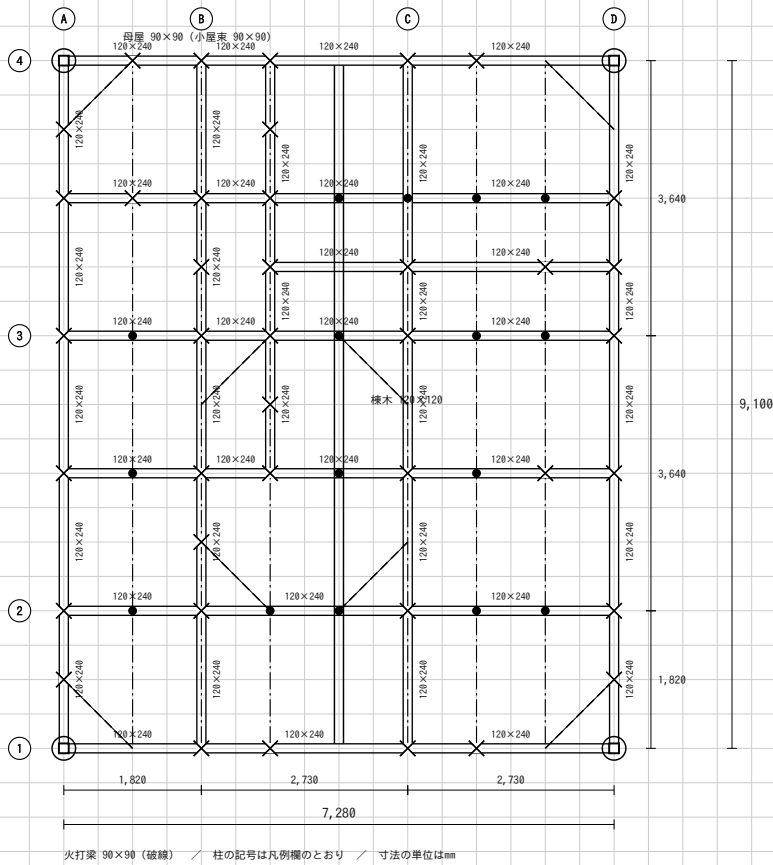

(8) 計画の要点等

① 北側道路に対して、住宅部分の日照をどのように確保したか

② 階段の位置について工夫した点

③ 防火及び避難について配慮した点

※ 解答例の本文は別紙「計画の要点等（記述だけ）」に


(6) 部分詳細図（断面） （目盛10mm）

部分詳細図 A－A（外壁 断面） 1/20

左が室内・右が屋外 ／ 準防火地域の準耐火建築物（45分）を想定

★ 本番の解答用紙に描いて提出するのは、この1枚

← 室内 屋外 →

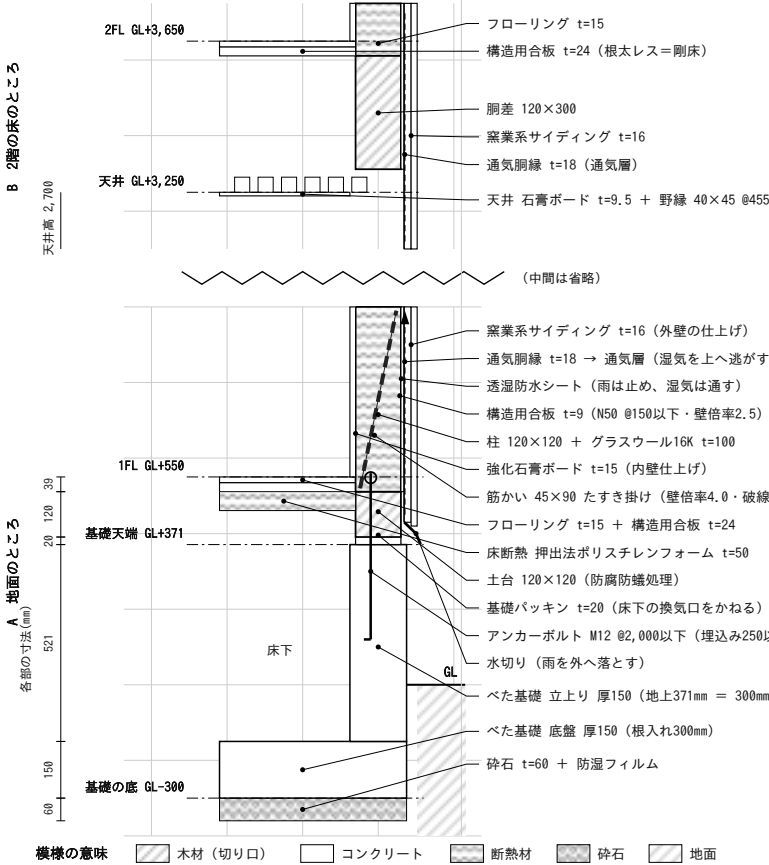

- ★ 外壁の厚さ 15+120+9+18+16 = 178mm。この6層を「内から外へ」の順で覚える。
- ★ 1FL は GL+550。基礎の立上りを地上300mm以上とるため、GL+400 では納まらない（本文の解説を参照）。
- ★ 数値は必ず法令集・告示（平12建告1347号ほか）で確認すること。

万眼は答案用紙の目盛 1目盛 10mm = 実物200mm（この図だけ1／20なので、ふつうの4.55mmとちがう）

標準解答例

受験番号	氏名
------	----

予想問題 F 北側道路の併用住宅（書店）
木造3階建て ／ 8マス × 10マス（7,280 × 9,100）

図の中の梁1本ずつのわきに記入する。