

設計課題 「商店街に建つ併用住宅（木造3階建て）」

問題用紙 予想問題C 間口の狭い敷地

1. 設計条件

- ある地方都市の商店街において、パン屋を営む夫婦とその子ども2人が住むための併用住宅を計画する。
- 計画に当たっては、次の①～③に特に留意する。
- ① 間口が狭い敷地であることを踏まえた平面計画とする。
  - ② 奥行きが深い店舗売場の採光及び通風に配慮する。
  - ③ 店舗部分と住宅部分の動線が交錯しないようにする。

(1) 敷地

- ア. 形状、道路との関係、方位等は、下に示す敷地図のとおりである。
- イ. 近隣商業地域内にあり、準防火地域に指定されている。
- ウ. 建蔽率の限度は80%、容積率の限度は300%である。
- エ. 地形は平坦で、道路及び隣地との高低差はなく、地盤は良好である。
- オ. 電気、都市ガス、上水道及び公共下水道は完備している。

(2) 構造、階数、建築物の高さ等

- ア. 木造3階建てとする。
- イ. 建築物の最高の高さは11m以下、かつ、軒の高さは9.5m以下とする。
- ウ. 耐力壁（構造耐力上有効な壁）は、必要な量をバランスよく配置する。

(3) 延べ面積等

- ア. 延べ面積は、「180㎡以上、200㎡以下」とする。
- イ. 玄関ポーチ、バルコニー、駐輪スペース等は、床面積に算入しない。

(4) 人員構成等

- 夫婦（40歳代）、子ども2人（中学生、小学生）

(5) 要求室等

- 下表の全ての室等は、指定された設置階に計画する。


| 設置階 | 室名等       | 特記事項                                                                                        |
|-----|-----------|---------------------------------------------------------------------------------------------|
| 1階  | 店舗売場      | ア. 25㎡以上とする。<br>イ. 道路に面して出入口を設ける。<br>ウ. 陳列棚及びレジカウンターを設ける。                                   |
|     | 厨房・作業場    | ア. 9㎡以上とする。<br>イ. 店舗売場に隣接させ、直接行き来できるようにする。<br>ウ. 流し台、調理台、作業台及びオープンを設ける。                     |
|     | スタッフルーム   | ア. 6㎡以上とする。<br>イ. 従業員の更衣及び休憩に使用する。                                                          |
|     | 店舗用便所     | ア. 来客が利用できるものとする。<br>イ. 洋式便器及び手洗い器を設ける。                                                     |
|     | 倉庫        | ・商品及び材料を保管する。                                                                               |
|     | 玄関        | ア. 住宅部分の玄関とし、道路から直接出入りできるものとする。<br>イ. 下足入れを設ける。                                             |
| 2階  | 居間・食事室・台所 | ア. 1室にまとめ、25㎡以上として計画する。<br>イ. ソファ、テーブル及び椅子（計4席以上）を設ける。<br>ウ. 台所設備機器（流し台・調理台・コンロ台・冷蔵庫等）を設ける。 |
|     | 和室        | ア. 6畳以上とする。<br>イ. 居間に隣接させ、直接行き来できるようにする。<br>ウ. 押入れを設ける。                                     |
|     | 浴室・洗面脱衣室  | ・浴室には浴槽、洗面脱衣室には洗面台及び洗濯機を設ける。                                                                |
|     | 便所        | ・洋式便器を設ける。                                                                                  |
|     | 家事室       | ・納戸を兼ねてもよい。                                                                                 |
| 3階  | 夫婦寝室      | ア. 13㎡以上とする。<br>イ. 洋室とし、ベッド（計2台）及び収納を設ける。                                                   |
|     | 子ども室      | ア. 2室（各8㎡以上）設け、いずれも同じ広さとする。<br>イ. いずれも洋室とし、ベッド、机及び収納を設ける。                                   |
|     | 便所        | ・洋式便器を設ける。                                                                                  |
|     | 納戸        |                                                                                             |

- （注1）各要求室等においては、床面積・広さの指定がない場合、床面積は適宜とする。
- （注2）階段は、安全を確保するために、踊場を設ける。

(6) 屋外施設等

- 屋外に下表のものを計画する。

|         |           |
|---------|-----------|
| 駐輪スペース  | ・4台分を設ける。 |
| 門・塀・植栽等 |           |

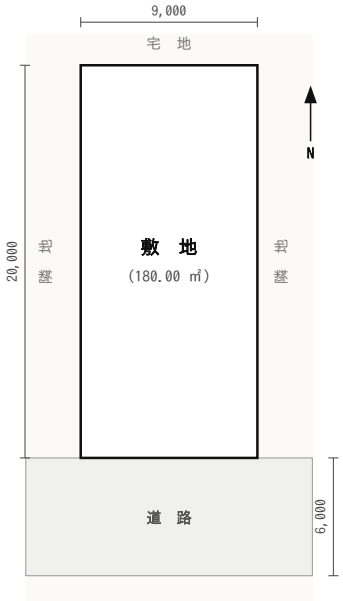

2. 要求図書

- ・a. 答案用紙の定められた枠内に、下表の要求図書を記入する。（寸法線は、枠外にはみだして記入してもよい。）
- ・b. 図面は黒鉛筆仕上げとする。（定規を用いなくてもよい。）
- ・c. 記入寸法の単位は、mmとする。なお、答案用紙の1目盛は、4.55mm（部分詳細図にあつては、10mm）である。
- ・d. シックハウス対策のための機械換気設備等は、記入しなくてもよい。

| 要求図書<br>（ ）内は縮尺                                                                  | 特記事項   |
|----------------------------------------------------------------------------------|---|
| (1) 1階平面図兼配置図<br>（1/100）<br><br>(2) 2階平面図<br>（1/100）<br><br>(3) 3階平面図<br>（1/100） | ア. 1階平面図兼配置図、2階平面図及び3階平面図には、次のものを記入する。<br>・建築物の主要な寸法<br>・室名等<br>・「通し柱」を○印で囲み、「耐力壁」には△印を付ける。<br>・部分詳細図の切断位置及び方向<br>イ. 1階平面図兼配置図には、次のものを記入する。<br>・敷地境界線と建築物との距離<br>・道路から建築物へのアプローチ、駐輪スペース、門、塀、植栽等<br>・道路から敷地及び建築物への出入口には、▲印を付ける。<br>・玄関の土間部分及びポーチの地盤面からの高さ<br>・玄関ホール（廊下）及び店舗売場の床高<br>・店舗売場…陳列棚及びレジカウンター<br>・厨房・作業場…流し台、調理台、作業台及びオープン<br>・店舗用便所…洋式便器及び手洗い器<br>・玄関…下足入れ<br>ウ. 2階平面図には、次のものを記入する。<br>・居間・食事室・台所…ソファ、テーブル、椅子及び台所設備機器<br>・和室…畳及び押入れ<br>・浴室…浴槽／洗面脱衣室…洗面台及び洗濯機／便所…洋式便器<br>エ. 3階平面図には、次のものを記入する。<br>・夫婦寝室…ベッド及び収納<br>・子ども室…ベッド、机及び収納<br>・便所…洋式便器 |
| (4) 床伏図兼小屋伏図<br>（1/100）                                                          | ア. 3階床伏図兼小屋伏図とする。<br>イ. 主要部材（通し柱、各階の管柱、胴差、床梁、桁、小屋梁、火打梁、棟木、母屋、小屋束等必要なもの）については、凡例の表示記号にしたがって記入し、断面寸法（小屋束を除く。）を凡例欄に記入する。<br>ウ. 火打梁の代わりに構造用面材による床組とする場合には、胴差、床梁、桁を記入したうえで、構造用合板の厚さ、釘の種類・打ち付け間隔を明記する。<br>エ. 建築物の主要な寸法を記入する。   |
| (5) 立面図<br>（1/100）                                                               | ア. 南側立面図とする。<br>イ. 建築物の最高の高さを記入する。   |
| (6) 部分詳細図（断面）<br>（1/20）                                                          | ア. 切断位置は、外壁を含む部分とし、開口部を含むものとする。<br>イ. 作図の範囲は、基礎から2階の床までとする。<br>ウ. 主要部の寸法等（床高、天井高、階高、基礎の寸法等）を記入する。<br>エ. 主要部材（基礎、土台、柱、胴差、床梁等必要なもの）の名称・断面寸法を記入する。<br>オ. アンカーボルト等の名称・寸法を記入する。<br>カ. 外壁、床、その他必要と思われる部分の断熱・防湿措置を記入する。<br>キ. 内外の主要な部位（外壁、床、内壁、天井）の仕上材料名を記入する。   |
| (7) 面積表                                                                          | ア. 建築面積、床面積及び延べ面積を記入する。<br>イ. 建築面積及び床面積については、計算式も記入する。<br>ウ. 面積の数値は、小数点以下第2位までとし、第3位以下は切り捨てて。   |
| (8) 計画の要点等                                                                       | ・建築物の計画に関する次の①～③について、具体的に記述する。<br>・① 間口が狭い敷地に対して、平面計画上工夫した点<br>・② 奥行きが深い店舗売場の採光及び通風について工夫した点<br>・③ 木造3階建てとするに当たり、構造計画上工夫した点   |

※ この問題用紙は、公表されている過去問（令和4～7年）の様式にならって作成した予想問題です。本物の試験問題ではありません。

【注意事項】試験問題を十分に読んだうえで、「設計製図の試験」に臨むようにしてください。なお、建築基準法等の関係法令や要求図書、主要な要求室等の計画等の設計と条件に  
対して解答内容が不十分な場合には、「設計条件・要求図書に対する重大な不適合」と判断されます。

下書欄（目盛4.55mm）