
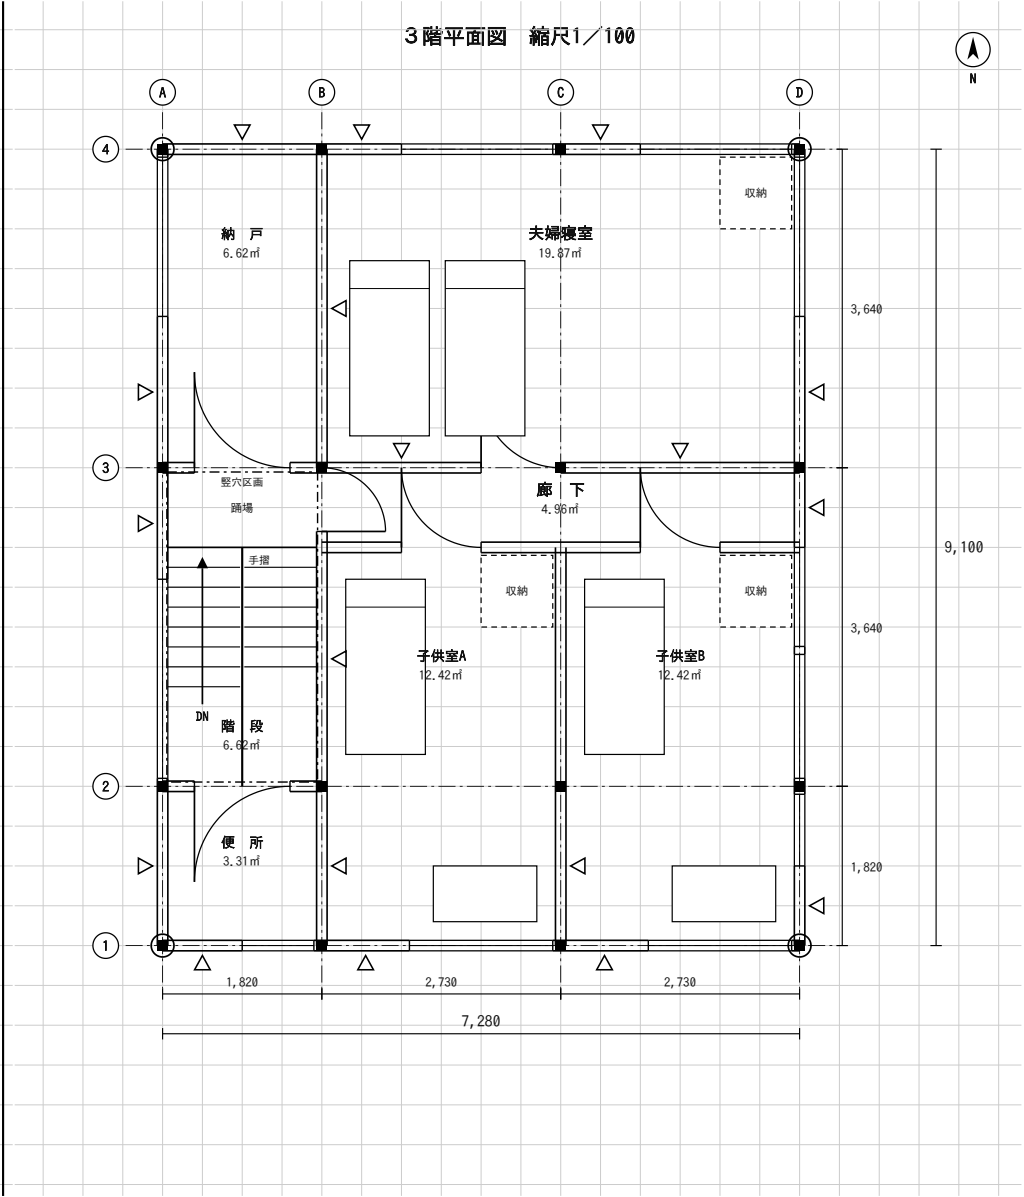
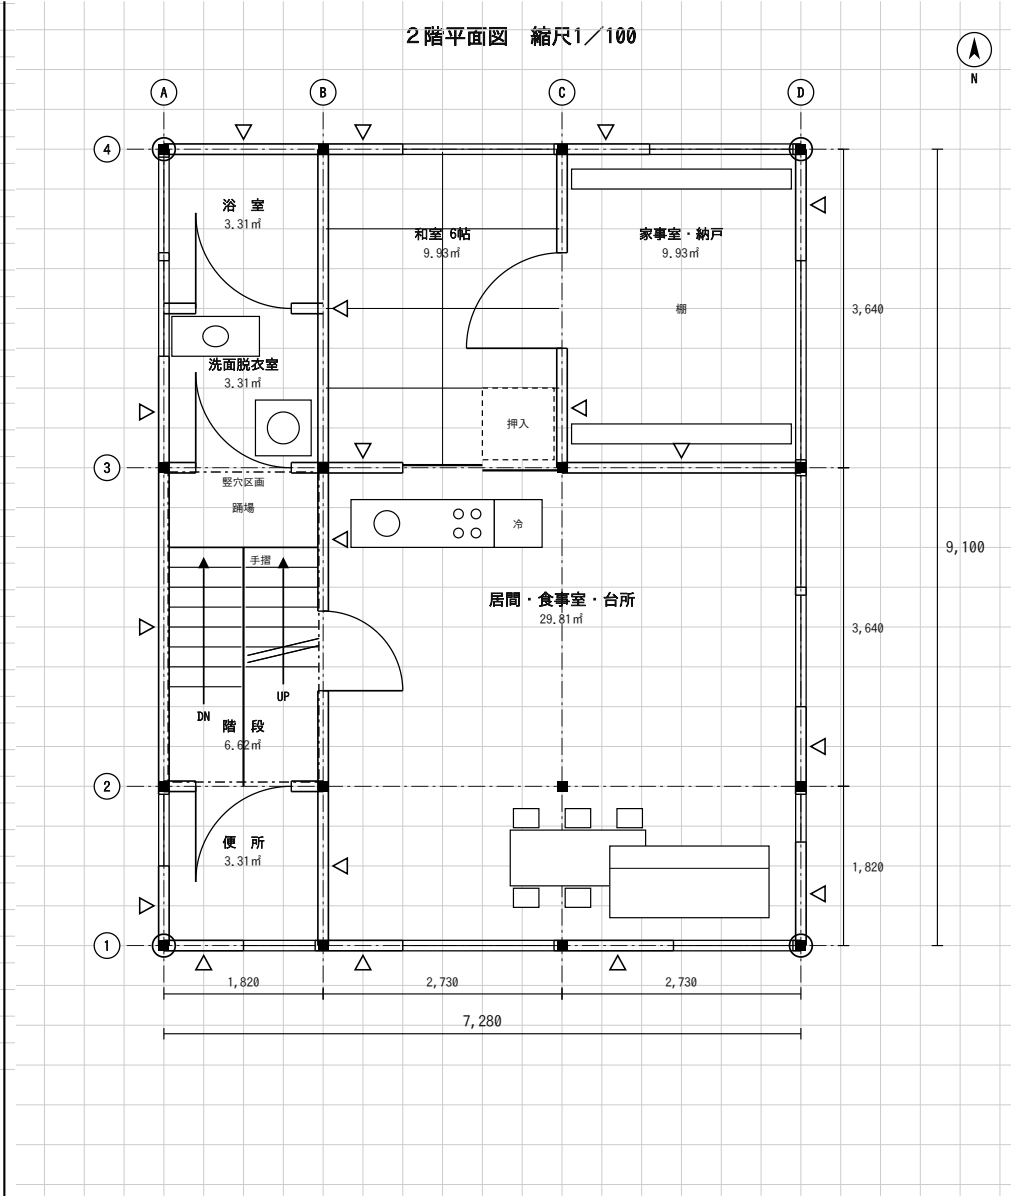


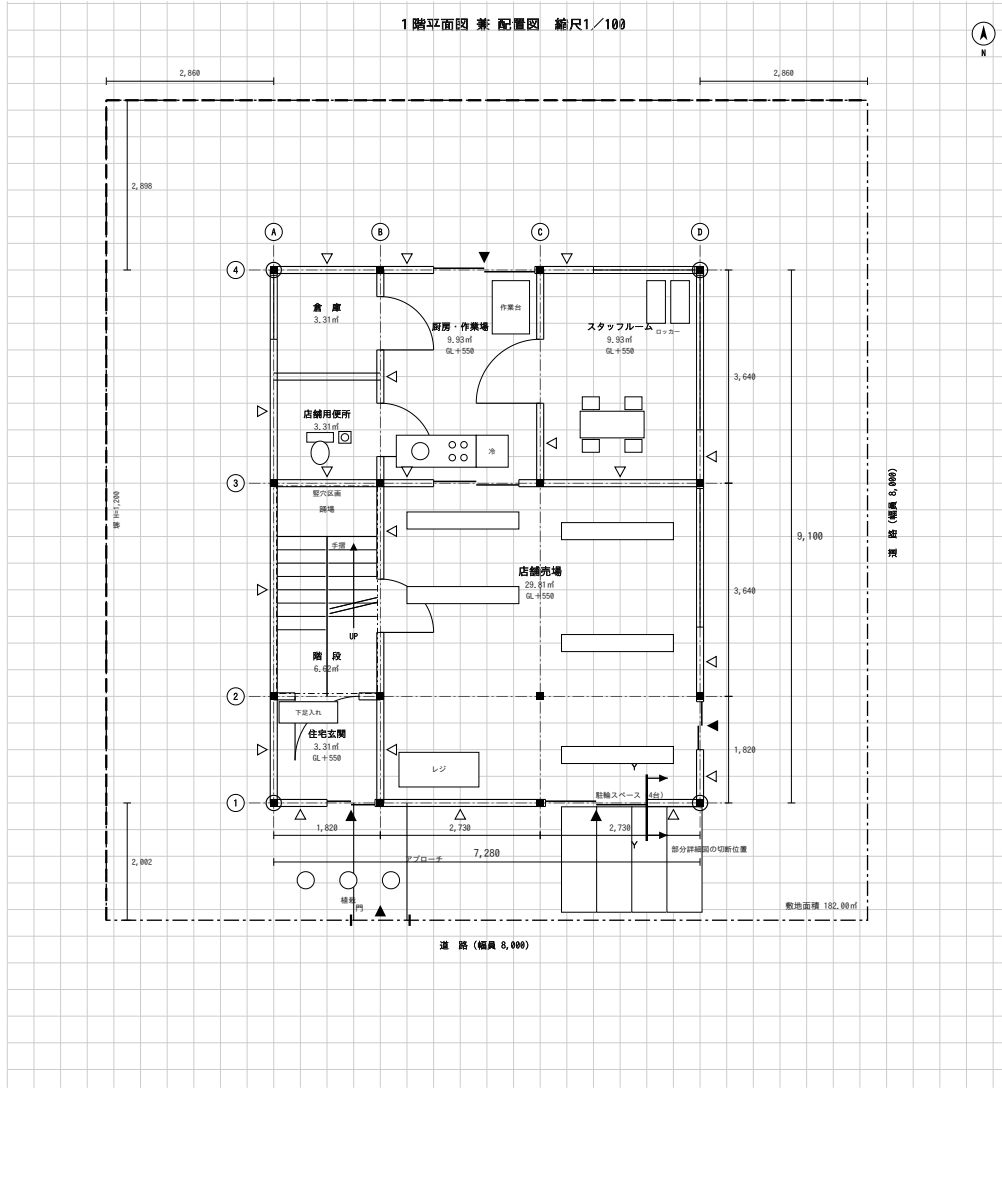

面 積 表

敷地面積		182.00㎡
建築面積	(計算式) 7.28×9.10	66.24㎡
床面積 1階 ア	(計算式) 7.28×9.10	66.24㎡
2階 イ	(計算式) 7.28×9.10	66.24㎡
3階 ウ	(計算式) 7.28×9.10	66.24㎡
延べ面積 ア+イ+ウ		198.72㎡

小数点以下第3位以下は切り捨て。計算式はm単位で書く。

凡 例（床伏図兼小屋伏図の表示記号）

通し柱	1階の管柱	2階の管柱	重なる管柱	胴差・床梁・桁	火打梁	棟木	母屋
120×120	120×120	120×120	—	120×120	90×90	120×120	90×90

標 準 解 答 例

予想問題 E


南東の角地に建つ併用住宅（パン店）
木造3階建て / 8マス × 10マス（7,280 × 9,100）

※ 立面図・床伏図兼小屋伏図・部分詳細図は、別紙「共通図」をご覧ください。

この解答例のポイント

- ・ 南と東の2面が道路なので、店舗出入口を角に向けて開いている。
- ・ 東面にも窓を取り、売場と住宅の採光を両方から確保している。
- ・ 角地の建蔽率の割増し（法53条3項）を使える敷地としている。

南側立面図 縮尺1／100

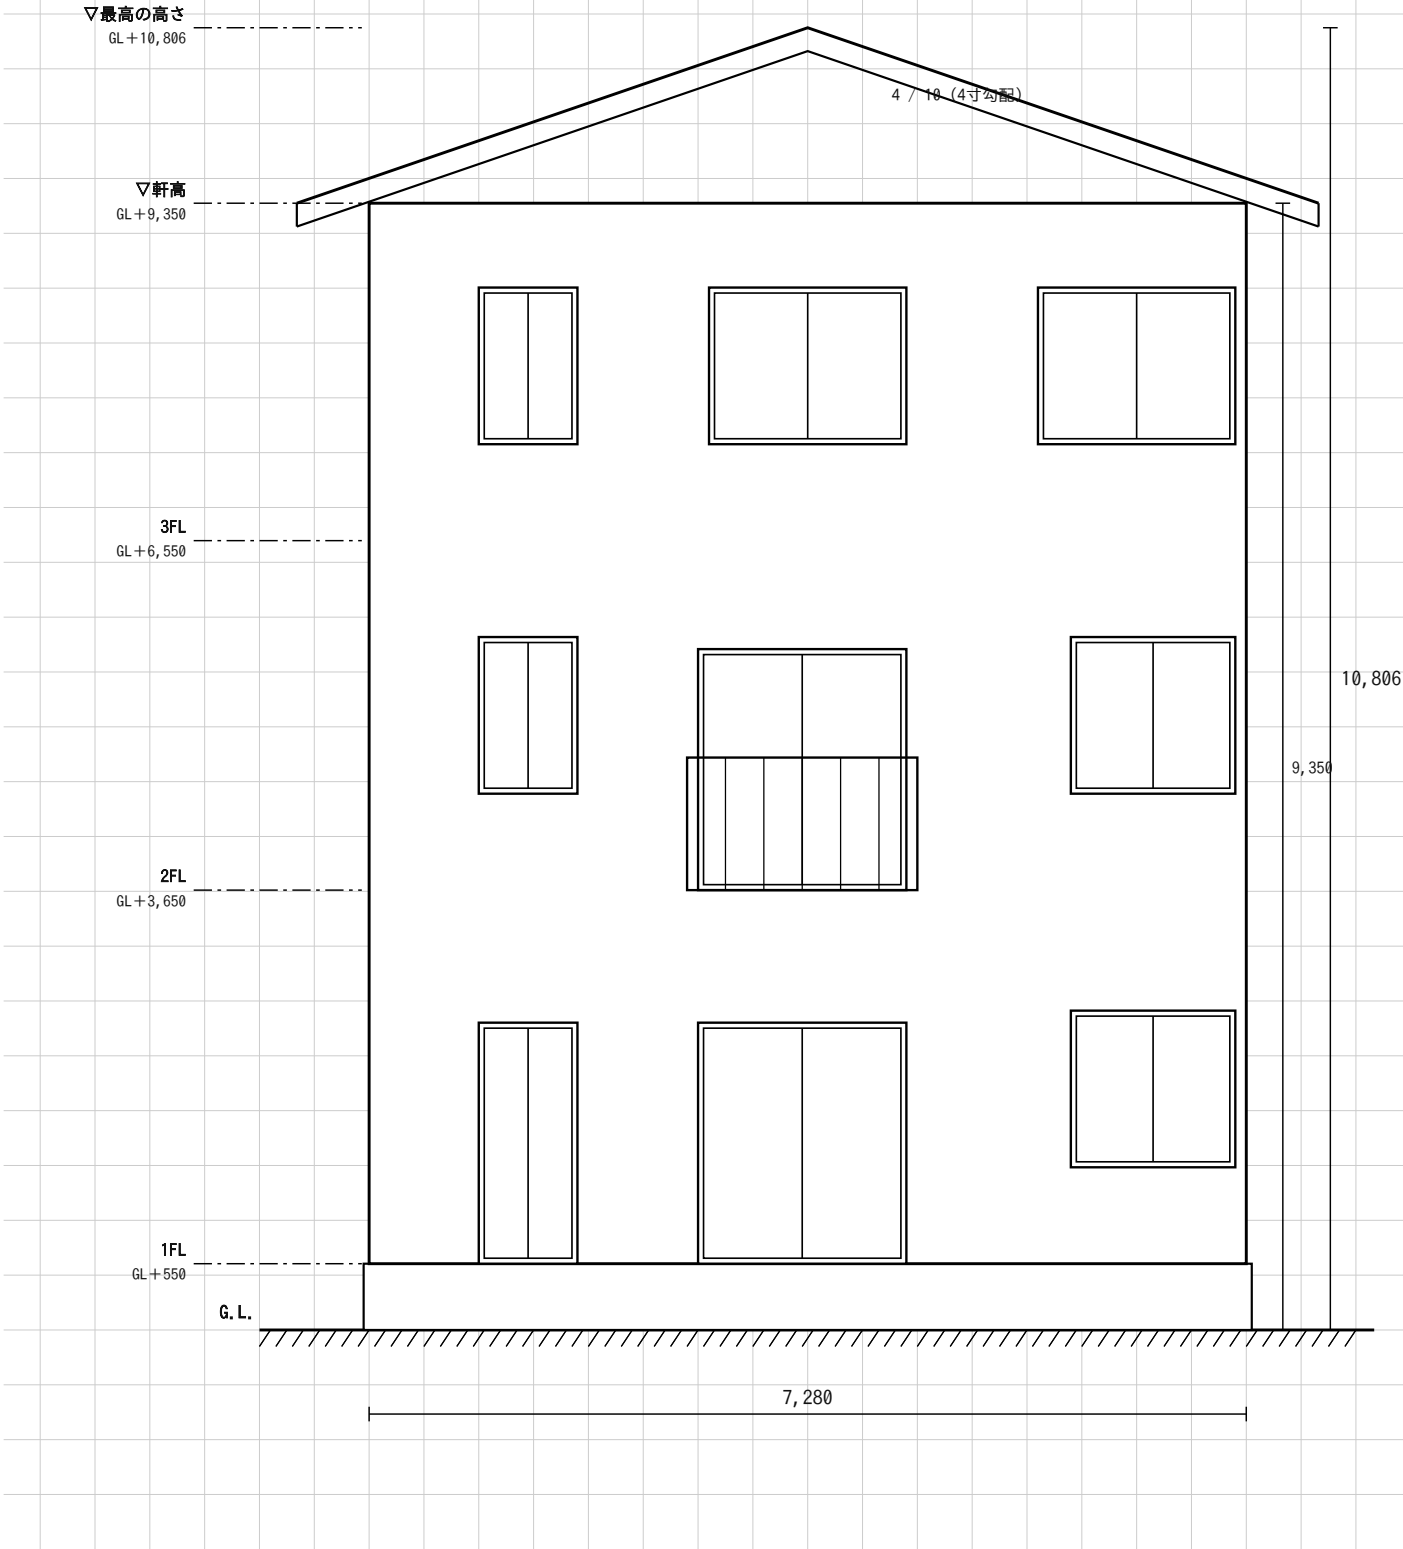

部分詳細図（外壁 断面） 1/20


左が室内・右が屋外 / 準防火地域の準耐火建築物（45分）を想定

★ 本番の解答用紙に描いて提出するのは、この1枚

← 室内 屋外 →

B 2階の床のところ


天井高 2,700

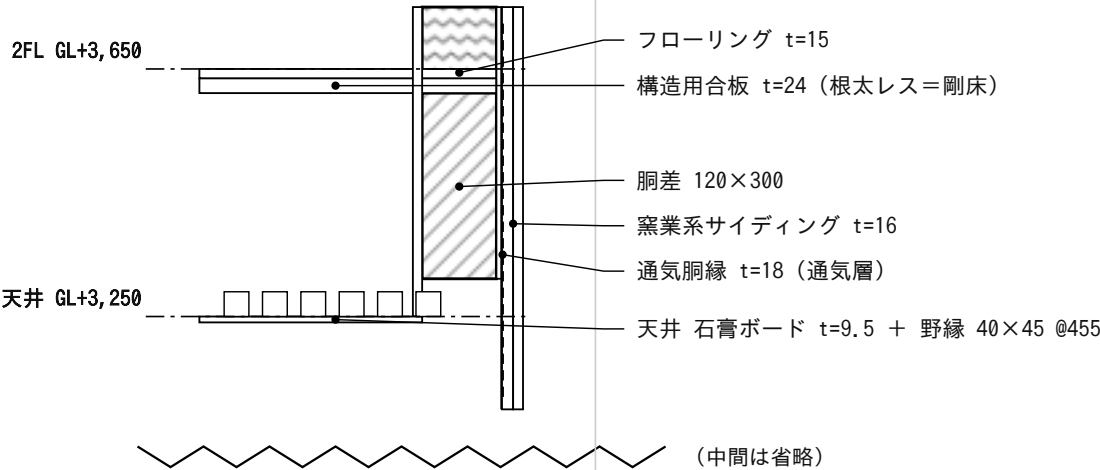

A 地面のところ

各部の寸法 (mm)

39
20
120
521
150
60

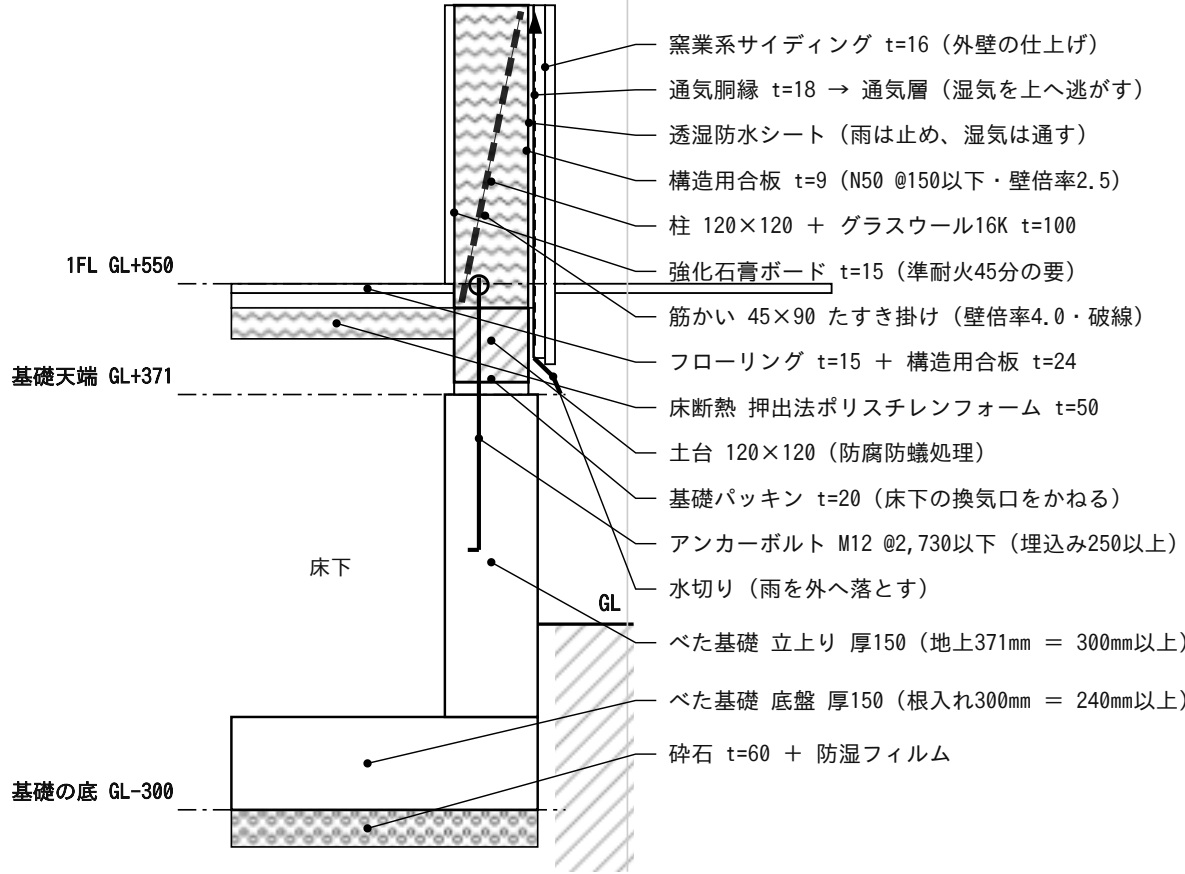


模様の意味 木材（切り口） コンクリート 断熱材 砕石 地面

- ★ 外壁の厚さ 15+120+9+18+16 = 178mm。この6層を「内から外へ」の順で覚える。
- ★ 1FL は GL+550。基礎の立上りを地上300mm以上とるため、GL+400 では納まらない（本文の解説を参照）。
- ★ 数値は必ず法令集・告示（平12建告1347号ほか）で確認すること。

※ この2枚は「型（8マス×10マス）」のもの。問題B（9マス）・C（7マス）は間口が違うので寸法を読みかえる。

小屋伏図 縮尺1/100

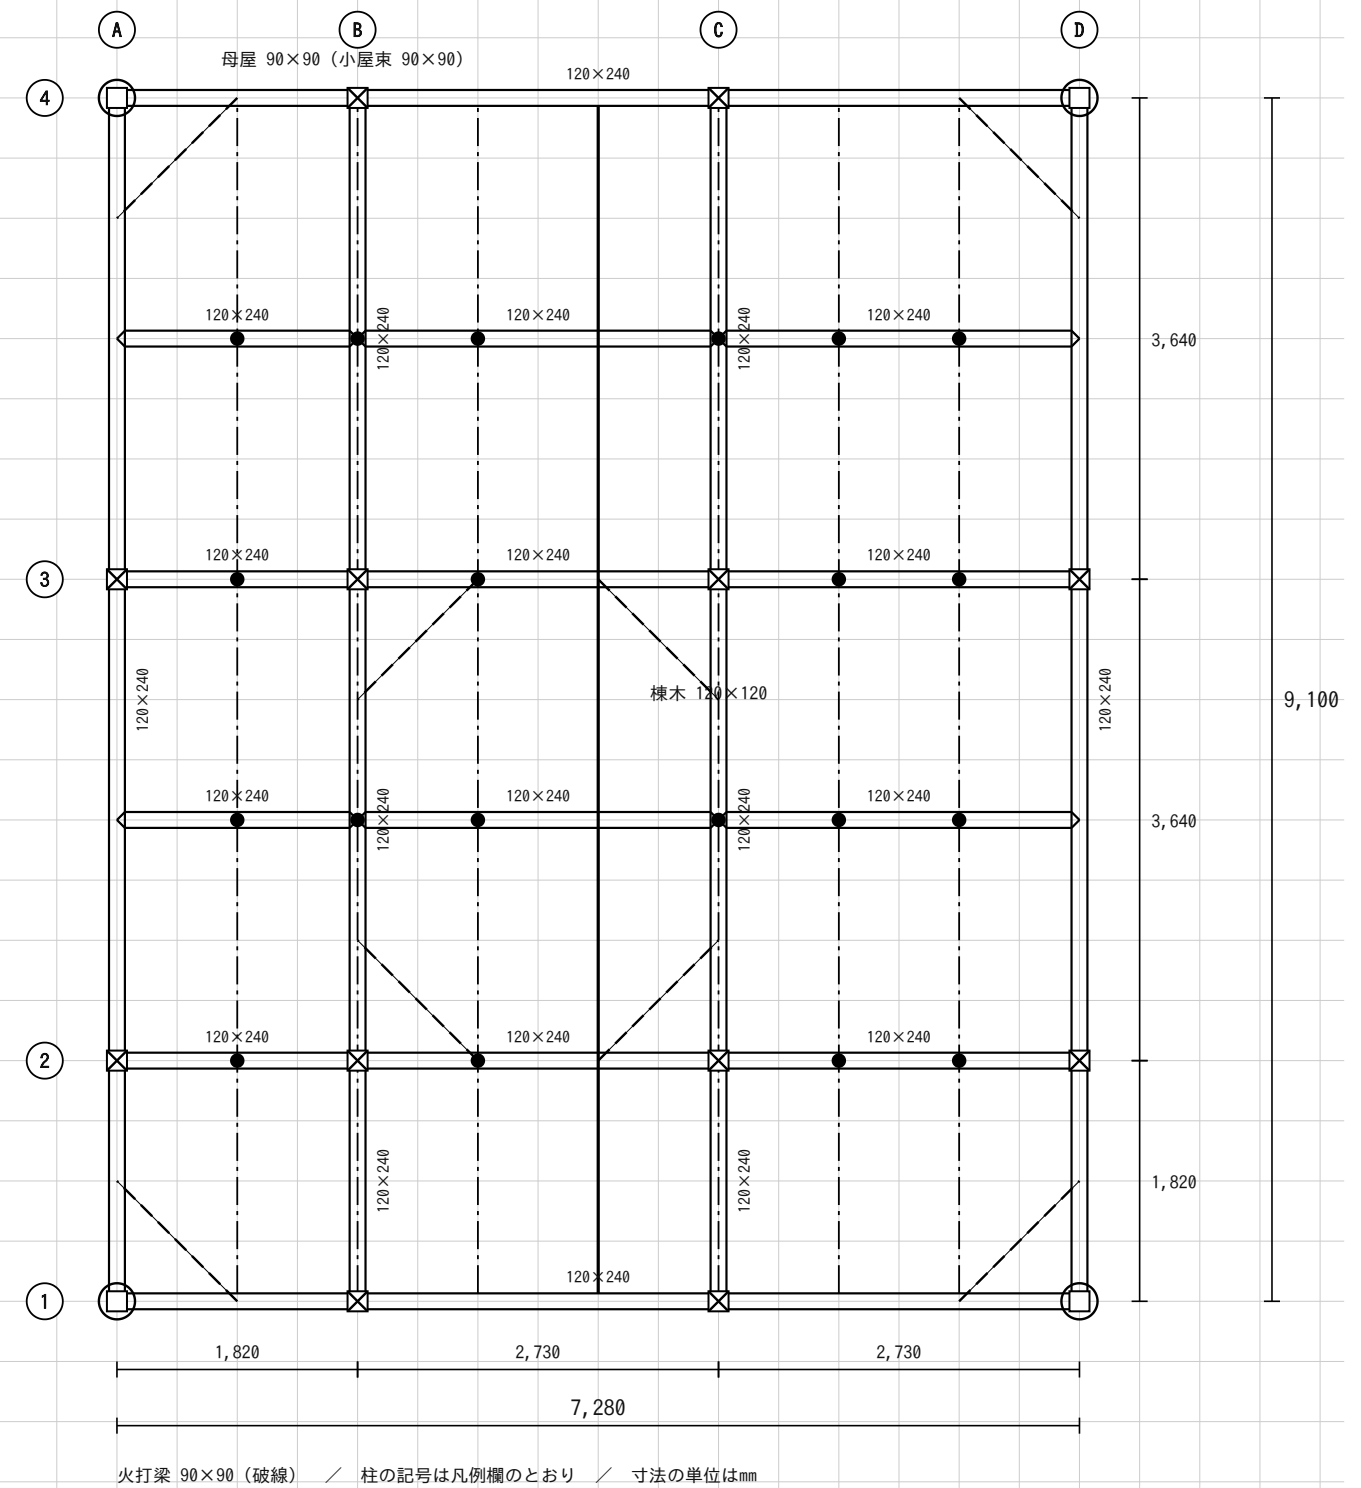

※ 2階の床伏図と3階の床伏図は同じ組み方でよい。小屋伏図は棟が南北方向・4寸勾配。