
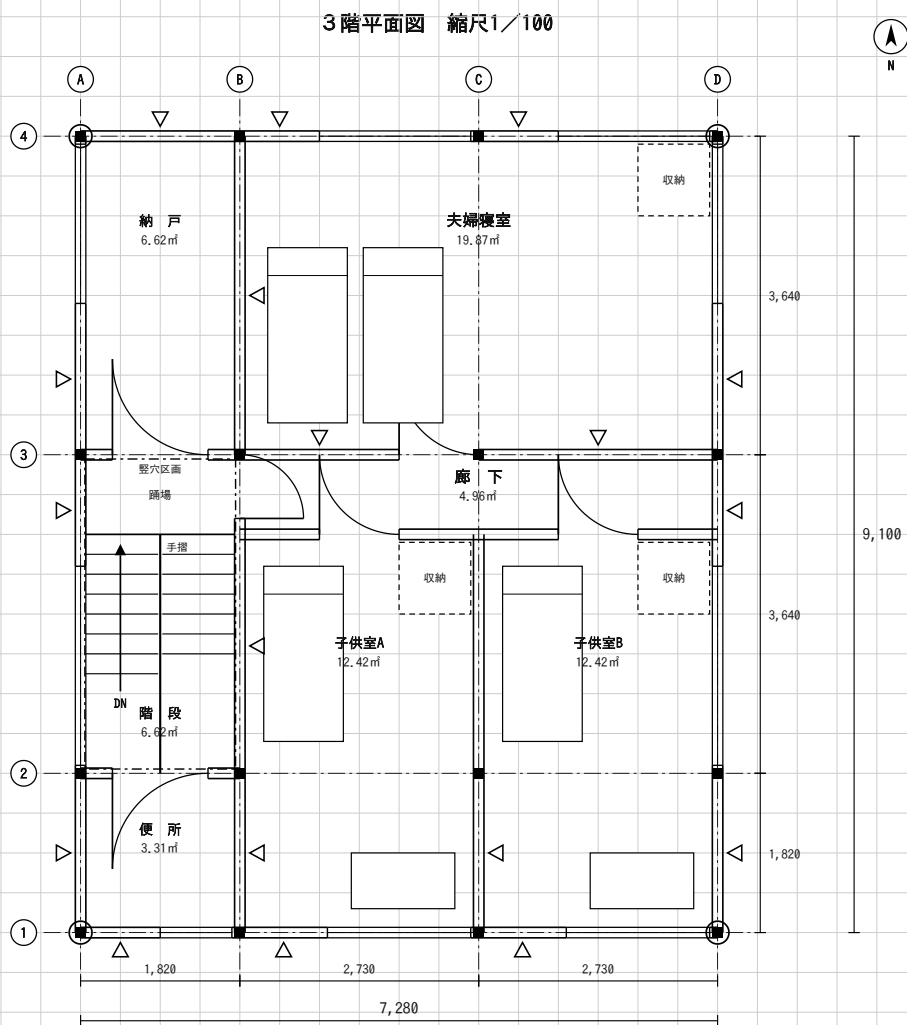
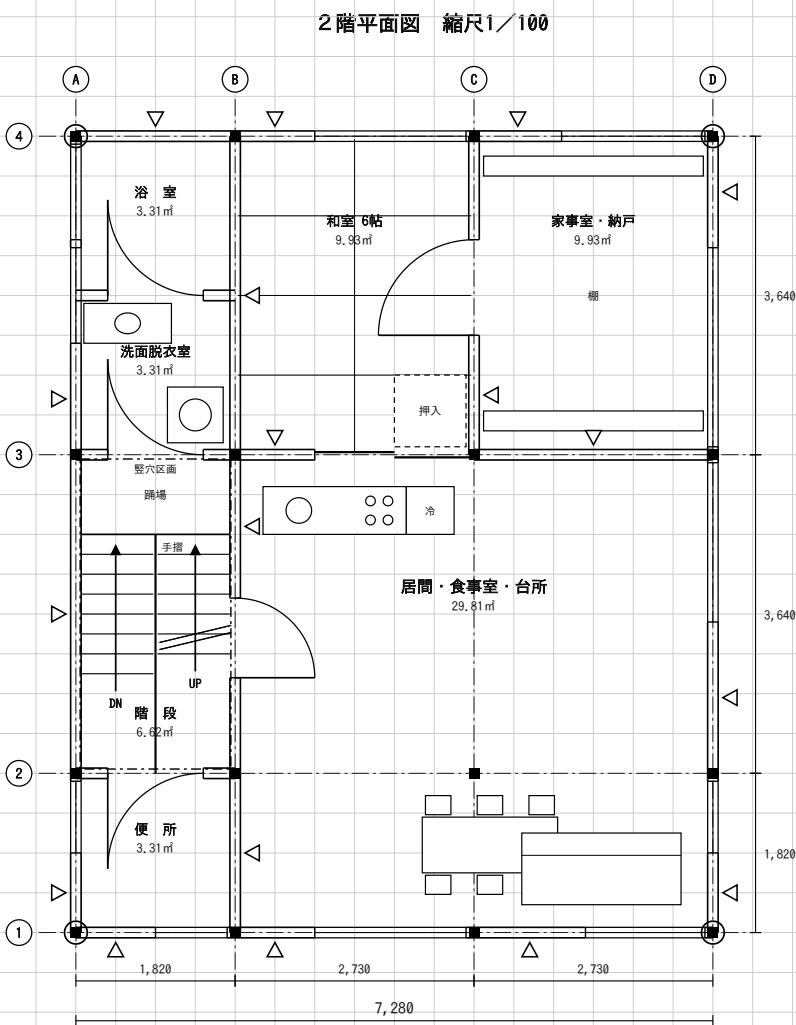


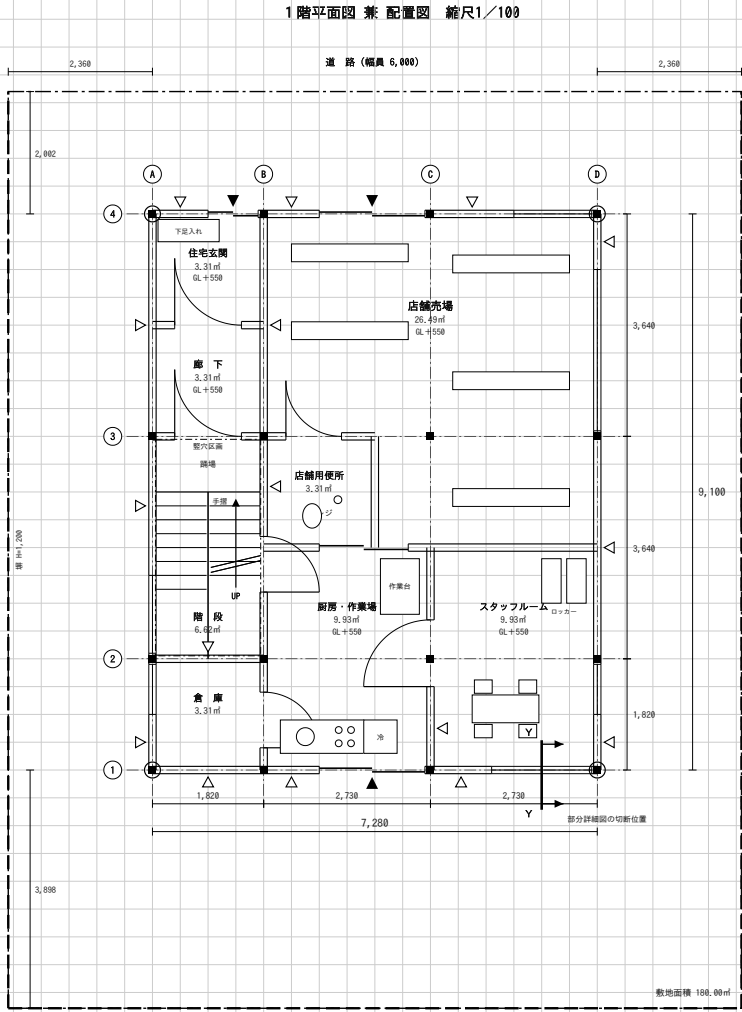

面 積 表

|            |                    |          |
|------------|--------------------|----------|
| 敷地面積       |                    | 180.00 ㎡ |
| 建築面積       | (計算式)<br>7.28×9.10 | 66.24 ㎡  |
| 床面積 1階 ア   | (計算式)<br>7.28×9.10 | 66.24 ㎡  |
| 2階 イ       | (計算式)<br>7.28×9.10 | 66.24 ㎡  |
| 3階 ウ       | (計算式)<br>7.28×9.10 | 66.24 ㎡  |
| 延べ面積 ア+イ+ウ |                    | 198.72 ㎡ |

小数点以下第3位以下は切り捨て。計算式はm単位で書く。

凡 例 (床伏図兼小屋伏図の表示記号)

| 通し柱 | 1階の管柱   | 2階の管柱   | 重なる管柱   | 胴差・床梁・桁 | 火打梁     | 棟木    | 母屋    |
|-----|---------|---------|---------|---------|---------|-------|-------|
| 記号  |         |         |         |         |         |       |       |
| 寸法  | 120×120 | 120×120 | 120×120 | —       | 120×120 | 90×90 | 90×90 |

標 準 解 答 例

予想問題 F


北側道路の併用住宅（書店）  
木造3階建て / 8マス × 10マス (7,280 × 9,100)

※ 立面図・床伏図兼小屋伏図・部分詳細図は、別紙「共通図」をご覧ください。

この解答例のポイント

- ・道路が北なので、1階だけ南北を入れかえて店舗を北（道路側）に向けた。
- ・階段の位置は動かさないで、2階・3階は型のまま使える。
- ・住宅の居室は南側に集め、日当たりを確保している。

南側立面図 縮尺1/100

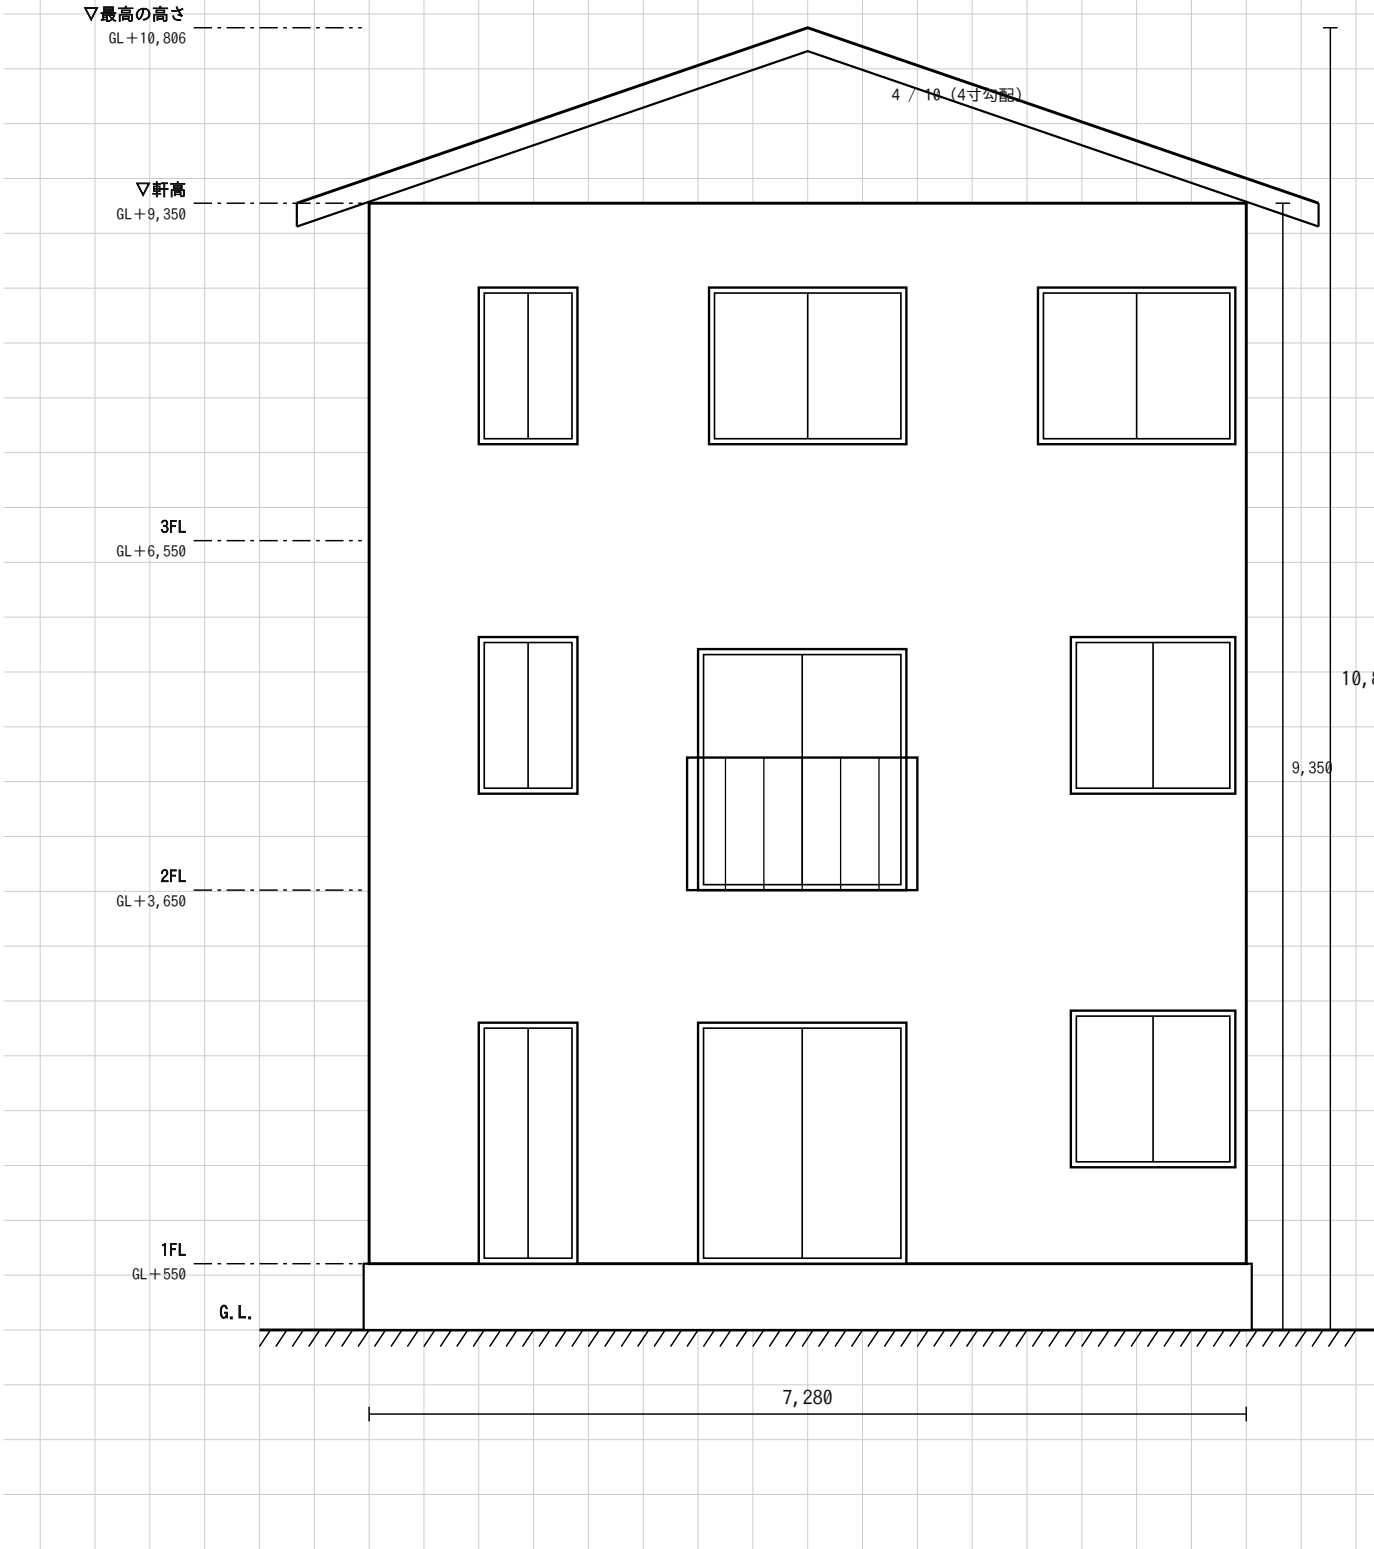

部分詳細図（外壁 断面） 1/20


左が室内・右が屋外 / 準防火地域の準耐火建築物（45分）を想定

★ 本番の解答用紙に描いて提出するのは、この1枚

← 室内 屋外 →

B 2階の床のところ


天井高 2,700

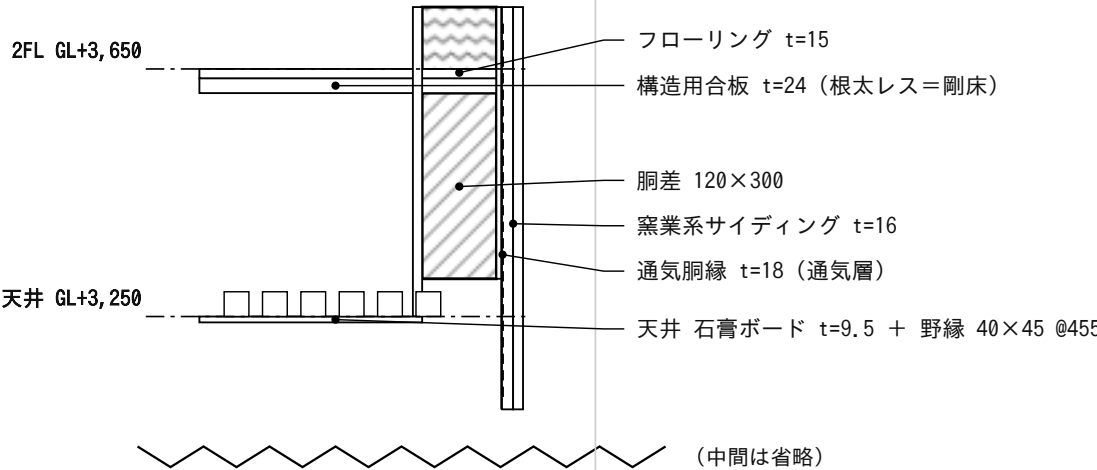

A 地面のところ

各部の寸法 (mm)

39  
120  
20  
521  
150  
60

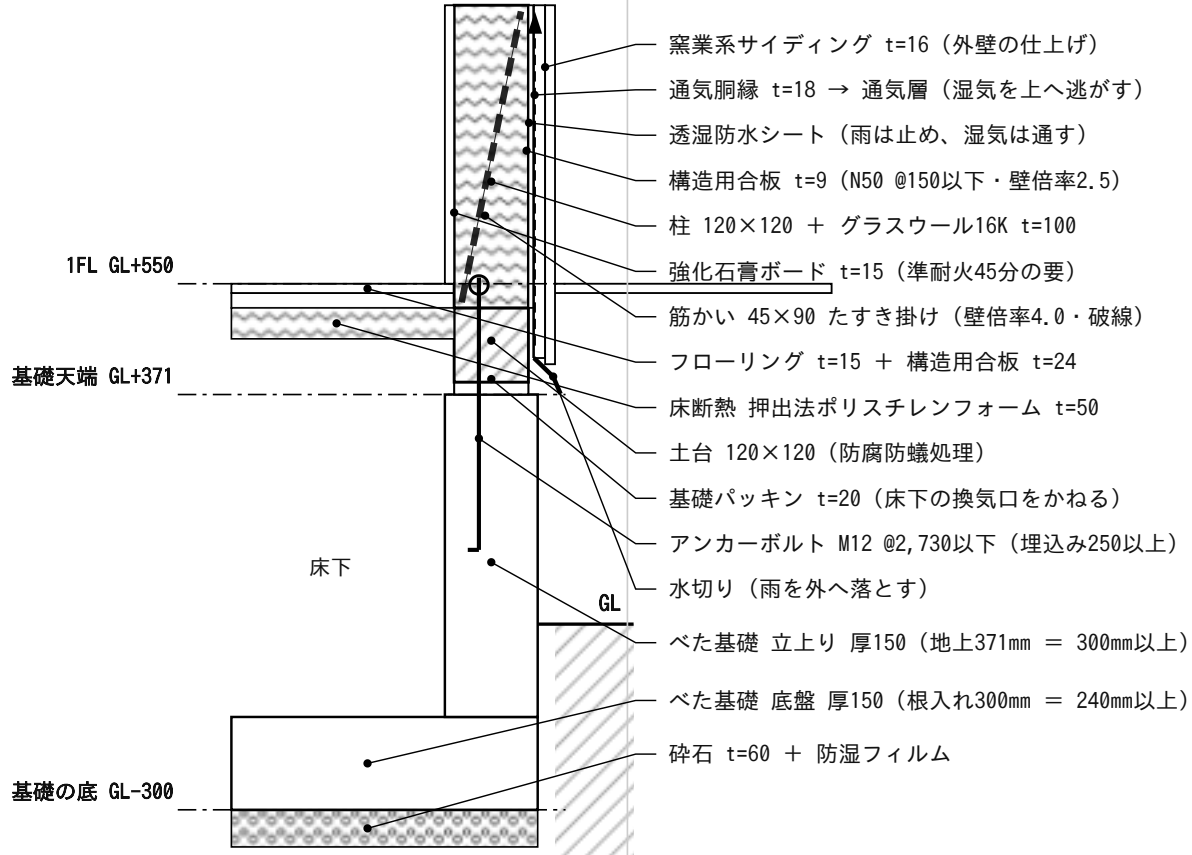


模様の意味 木材 (切り口) コンクリート 断熱材 砕石 地面

- ★ 外壁の厚さ 15+120+9+18+16 = 178mm。この6層を「内から外へ」の順で覚える。
- ★ 1FL は GL+550。基礎の立上りを地上300mm以上とるため、GL+400 では納まらない（本文の解説を参照）。
- ★ 数値は必ず法令集・告示（平12建告1347号ほか）で確認すること。

※ この2枚は「型（8マス×10マス）」のもの。問題B（9マス）・C（7マス）は間口が違うので寸法を読みかえる。

小屋伏図 縮尺1/100

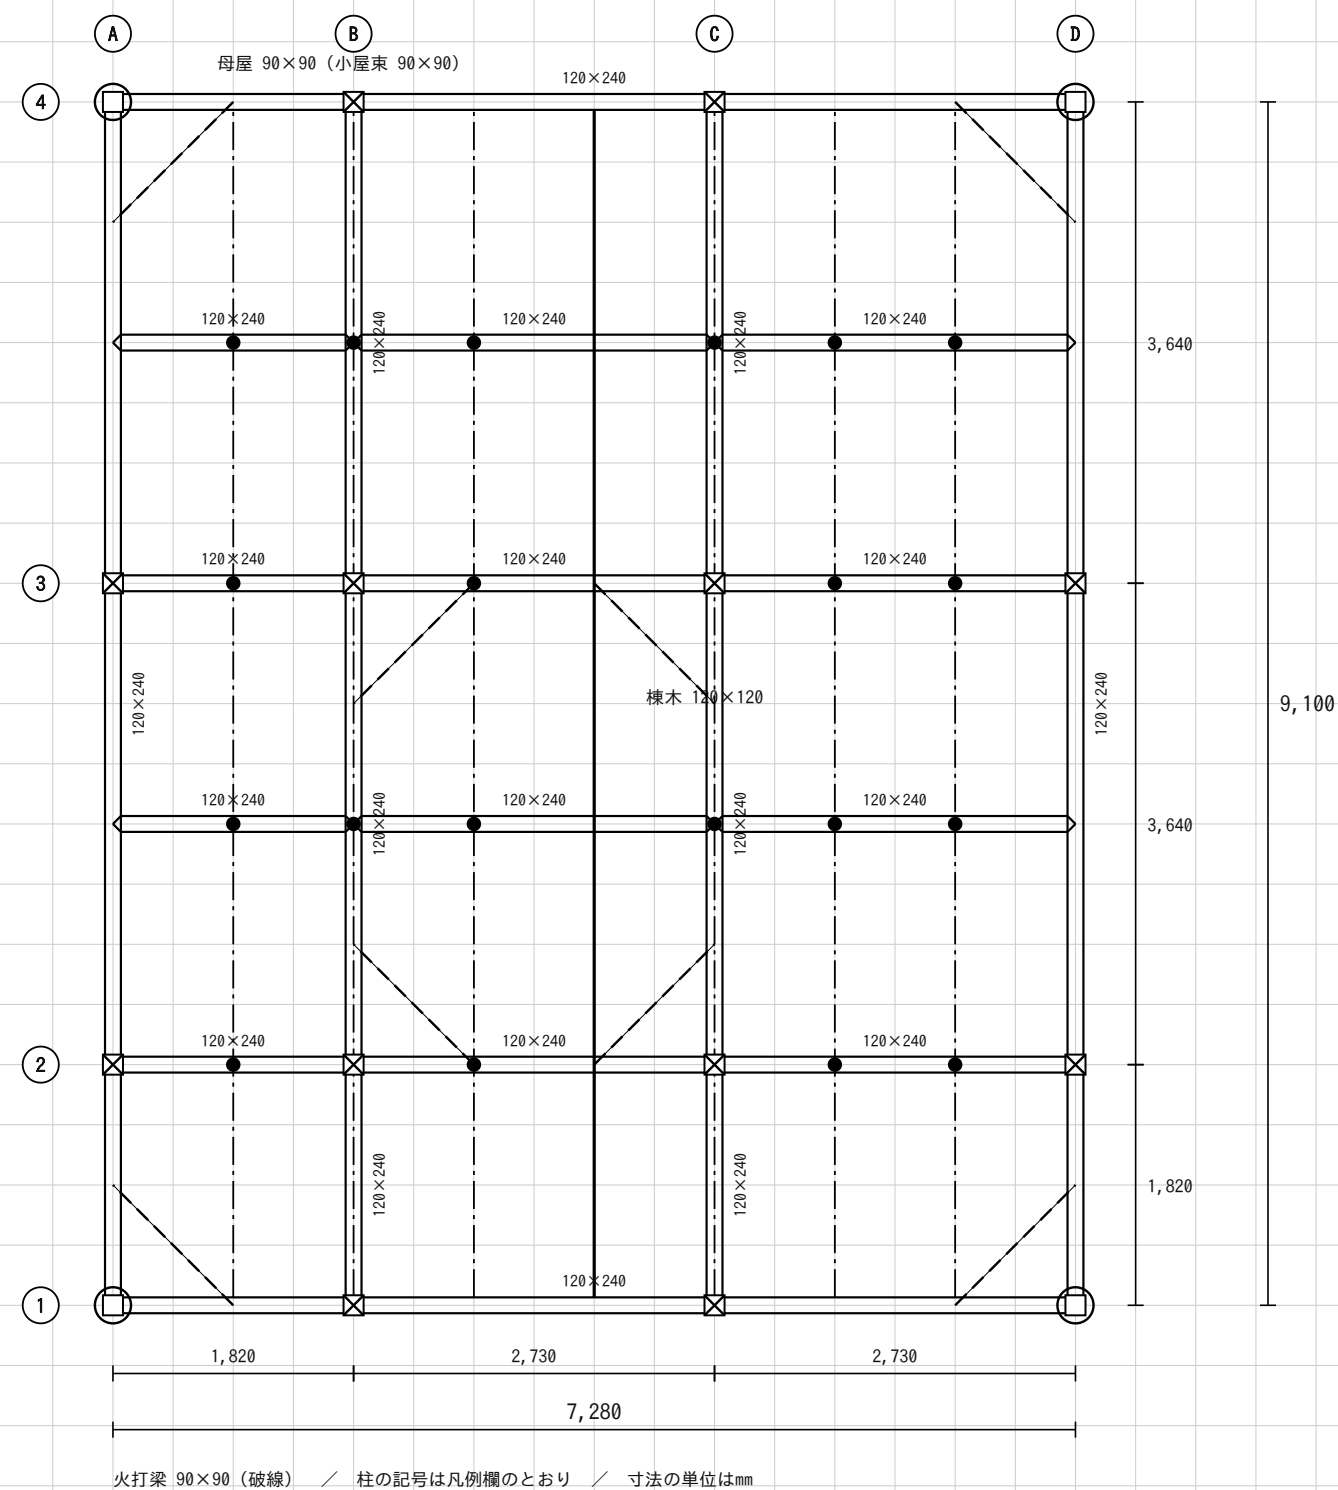

※ 2階の床伏図と3階の床伏図は同じ組み方でよい。小屋伏図は棟が南北方向・4寸勾配。