




1 階平面図 兼 配置図 縮尺1／100

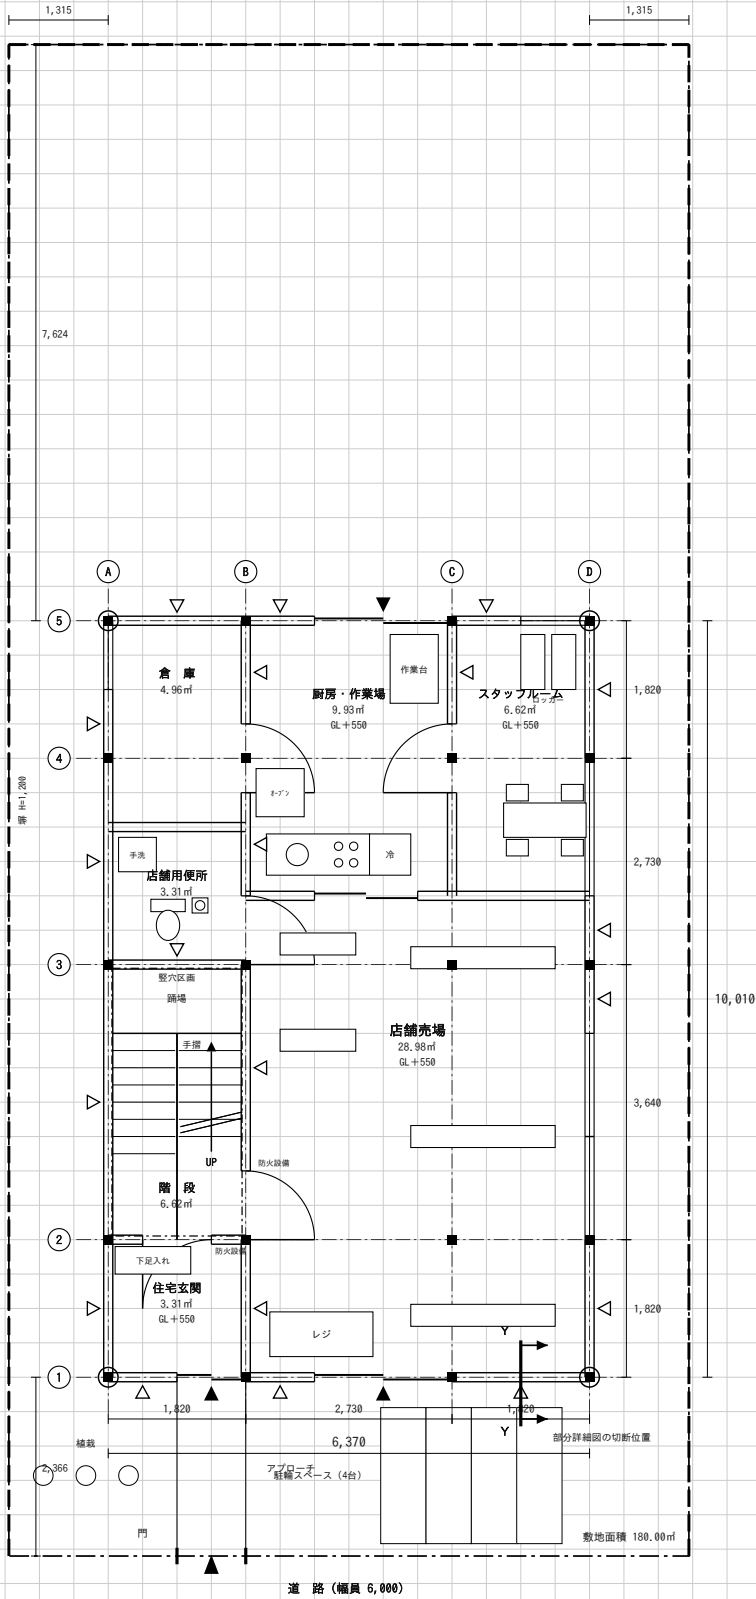

2 階平面図 縮尺1／100

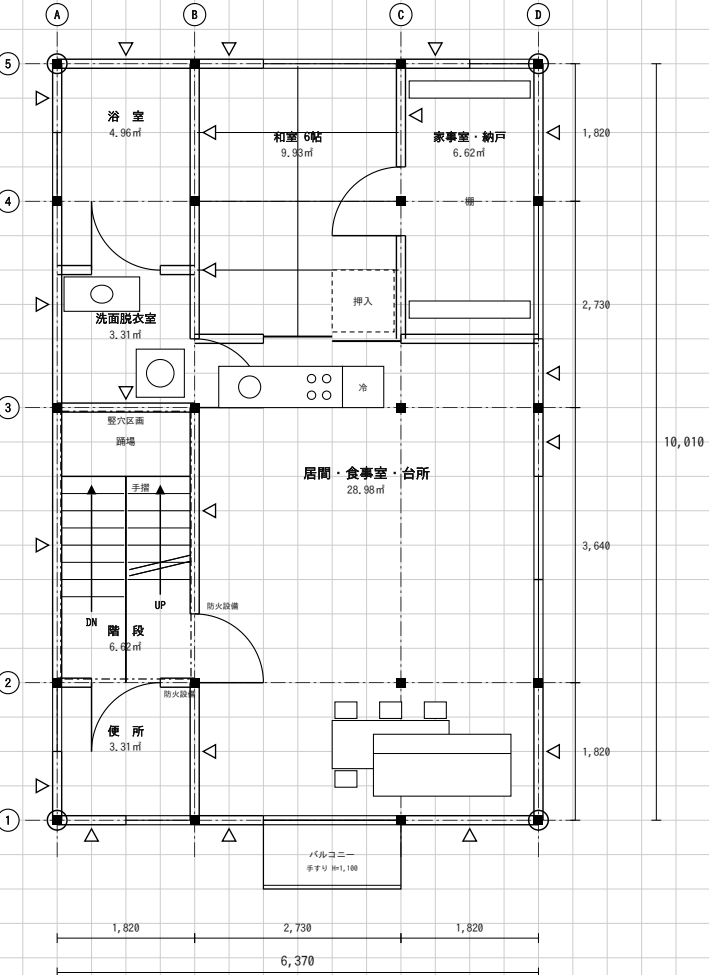

3 階平面図 縮尺1／100

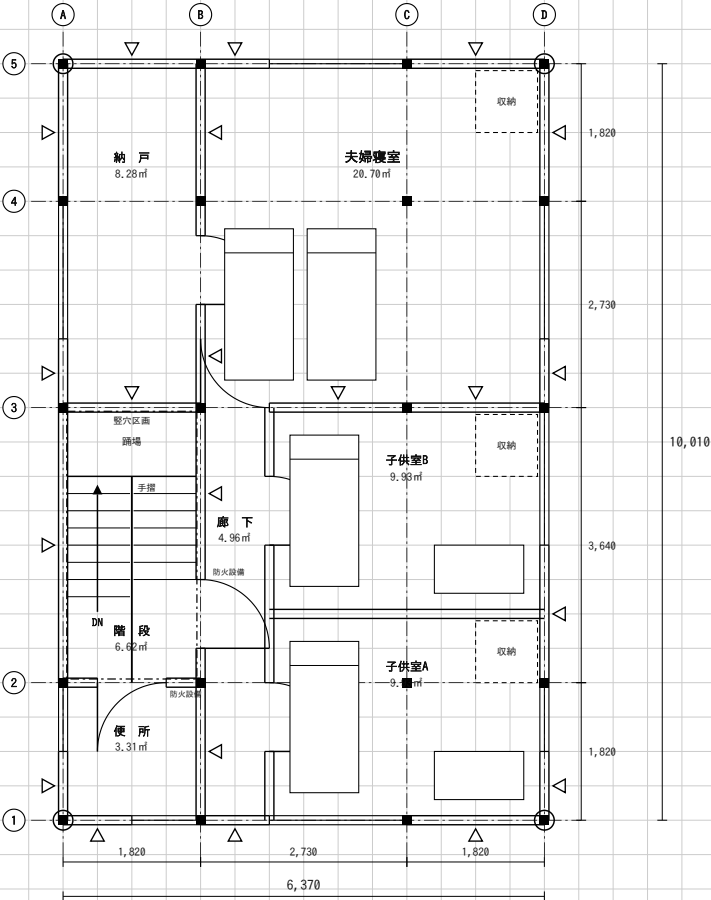

面 積 表

|            |                     |         |
|------------|---------------------|---------|
| 敷地面積       |                     | 180.00㎡ |
| 建築面積       | (計算式)<br>6.37×10.01 | 63.76㎡  |
| 床面積 1階 ア   | (計算式)<br>6.37×10.01 | 63.76㎡  |
| 2階 イ       | (計算式)<br>6.37×10.01 | 63.76㎡  |
| 3階 ウ       | (計算式)<br>6.37×10.01 | 63.76㎡  |
| 延べ面積 ア+イ+ウ |                     | 191.28㎡ |

小数点以下第3位以下は切り捨て。計算式はm単位で書く。

凡 例（床伏図兼小屋伏図の表示記号）

|    | 通し柱     | 1階の管柱   | 2階の管柱   | 重なる管柱 | 胴差・桁（正角材） | 同上（平角材） | 同上（丸太材） | 火打梁   | 棟木      | 母屋・小屋束 |
|----|---------|---------|---------|-------|-----------|---------|---------|-------|---------|--------|
| 記号 |         |         |         |       |           |         |         |       |         |        |
| 寸法 | 120×120 | 120×120 | 120×120 | —     | 120×120   | 図中に記入   | 図中に記入   | 90×90 | 120×120 | 90×90  |

※ 平角材（120×240 など）の断面寸法は、この欄ではなく 床伏図の中の梁1本ずつのわきに記入する。



標 準 解 答 例

予想問題 C  
間口の狭い敷地の併用住宅（喫茶店）  
木造3階建て / 7マス × 11マス (6,370 × 10,010)


※ 立面図・床伏図兼小屋伏図・部分詳細図は、別紙「共通図」をご覧ください。

この解答例のポイント

- ・間口が狭いので7マス×11マスとし、売場を奥へ長く取っている。
- ・水まわりを西の列にそろえて、1階から3階まで配管の位置を合わせている。
- ・通り芯を1・2・3・4・5の5本にして、奥行方向のスパンを2,730以下に抑えた。

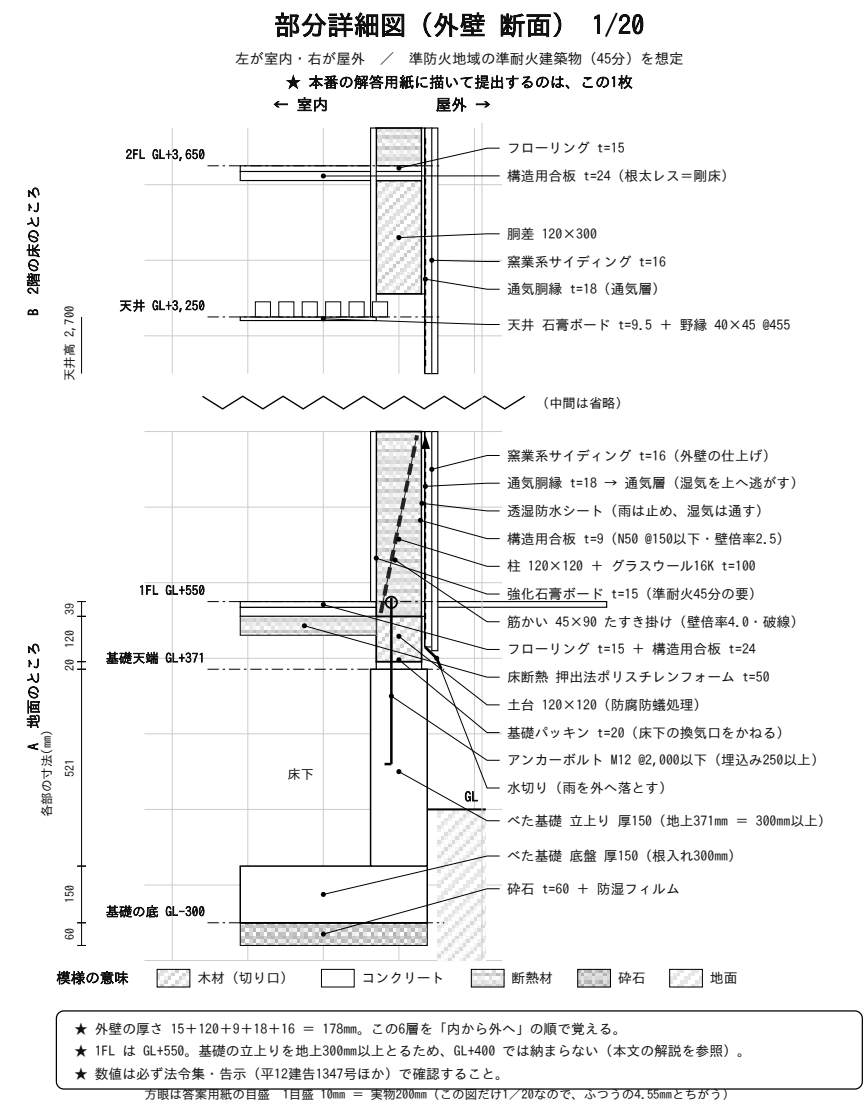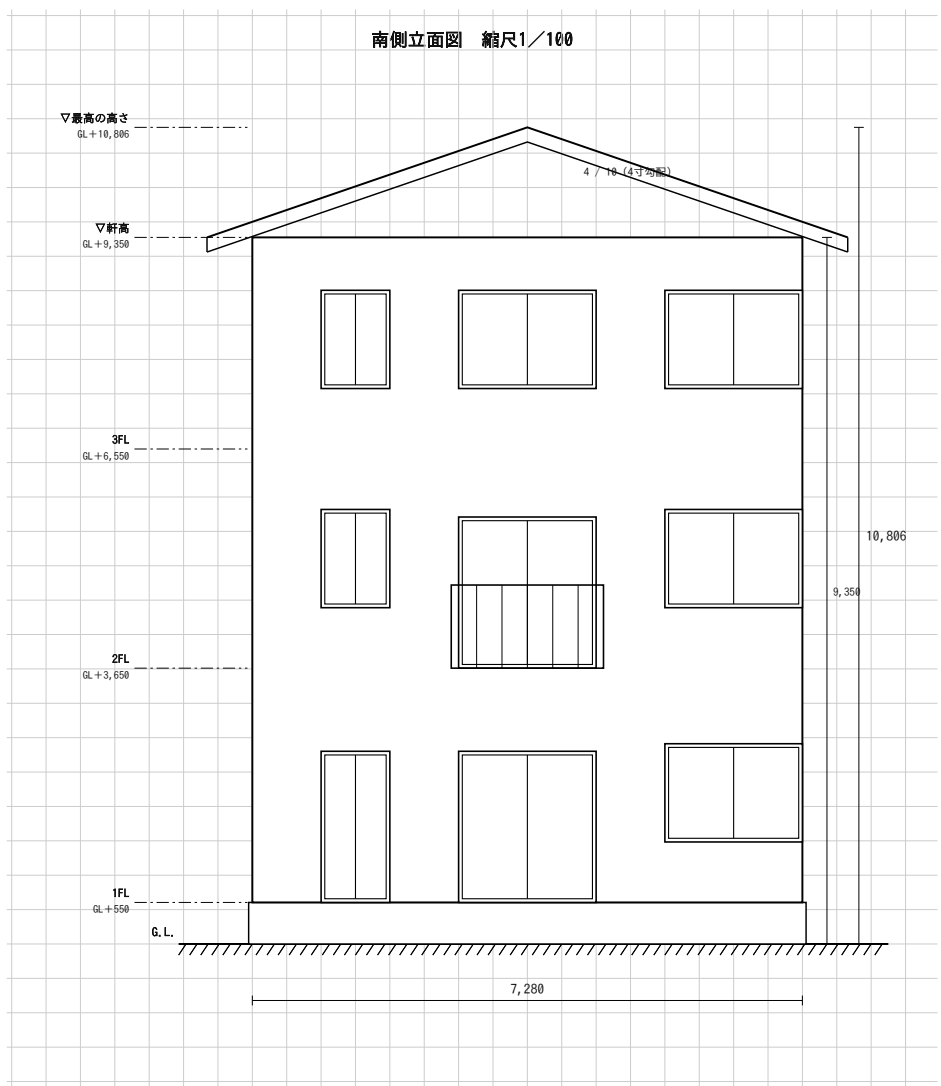

※ この2枚は「型（8マス×10マス）」のもの。問題B（9マス）・C（7マス）は間口が違うので寸法を読みかえる。

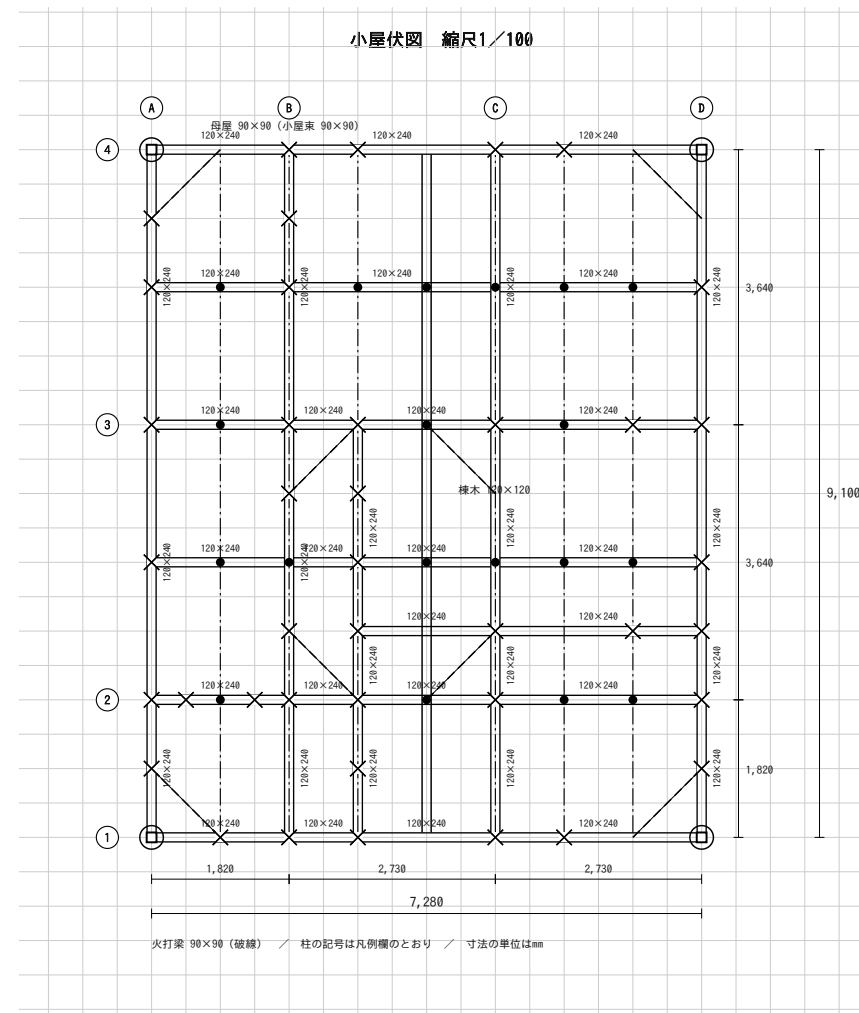

※ 梁は2階・3階の壁の上下と通り芯に必ず通し、残りを床梁φ910で埋める。小屋伏図は棟が南北方向・4寸勾配。3階の壁の上には桁。