
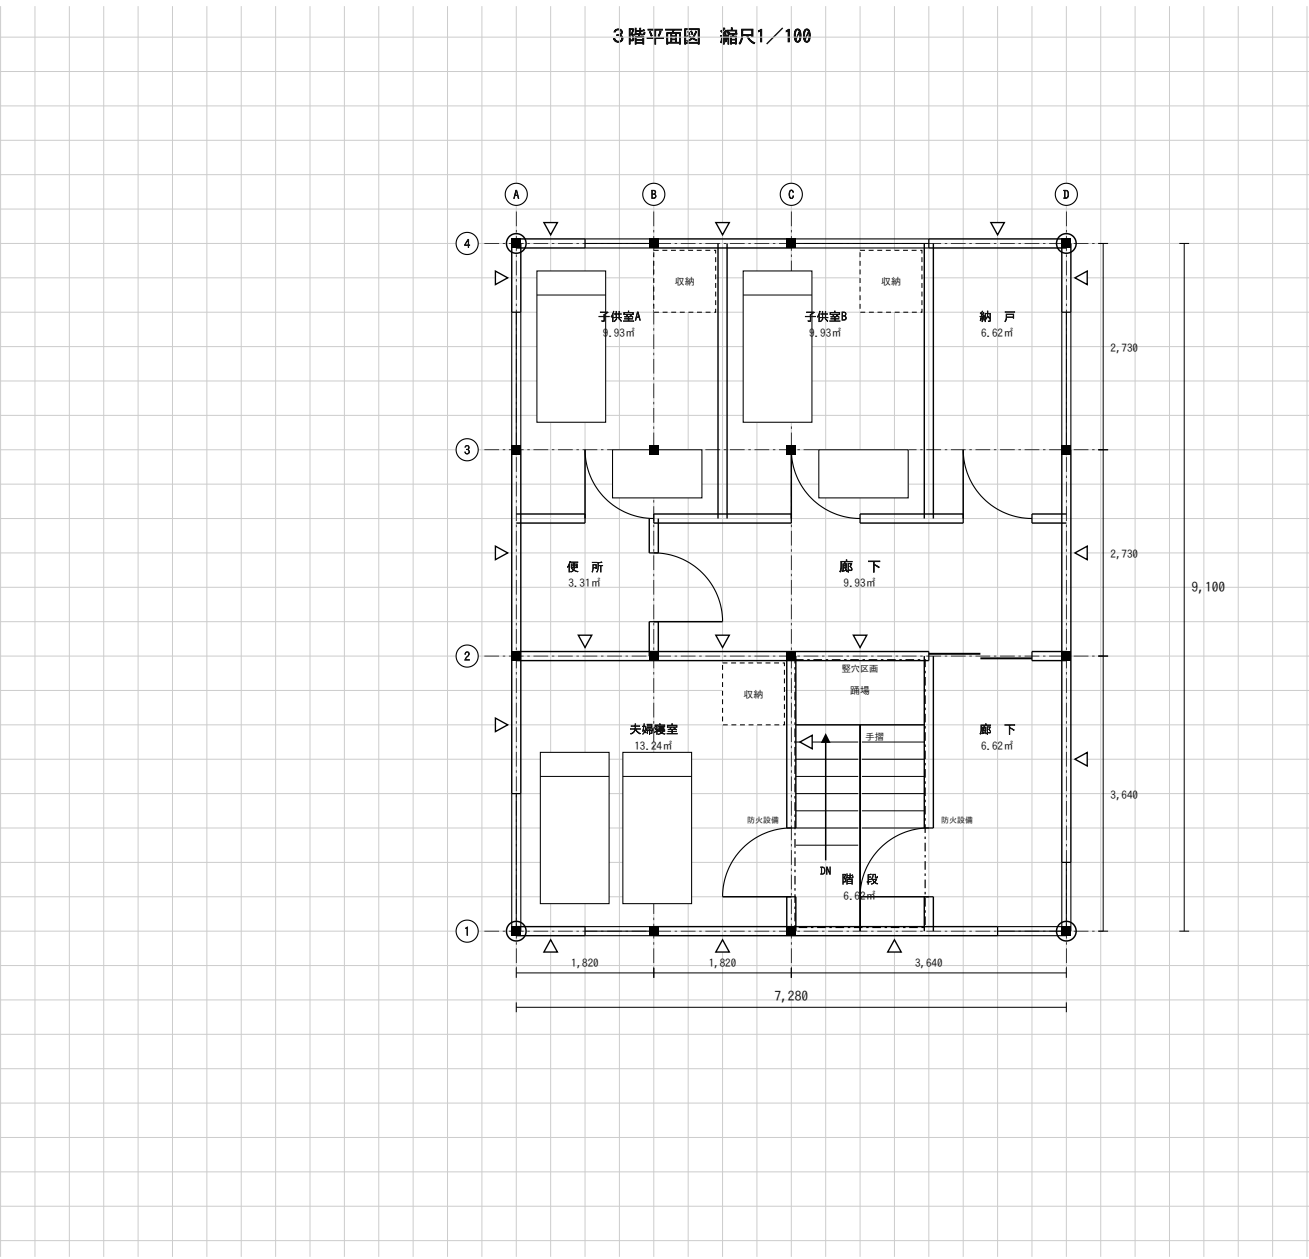
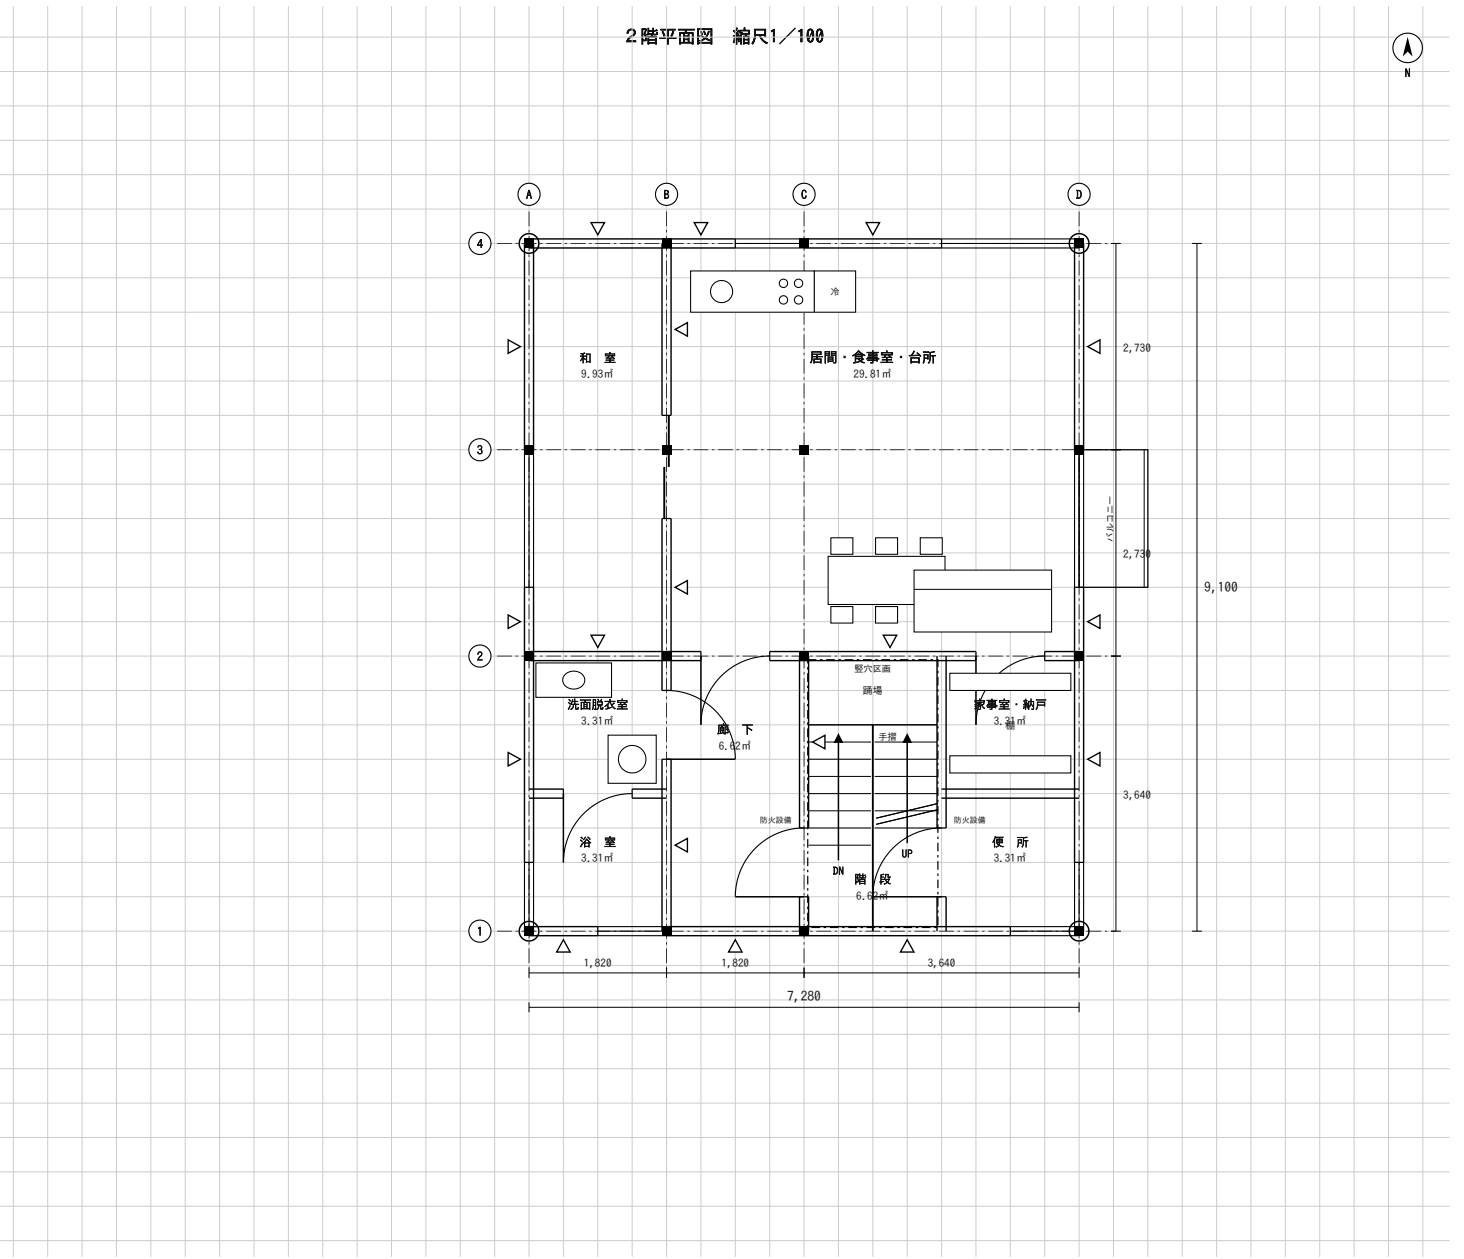


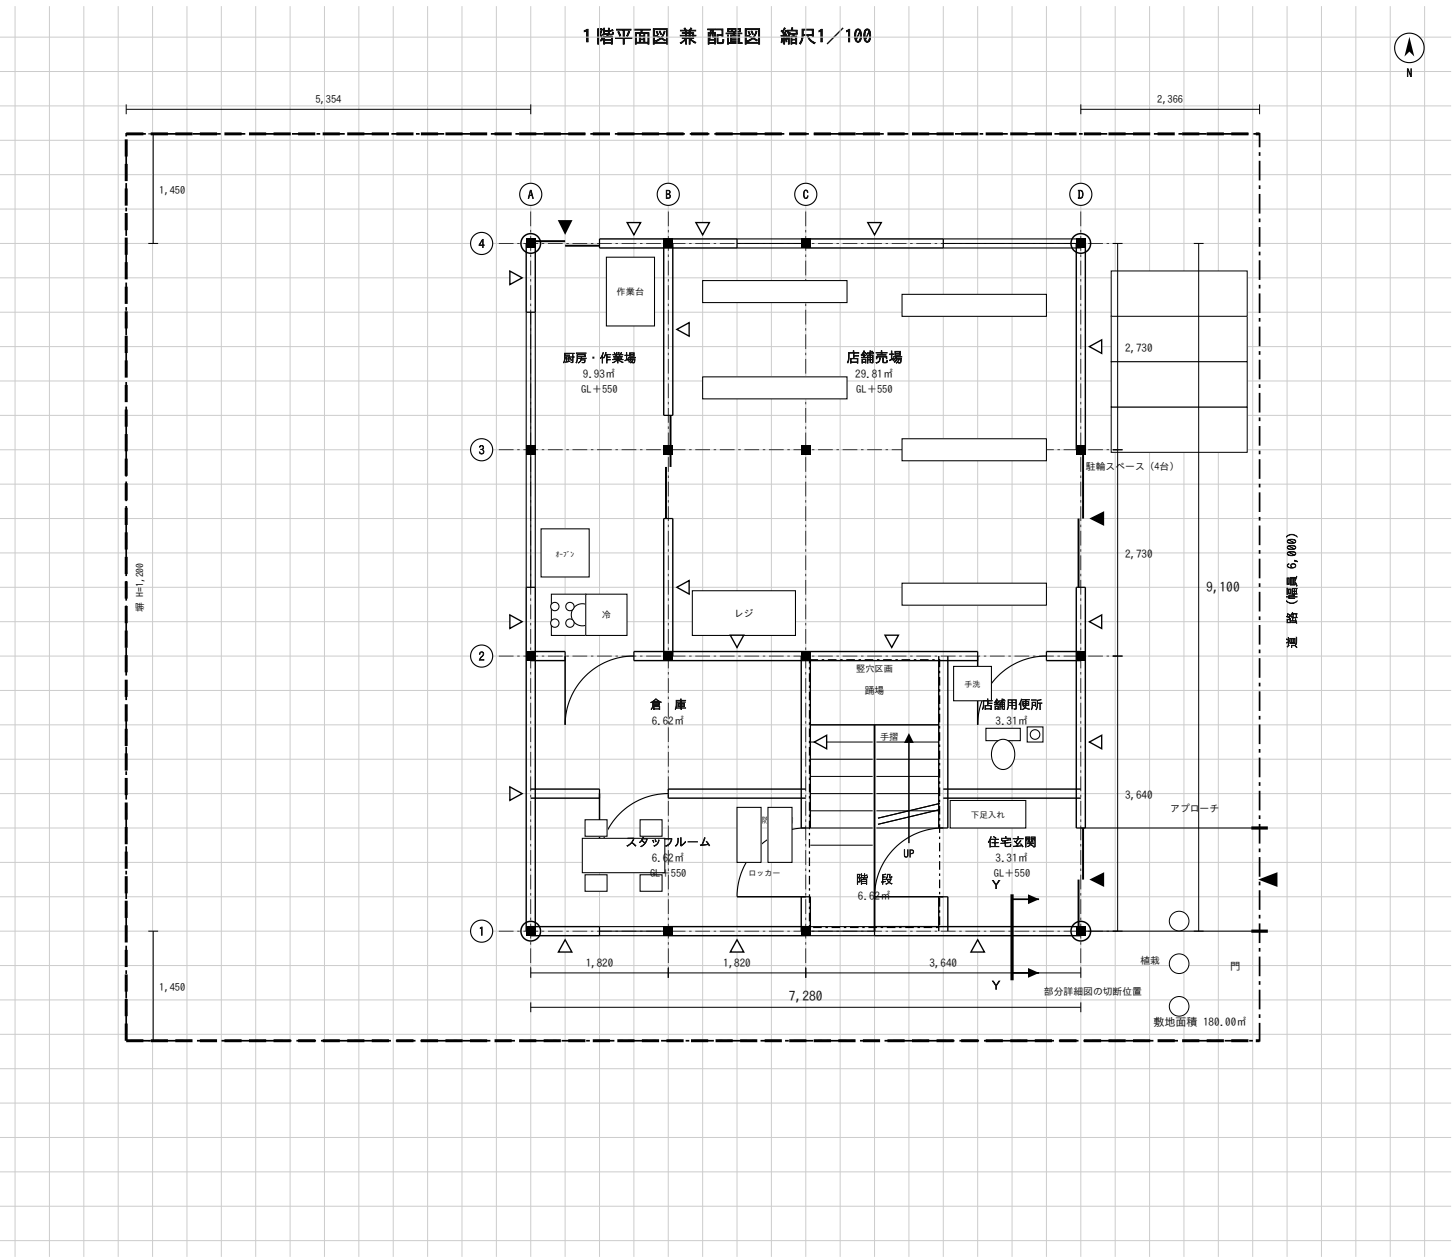

面積表

敷地面積		180.00㎡
建築面積	(計算式) 7.28×9.10	66.24㎡
床面積 1階 ア	(計算式) 7.28×9.10	66.24㎡
2階 イ	(計算式) 7.28×9.10	66.24㎡
3階 ウ	(計算式) 7.28×9.10	66.24㎡
延べ面積 ア+イ+ウ		198.72㎡

小数点以下第3位以下は切り捨て。計算式はm単位で書く。

凡 例（床伏図兼小屋伏図の表示記号）

	通し柱	1階の管柱	2階の管柱	重なる管柱	胴差・桁（正角材）	同上（平角材）	同上（丸太材）	火打梁	棟木	母屋・小屋束
記号										
寸法	120×120	120×120	120×120	—	120×120	図中に記入	図中に記入	90×90	120×120	90×90

※ 平角材（120×240 など）の断面寸法は、この欄ではなく 床伏図の中の梁1本ずつのわきに記入する。

標準解答例

予想問題 D



東側道路の併用住宅（美容室）

木造3階建て ／ 8マス × 10マス（7,280 × 9,100）


※ 立面図・床伏図兼小屋伏図・部分詳細図は、別紙「共通図」を見てください。

この解答例のポイント

- ・道路が東なので売場を東面に向け、店舗出入口も東に取っている。
- ・階段を玄関の西どなりへ動かし、住宅の動線が売場を通らないようにした。
- ・通り芯の組み方を東西方向に変え、大梁のスパンを3,640以下に収めている。

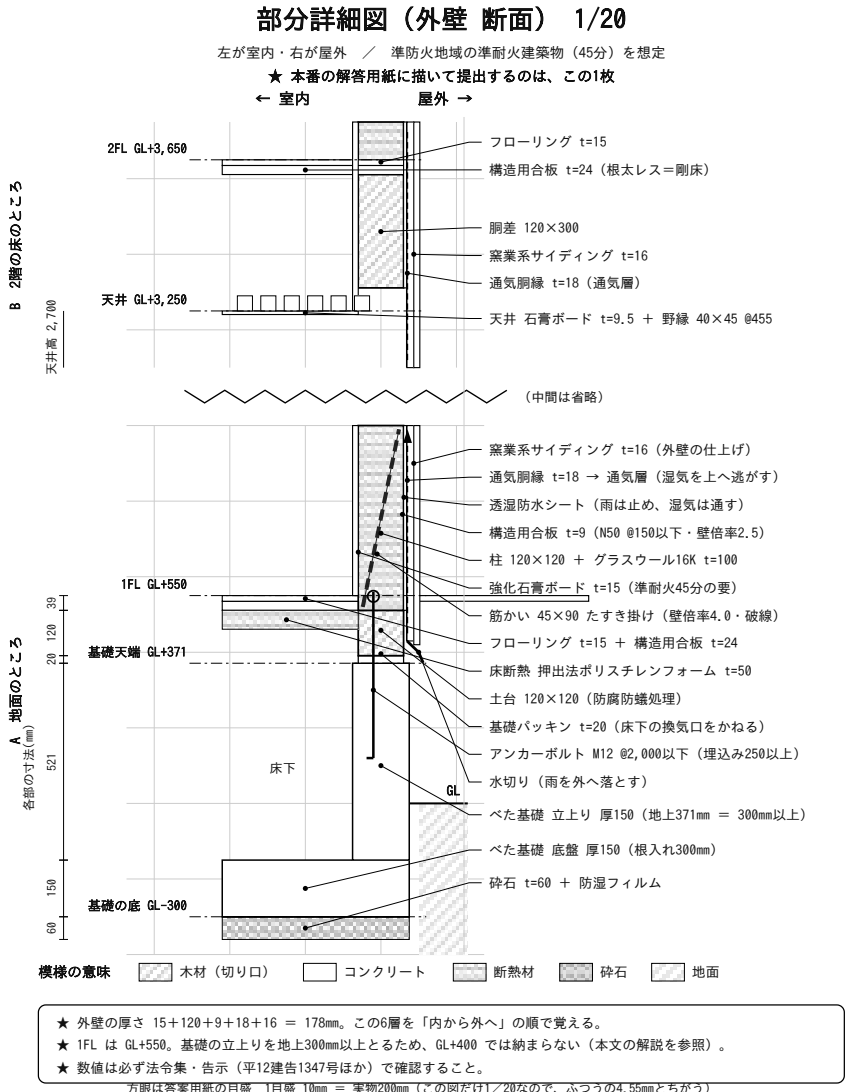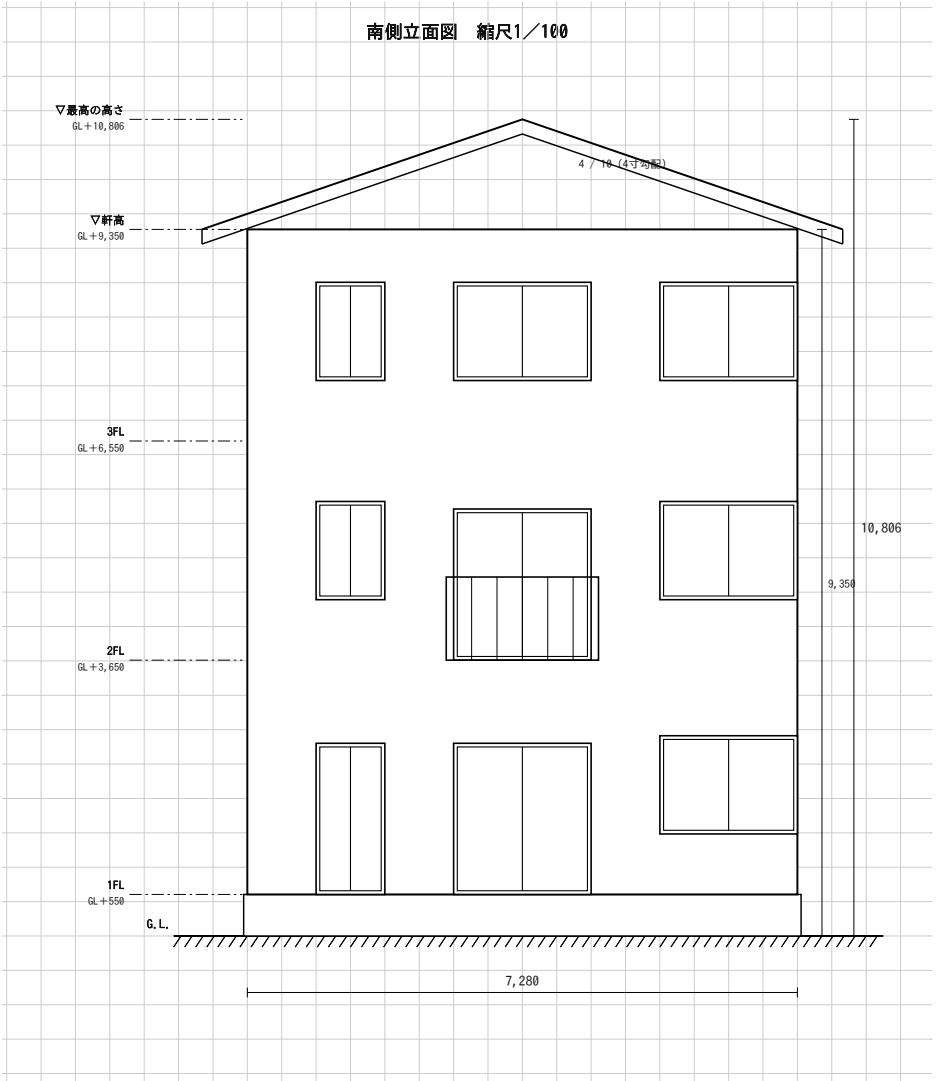

※ この2枚は「型 (8マス×10マス)」のもの。問題B (9マス)・C (7マス) は間口が違うので寸法を読みかえる。

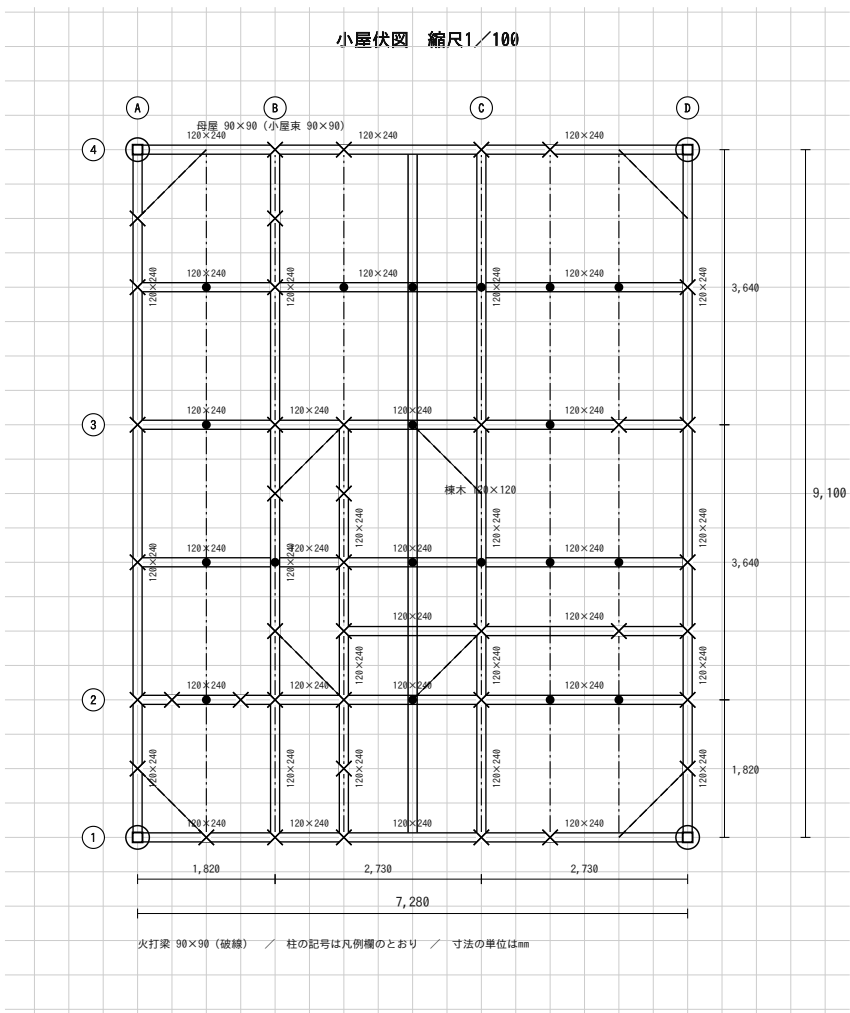

※ 梁は2階・3階の壁の上下と通り芯に必ず通し、残りを床梁φ910で埋める。小屋伏図は棟が南北方向・4寸勾配。3階の壁の上には桁。