
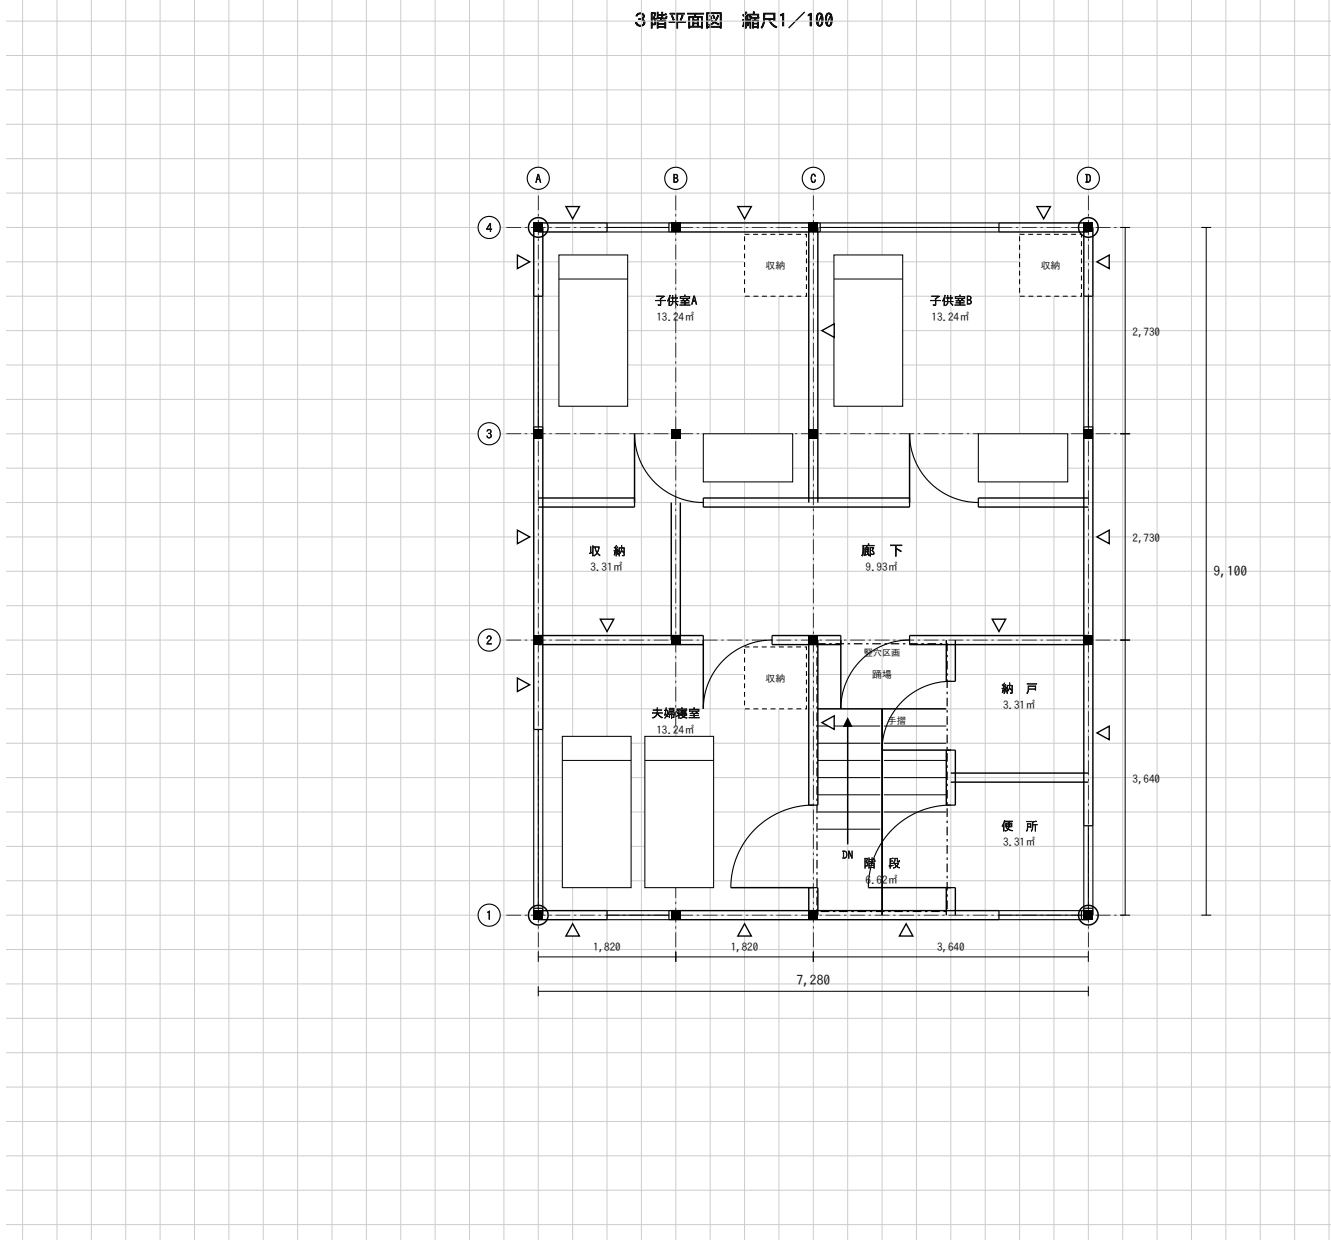
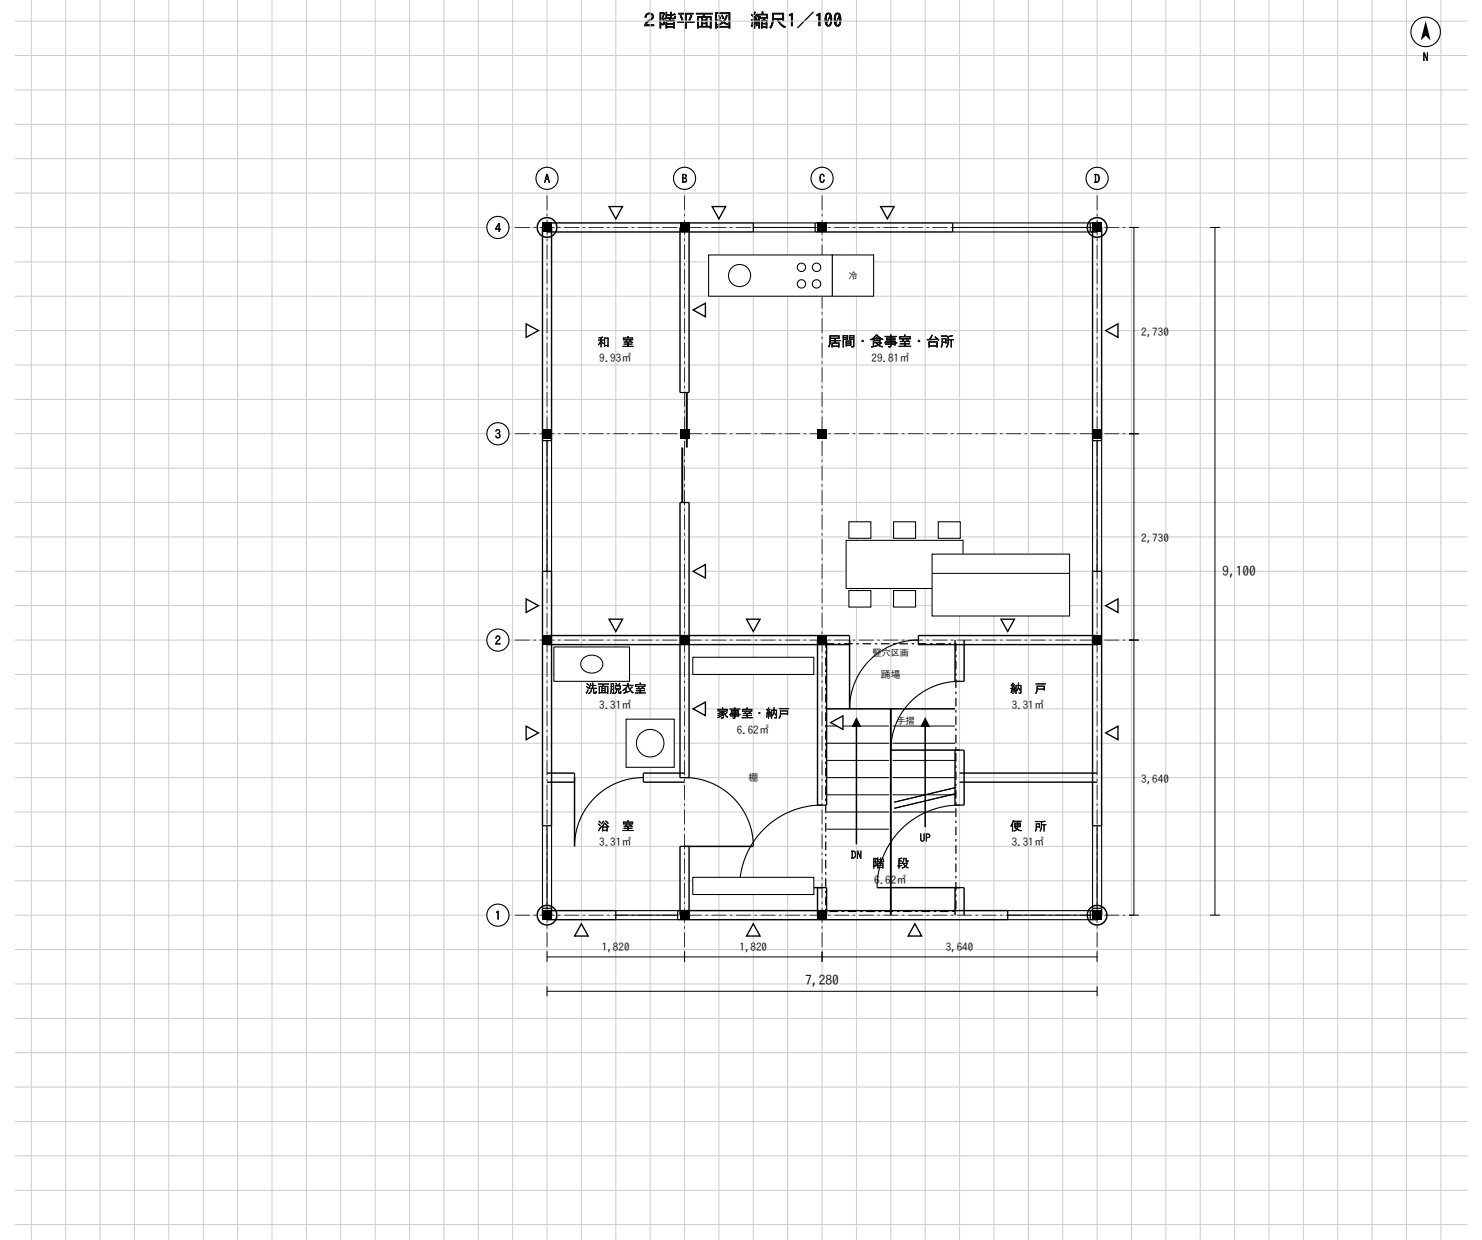


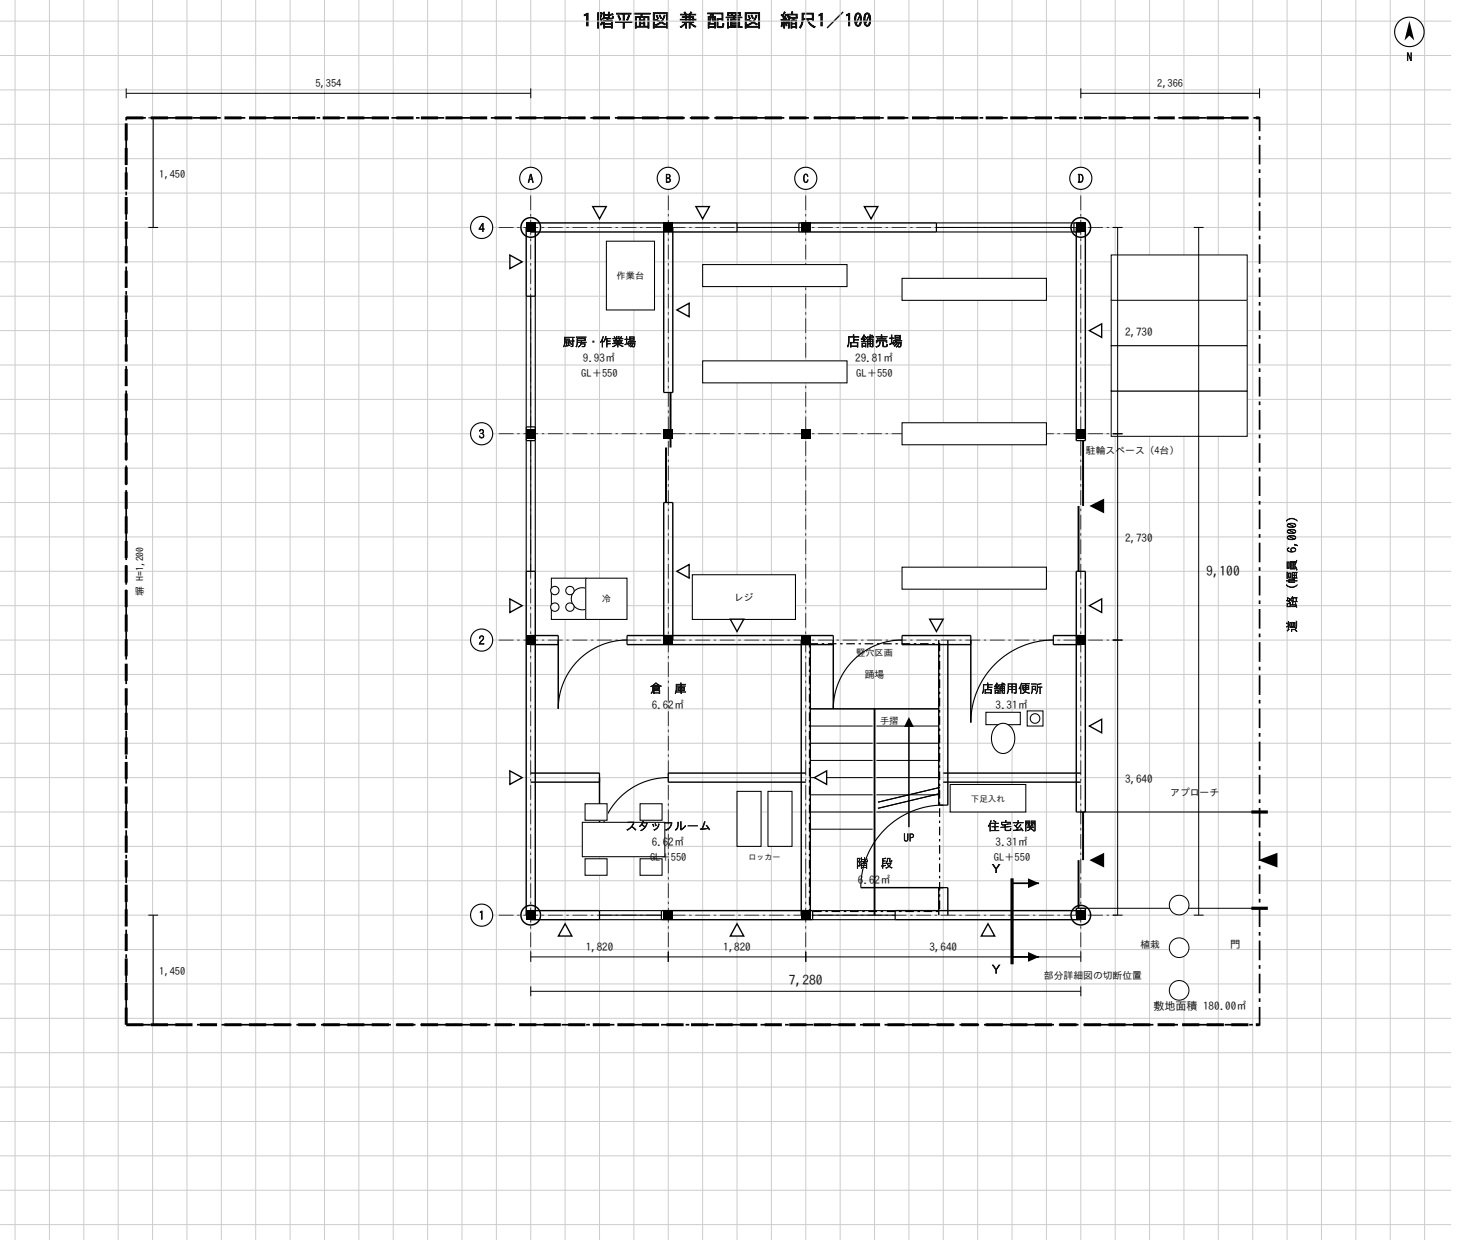

面 積 表

|            |                    |         |
|------------|--------------------|---------|
| 敷地面積       |                    | 180.00㎡ |
| 建築面積       | (計算式)<br>7.28×9.10 | 66.24㎡  |
| 床面積 1階 ア   | (計算式)<br>7.28×9.10 | 66.24㎡  |
| 2階 イ       | (計算式)<br>7.28×9.10 | 66.24㎡  |
| 3階 ウ       | (計算式)<br>7.28×9.10 | 66.24㎡  |
| 延べ面積 ア+イ+ウ |                    | 198.72㎡ |

小数点以下第3位以下は切り捨て。計算式は㎡単位で書く。

凡 例（床伏図兼小屋伏図の表示記号）

|    | 通し柱     | 1階の管柱   | 2階の管柱   | 重なる管柱 | 胴差・床梁・桁 | 火打梁   | 棟木      | 母屋    |
|----|---------|---------|---------|-------|---------|-------|---------|-------|
| 記号 |         |         |         |       |         |       |         |       |
| 寸法 | 120×120 | 120×120 | 120×120 | —     | 120×120 | 90×90 | 120×120 | 90×90 |



標準解答例

予想問題 D  
東側道路の併用住宅（美容室）  
木造3階建て ／ 8マス × 10マス（7,280 × 9,100）

※ 立面図・床伏図兼小屋伏図・部分詳細図は、別紙「共通図」を見てください。

この解答例のポイント

- ・道路が東なので売場を東面に向け、店舗出入口も東に取っている。
- ・階段を玄関の西どなりへ動かし、住宅の動線が売場を通らないようにした。
- ・通り芯の組み方を東西方向に変え、大梁のスパンを3,640以下に収めている。

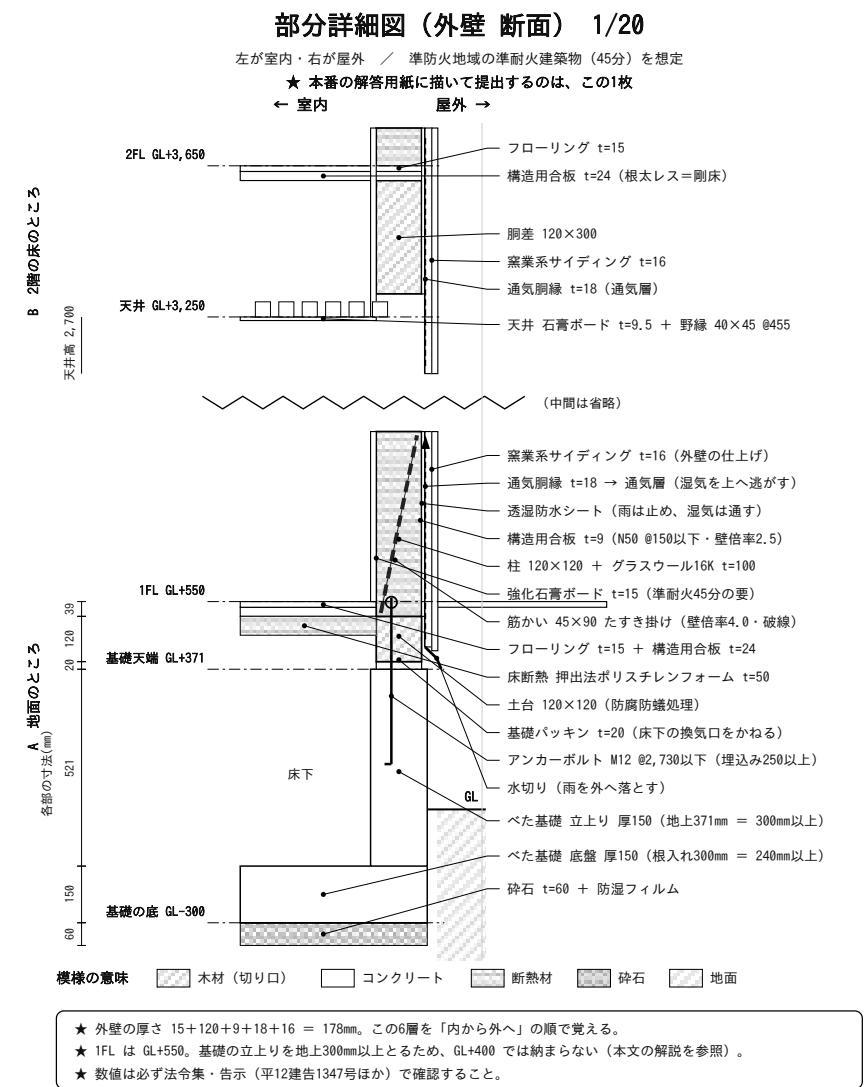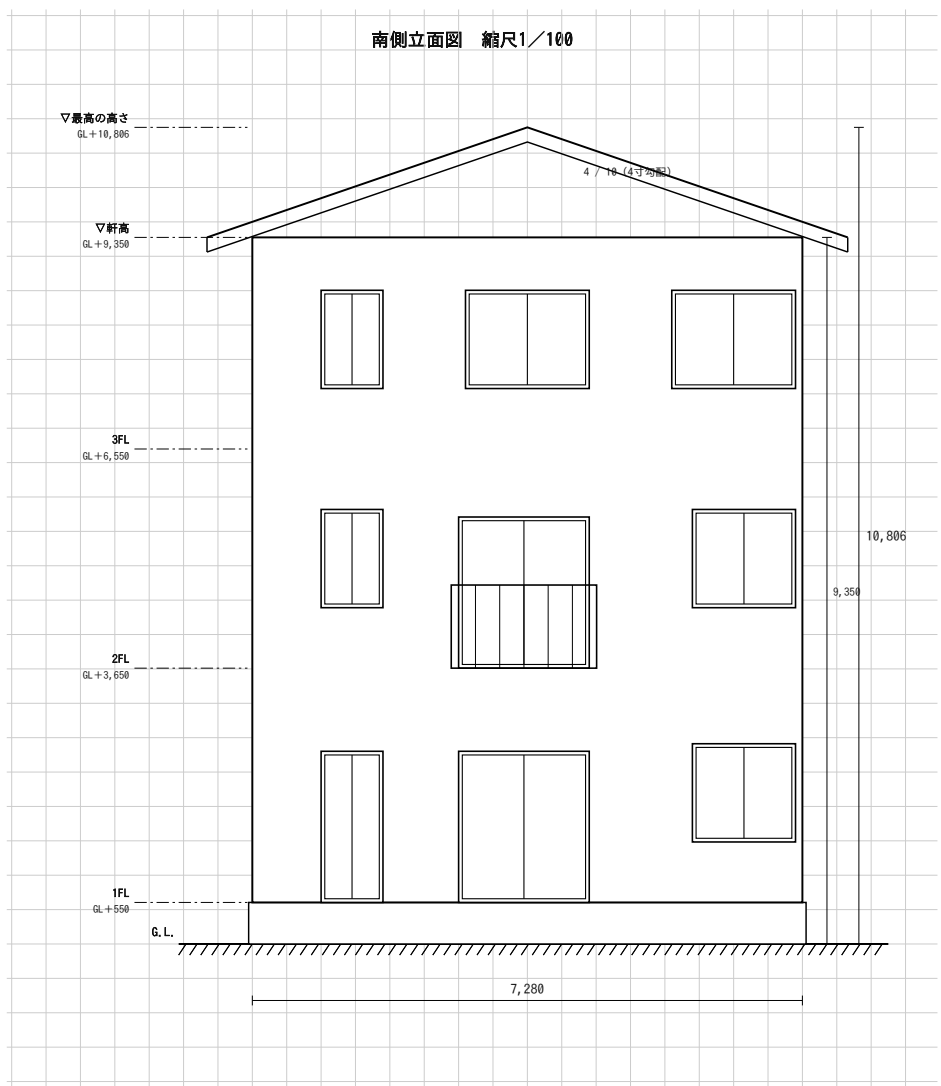

※ この2枚は「型（8マス×10マス）」のもの。問題B（9マス）・C（7マス）は間口が違うので寸法を読みかえる。

