
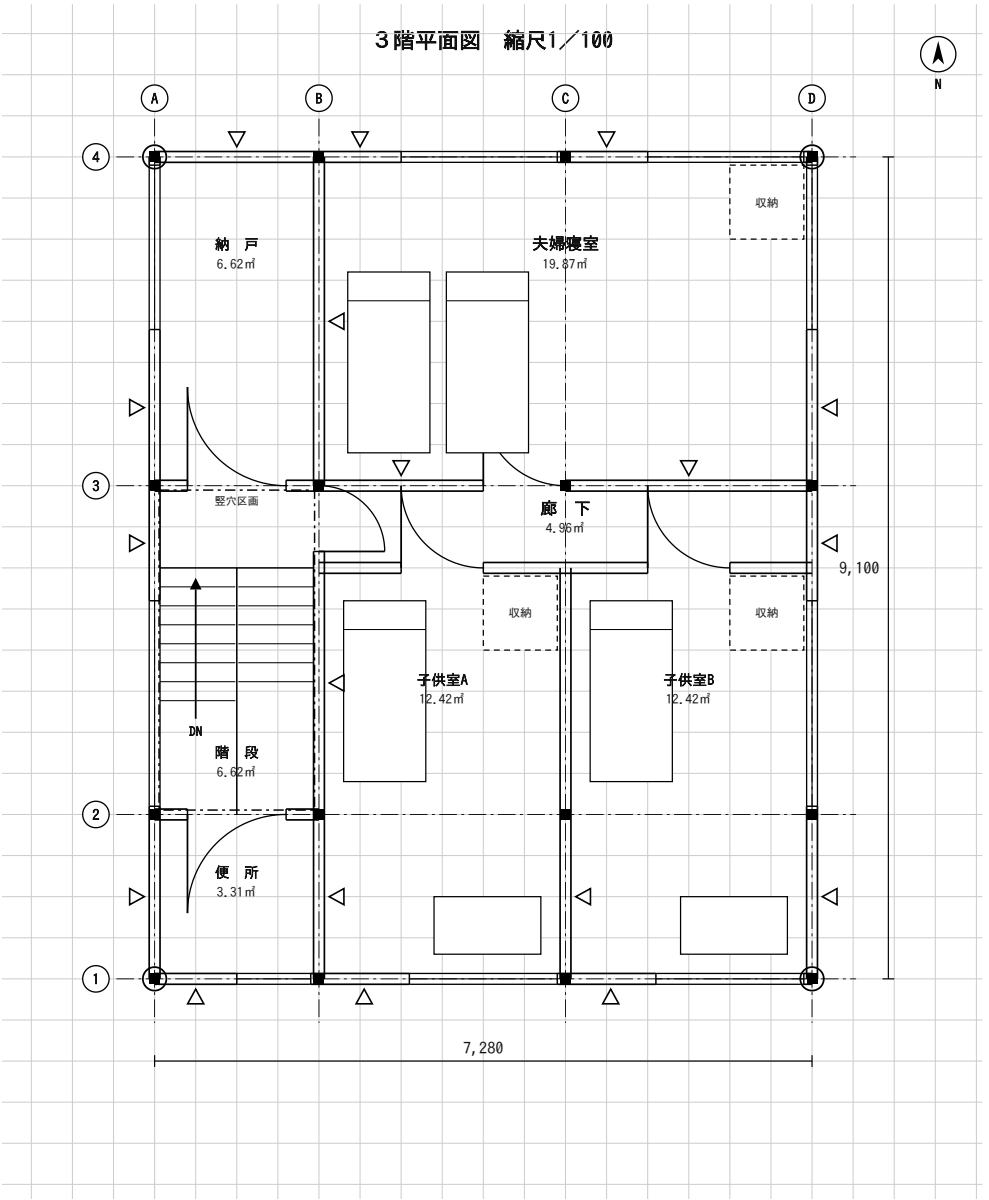
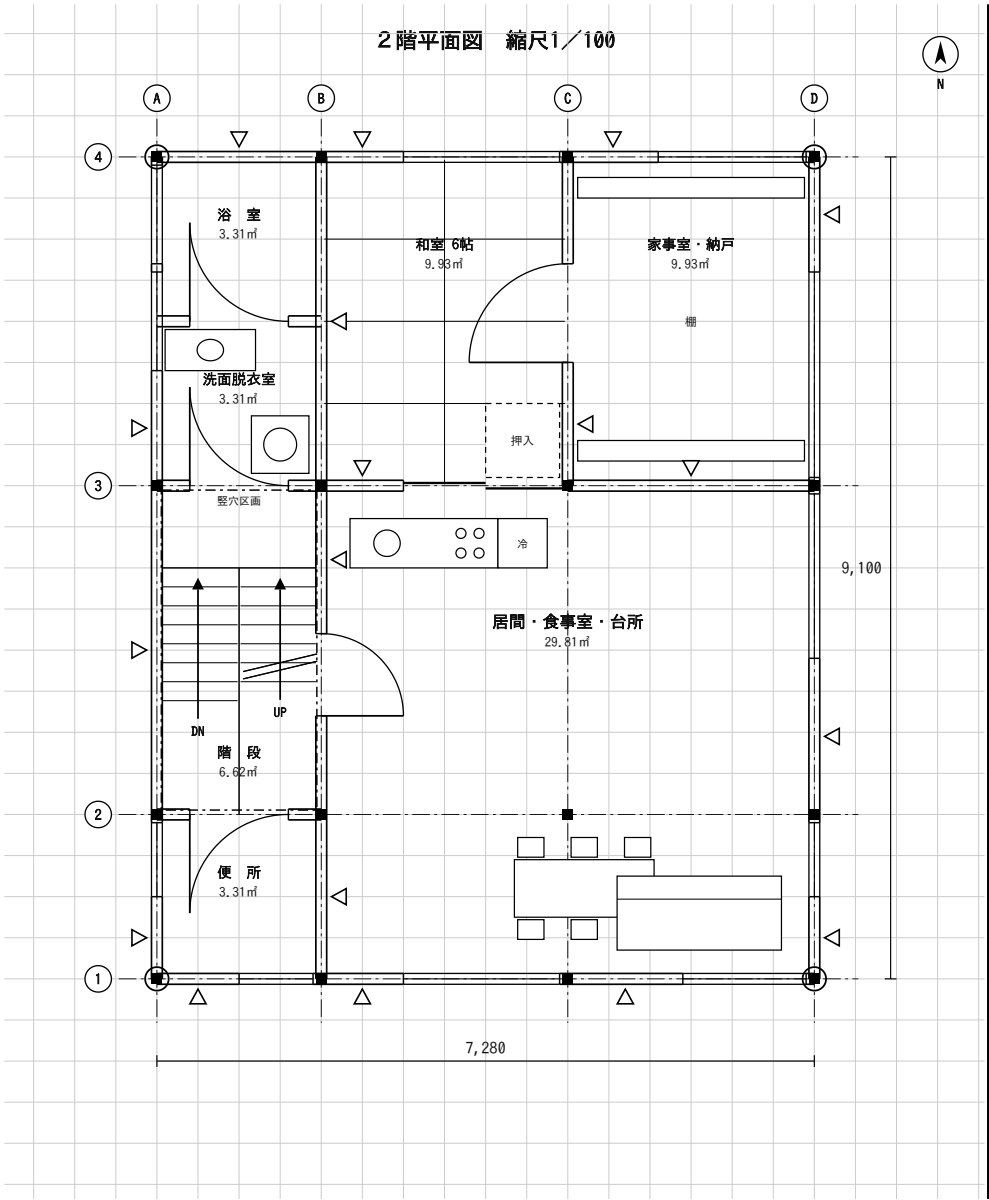


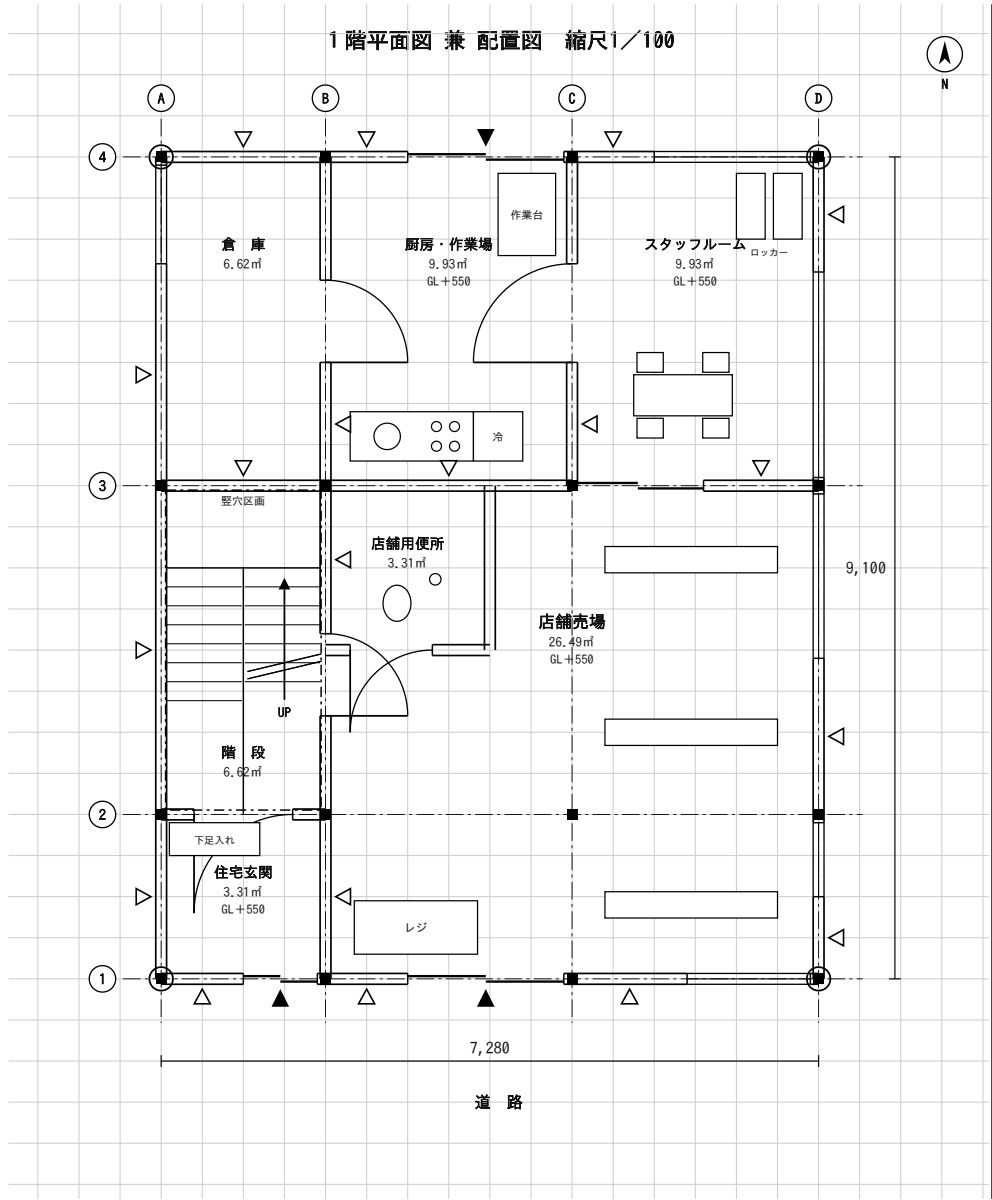

面 積 表

敷地面積		180.00㎡
建築面積	(計算式) 7.28×9.10	66.24㎡
床面積 1階 ア	(計算式) 7.28×9.10	66.24㎡
2階 イ	(計算式) 7.28×9.10	66.24㎡
3階 ウ	(計算式) 7.28×9.10	66.24㎡
延べ面積 ア+イ+ウ		198.72㎡

小数点以下第3位以下は切り捨て。計算式は㎡単位で書く。

凡 例（床伏図兼小屋伏図の表示記号）

通し柱	1階の管柱	2階の管柱	重なる管柱	胴差・床梁・桁	火打梁	棟木	母屋
記号							
寸法	120×120	120×120	—	120×120	90×90	120×120	90×90


標準解答例

予想問題 A
商店街に建つ併用住宅（物販店舗）
木造3階建て / 8マス × 10マス（7,280 × 9,100）

※ 立面図・床伏図兼小屋伏図・部分詳細図は、別紙「共通図」をご覧ください。

この解答例のポイント

- ・売場を道路（南）に面して最大に取り、住宅玄関と店舗出入口を分けている。
- ・店舗用便所を売場の角から直接入れるようにして、客が厨房を通らない。
- ・階段を西側の同じ位置に3階まで通し、直下率100%としている。

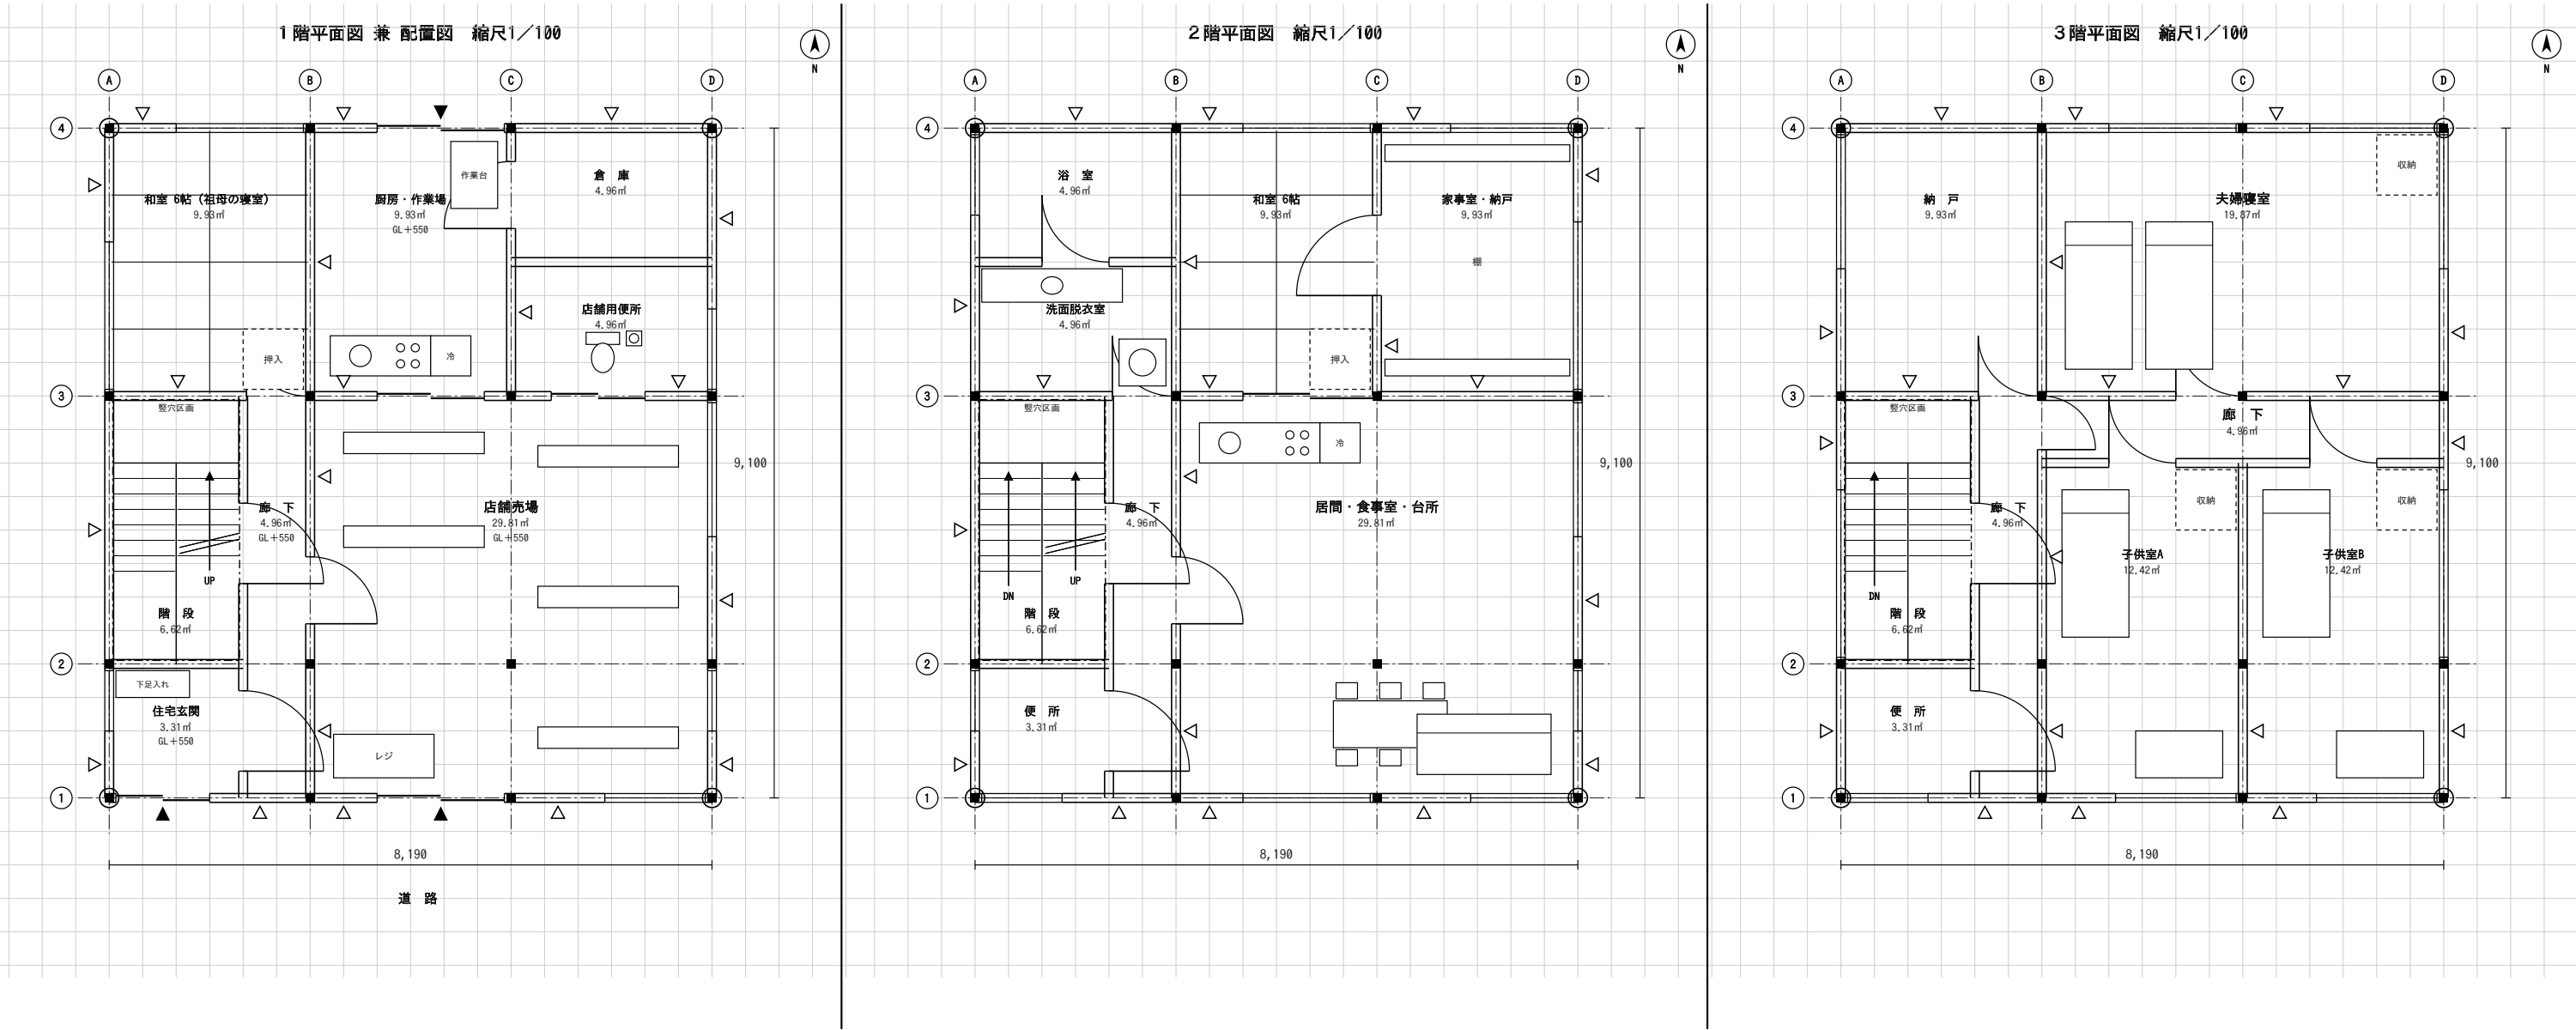

面積表

敷地面積		224.00㎡
建築面積	(計算式) 8.19×9.10	74.52㎡
床面積 1階 ア	(計算式) 8.19×9.10	74.52㎡
2階 イ	(計算式) 8.19×9.10	74.52㎡
3階 ウ	(計算式) 8.19×9.10	74.52㎡
延べ面積 ア+イ+ウ		223.56㎡

小数点以下第3位以下は切り捨て。計算式はm単位で書く。

凡 例（床伏図兼小屋伏図の表示記号）

通し柱	1階の管柱	2階の管柱	重なる管柱	胴差・床梁・桁	火打梁	棟木	母屋
記号							
寸法	120×120	120×120	120×120	—	120×120	90×90	90×90

標準解答例




予想問題 B

祖母と暮らす併用住宅（和菓子店）
木造3階建て / 9マス × 10マス (8,190 × 9,100)

※ 立面図・床伏図兼小屋伏図・部分詳細図は、別紙「共通図」をご覧ください。

この解答例のポイント

- ・1階の西側を3マス幅にして廊下を通し、その北に祖母の和室6帖を置いている。
- ・和室から便所・洗面へ廊下1本で行けるようにして、段差をなくしている。
- ・間口を9マスに広げたぶん、通り芯をA・B・C・Dの4本に組みかえている。

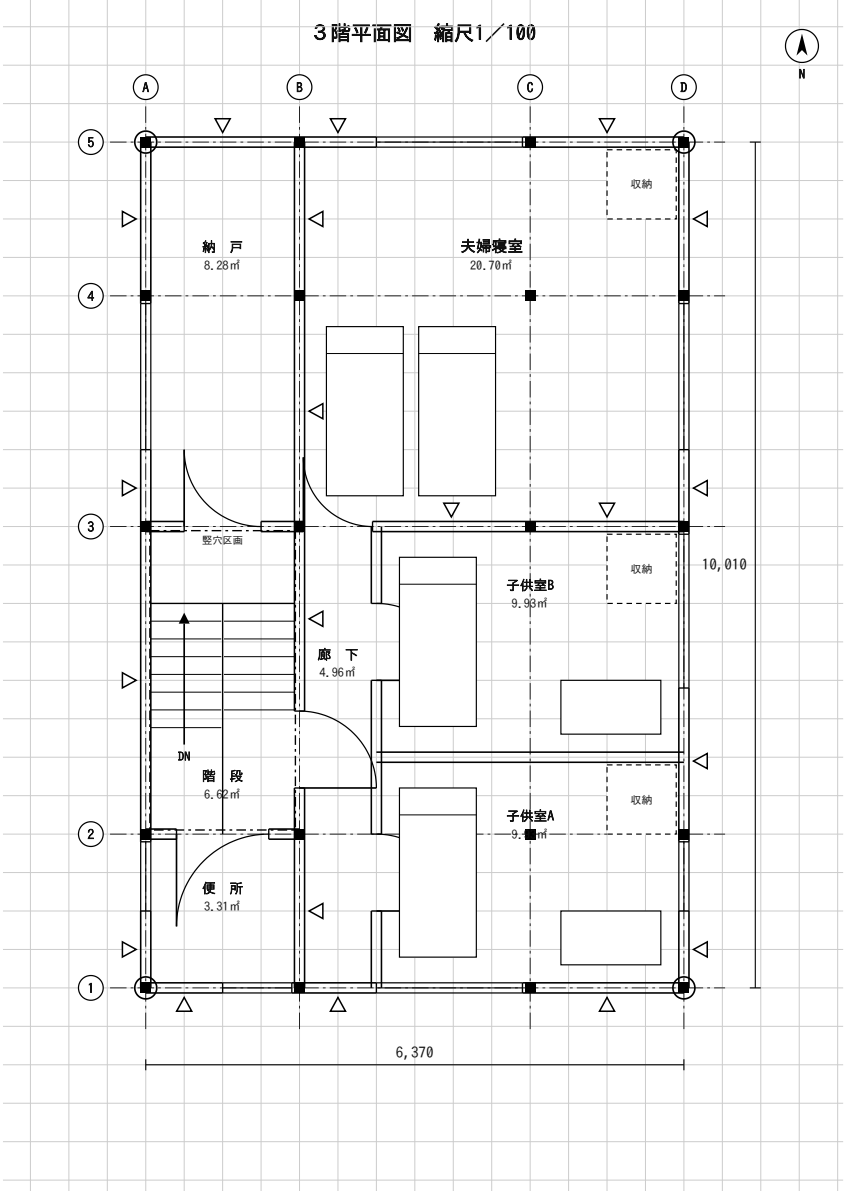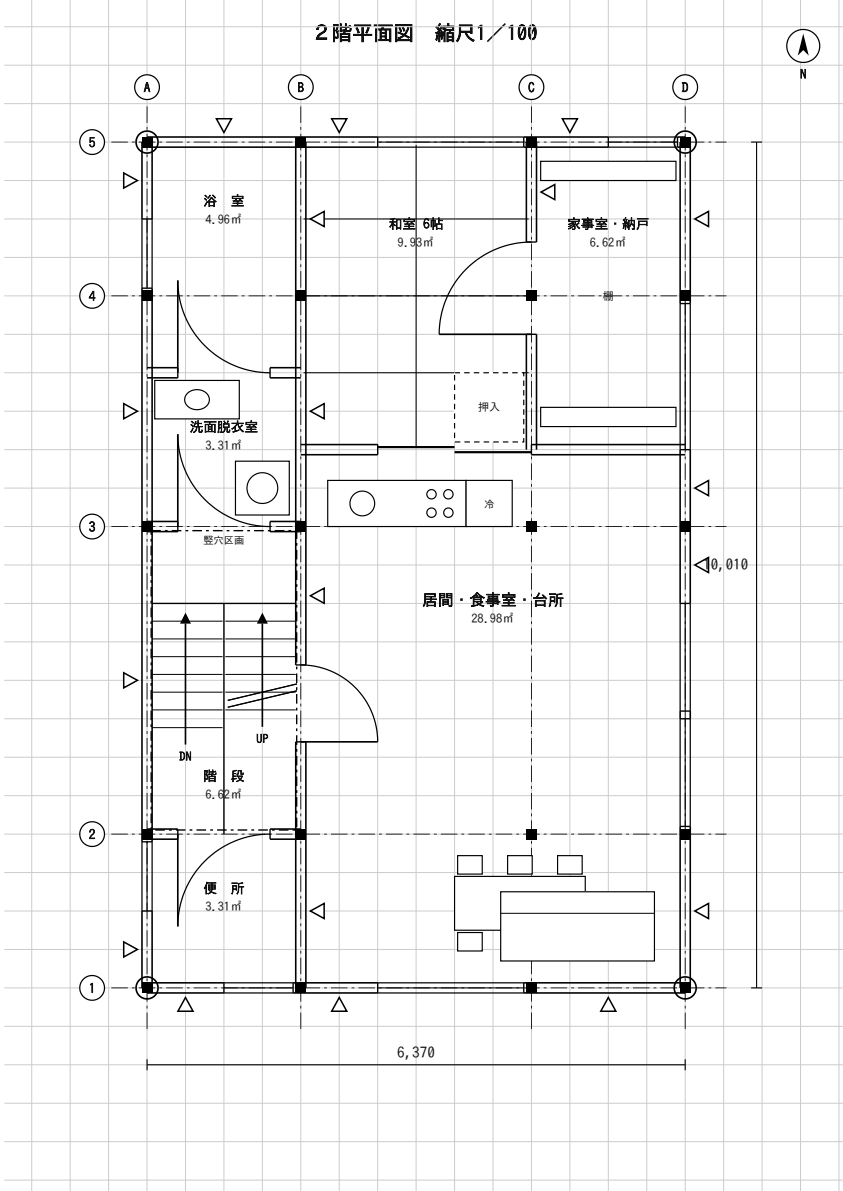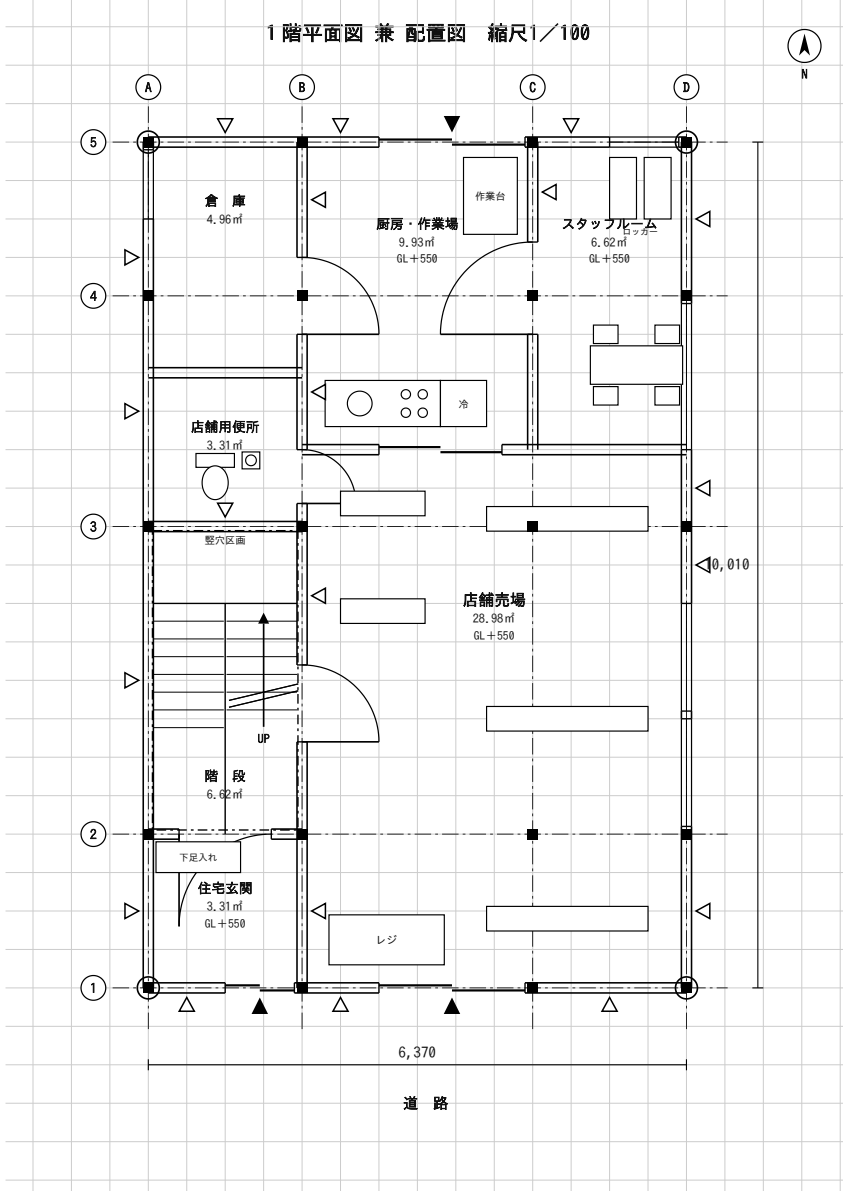

面積表

敷地面積		180.00 ㎡
建築面積	(計算式) 6.37×10.01	63.76 ㎡
床面積 1階 ア	(計算式) 6.37×10.01	63.76 ㎡
2階 イ	(計算式) 6.37×10.01	63.76 ㎡
3階 ウ	(計算式) 6.37×10.01	63.76 ㎡
延べ面積 ア+イ+ウ		191.28 ㎡

小数点以下第3位以下は切り捨て。計算式は㎡単位で書く。

凡 例（床伏図兼小屋伏図の表示記号）

	通し柱	1階の管柱	2階の管柱	重なる管柱	胴差・床梁・桁	火打梁	棟木	母屋
記号								
寸法	120×120	120×120	120×120	—	120×120	90×90	120×120	90×90

標準解答例




予想問題 C

間口の狭い敷地の併用住宅（喫茶店）
木造3階建て / 7マス × 11マス (6,370 × 10,010)

※ 立面図・床伏図兼小屋伏図・部分詳細図は、別紙「共通図」をご覧ください。

この解答例のポイント

- ・ 間口が狭いので7マス×11マスとし、売場を奥へ長く取っている。
- ・ 水まわりを西の列にそろえて、1階から3階まで配管の位置を合わせている。
- ・ 通り芯を1・2・3・4・5の5本にして、奥行方向のスパンを2,730以下に抑えた。

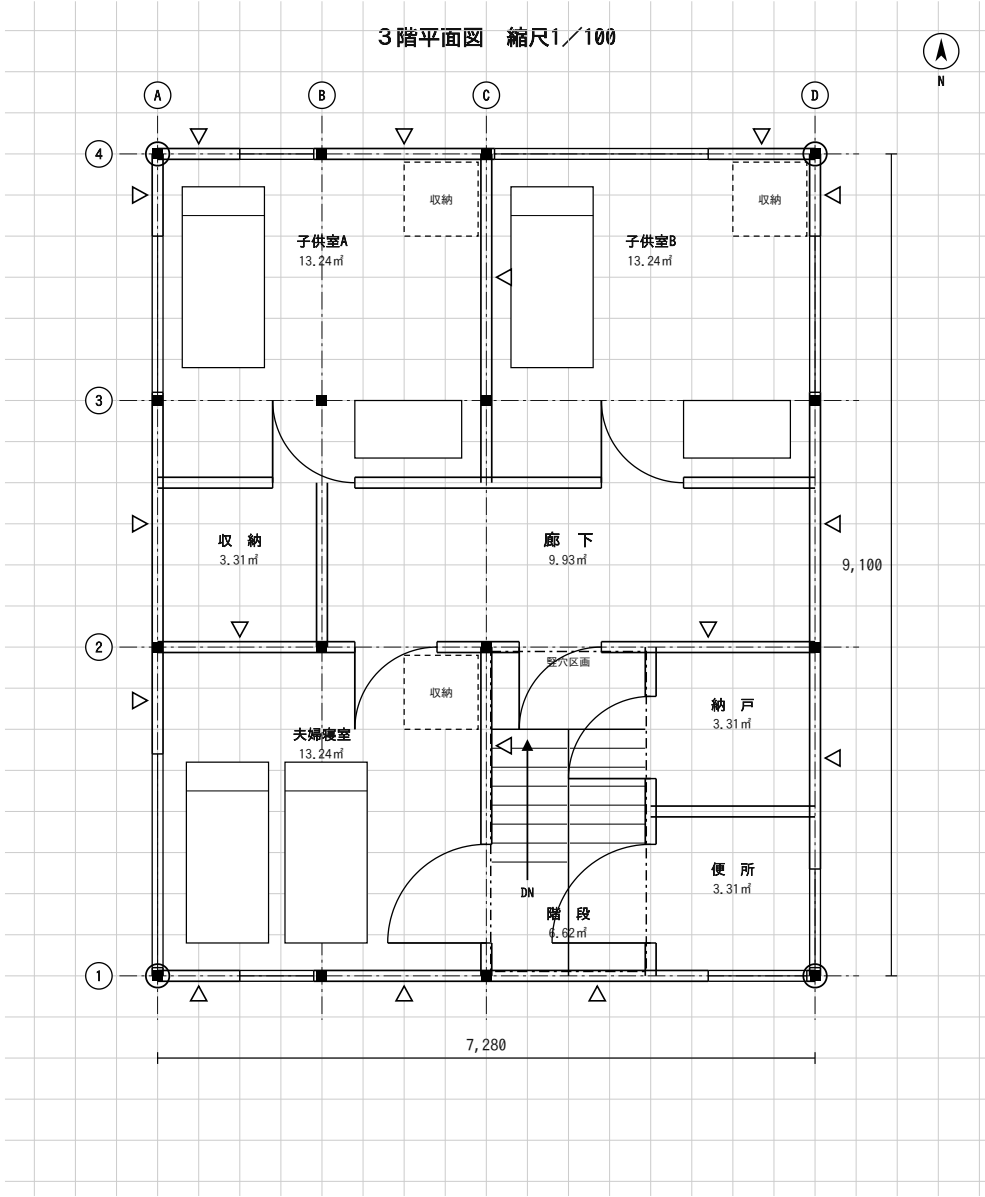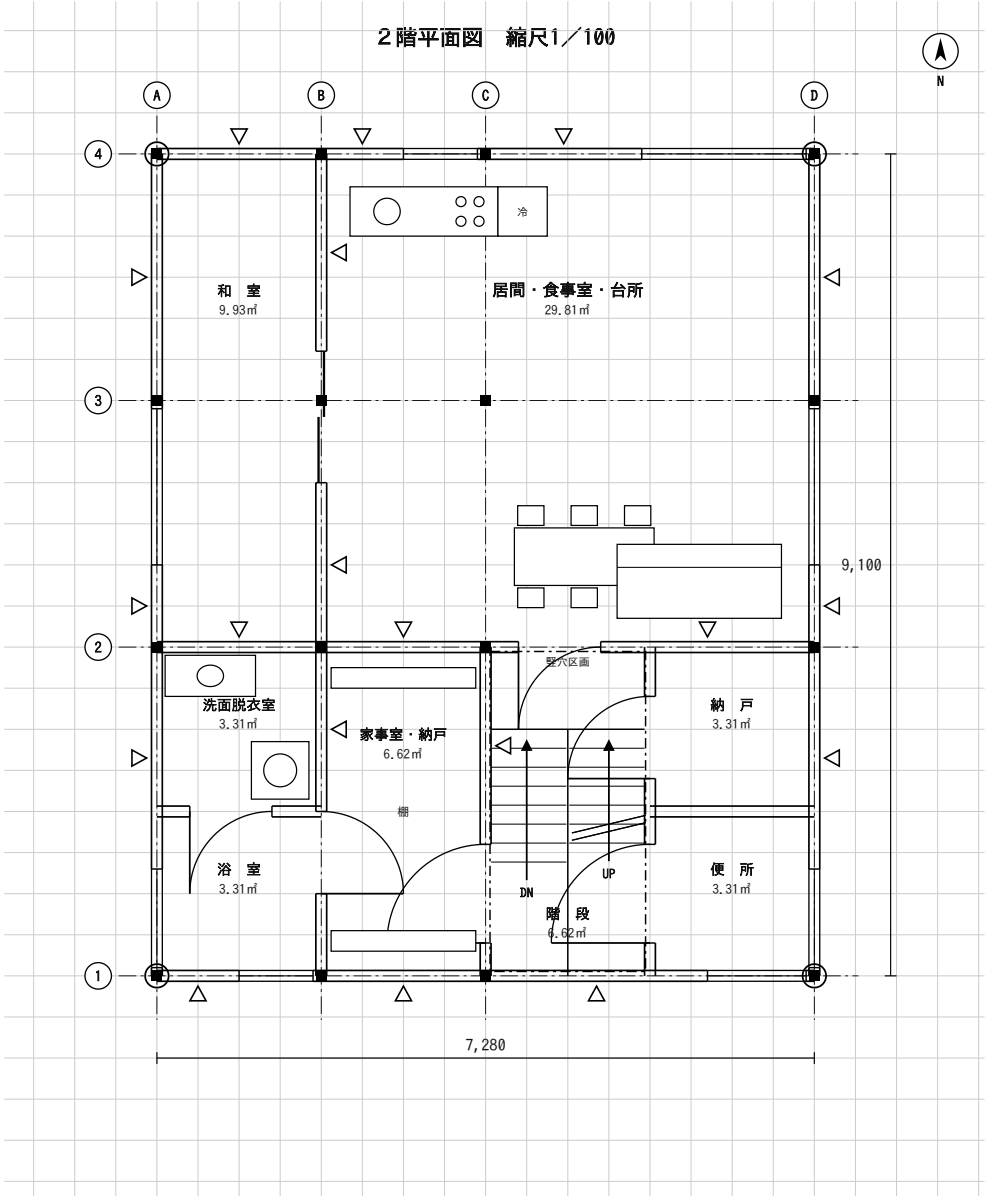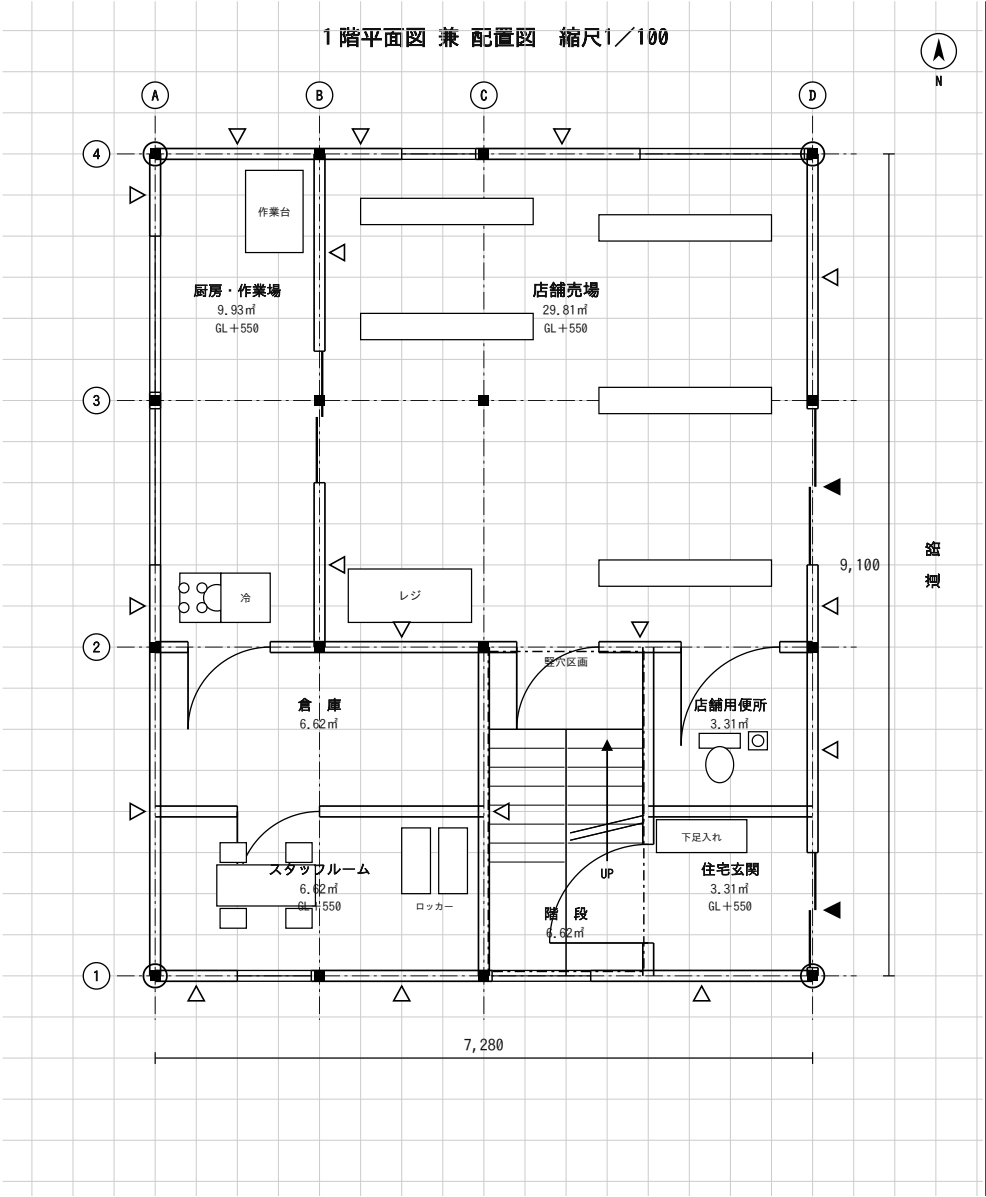

面 積 表

敷地面積		180.00㎡
建築面積	(計算式) 7.28×9.10	66.24㎡
床面積 1階 ア	(計算式) 7.28×9.10	66.24㎡
2階 イ	(計算式) 7.28×9.10	66.24㎡
3階 ウ	(計算式) 7.28×9.10	66.24㎡
延べ面積 ア+イ+ウ		198.72㎡

小数点以下第3位以下は切り捨て。計算式は㎡単位で書く。

凡 例（床伏図兼小屋伏図の表示記号）

	通し柱	1階の管柱	2階の管柱	重なる管柱	胴差・床梁・桁	火打梁	棟木	母屋
記号								
寸法	120×120	120×120	120×120	—	120×120	90×90	120×120	90×90

標 準 解 答 例




予想問題 D

東側道路の併用住宅（美容室）
木造3階建て / 8マス × 10マス（7,280 × 9,100）

※ 立面図・床伏図兼小屋伏図・部分詳細図は、別紙「共通図」をご覧ください。

この解答例のポイント

- ・道路が東なので売場を東面に向け、店舗出入口も東に取っている。
- ・階段を玄関の西どなりへ動かし、住宅の動線が売場を通らないようにした。
- ・通り芯の組み方を東西方向に変え、大梁のスパンを3,640以下に収めている。

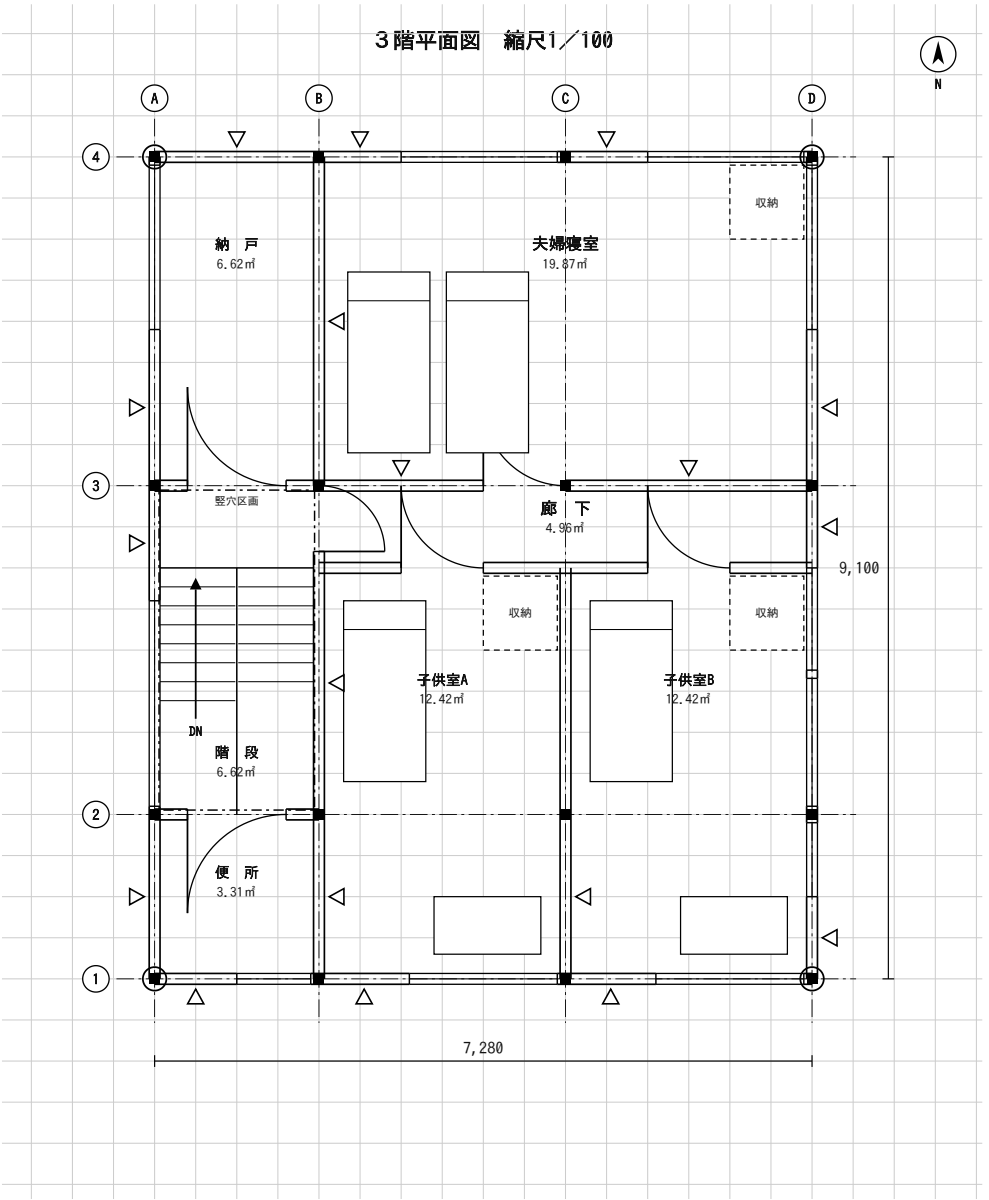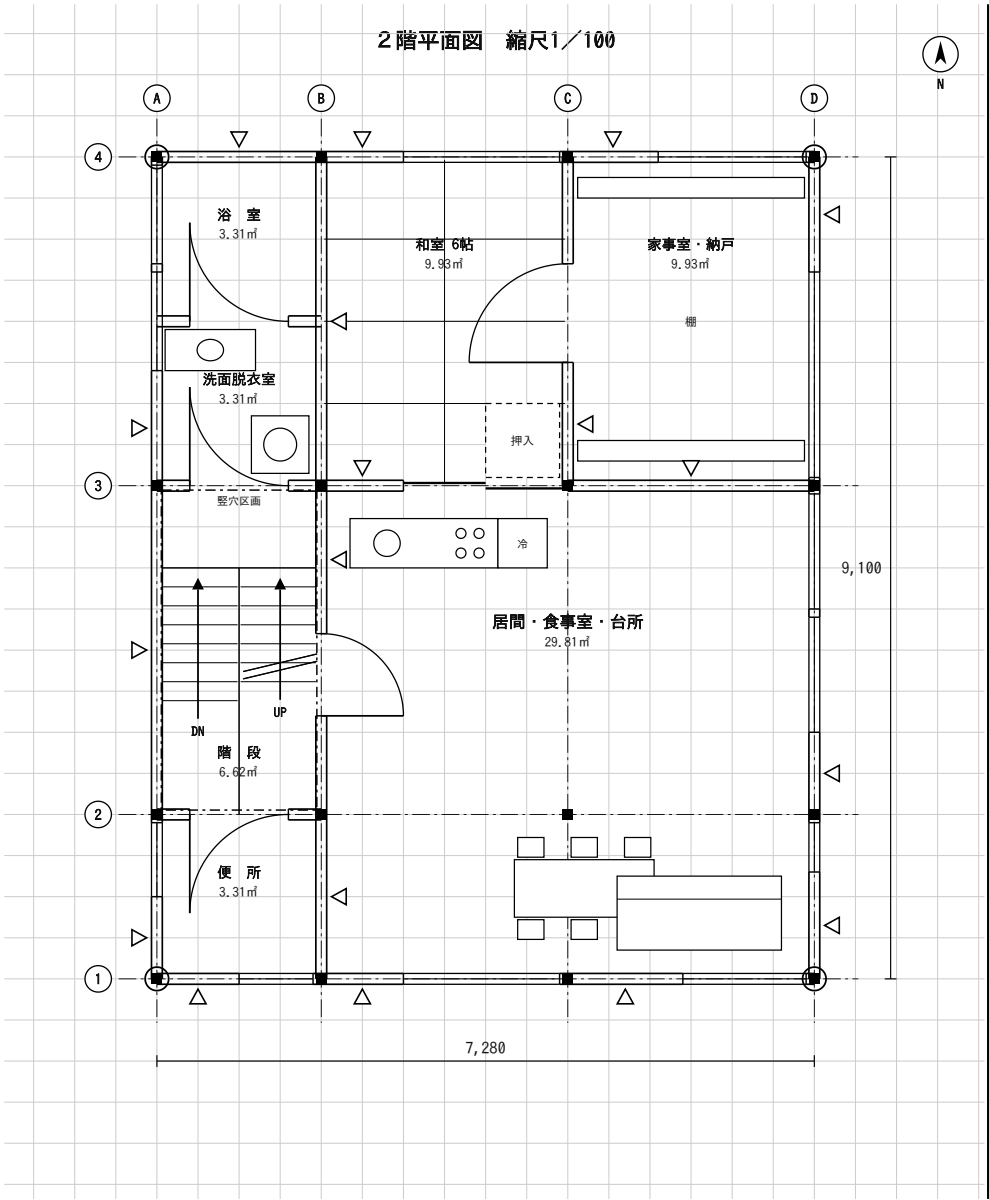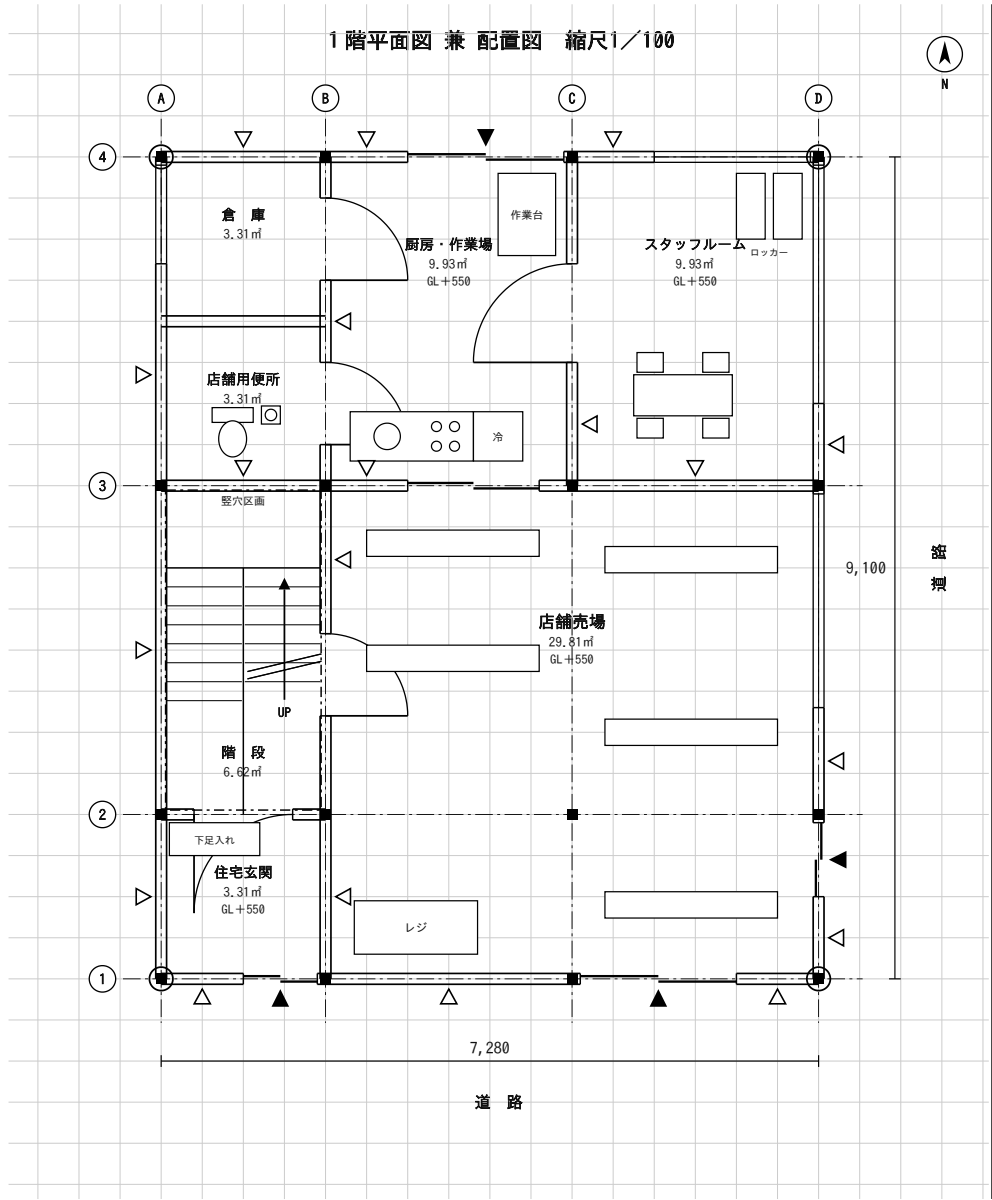

面 積 表

敷地面積		182.00 ㎡
建築面積	(計算式) 7.28×9.10	66.24 ㎡
床面積 1階 ア	(計算式) 7.28×9.10	66.24 ㎡
2階 イ	(計算式) 7.28×9.10	66.24 ㎡
3階 ウ	(計算式) 7.28×9.10	66.24 ㎡
延べ面積 ア+イ+ウ		198.72 ㎡

小数点以下第3位以下は切り捨て。計算式は㎡単位で書く。

凡 例（床伏図兼小屋伏図の表示記号）

通し柱	1階の管柱	2階の管柱	重なる管柱	胴差・床梁・桁	火打梁	棟木	母屋
記号							
寸法	120×120	120×120	120×120	—	120×120	90×90	90×90

標 準 解 答 例




予想問題 E

南東の角地に建つ併用住宅（パン店）
木造3階建て / 8マス × 10マス（7,280 × 9,100）

※ 立面図・床伏図兼小屋伏図・部分詳細図は、別紙「共通図」をご覧ください。

この解答例のポイント

- ・ 南と東の2面が道路なので、店舗出入口を角に向けて開いている。
- ・ 東面にも窓を取り、売場と住宅の採光を両方から確保している。
- ・ 角地の建蔽率の割増し（法53条3項）を使える敷地としている。

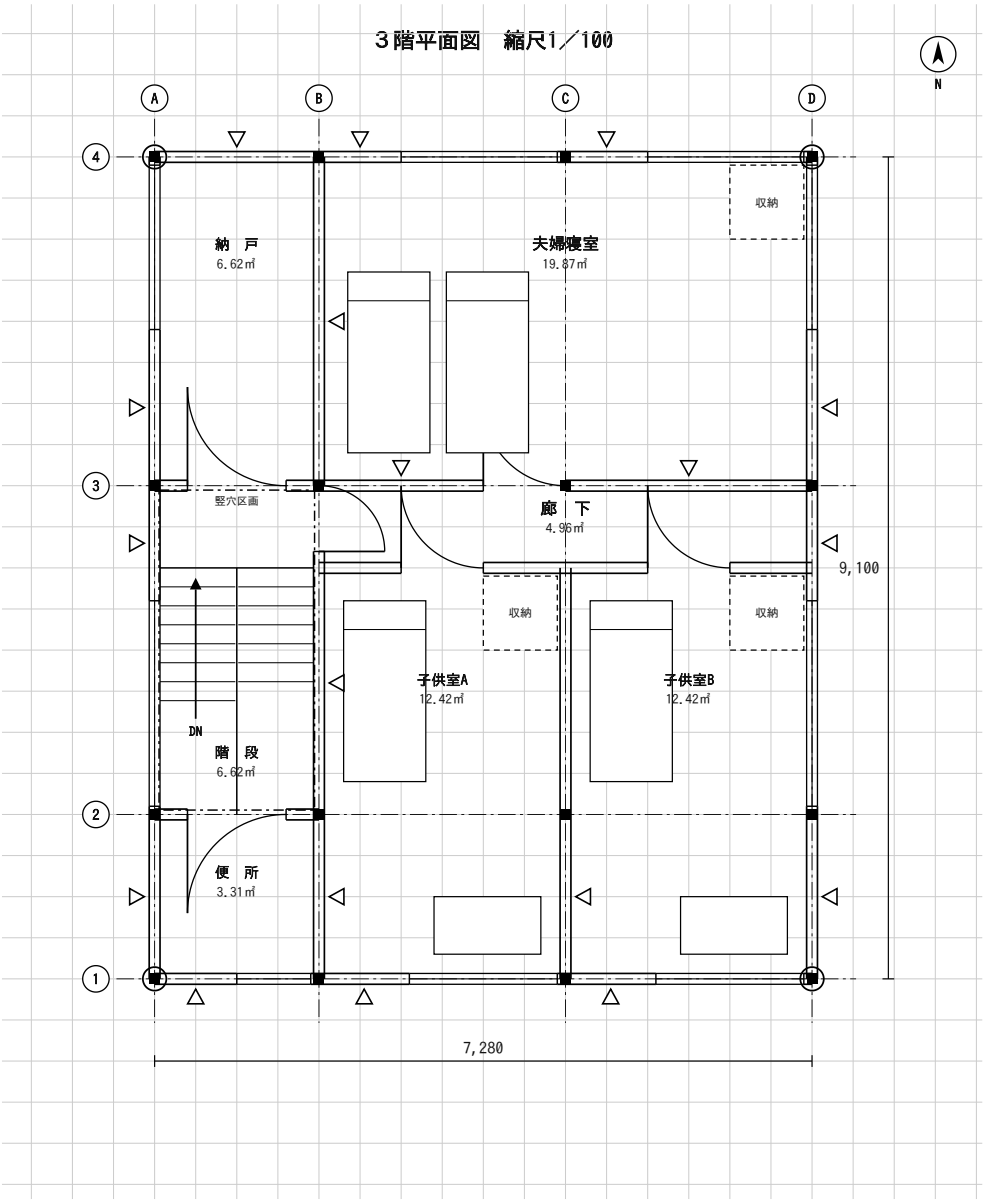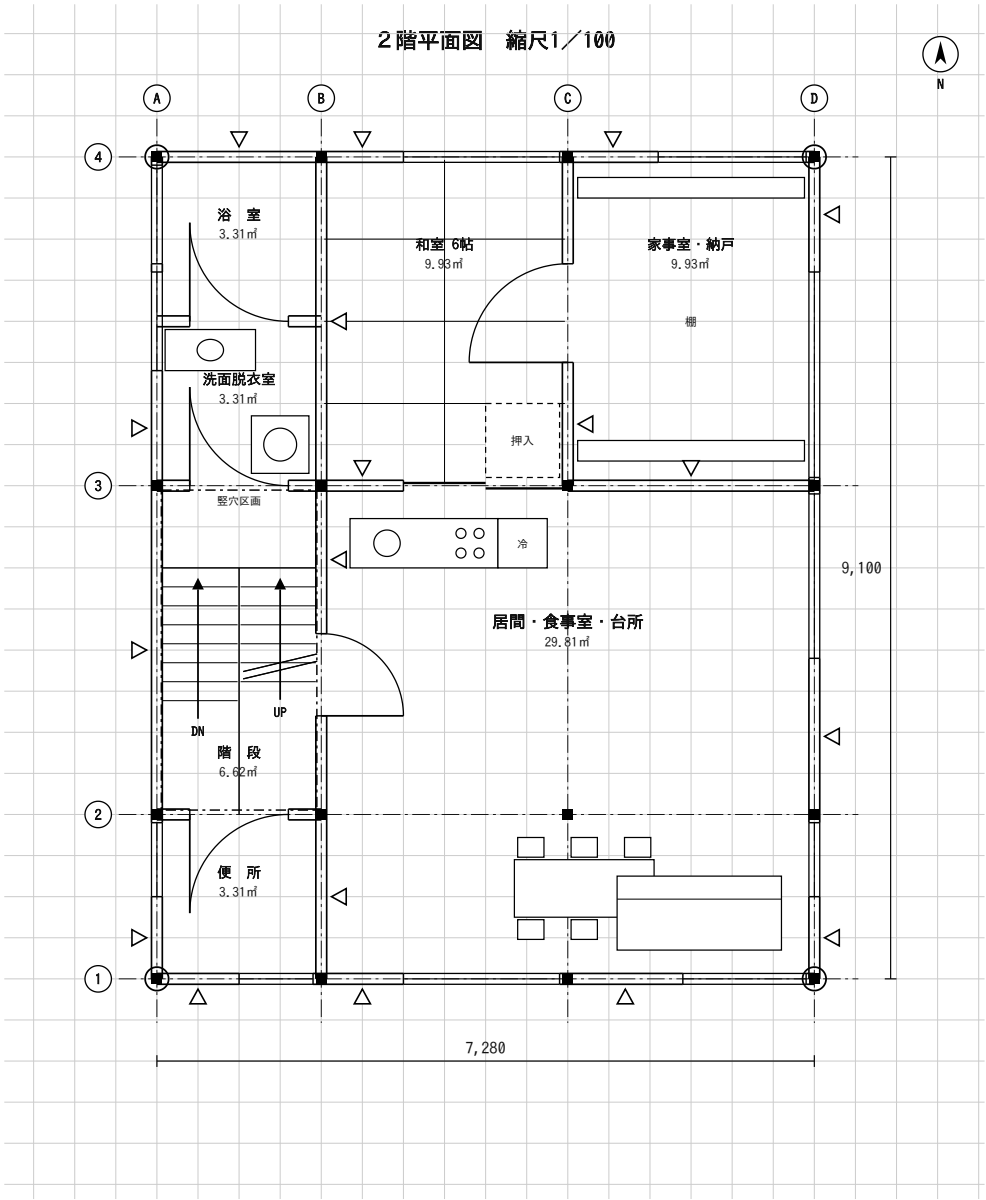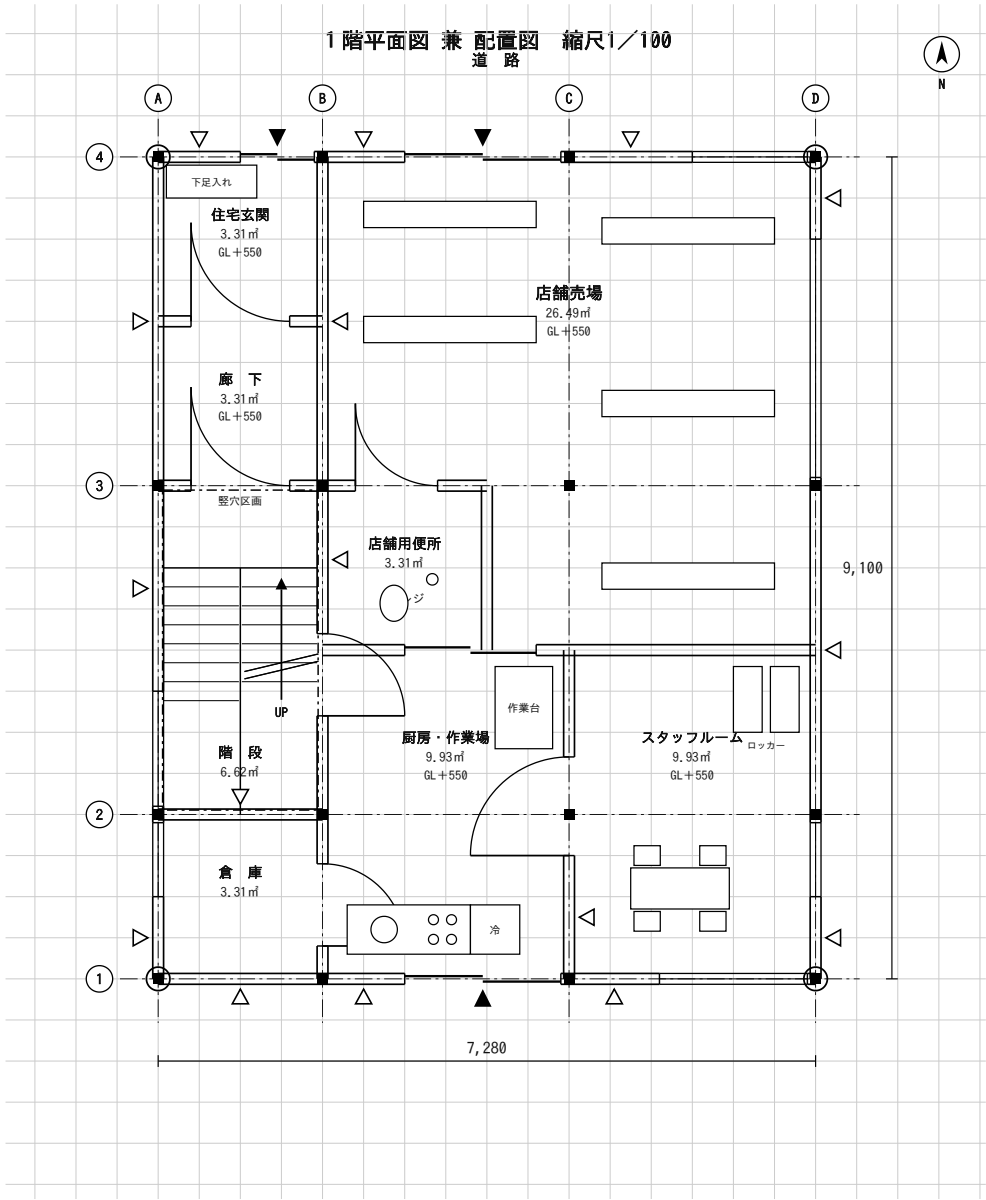

面 積 表

敷地面積		180.00 ㎡
建築面積	(計算式) 7.28×9.10	66.24 ㎡
床面積 1階 ア	(計算式) 7.28×9.10	66.24 ㎡
2階 イ	(計算式) 7.28×9.10	66.24 ㎡
3階 ウ	(計算式) 7.28×9.10	66.24 ㎡
延べ面積 ア+イ+ウ		198.72 ㎡

小数点以下第3位以下は切り捨て。計算式はm単位で書く。

凡 例（床伏図兼小屋伏図の表示記号）

通し柱	1階の管柱	2階の管柱	重なる管柱	胴差・床梁・桁	火打梁	棟木	母屋
記号							
寸法	120×120	120×120	—	120×120	90×90	120×120	90×90

標 準 解 答 例

予想問題 F
北側道路の併用住宅（書店）
木造3階建て / 8マス × 10マス（7,280 × 9,100）

※ 立面図・床伏図兼小屋伏図・部分詳細図は、別紙「共通図」をご覧ください。


この解答例のポイント

- ・道路が北なので、1階だけ南北を入れかえて店舗を北（道路側）に向けた。
- ・階段の位置は動かさないで、2階・3階は型のまま使える。
- ・住宅の居室は南側に集め、日当たりを確保している。

南立面図 (妻面) 1/100

棟が南北方向なので、南から見ると屋根は三角形に見える

切妻・4寸勾配 / 軒の出 600

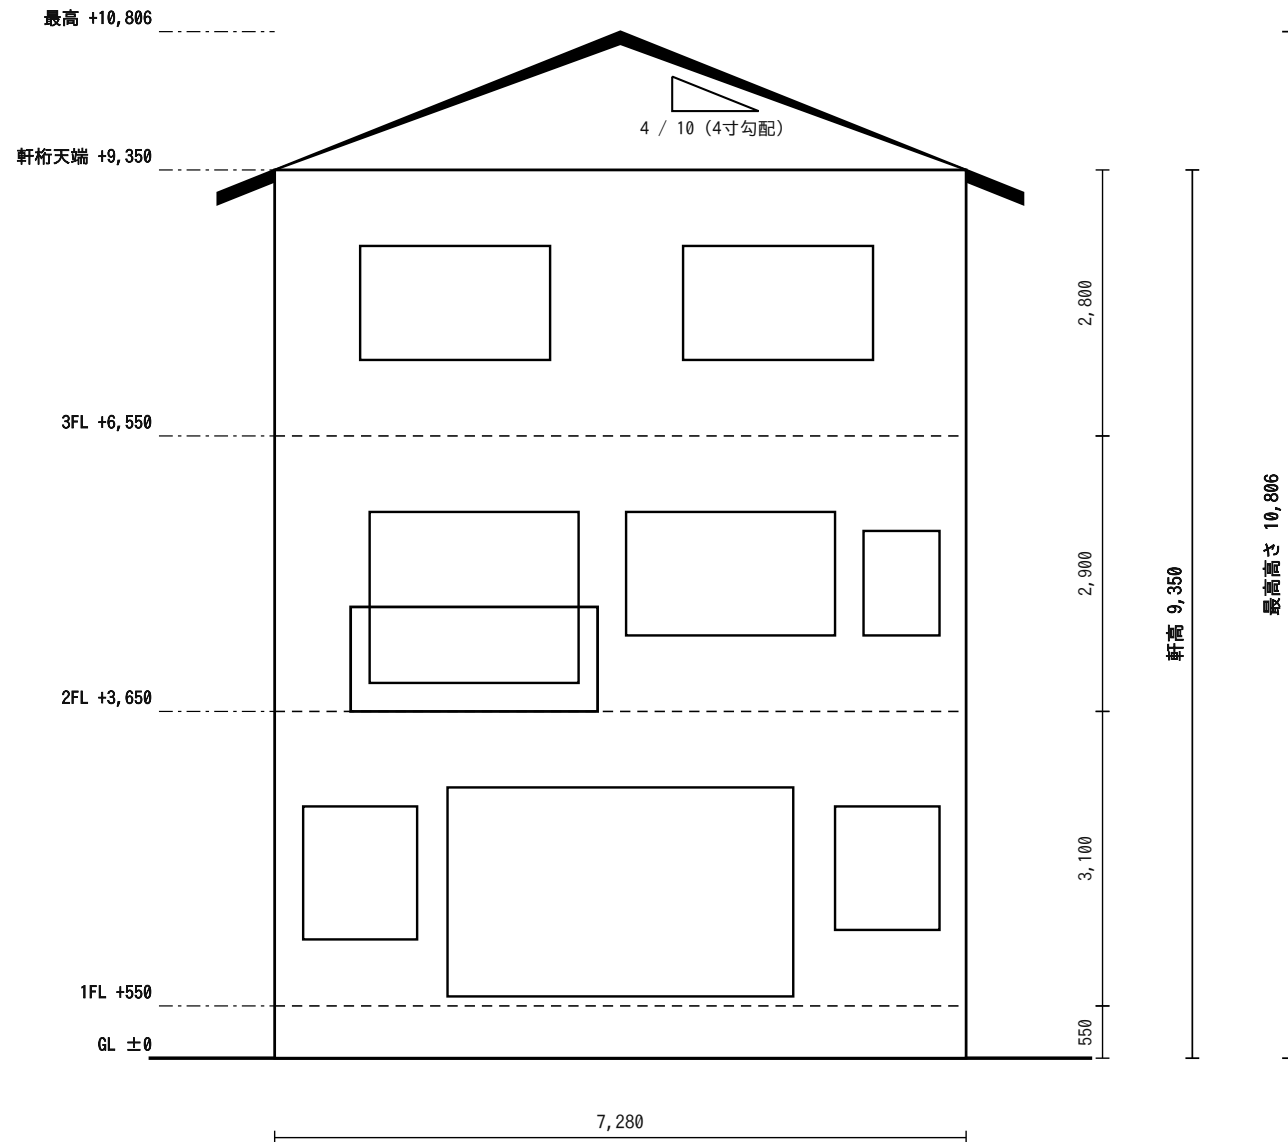
$$\text{棟までの高さ} = 3,640 \times 0.4 = 1,456 \rightarrow 9,350 + 1,456 = 10,806$$


※ 1FL を GL+400 とする型では 軒高 9,200 / 最高 10,656 になる。どちらか一方に必ずそろえること。

部分詳細図（外壁 断面） 1/20

左が室内・右が屋外　／　準防火地域の準耐火建築物（45分）を想定

★ 本番の解答用紙に描いて提出するのは、この1枚

← 室内 屋外 →

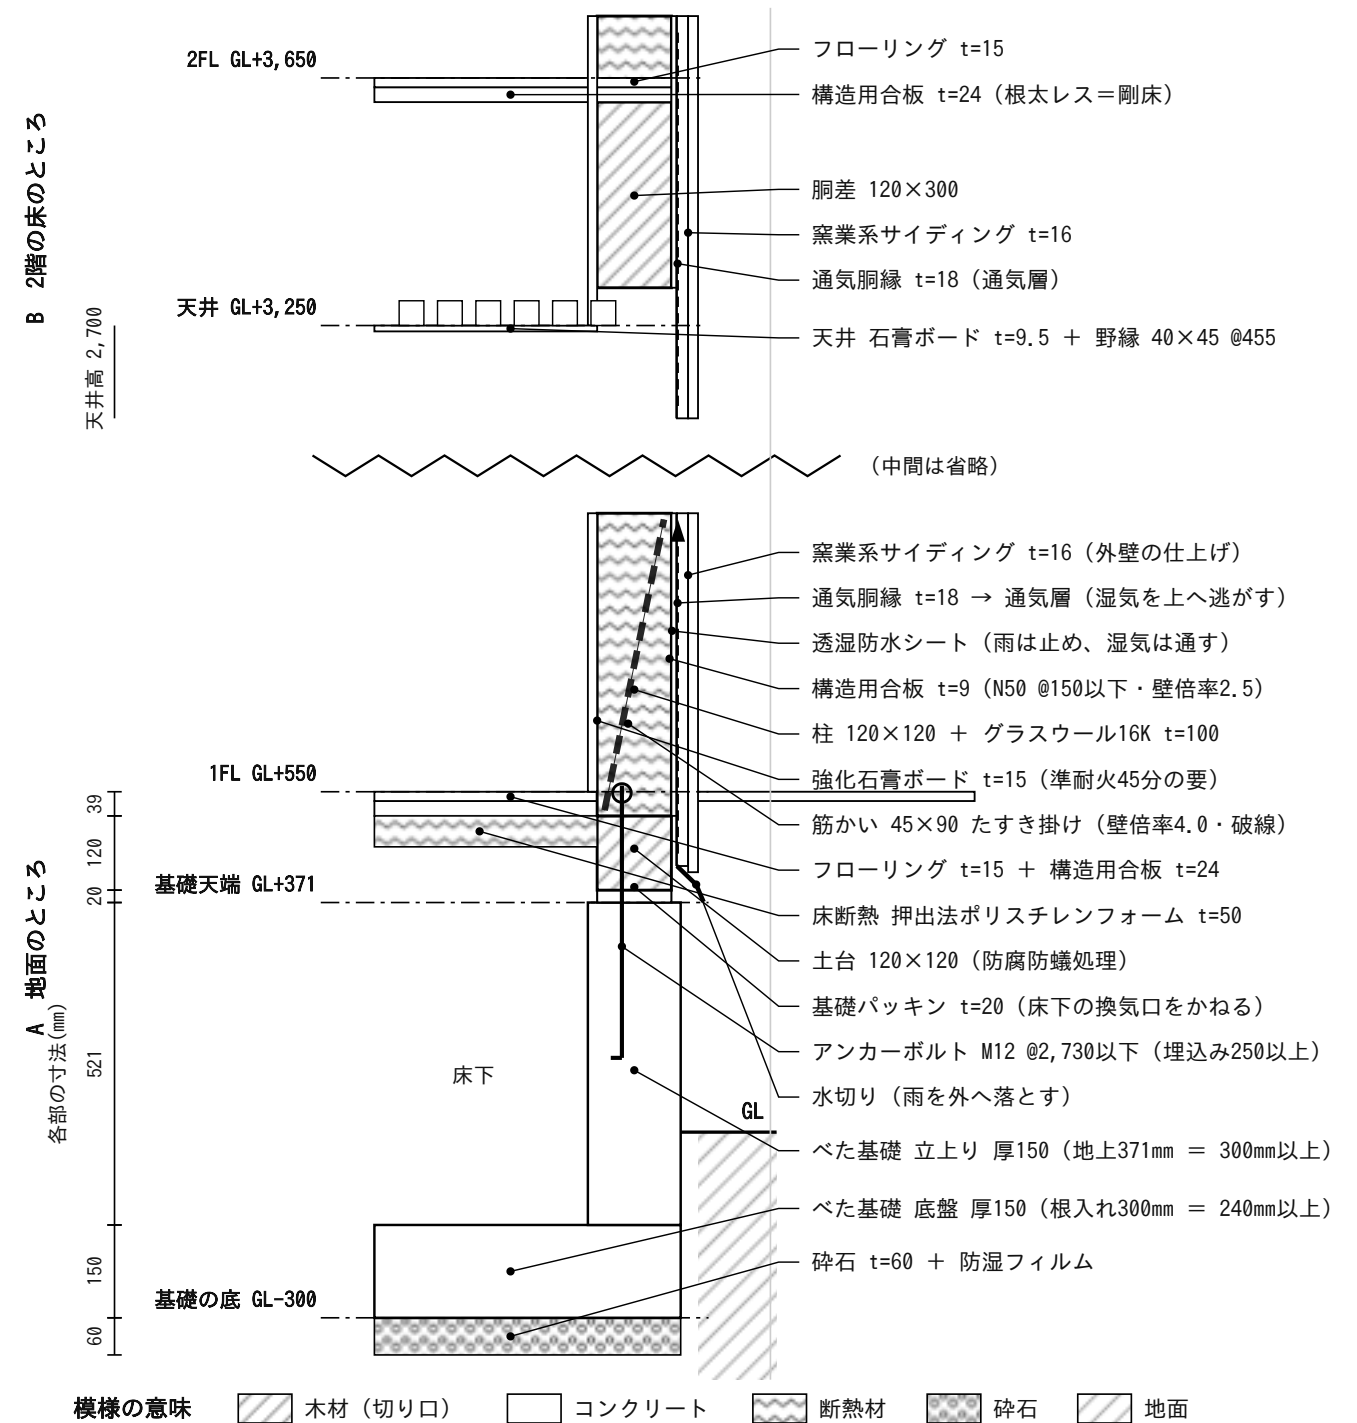

★ 外壁の厚さ $15+120+9+18+16 = 178\text{mm}$ 。この6層を「内から外へ」の順で覚える。


★ 1FL は GL+550。基礎の立上りを地上300mm以上とるため、GL+400 では納まらない（本文の解説を参照）。

★ 数値は必ず法令集・告示（平12建告1347号ほか）で確認すること。

※ この2枚は「型（8マス×10マス）」のもの。問題B（9マス）・C（7マス）は間口が違うので寸法を読みかえる。

床伏図の型（2階床伏図／3階床伏図 共通）

1マス = 910mm / 梁は「東西方向」に910ピッチで並べ、それを「南北方向」の4本の大梁で受ける

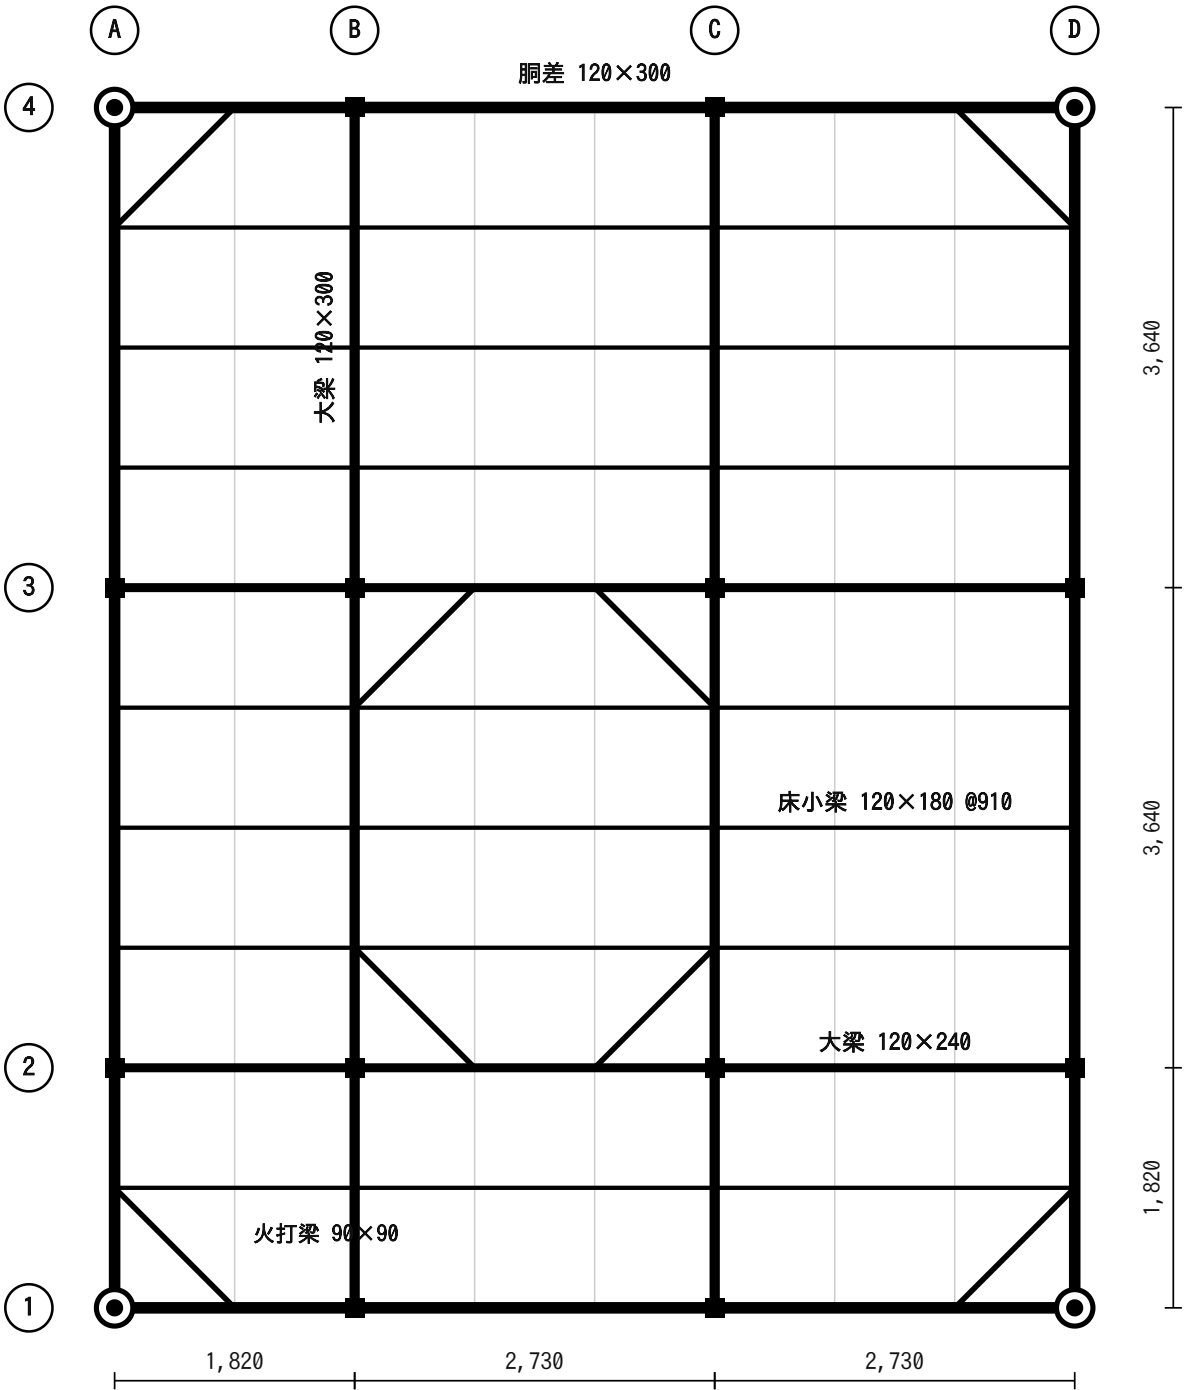


- 通し柱 120×120（建物の四隅・1階から3階まで1本）
- 管柱 120×120（各階ごとの柱・16か所すべて上下でそろう）
- 胴差 120×300（外周をぐるり1周）
- 大梁 120×300／120×240（B・C通り と 2・3通り）
- 床小梁 120×180 @910（東西方向に並べる）
- 火打梁 90×90（隅8か所・水平のゆがみ止め）

床は構造用合板 t=24 を梁に直接張る（根太レス＝剛床）。梁の最大スパンは 3,640mm におさえている。

小屋伏図の型（切妻・棟は南北方向・4寸勾配）

1マス = 910mm / 棟木は建物の中央（X=3,640）。屋根は東西の2方向へ流れる

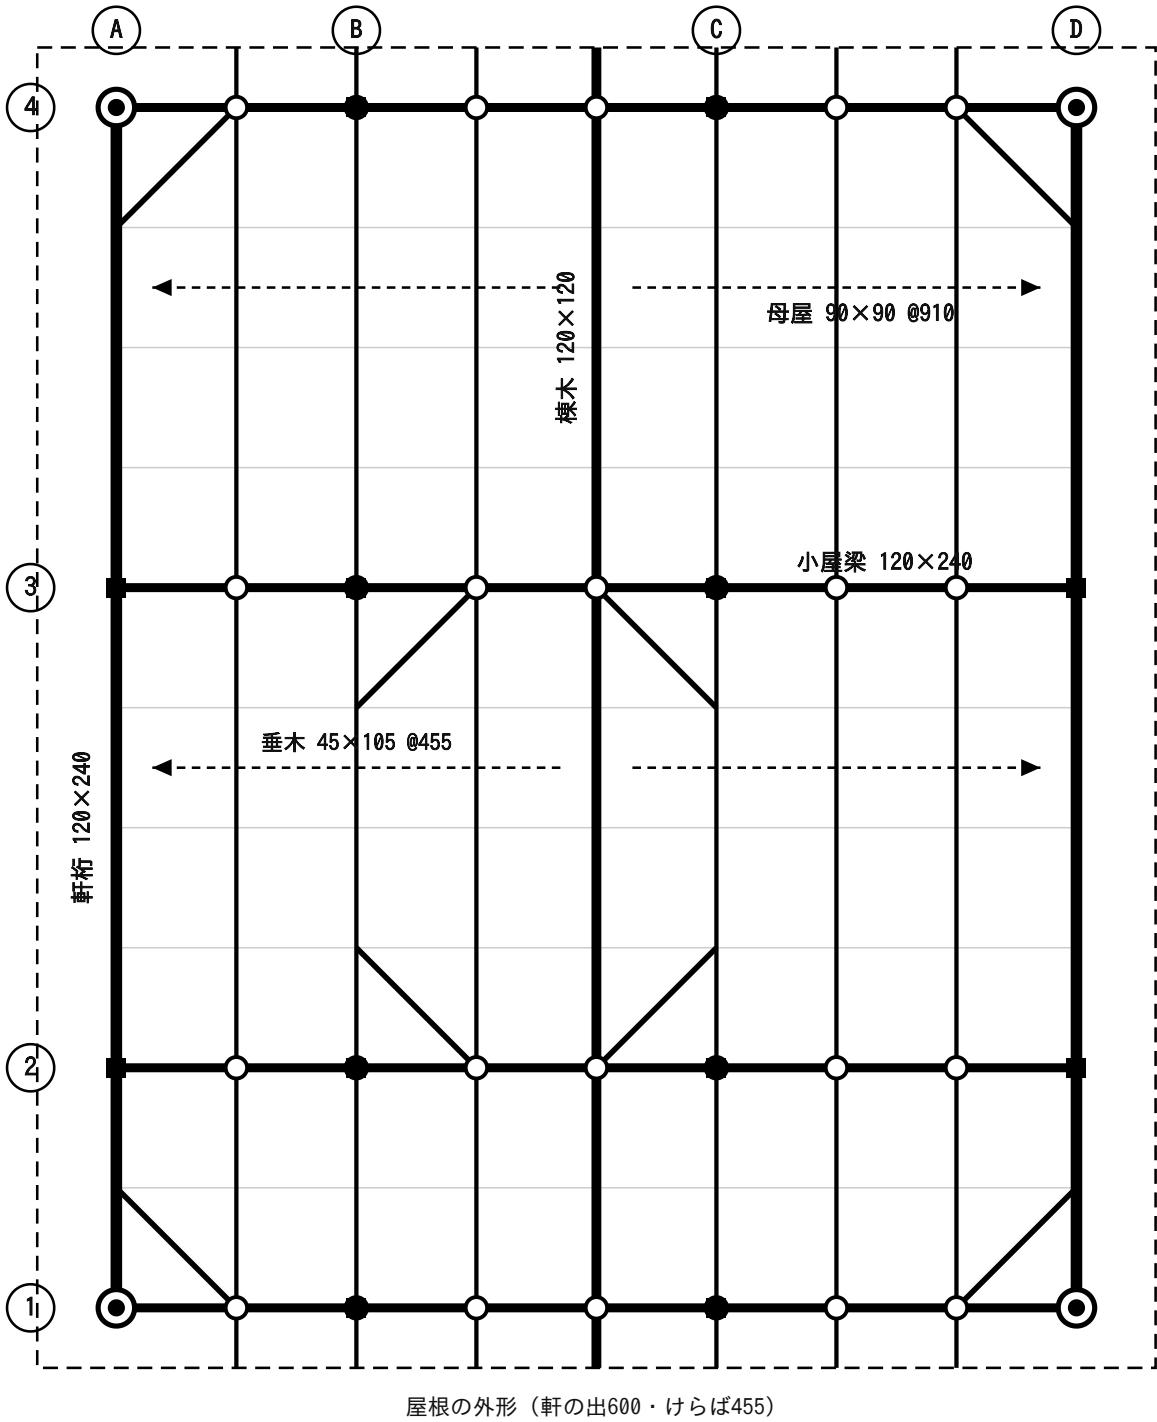

- 棟木 120×120（建物の中央・南北方向に1本）
- 母屋 90×90 @910（棟木と平行に6本）
- 小屋束 90×90（母屋と小屋梁の交点に立てる）
- 小屋梁 120×240（東西方向・柱のある通りに）
- 軒桁 120×240（A通り・D通り）
- - - 垂木 45×105 @455（棟から軒へ東西に流す）

4寸勾配 → 棟までの高さ 3,640 × 0.4 = 1,456mm。軒桁天端+1,456 が屋根のいちばん高いところ。

※ 2階の床伏図と3階の床伏図は同じ組み方でよい。小屋伏図は棟が南北方向・4寸勾配。