

設計課題 「商店街に建つ併用住宅（木造3階建て）」

問題用紙 予想問題E 南東の角地

1. 設計条件

- ある地方都市の商店街において、パン屋を営む夫婦とその子ども2人が住むための併用住宅を計画する。
- 計画に当たっては、次の①～③に特に留意する。
- ① 角地であることを活かした計画とする。
 - ② 店舗部分と住宅部分の動線が交錯しないようにする。
 - ③ 防火及び避難に配慮する。

(1) 敷地

- ア. 形状、道路との関係、方位等は、下に示す敷地図のとおりである。
- イ. 近隣商業地域内にあり、準防火地域に指定されている。
- ウ. 建蔽率の限度は90％（特定行政庁が指定した角地における加算を含む。）、容積率の限度は300％である。
- エ. 地形は平坦で、道路及び隣地との高低差はなく、地盤は良好である。
- オ. 電気、都市ガス、上水道及び公共下水道は完備している。

(2) 構造、階数、建築物の高さ等

- ア. 木造3階建てとする。
- イ. 建築物の最高の高さは11m以下、かつ、軒の高さは9.5m以下とする。
- ウ. 耐力壁（構造耐力上有効な壁）は、必要な量をバランスよく配置する。

(3) 延べ面積等

- ア. 延べ面積は、「180㎡以上、200㎡以下」とする。
- イ. 玄関ポーチ、バルコニー、駐輪スペース等は、床面積に算入しない。

(4) 人員構成等

- 夫婦（40歳代）、子ども2人（中学生、小学生）

(5) 要求室等

下表の全ての室等は、指定された設置階に計画する。

設置階	室名等	特記事項
1階	店舗売場	ア. 25㎡以上とする。 イ. 道路に面して出入口を設ける。 ウ. 陳列棚及びレジカウンターを設ける。
	厨房・作業場	ア. 9㎡以上とする。 イ. 店舗売場に隣接させ、直接行き来できるようにする。 ウ. 流し台、調理台、作業台及びオープンを設ける。
	スタッフルーム	ア. 6㎡以上とする。 イ. 従業員の更衣及び休憩に使用する。
	店舗用便所	ア. 来客が利用できるものとする。 イ. 洋式便器及び手洗い器を設ける。
	倉庫	・商品及び材料を保管する。
	玄関	ア. 住宅部分の玄関とし、道路から直接出入りできるものとする。 イ. 下足入れを設ける。
2階	居間・食事室・台所	ア. 1室にまとめ、25㎡以上として計画する。 イ. ソファ、テーブル及び椅子（計4席以上）を設ける。 ウ. 台所設備機器（流し台・調理台・コンロ台・冷蔵庫等）を設ける。
	和室	ア. 6畳以上とする。 イ. 居間に隣接させ、直接行き来できるようにする。 ウ. 押入れを設ける。
	浴室・洗面脱衣室	・浴室には浴槽、洗面脱衣室には洗面台及び洗濯機を設ける。
	便所	・洋式便器を設ける。
	家事室	・納戸を兼ねてもよい。
3階	夫婦寝室	ア. 13㎡以上とする。 イ. 洋室とし、ベッド（計2台）及び収納を設ける。
	子ども室	ア. 2室（各8㎡以上）設け、いずれも同じ広さとする。 イ. いずれも洋室とし、ベッド、机及び収納を設ける。
	便所	・洋式便器を設ける。
	納戸	


（注1）各要求室等においては、床面積・広さの指定がない場合、床面積は適宜とする。

（注2）階段は、安全を確保するために、踊場を設ける。

(6) 屋外施設等

屋外に下表のものを計画する。

駐輪スペース	・4台分を設ける。
門・塀・植栽等	

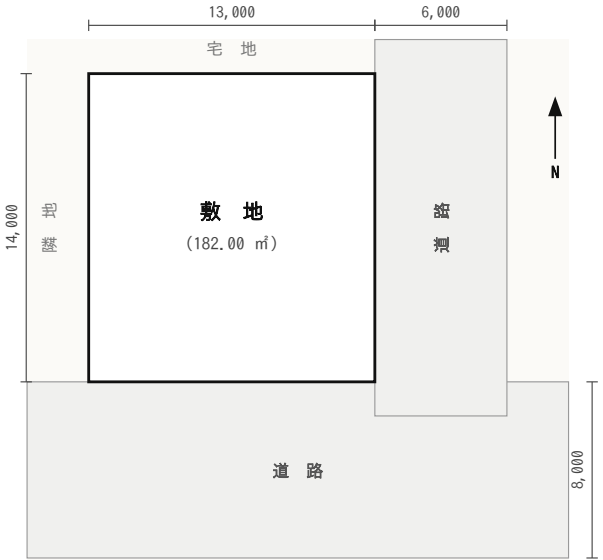

2. 要求図書

- ・ a. 答案用紙の定められた枠内に、下表の要求図書を記入する。（寸法線は、枠外にはみだして記入してもよい。）
- ・ b. 図面は黒鉛筆仕上げとする。（定規を用いなくてもよい。）
- ・ c. 記入寸法の単位は、mmとする。なお、答案用紙の1目盛は、4.55mm（部分詳細図にあっては、10mm）である。
- ・ d. シックハウス対策のための機械換気設備等は、記入しなくてよい。

要求図書 ()内は縮尺	特記事項
(1) 1階平面図兼配置図 (1/100)	ア. 1階平面図兼配置図、2階平面図及び3階平面図には、次のものを記入する。 ・建築物の主要な寸法 ・室名等 ・「通し柱」を○印で囲み、「耐力壁」には△印を付ける。 ・部分詳細図の切断位置及び方向
(2) 2階平面図 (1/100)	イ. 1階平面図兼配置図には、次のものを記入する。 ・敷地境界線と建築物との距離 ・道路から建築物へのアプローチ、駐輪スペース、門、塀、植栽等 ・道路から敷地及び建築物への出入口には、▲印を付ける。 ・玄関及び店舗売場の土間部分の地盤面からの高さ ・玄関ホール（廊下）の床高 ・店舗売場…陳列棚及びレジカウンター ・厨房・作業場…流し台、調理台、作業台及びオープン ・店舗用便所…洋式便器及び手洗い器 ・玄関…下足入れ
(3) 3階平面図 (1/100)	ウ. 2階平面図には、次のものを記入する。 ・居間・食事室・台所…ソファ、テーブル、椅子及び台所設備機器 ・和室…畳及び押入れ ・浴室…浴槽／洗面脱衣室…洗面台及び洗濯機／便所…洋式便器
(4) 床伏図兼小屋伏図 (1/100)	エ. 3階平面図には、次のものを記入する。 ・夫婦寝室…ベッド及び収納 ・子ども室…ベッド、机及び収納 ・便所…洋式便器
(5) 立面図 (1/100)	ア. 南側立面図とする。 イ. 建築物の最高の高さを記入する。
(6) 部分詳細図（断面） (1/20)	ア. 切断位置は、外壁を含む部分とし、開口部を含むものとする。 イ. 作図の範囲は、基礎から2階の床までとする。 ウ. 主要部の寸法等（床高、天井高、階高、基礎の寸法等）を記入する。 エ. 主要部材（基礎、土台、柱、胴差、床梁等必要なもの）の名称・断面寸法を記入する。 オ. アンカーボルト等の名称・寸法を記入する。 カ. 外壁、床、その他必要と思われる部分の断熱・防湿措置を記入する。 キ. 内外の主要な部位（外壁、床、内壁、天井）の仕上材料名を記入する。
(7) 面積表	ア. 建築面積、床面積及び延べ面積を記入する。 イ. 建築面積及び床面積については、計算式も記入する。 ウ. 面積の数値は、小数点以下第2位までとし、第3位以下は切り捨てて。
(8) 計画の要点等	・建築物の計画に関する次の①～③について、具体的に記述する。 ・① 角地であることを活かして工夫した点 ・② 容積率及び建蔽率の算定について ・③ 防火及び避難について配慮した点

※ この問題用紙は、公表されている過去問（令和4～7年）の様式にならって作成した予想問題です。本物の試験問題ではありません。

【注意事項】試験問題を十分に読んでうえで、「設計製図の試験」に臨むようにしてください。なお、建築基準法等の関係法令や要求図書、主要な要求室等の計画等の設計と条件に対して解答内容が不十分な場合には、「設計条件・要求図書に対する重大な不適合」と判断されます。

下書欄

（目盛4.55mm）

Blank area for drawing, with a grid pattern.